

DANH MỤC BẢN VẼ




			CÔNG TY CỔ PHẦN ĐẦU TƯ ĐỊA ỐC NO VA							
			DANH MỤC BẢN VẼ DRAWING LIST							
DỰ ÁN: PHOENIX.P2 - 52,1 HA										
ĐỊA ĐIỂM: PHƯỜNG TAM PHƯỚC, THÀNH PHỐ ĐỒNG NAI, VN										
TƯ VẤN THIẾT KẾ: Công ty Cổ phần TNHH Tư vấn Xây dựng FUJINAMI										
A	= Approval (Duyệt)									
C	= Comment (Ý kiến)									
Cn	= Construction (Thi công)									
I	= Information (Thông tin)									
P	= Preliminary (lần đầu)									
R	= Record (Hồ sơ)									
T	= Tender (Đấu thầu)									
Cp	= Cost Plan (Kế hoạch chi phí)									

Stt Item	Số bản vẽ Dwg. No.		Tên bản vẽ Drawing Title	Ngày PH/ Issue	Điều chỉnh Revision			
					00	01	02	03
	SERIES 130		MẶT BẰNG TRẦN					
23	PN2.DN-FCC-CD-SH1-A-131		MẶT BẰNG TRẦN TẦNG 1		x			
24	PN2.DN-FCC-CD-SH1-A-132		MẶT BẰNG TRẦN TẦNG 2		x			
25	PN2.DN-FCC-CD-SH1-A-133		MẶT BẰNG TRẦN TẦNG 3		x			
	SERIES 140		MẶT BẰNG HOÀN THIỆN TƯỜNG					
26	PN2.DN-FCC-CD-SH1-A-141		MẶT BẰNG HOÀN THIỆN TƯỜNG TẦNG 1		x			
27	PN2.DN-FCC-CD-SH1-A-142		MẶT BẰNG HOÀN THIỆN TƯỜNG TẦNG 2		x			
28	PN2.DN-FCC-CD-SH1-A-143		MẶT BẰNG HOÀN THIỆN TƯỜNG TẦNG 3		x			
29	PN2.DN-FCC-CD-SH1-A-144		MẶT BẰNG HOÀN THIỆN TƯỜNG TẦNG 4		x			
	SERIES 200		MẶT ĐỨNG					
30	PN2.DN-FCC-CD-SH1-A-201		MẶT ĐỨNG A-B		x			
31	PN2.DN-FCC-CD-SH1-A-202		MẶT ĐỨNG B-A		x			
	SERIES 210		CHI TIẾT MẶT ĐỨNG					
32	PN2.DN-FCC-CD-SH1-A-211		MẶT ĐỨNG KÍCH THƯỚC TRỤC A-B - TẦNG 1		x			
33	PN2.DN-FCC-CD-SH1-A-212		MẶT ĐỨNG KÍCH THƯỚC TRỤC A-B - TẦNG 2		x			
34	PN2.DN-FCC-CD-SH1-A-213		MẶT ĐỨNG KÍCH THƯỚC TRỤC A-B - TẦNG 3		x			
35	PN2.DN-FCC-CD-SH1-A-214		MẶT ĐỨNG KÍCH THƯỚC TRỤC B-A - TẦNG 1		x			
36	PN2.DN-FCC-CD-SH1-A-215		MẶT ĐỨNG KÍCH THƯỚC TRỤC B-A - TẦNG 2		x			
37	PN2.DN-FCC-CD-SH1-A-216		MẶT ĐỨNG KÍCH THƯỚC TRỤC B-A - TẦNG 3		x			
	SERIES 300		MẶT CẮT					
38	PN2.DN-FCC-CD-SH1-A-301		MẶT CẮT A-A		x			
39	PN2.DN-FCC-CD-SH1-A-302		MẶT CẮT B-B		x			
40	PN2.DN-FCC-CD-SH1-A-303		MẶT CẮT C-C		x			
	SERIES 400		CHI TIẾT KHAI TRIỂN					
41	PN2.DN-FCC-CD-SH1-A-401		CHI TIẾT SÀN HIỂN		x			
42	PN2.DN-FCC-CD-SH1-A-402		CHI TIẾT BAN CÔNG		x			
43	PN2.DN-FCC-CD-SH1-A-403		CHI TIẾT CẦU THANG		x			
43	PN2.DN-FCC-CD-SH1-A-404-1		CHI TIẾT MÁI ĐÓN TỜ 1		x			
44	PN2.DN-FCC-CD-SH1-A-404-2		CHI TIẾT MÁI ĐÓN TỜ 2		x			
45	PN2.DN-FCC-CD-SH1-A-405		CHI TIẾT KHÁC		x			
	SERIES 500		THỐNG KÊ CỬA					
46	PN2.DN-FCC-CD-SH1-A-501		MẶT BẰNG ĐỊNH VỊ CỬA		x			
47	PN2.DN-FCC-CD-SH1-A-502		BẢNG THỐNG KÊ CỬA-A-01		x			
48	PN2.DN-FCC-CD-SH1-A-503		BẢNG THỐNG KÊ CỬA-A-02		x			
TỔNG SỐ BẢN VẼ					49			

VIẾT TẮT / ABBREVIATIONS

&	VÀ	FW	PHẪU THU NƯỚC SÀN
Ø	ĐƯỜNG KÍNH	FFL	CAO ĐỘ SÀN HOÀN THIỆN NGOẠI THẤT CAO ĐỘ SÀN HOÀN THIỆN DỰ KIẾN NỘI THẤT
#	SỐ	SSL	CAO ĐỘ SÀN KẾT CẤU
±	CỘNG TRỪ	H	CHIỀU CAO
AC	ĐIỀU HÒA KHÔNG KHÍ	HVAC	SỬ DỤNG, THÔNG GIÓ, ĐIỀU HÒA
AFFL	TRÊN SÀN HOÀN THIỆN	L	CHIỀU DÀI
AP	NẬP THẨM TRẦN	M	MÉT
APX	VÀO KHOẢNG	MAX	TỐI ĐA
AS	THEO BẢN VẼ	M&E	CƠ ĐIỆN
BAL	BÀN CÔNG	MIN	TỐI THIỂU
BDB	ỐNG THOÁT NƯỚC	MISC	HỖN HỢP
BIN	PHÒNG RÁC	NTS	KHÔNG CÓ TỈ LỆ
BTCT	BÊ TÔNG CỐT THÉP	NSX	NHÀ SẢN XUẤT
BVKC	BẢN VẼ KẾT CẤU	No.	SỐ LƯỢNG
CH	CAO ĐỘ TRẦN	REF	THAM KHẢO
CL.	ĐƯỜNG TIM	R	BÁN KÍNH
COL	CỘT	SEC	MẶT CẮT
CONC	BÊ TÔNG	SO	LỖ MỜ KẾT CẤU
CONT	TIẾP TỤC	S.O.P	ĐIỂM MỐC
CONTR	NHÀ THẦU	SPEC.	TIÊU CHUẨN KỸ THUẬT
D	CHIỀU DÀY	ST	CẦU THANG
DIA	ĐƯỜNG KÍNH	TYP	ĐIỂN HÌNH
DIM	KÍCH THƯỚC	WC	PHÒNG VỆ SINH
DWG	BẢN VẼ	WIN	CỬA SỔ
DR	CỬA ĐI	W	CHIỀU RỘNG
ELE	MẶT ĐỨNG		
EQ	ĐỀU NHAU		
EQMT	THIẾT BỊ		

CHÚ THÍCH KÝ HIỆU / SIGN NOTES

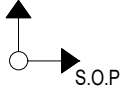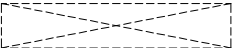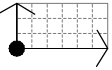RANH ĐẤT	
KHOẢNG LÙI	
ĐƯỜNG TIM	
DẤU NGÁT	
ĐIỂM ĐỊNH VỊ	
ĐIỂM MỐC	
HIỆU CHỈNH	
THÔNG TẦNG	
THÔNG TẦNG PHÍA TRÊN	
GẠCH MỐC ĐỊNH VỊ LÁT SÀN	
KÍ HIỆU ĐỘ LỆCH SÀN	

DANH MỤC VẬT LIỆU HOÀN THIỆN NGOẠI THẤT

VẬT LIỆU HOÀN THIỆN TƯỜNG		
KÝ HIỆU		MÔ TẢ
	FW1	TƯỜNG HOÀN THIỆN SƠN NƯỚC MÀU TRẮNG - RAL 9003
	FW2	TƯỜNG HOÀN THIỆN SƠN NƯỚC MÀU XÁM ĐẬM - RAL 7022
	FW3	TƯỜNG HOÀN THIỆN SƠN NƯỚC MÀU HỒNG NÂU - RAL 4009
	FW4	TƯỜNG HOÀN THIỆN SƠN NƯỚC MÀU VÀNG NHẠT - RAL 1015
	FW5	TƯỜNG HOÀN THIỆN SƠN NƯỚC MÀU XÁM - RAL 7042
	FW6	TƯỜNG HOÀN THIỆN SƠN NƯỚC MÀU DƯƠNG NHẬT -RAL - 6027
	FW7	TƯỜNG HOÀN THIỆN SƠN NƯỚC GIẢ GỖ - RAL - 8011
	L1	LEN CHẦN TƯỜNG GẠCH PORCELAIN 300X600mm,CHÔNG THÂM TỐI MÀU

GHI CHÚ VẬT LIỆU SÀN NGOẠI THẤT					
TÊN	KÍ HIỆU	CHỦ THÍCH	TÊN	KÍ HIỆU	CHỦ THÍCH
Fi		SÀN BÊ TÔNG CỐT THÉP THỎ			
Fi-2		SÀN BÊ TÔNG CỐT THÉP, CHÔNG THÂM			
F1		GẠCH PORCELAIN 300x600mm,CHÔNG TRƯỢT, NGOẠI THẤT			
F2		ĐÁ ĐÁ GRANITE DÀY 20mm CHÔNG TRƯỢT 600x600mm			VIÊN GẠCH ĐUÔI
F3		ĐÁ ĐÁ GRANITE DÀY 20mm LÁT NGÁCH CỬA			
F4		GẠCH ĐỒNG NHẤT CHÔNG TRƯỢT, MÀU SÁNG 300x300			ĐIỂM MỐC CODE CAO ĐỘ
F5		ĐÁ BAZAN 300X600			

VẬT LIỆU HOÀN THIỆN TRẦN		
KÝ HIỆU	MÔ TẢ	
	FC-01	TRẦN CEMBOARD HOÀN THIỆN SƠN NƯỚC MÀU TRẮNG
	FC-02	TRẦN GỖ NHỰA MÀU NÂU ĐẬM
	FC-03	TRẦN ĐẾ THỎ
	FC-04	DĂM BÊ TÔNG TRÁT VỮA HOÀN THIỆN SƠN NƯỚC (MÀU THEO PC)

ĐÈN NGOẠI THẤT		
KÝ HIỆU	MÔ TẢ	
	ĐÈN ÁP TRẦN NGOẠI THẤT, 12W, ÁNH SÁNG 3700K	
	ĐÈN GẮN TƯỜNG NGOẠI THẤT ÁNH SÁNG 3700K, CÔNG SUẤT 15W	
	ĐÈN TRỤ CÔNG ÁNH SÁNG 3000K, CÔNG SUẤT 9W	

DANH MỤC VẬT LIỆU HOÀN THIỆN TƯỜNG RÀO

VỊ TRÍ	LỚP HOÀN THIỆN	THÔNG TIN
TƯỜNG RÀO mặt tiền	SƠN NƯỚC HOÀN THIỆN (SƠN NGOẠI THẤT)	Duluxe/Nippon/hoặc tương đương Màu trắng
TƯỜNG RÀO mặt bên + mặt sau	SƠN NƯỚC HOÀN THIỆN (SƠN NGOẠI THẤT)	Duluxe/Nippon/hoặc tương đương Màu trắng
TƯỜNG RÀO GỖ TƯỜNG RÀO	SƠN NƯỚC HOÀN THIỆN (SƠN NGOẠI THẤT)	Duluxe/Nippon/hoặc tương đương Màu xám nhạt
CÔNG VÀO	SẮT SƠN TÍNH ĐIỆN	Màu xám đậm
TỦ KÍ THUẬT (RÁC+ĐIỆN)	SƠN NƯỚC HOÀN THIỆN (SƠN NGOẠI THẤT)	Duluxe/Nippon/hoặc tương đương Màu trắng

DANH MỤC VẬT LIỆU KIM LOẠI

VỊ TRÍ	LỚP HOÀN THIỆN	THÔNG TIN
LAN CAN SẮT	LAN CAN SẮT SƠN TÍNH ĐIỆN	Màu xám đậm
LAN CAN KÍNH	THANH CHÔNG ĐỪNG THÉP KHÔNG RỈ 80x10mm TAY VỊN THÉP KHÔNG RỈ TRÒN Ø 50 DÂY 1.5mm	Hoàn thiện bề mặt sọc nhuyển Hoàn thiện bề mặt sọc nhuyển
CỬA THẨM MÁI	CỬA THÉP SƠN TÍNH ĐIỆN THEO NSX	Hoàn thiện màu xám nhạt

MẪU TÔ VẬT LIỆU
(KHÔNG ÁP DỤNG CHO MB HOÀN THIỆN TRẦN SÀN)

MẪU HATCH	VẬT LIỆU
	GẠCH
	BÊ TÔNG CỐT THÉP
	VỮA
	CỎ
	KÍNH
	ĐÁ TỰ NHIÊN
	SƠN NƯỚC
	ĐÁ GRANITE
	GẠCH PORCELAIN

CHÚ THÍCH, KÝ HIỆU

KÝ HIỆU	MÔ TẢ
	CAO ĐỘ MẶT ĐỨNG
	CAO ĐỘ HOÀN THIỆN TRẦN
	CAO ĐỘ SÀN HOÀN THIỆN
	CAO ĐỘ SÀN KẾT CẤU
	KÍ HIỆU MẶT CÁT
	KÝ HIỆU TRỤC
	KÝ HIỆU MẶT ĐỨNG
	KÍ HIỆU HOÀN THIỆN SÀN
	KÍ HIỆU HOÀN THIỆN TRẦN
	KÍ HIỆU HOÀN THIỆN TƯỜNG
	KÝ HIỆU CỬA ĐI, CỬA SỎ
	ĐỊNH VỊ CHI TIẾT




HƯỚNG DẪN CHUNG

- TẤT CẢ CÁC KÍCH THƯỚC ĐƯA RA LÀ KÍCH THƯỚC HOÀN THIỆN, ĐƠN VỊ MILIMET (mm) TRỪ MỘT SỐ TRƯỜNG HỢP KHÁC
- NHÀ THẦU PHẢI KIỂM TRA TẤT CẢ CÁC KÍCH THƯỚC THỰC TẾ TRÊN CÔNG TRƯỜNG TRƯỚC KHI TIẾN HÀNH THI CÔNG, NẾU CÓ BẤT KỲ SỰ KHÔNG ĐỒNG NHẤT GIỮA BẢN VẼ CỦA CÁC BỘ MÔN VỚI THỰC TẾ CÔNG TRƯỜNG ĐỀU PHẢI ĐƯỢC TRÌNH CHO ĐẠI DIỆN CỦA CHỦ ĐẦU TƯ VÀ ĐƠN VỊ TƯ VẤN XEM XÉT ĐỂ ĐIỀU CHỈNH TRƯỚC KHI BẮT ĐẦU CÔNG VIỆC. TRONG TRƯỜNG HỢP CÓ NHỮNG Mâu THUẬN GIỮA CÁC BỘ MÔN DẪN ĐẾN CHI TIẾT LẮP ĐẶT BẤT THƯỜNG, NHÀ THẦU CẦN THÔNG BÁO CHO ĐƠN VỊ TƯ VẤN THIẾT KẾ ĐỂ ĐƯỢC HƯỚNG DẪN LÂM RỎ. BẤT KỲ CÔNG TÁC LẮP ĐẶT NÀO CÓ Mâu THUẬN VỚI BỘ BẢN VẼ KIẾN TRÚC, SẼ ĐƯỢC THỰC HIỆN LẠI BỞI NHÀ THẦU VÀ KHÔNG CÓ CHI PHÍ PHÁT SINH
- NHÀ THẦU PHẢI THEO NHỮNG CHI TIẾT VÀ PHƯƠNG PHÁP LẮP ĐẶT, BẢO HÀNH TỐT NHẤT CỦA NHÀ SẢN XUẤT, SỰ KHÁC BIỆT VỚI CHI TIẾT CỦA NHÀ SẢN XUẤT ĐỀU PHẢI ĐƯỢC TRÌNH CHO ĐẠI DIỆN CHỦ ĐẦU TƯ XEM XÉT.
- CHI TIẾT VÀ SẢN PHẨM MÀ THEO KINH NGHIỆM CỦA NHÀ THẦU LÀ KHÔNG TỐT, NHỮNG CHI TIẾT KHÔNG RÕ RÀNG, KHÔNG CHÍNH XÁC PHẢI TRÌNH CHO ĐƠN VỊ TƯ VẤN TRONG THỜI GIAN SỚM NHẤT ĐỂ GIẢI QUYẾT
- NHÀ THẦU PHẢI CUNG CẤP MÔ HÌNH HOÀN THIỆN VÀ MẪU THỦ NHƯ HỢP ĐỒNG THẦU CHO ĐẠI DIỆN CỦA CHỦ ĐẦU TƯ, BAN QUẢN LÝ DỰ ÁN VÀ ĐƠN VỊ TƯ VẤN THIẾT KẾ PHÊ DUYỆT TRƯỚC KHI TIẾN HÀNH THI CÔNG
- TẤT CẢ MÁI CHE VÀ LÁT ĐƯỜNG PHẢI ĐÁNH DỐC CHẤY VỀ MƯƠNG THOÁT NƯỚC ĐỂ TRÁNH ĐỘNG NƯỚC, Ứ NƯỚC
- TẤT CẢ CÁC CAO ĐỘ TRONG BẢN VẼ LÀ CAO ĐỘ SÀN HOÀN THIỆN TRỪ KHI CÓ NHỮNG CHI TIẾT ĐẶC BIỆT KHÁC
- BẢN VẼ PHẢI ĐƯỢC XEM XÉT VỚI SỰ LIÊN KẾT VỚI TẤT CẢ CÁC BẢN VẼ LIÊN QUAN KHÁC VÀ SPEC.
- BẢN VẼ LẮP ĐẶT THI CÔNG (SHOP DRAWING) PHẢI ĐƯỢC NHÀ THẦU THỰC HIỆN VÀ ĐỀ TRÌNH. TRỪ NHỮNG CHI TIẾT ĐƯỢC THỂ HIỆN RÕ RÀNG KÍCH THƯỚC, THÌ VỊ TRÍ CỦA CÁC HỆ THỐNG, THIẾT BỊ CƠ ĐIỆN, NƯỚC, PCCC, ĐƯỜNG ỐNG VÀ CÁC PHỤ KIỆN CHỈ LÀ TƯƠNG ĐỐI. VỊ TRÍ CHÍNH XÁC TẠI CÔNG TRƯỜNG SẼ ĐƯỢC XÁC ĐỊNH THÔNG QUA BỘ BẢN VẼ LẮP ĐẶT THI CÔNG (SHOP DRAWING) CỦA NHÀ THẦU CHÍNH (HOẶC CÁC THẦU PHỤ CỦA HỌ) VÀ ĐƯỢC SỰ CHẤP THUẬN CỦA ĐƠN VỊ TƯ VẤN THIẾT KẾ TRƯỚC KHI THỰC HIỆN CÔNG TÁC LẮP ĐẶT CHI TIẾT ĐÓ.


SƠN NƯỚC HOÀN THIỆN VỮA XÂY GẠCH VỮA XÂY SƠN NƯỚC HOÀN THIỆN CHI TIẾT TƯỜNG XÂY DÀY 110mm SƠN NƯỚC HOÀN THIỆN VỮA XÂY GẠCH VỮA XÂY SƠN NƯỚC HOÀN THIỆN CHI TIẾT TƯỜNG XÂY DÀY 210mm SÂN LÁT GẠCH PORCELAIN VỮA XI MĂNG MẠC 75 DÀY 20mm SÂN BTCT (XEM BV KẾT CẤU)	LỚP VỮA XI MĂNG M75 DÀY 20 mm NẾP CHỈ NHỰA uPVC ẨM TƯỜNG CHỮ U TƯỜNG GẠCH XÂY	TRONG NHÀ TRONG NHÀ NGOÀI NHÀ TẦM XÓP GIẢN NỖ CHÈN KHE SIKAFLEX CO GIẢN LỚP VỮA TÔ HOÀN THIỆN LỚP CHỐNG THẨM BU LÔNG NỖ NẾP KHE CO GIẢN INOX 316	BACKER ROD THANH CHÈN XÓP KHE CO GIẢN SIKAFLEX CO GIẢN THÉP GIA CỐ GÓCTƯỜNG TÔ TƯỜNG VÁT KICKER ĐỎ TÁCH CEMBOARD NGẮN 2 NHÀ
CHI TIẾT CẤU TẠO SÀN, TƯỜNG ĐIỆN HÌNH	CHI TIẾT RON ẨM TƯỜNG	CHI TIẾT JOIN MẶT TIỀN, HÀNG RÀO 2 NHÀ	CT CHỐNG THẨM TƯỜNG MÁI ,ĐỈNH HÀNH RÀO GIỮA 2 NHÀ
LỚP VỮA XI MĂNG M75 DÀY 20 SƠN NƯỚC NGOẠI THẤT NHƯ THIẾT KẾ LỚP CHỐNG THẨM CAO 300 TỪ CAO ĐỘ HOÀN THIỆN SÂN VƯỜN COTE SÂN VƯỜN	LEN TƯỜNG ỐP GẠCH LỚP VỮA XI MĂNG M.75 DÀY 20 TƯỜNG GẠCH LỚP CHỐNG THẨM LEN CHÂN TƯỜNG NGOÀI NHÀ LEN TƯỜNG ỐP GẠCH LỚP VỮA XI MĂNG M.75 DÀY 20 COTE SÂN VƯỜN	TƯỜNG GẠCH KICKER BÊ TÔNG SÂN BTCT (XEM BVKC) ÔNG THOÁT NƯỚC (XEM BẢN VẼ NƯỚC) LỚP VỮA BÙ CO NGÓT BĂNG TRƯƠNG NỖ	NẬP THU THAM KHẢO BẢN VẼ MEP THÉP CHỒNG RỈ NIỀNG MIỆNG LỖ THU NẬP THU THÉP LÁ 5X25 THÉP CHỒNG RỈ NIỀNG MIỆNG LỖ THU FFL LỚP CHỐNG THẨM THÉP LÁ 30X3 CHÉ ĐUÔI CÁ CHỖN VÀO LỚP KẾT CẤU SÀN ÔNG NỖI XEM BẢN VẼ NƯỚC ÔNG XUỐNG XEM BẢN VẼ NƯỚC
CHI TIẾT CHỐNG THẨM CHÂN TƯỜNG NGOÀI NHÀ TẠI VỊ TRÍ KHÔNG ỐP LEN TƯỜNG		CHI TIẾT SÀN WC	CHI TIẾT PHẾU THU NƯỚC SÀN MÁI- BAN CÔNG-SÂN THƯỢNG
LỚP VỮA XI MĂNG M75 DÀY 20 KỀ RON 20, SÂU 10 LEN TƯỜNG SƠN NƯỚC NGOÀI TRỜI MÀU XÁM ĐẬM LỚP CHỐNG THẨM CAO 200 TỪ CAO ĐỘ HOÀN THIỆN SÂN VƯỜN COTE SÂN VƯỜN		DÁN GẠCH HOÀN THIỆN LỚP VỮA CÁN NỀN DỌC VỀ RÃNH THU LỚP CHỐNG THẨM CUỐN LÊN TƯỜNG 300 SÂN BTCT (XEM BV KC) HOÀN THIỆN SƠN NƯỚC NGOẠI THẤT HỆ KHUNG TRẦN TẦM CEMBOARD SƠN NƯỚC HOÀN THIỆN LAN CAN KÍNH CHỈ NGĂN NƯỚC MẠCH DỪNG THI CÔNG THANH SHADOW LINE MÀU TRẮNG HOÀN THIỆN THEO NSX	CHỐT NEO KÍNH VỚI NẬP ĐẦY BĂNG THÉP KHÔNG GỈ XEM CHI TIẾT NSX KÍNH TRONG CƯỜNG LỰC 10mm HOÀN THIỆN ĐÁ GANITE CHÙA THÉP NEO ĐÁP VỮA KICKER BÊ TÔNG TAY VIN THÉP KHÔNG RỈ 316 TRÒN Ø 50 DÂY 1.5mm HOÀN THIỆN BỀ MẶT SỌC NHUYỄN THANH CHỒNG ĐỨNG THÉP KHÔNG RỈ 80x10mm HOÀN THIỆN BỀ MẶT SỌC NHUYỄN THÉP BÀN ẨM SÀN LIỀN KẾT VỚI DẦM BTCT BĂNG BU LÔNG NỖ GẠCH ỐP LEN CHÂN TƯỜNG CÙNG LOẠI GẠCH LÁT SÀN THANH CHỒNG ĐỨNG THÉP KHÔNG RỈ 80x10mm HOÀN THIỆN BỀ MẶT SỌC NHUYỄN MÀNG CHỐNG THẨM XEM BẢN VẼ CẤU TẠO SÀN THÉP BÀN ẨM SÀN LIỀN KẾT VỚI DẦM BTCT BĂNG BU LÔNG NỖ
CHI TIẾT CHÂN TƯỜNG HÀNG RÀO	CHI TIẾT LEN TƯỜNG NGOÀI NHÀ	CHI TIẾT SÀN BAN CÔNG, SÂN THƯỢNG	CHI TIẾT LAN CAN KÍNH ĐIỆN HÌNH
TRONG NHÀ CHIỀU RỘNG KHUNG CỬA CỬA CẢNH MỜ ĐÁ GRANITE NGOÀI NHÀ FFL	TRONG NHÀ 100 KHUNG CỬA CỬA LỪA NHÔM KÍNH ĐÁ GRANITE NGOÀI NHÀ FFL	DẦM HOẶC SÀN BTCT LỚP VỮA TÔ VÁT XÉO NGẠT NƯỚC DIM < 200 VÁT XÉO DẦM HOẶC SÀN BTCT LỚP VỮA TÔ CHỈ NHỰA NGẠT NƯỚC	
CHI TIẾT NGẠCH CỬA MỜ CẢNH NGOÀI NHÀ	CHI TIẾT NGẠCH CỬA LỪA NGOÀI NHÀ	CHI TIẾT CHỈ NGĂN NƯỚC	CHI TIẾT CHỐNG THẨM SÀN MÁI

GHI CHÚ: CAO ĐỘ ±0.00 TRONG BẢN VẼ TƯƠNG ỨNG CAO ĐỘ HỒN DẦU TẠI VỊA HẸ. CAO ĐỘ VÍA HẸ VUI LÒNG XEM CÁC BẢN VẼ "THIẾT KẾ HẠ TẦNG"




BẢNG THỐNG KÊ CẤU TẠO SÀN

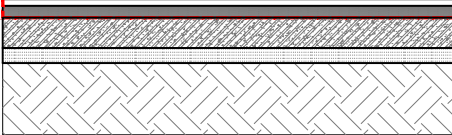
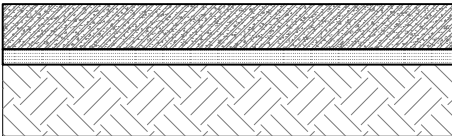
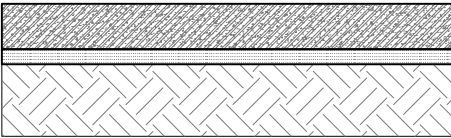
	KÍ HIỆU	VỊ TRÍ	CHI TIẾT	MÔ TẢ CÁC LỚP CẤU TẠO
TẦNG 1	F1.1	SẢNH HIỀN		- ĐÁ ĐÁ GRANITE DÀY 20mm HOÀN THIỆN - LỚP VỮA CÁN NỀN M75 ĐÁNH DỐC - LỚP CHỐNG THẤM CUỐN LÊN CHÂN TƯỜNG 300mm - SÀN BTCT(xem BVKC) - LỚP BÊ TÔNG LÓT(XEM BVKC) - ĐẤT TỰ NHIÊN ĐÁM CHẶT XỬ LÝ CHỐNG MÔI ĐỒNG THỜI
	F1.2	SÀN NỘI THẤT		- SÀN BTCT(xem BVKC) - LỚP BÊ TÔNG LÓT(xem BVKC) - ĐẤT TỰ NHIÊN ĐÁM CHẶT XỬ LÝ CHỐNG MÔI ĐỒNG THỜI
	F1.3	SÀN WC TẦNG 1		- SÀN BTCT(xem BVKC) - LỚP BÊ TÔNG LÓT(xem BVKC) - ĐẤT TỰ NHIÊN ĐÁM CHẶT XỬ LÝ CHỐNG MÔI ĐỒNG THỜI

BẢNG THỐNG KÊ CẤU TẠO SÀN
















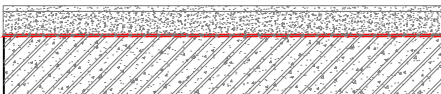
	KÍ HIỆU	VỊ TRÍ	CHI TIẾT	MÔ TẢ CÁC LỚP CẤU TẠO
MÁI		SÀN MÁI		- LỚP VỮA TẠO PHẪNG DÀY 10MM - LỚP BÊ TÔNG ĐÁ MI M200, LƯỚI THÉP D6@200, DÀY MIN 50mm, TẠO DỐC 1.5% VỀ PHẪU THU - LỚP CHỐNG THẤM GÓC PU CUỐN LÊN CHÂN TƯỜNG 300mm - SÀN BTCT(xem BVKC)

GHI CHÚ PHÂN LOẠI TƯỜNG

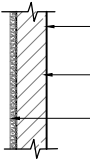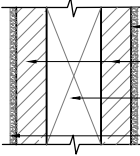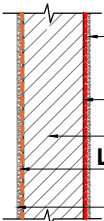CHI TIẾT	MÔ TẢ CẤU TẠO
 VỪA TÔ TƯỜNG DÀY 15-20mm 2 LỚP GẠCH ỐNG VỪA TÔ TƯỜNG DÀY 15-20mm, SƠN NƯỚC NGOẠI THẤT BÊN NGOÀI	<u>TƯỜNG NGOẠI THẤT</u> - TƯỜNG XÂY GẠCH ỐNG 2 LỚP (80X80X180mm) - TÔ VỪA TẠO PHẪNG 2 MẶT, DÀY 15-20mm - MẶT NGOÀI HOÀN THIỆN SƠN NƯỚC NGOẠI THẤT
 MẶT TRONG KHÔNG TÔ 1 LỚP GẠCH ỐNG VỪA TÔ TƯỜNG DÀY 15-20mm BÊN NGOÀI	<u>TƯỜNG GIÁP NHÀ</u> - TƯỜNG XÂY GẠCH ỐNG 1 LỚP (80X80X180mm) - MẶT TRONG KHÔNG TÔ - MẶT NGOÀI TRÁT VỪA TẠO PHẪNG DÀY 15-20mm
 VỪA TÔ TƯỜNG DÀY 15-20mm 1 LỚP GẠCH ỐNG KHOẢNG TRỐNG VỪA TÔ TƯỜNG DÀY 15-20mm, SƠN NƯỚC NGOẠI THẤT BÊN NGOÀI	<u>TƯỜNG 2 LỚP</u> - TƯỜNG XÂY 2 LỚP CHỨA KHOẢNG TRỐNG TUỖ THEO VỊ TRÍ , XEM BẢN VẼ KIẾN TRÚC - TÔ VỪA TẠO PHẪNG 2 MẶT DÀY 15-20mm - MẶT NGOÀI HOÀN THIỆN SƠN NƯỚC NGOẠI THẤT
 2 LỚP VỪA TÔ DÀY 15-20mm CHÈN CỐT LƯỚI CHỐNG NỨT LỚP CHỐNG THẤM 2 THÀNH PHẦN DẠNG QUÉT TƯỜNG (xem bvkc) LỚP CHỐNG THẤM GÓC BITUM, THI CÔNG DÁN ỚT 2 LỚP VỪA TÔ TƯỜNG DÀY 15-20mm BÊN NGOÀI	<u>TƯỜNG BÊ NGÀM</u> - TƯỜNG XÂY GẠCH ĐINH 2 LỚP (40x80x180). XEM BẢN VẼ MEP - TÔ 2 LỚP VỪA TẠO PHẪNG 2 MẶT DÀY 20-15mm - LỚP 01 TẠO NHẢM DÀY 8-10mm, DÁN LƯỚI CHỐNG NỨT - LỚP 02 TẠO PHẪNG DÀY 10mm - MẶT TRONG QUÉT CHỐNG THẤM DẠNG QUÉT 2 THÀNH PHẦN LÊN TỚI NÁP - MẶT NGOÀI PHỦ MÀNG BITUM CHỐNG THẤM, THI CÔNG DẠNG ỚT

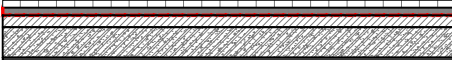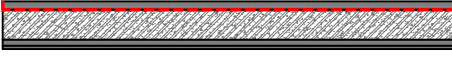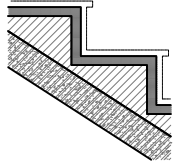TẦNG 2,3	F2.1	SÀN NỘI THẤT SÀN WC		SÀN BTCT(xem BVKC)
	F2.2	BAN CÔNG SÂN THƯỢNG SÀN P. GIẶT		- GẠCH PORCELAIN CHỐNG TRƯỢT HOÀN THIỆN - LỚP VỮA CÁN NỀN M75 ĐÁNH DỐC VỀ RÃNH THU - LỚP CHỐNG THẤM CUỐN LÊN CHÂN TƯỜNG 300mm - LỚP ĐÓN NỀN - SÀN BTCT(xem BVKC) - HOÀN THIỆN SƠN NƯỚC NGOẠI THẤT THEO SPEC
	F2.3	SÀN BỒN HOA		- LỚP VỮA CÁN NỀN M75 ĐÁNH DỐC VỀ RÃNH THU - LỚP CHỐNG THẤM CUỐN LÊN CAO TỐI THÀNH BỒN HOA - SÀN BTCT(xem BVKC) - HOÀN THIỆN SƠN NƯỚC NGOẠI THẤT THEO SPEC
	F2.4	CẦU THANG		- LỚP VỮA TẠO PHẪNG DÀY 8-10mm - LỚP GẠCH ĐÌNH XÂY TẠO BẠC - BÀN THANG BTCT(xem BVKC)


QUY ĐỊNH TƯỜNG XÂY

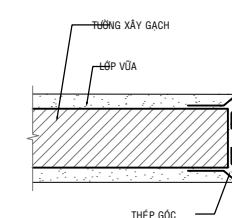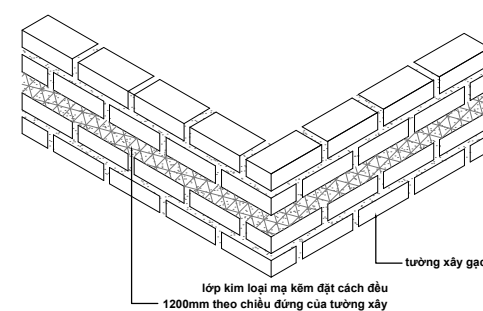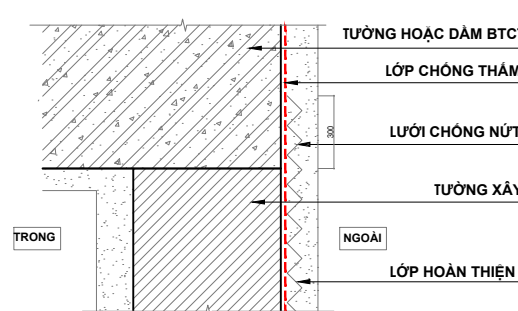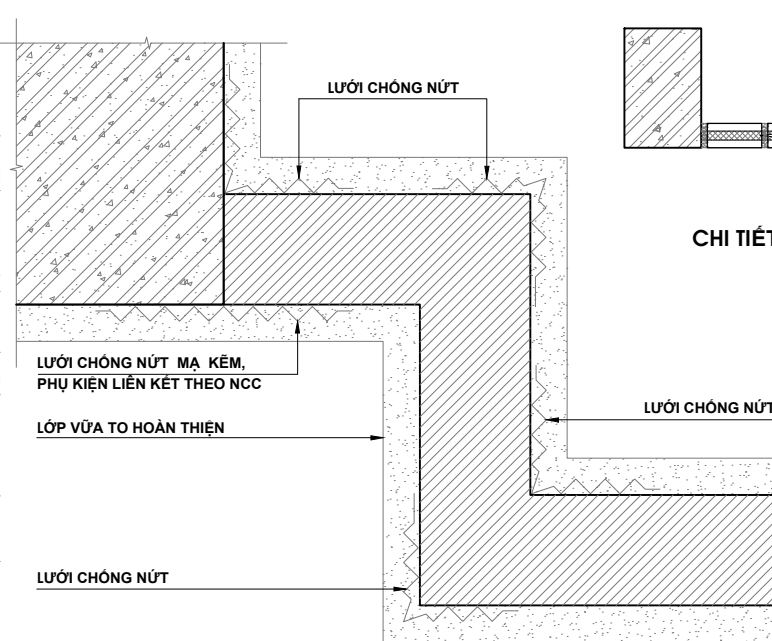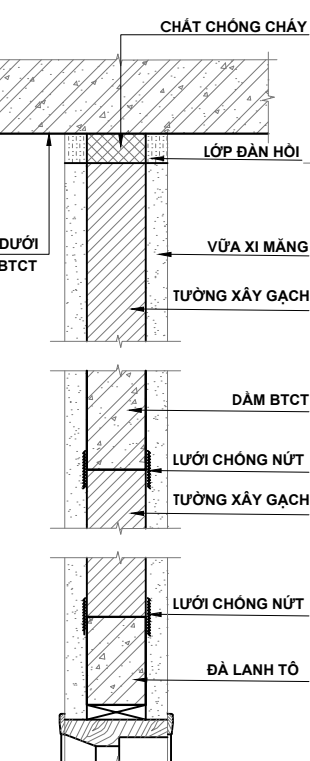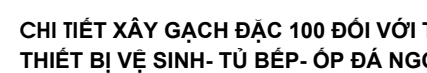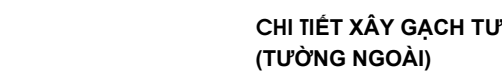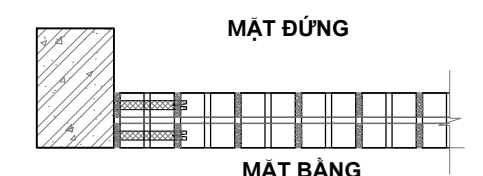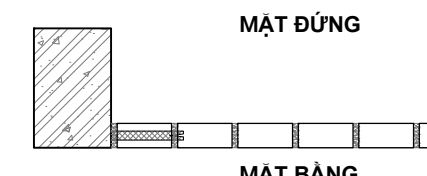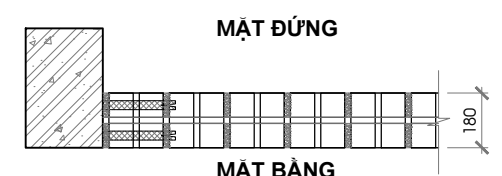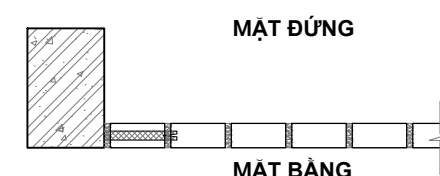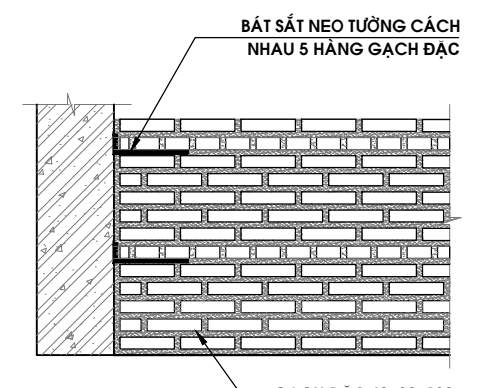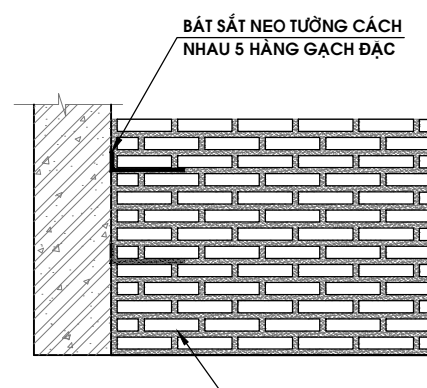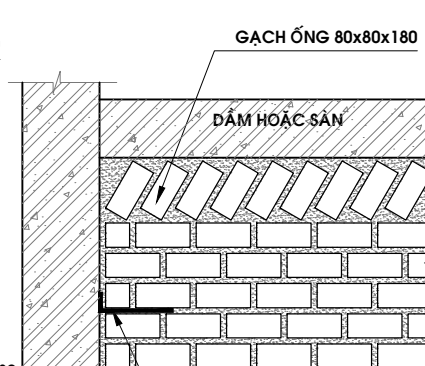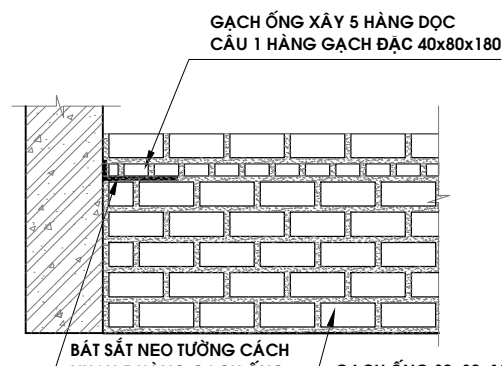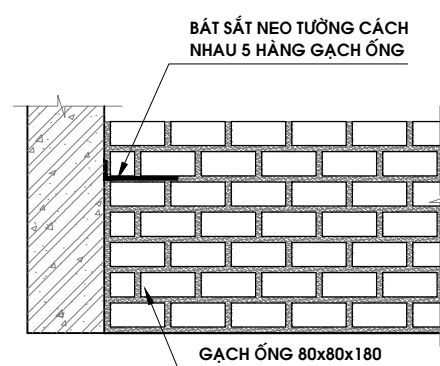

GHI CHÚ:

- ĐỐI VỚI TƯỜNG BAO CHE MẶT KHÔNG GIÁP 2 NHÀ, MẠC ĐỊNH CHIỀU DÂY TỐ THIỆU LẠ 200mm. NHÀ THƯỜNG CẦN KIỂM TRA VỊ TRÍ MẪU NHÀ TRÊN TỔNG MẶT BẰNG ĐỂ XÁC ĐỊNH VỊ TRÍ THỰC TẾ. CHIỀU DÂY TƯỜNG TRONG HỒ SƠ MẪU NHÀ CHỈ ÁP DỤNG MẪU ĐIỂN HÌNH.
- ĐỐI VỚI CỬA SỔ : CÔNG TÁC XÂY TỜ ĐƯỢC THỰC HIỆN ĐẾN BỀ CỬA SỔ, SAU 12 GIỜ (BỀ TỔNG BỀ KHỎI) TIẾN HÀNH XÂY TIẾP.
- ĐỐI VỚI CỬA ĐI: CÔNG TÁC XÂY TỜ ĐƯỢC THỰC HIỆN ĐẾN LẠNH TỖ CỬA, SAU 12 GIỜ (BỀ TỔNG LẠNH TỖ KHỎI) TIẾN HÀNH XÂY TIẾP.
- ĐỐI VỚI TƯỜNG NGOÀI: BÍT LỘ CÁC LỖ GẠCH PHÍA MẶT NGOÀI CÔNG TRÌNH TRONG QUÁ TRÌNH XÂY.
- SÁT BỒ RẪU NEO SÀN BẰNG VẬT LIỆU KẾT DÍNH VỚI ĐỘ SÂU TRÊN 100mm.

CHI TIẾT ĐÓNG TRẦN CEMBOARD ĐIỂN HÌNH		CHI TIẾT ĐÓNG TRẦN NHỰA LAM SÓNG ĐIỂN HÌNH	
CHI TIẾT ỐP ĐÁ ĐIỂN HÌNH	CHI RÃNH THU NƯỚC	CHI TIẾT KHE MẶT ĐỨNG GIỮA TƯỜNG 2 NHÀ VUÔNG GÓC	

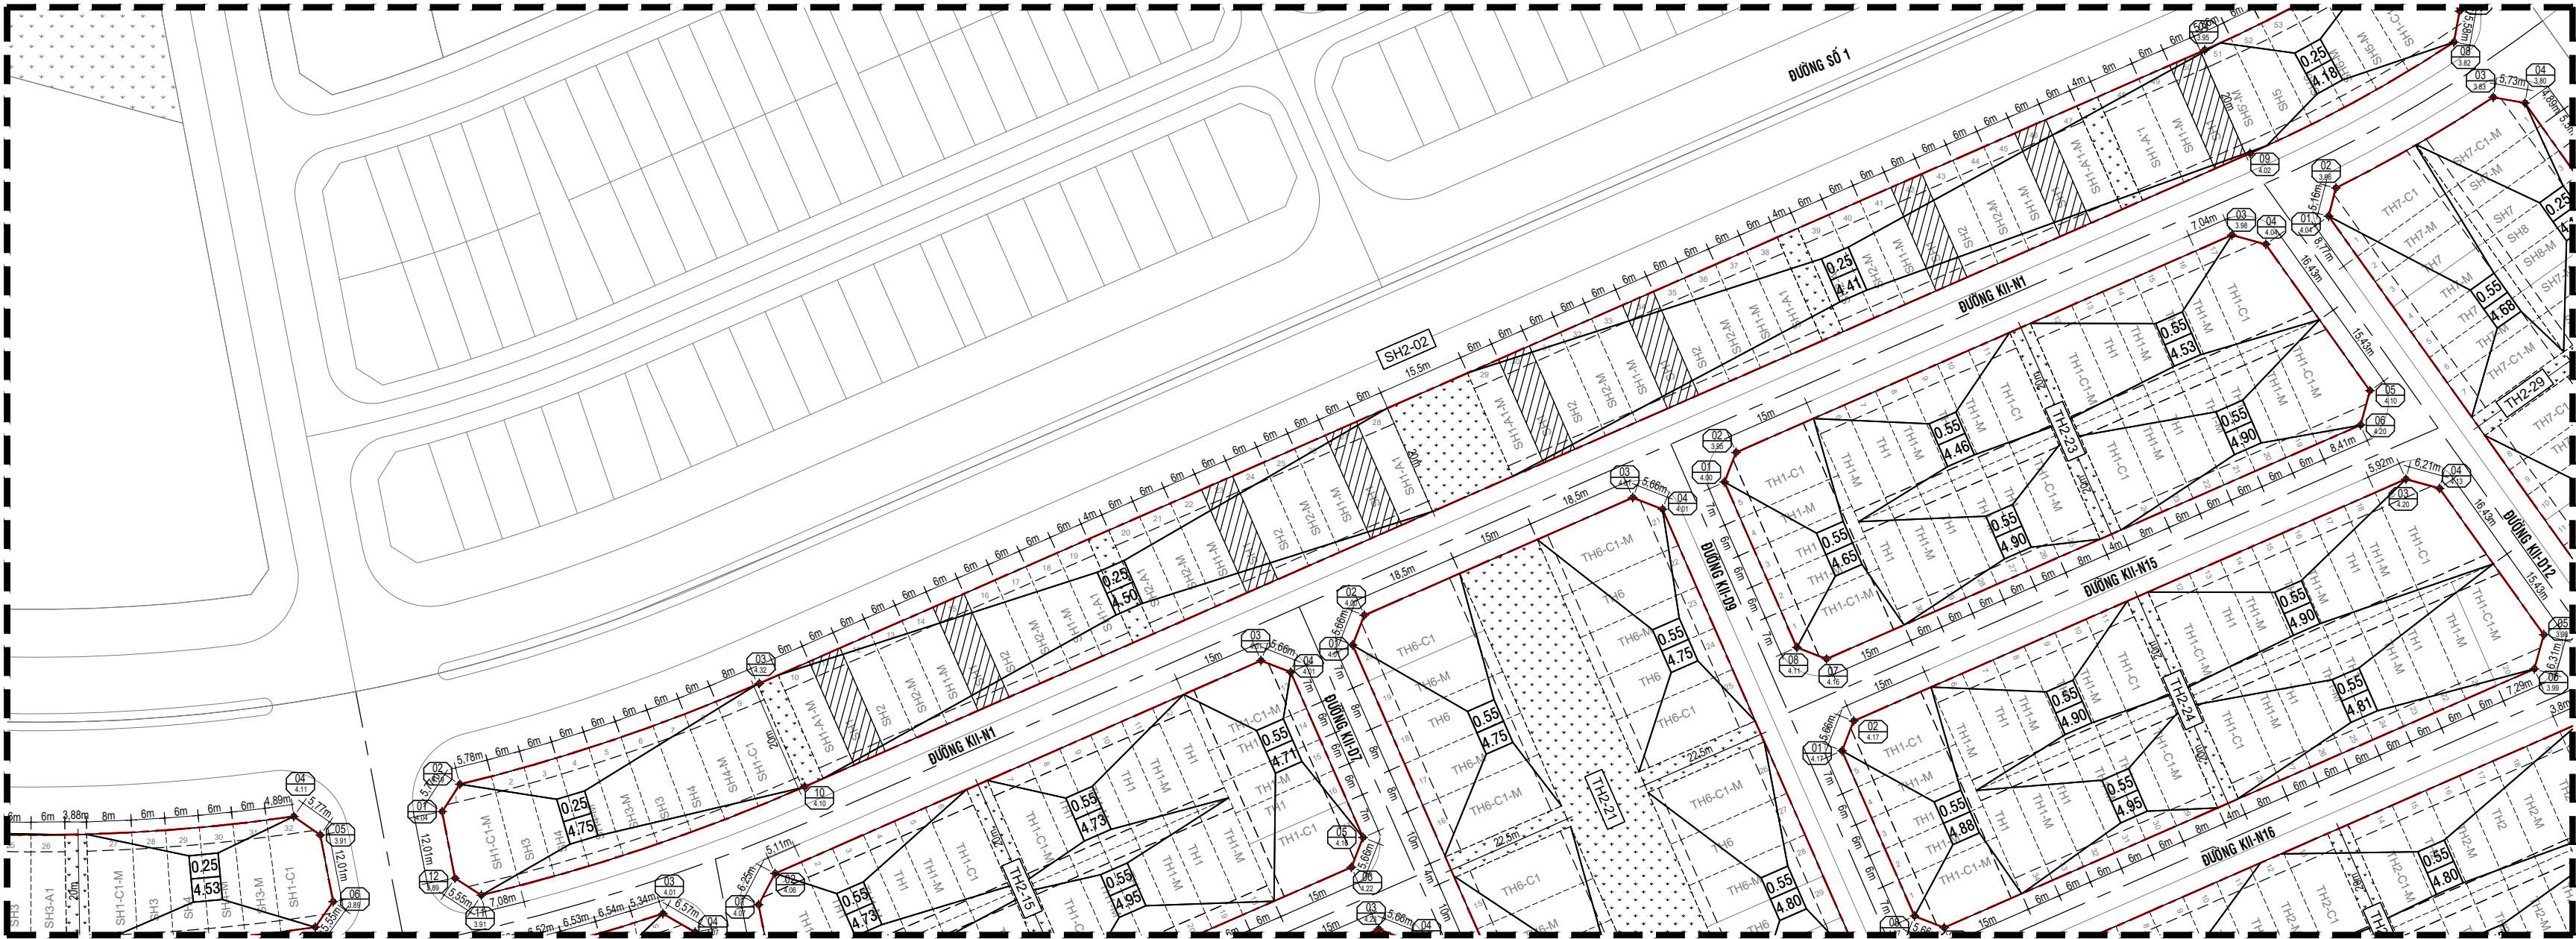


SƠ ĐỒ VỊ TRÍ LÔ ĐẤT _ TL:1/1000
KHU SH2-02


BẢNG THỐNG KÊ DIỆN TÍCH CÁC LÔ ĐẤT - MẬT ĐỘ XÂY DỰNG - TỔNG DIỆN TÍCH SÀN XÂY DỰNG																
KÝ HIỆU LÔ ĐẤT ÁP DỤNG MẪU NHÀ	MẪU NHÀ ÁP DỤNG	KÍCH THƯỚC LÔ ĐẤT XÂY DỰNG (m)	DIỆN TÍCH LÔ ĐẤT	SỐ LÔ	TỔNG DIỆN TÍCH ĐẤT	THEO THIẾT KẾ CƠ SỞ				HỆ SỐ SỬ DỤNG ĐẤT	TẦNG CAO	DIỆN TÍCH XÂY DỰNG TẦNG 1	DIỆN TÍCH XÂY DỰNG TẦNG 2		DIỆN TÍCH XÂY DỰNG TẦNG 3	
						MẬT ĐỘ XÂY DỰNG (%)	DIỆN TÍCH XÂY DỰNG 1 CĂN (m²)	TỔNG DIỆN TÍCH SÀN XÂY DỰNG 1 CĂN (m²)	TỔNG DIỆN TÍCH SÀN XÂY DỰNG TOÀN KHU (m²)				BAN CÔNG	SÀN THƯỢNG	BAN CÔNG	SÀN THƯỢNG
SH2-01	SH2-01 (2,6)	SH1	6 x 20	120,00	2	240,00	70,00	84,00	268,62	537,24	2,2	3	84,00	84,00	10,50	-
SH2-02	SH2-02 (11,15,23,27,30,34,42,46,50)	SH1	6 x 20	120,00	9	1.080,00	70,00	84,00	268,62	2.417,58	2,2	3	84,00	84,00	10,50	-

THUYẾT MINH ĐỊNH VỊ CÔNG TRÌNH


- CĂN CỨ THEO BẢN ĐỒ CẠM MỐC LỘ GIỚI ĐƯỢC CUNG CẤP BỞI CHỦ ĐẦU TƯ, TỪ ĐÓ XÁC ĐỊNH RANH PHẦN KHU ĐẤT DỰA TRÊN HỆ TOẠ ĐỘ ĐIỂM QUỐC GIA VN-2000 THEO NHỮNG ĐIỂM MỐC TOạ ĐỘ ĐỊNH VỊ PHÂN KHU NHƯ BẢNG BÊN TRÊN
- TỪ CÁC ĐIỂM MỐC TOạ PHÂN KHU SẼ ĐỊNH VỊ CÁC ĐIỂM MỐC RANH ĐẤT PHÂN LÔ. CĂN CỨ VÀO ĐIỂM MỐC RANH ĐẤT PHÂN LÔ SẼ XÁC ĐỊNH TRỰC CHỈNH CÔNG TRÌNH THEO BẢN VẼ.

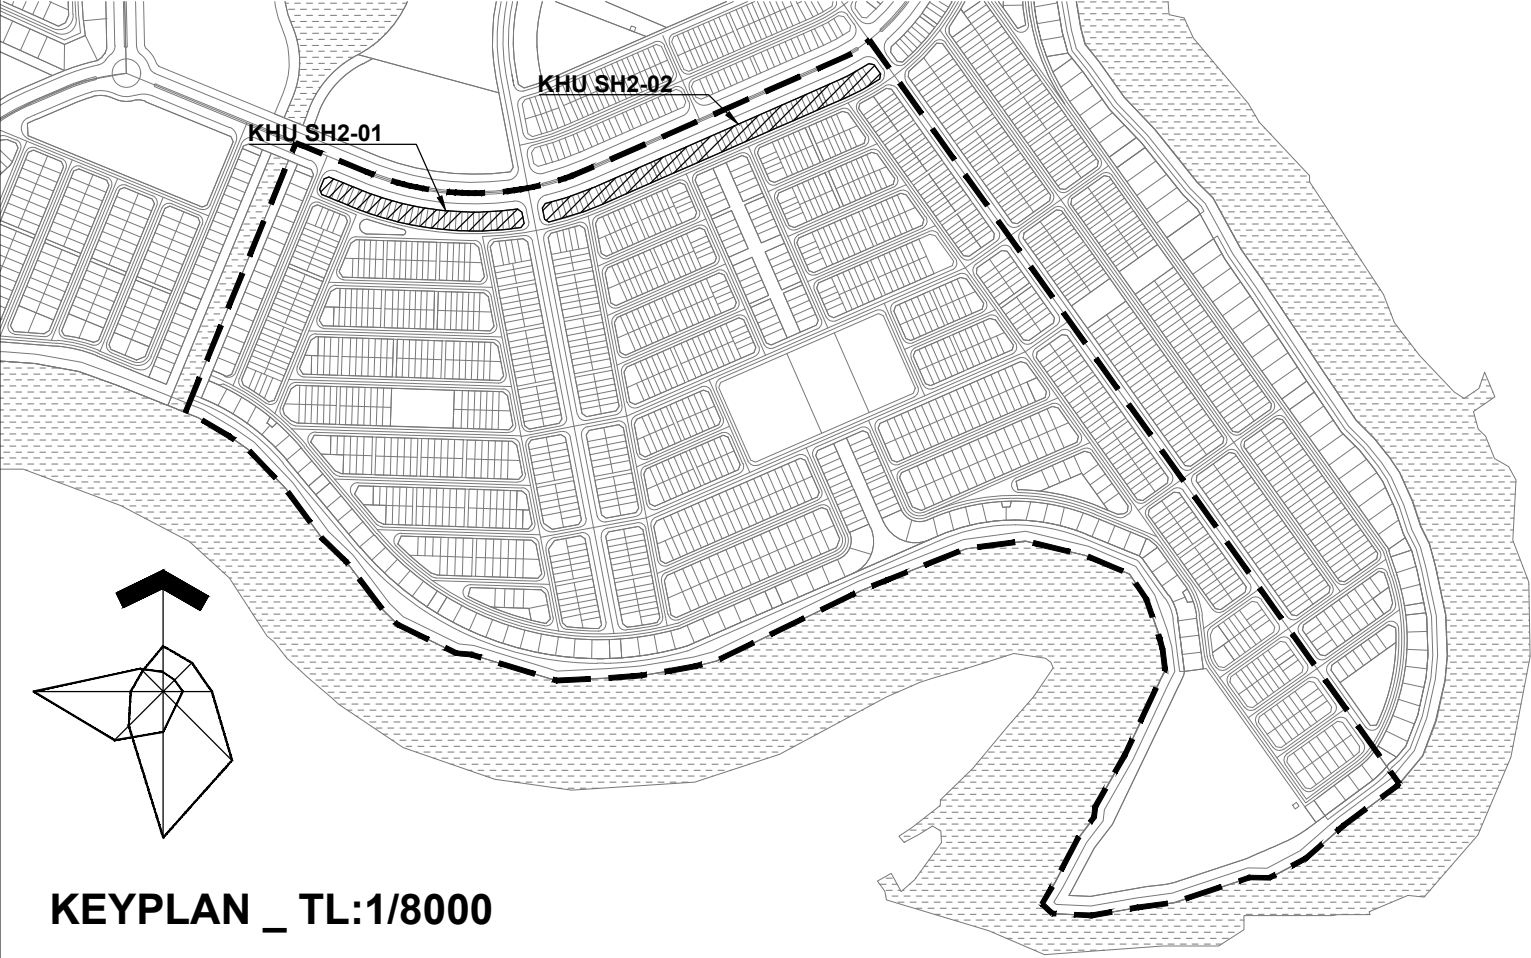

KEYPLAN _ TL:1/8000

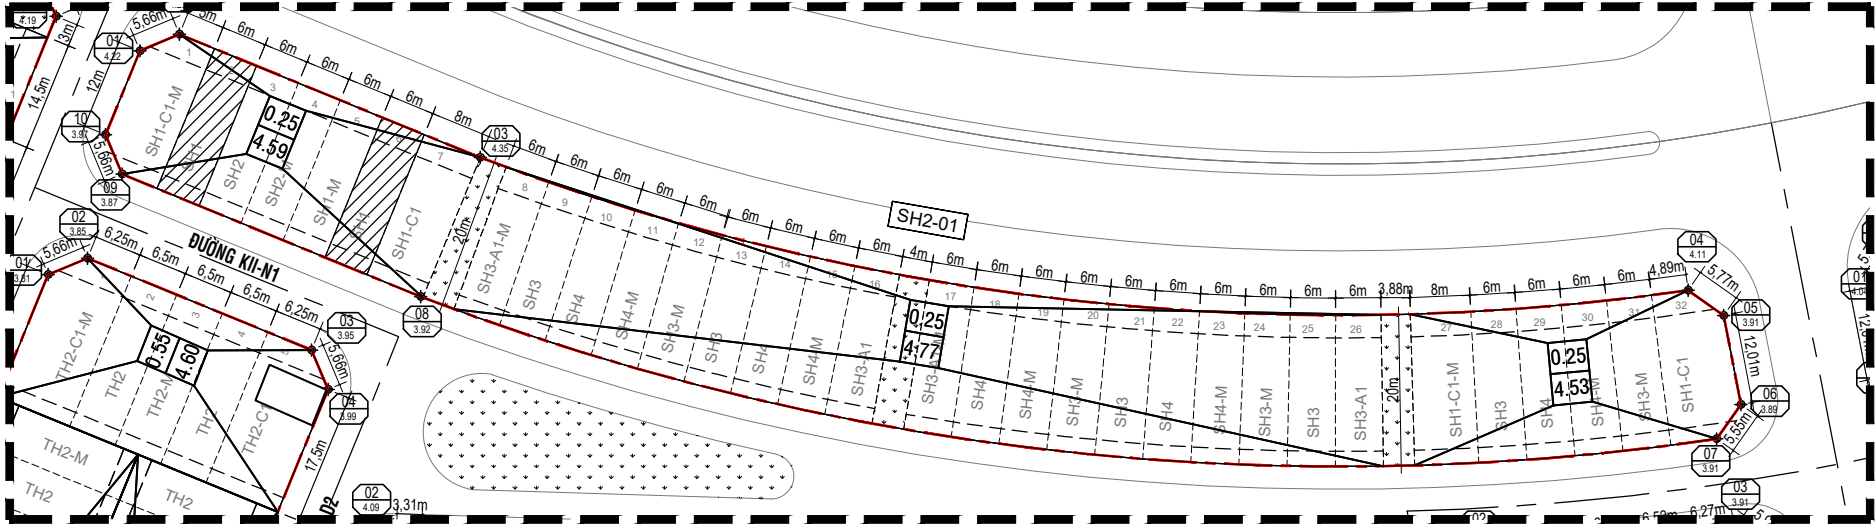

SƠ ĐỒ VỊ TRÍ LÔ ĐẤT _ TL:1/1000
KHU SH2-01

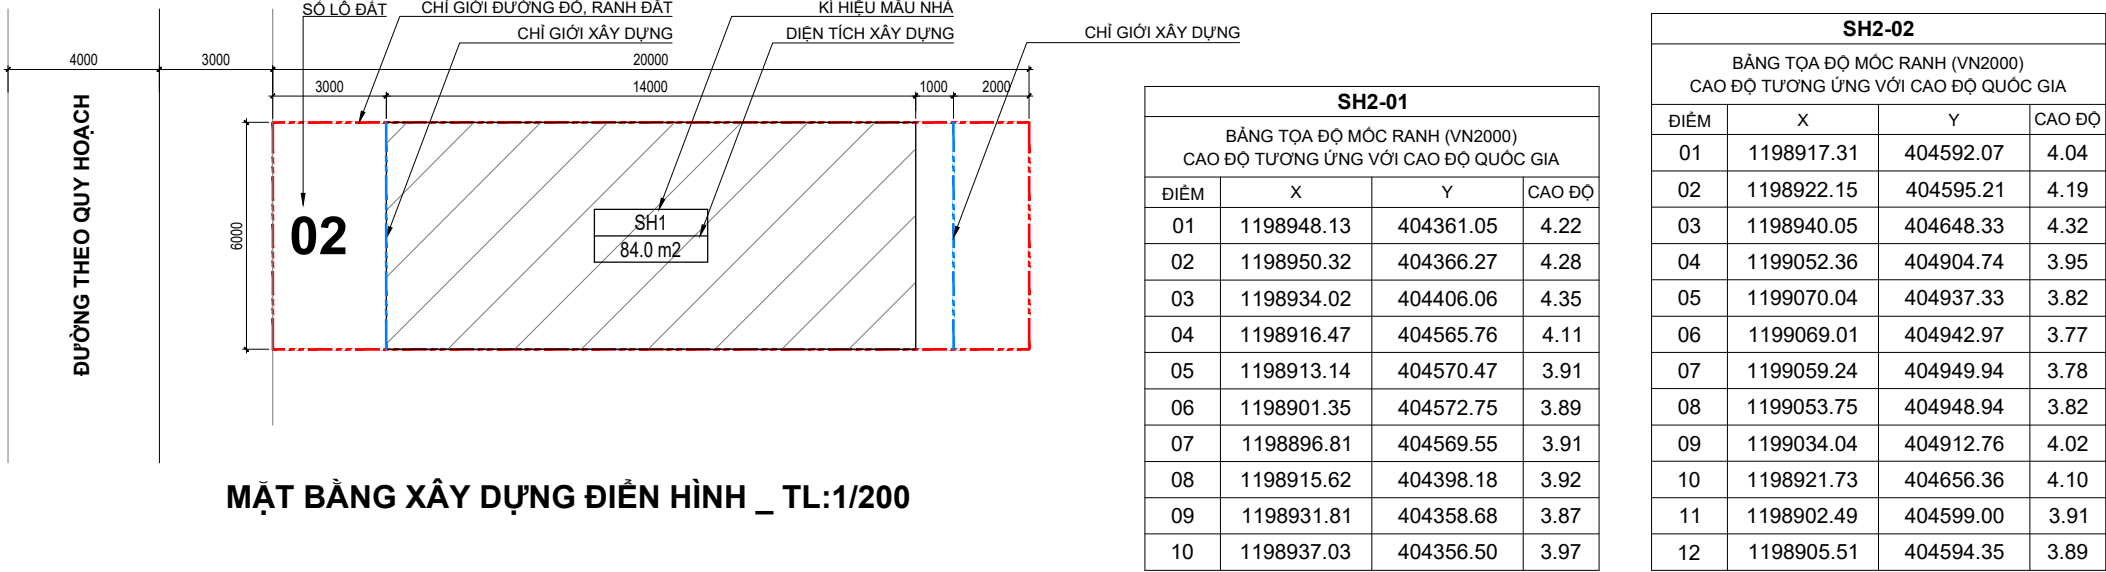


GHI CHÚ: CAO ĐỘ ±0.00 TRONG BẢN VẼ TƯƠNG ỨNG CAO ĐỘ HỒN DẦU TẠI VĨA HÉ. CAO ĐỘ VĨA HÉ VUI LÒNG XEM CÁC BẢN VẼ "THIẾT KẾ HẠ TẦNG"



MẶT ĐỨNG TRÍCH ĐOẠN GHÉP CĂN TRƯỚC _ TL:1/100




MẶT ĐỨNG TRÍCH ĐOẠN GHÉP CĂN SAU _ TL:1/100

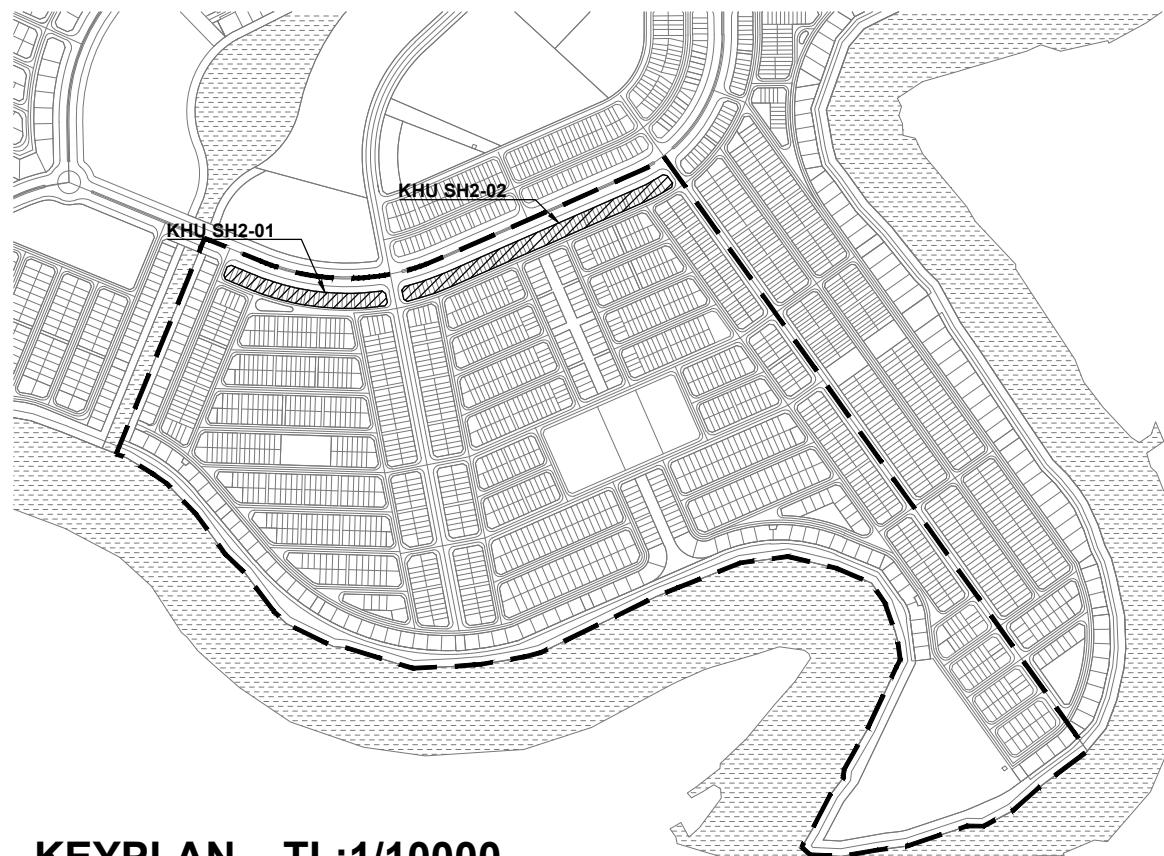


KEYPLAN _ TL:1/10000
GHI CHÚ: CAO ĐỘ ±0.00 TRONG BẢN VẼ TƯƠNG ỨNG CAO ĐỘ HÒN DẦU TẠI VÍA HÉ. CAO ĐỘ VÍA HÉ "VUI LÒNG XEM CÁC BẢN VẼ "THIẾT KẾ HẠ TẦNG"

BẢNG THỐNG KÊ DIỆN TÍCH CÁC LÔ ĐẤT - MẶT ĐỘ XÂY DỰNG - TỔNG DIỆN TÍCH SÀN XÂY DỰNG																			
	KÝ HIỆU LÔ ĐẤT ÁP DỤNG MẪU NHÀ	MẪU NHÀ ÁP DỤNG	KÍCH THƯỚC LÔ ĐẤT XÂY DỰNG (m)	DIỆN TÍCH LÔ ĐẤT	SỐ LÔ	TỔNG DIỆN TÍCH ĐẤT	THEO THIẾT KẾ CƠ SỞ				HỆ SỐ SỬ DỤNG ĐẤT	TẦNG CAO	DIỆN TÍCH XÂY DỰNG TẦNG 1	DIỆN TÍCH XÂY DỰNG TẦNG 2			DIỆN TÍCH XÂY DỰNG TẦNG 3		
							MẶT ĐỘ XÂY DỰNG (%)	DIỆN TÍCH XÂY DỰNG 1 CĂN (m²)	TỔNG DIỆN TÍCH SÀN XÂY DỰNG 1 CĂN (m²)	TỔNG DIỆN TÍCH SÀN XÂY DỰNG TOÀN KHU (m²)					BÀN CÔNG	SÂN THƯỢNG		BÀN CÔNG	SÂN THƯỢNG
SH2-01	SH2-01 (2,6)	SH1	6 x 20	120,00	2	240,00	70,00	84,00	268,62	537,24	2,2	3	84,00	84,00	10,50	-	82,30	7,82	-
SH2-02	SH2-02 (11,15,23,27,30,34,42,46,50)	SH1	6 x 20	120,00	9	1.080,00	70,00	84,00	268,62	2.417,58	2,2	3	84,00	84,00	10,50	-	82,30	7,82	-

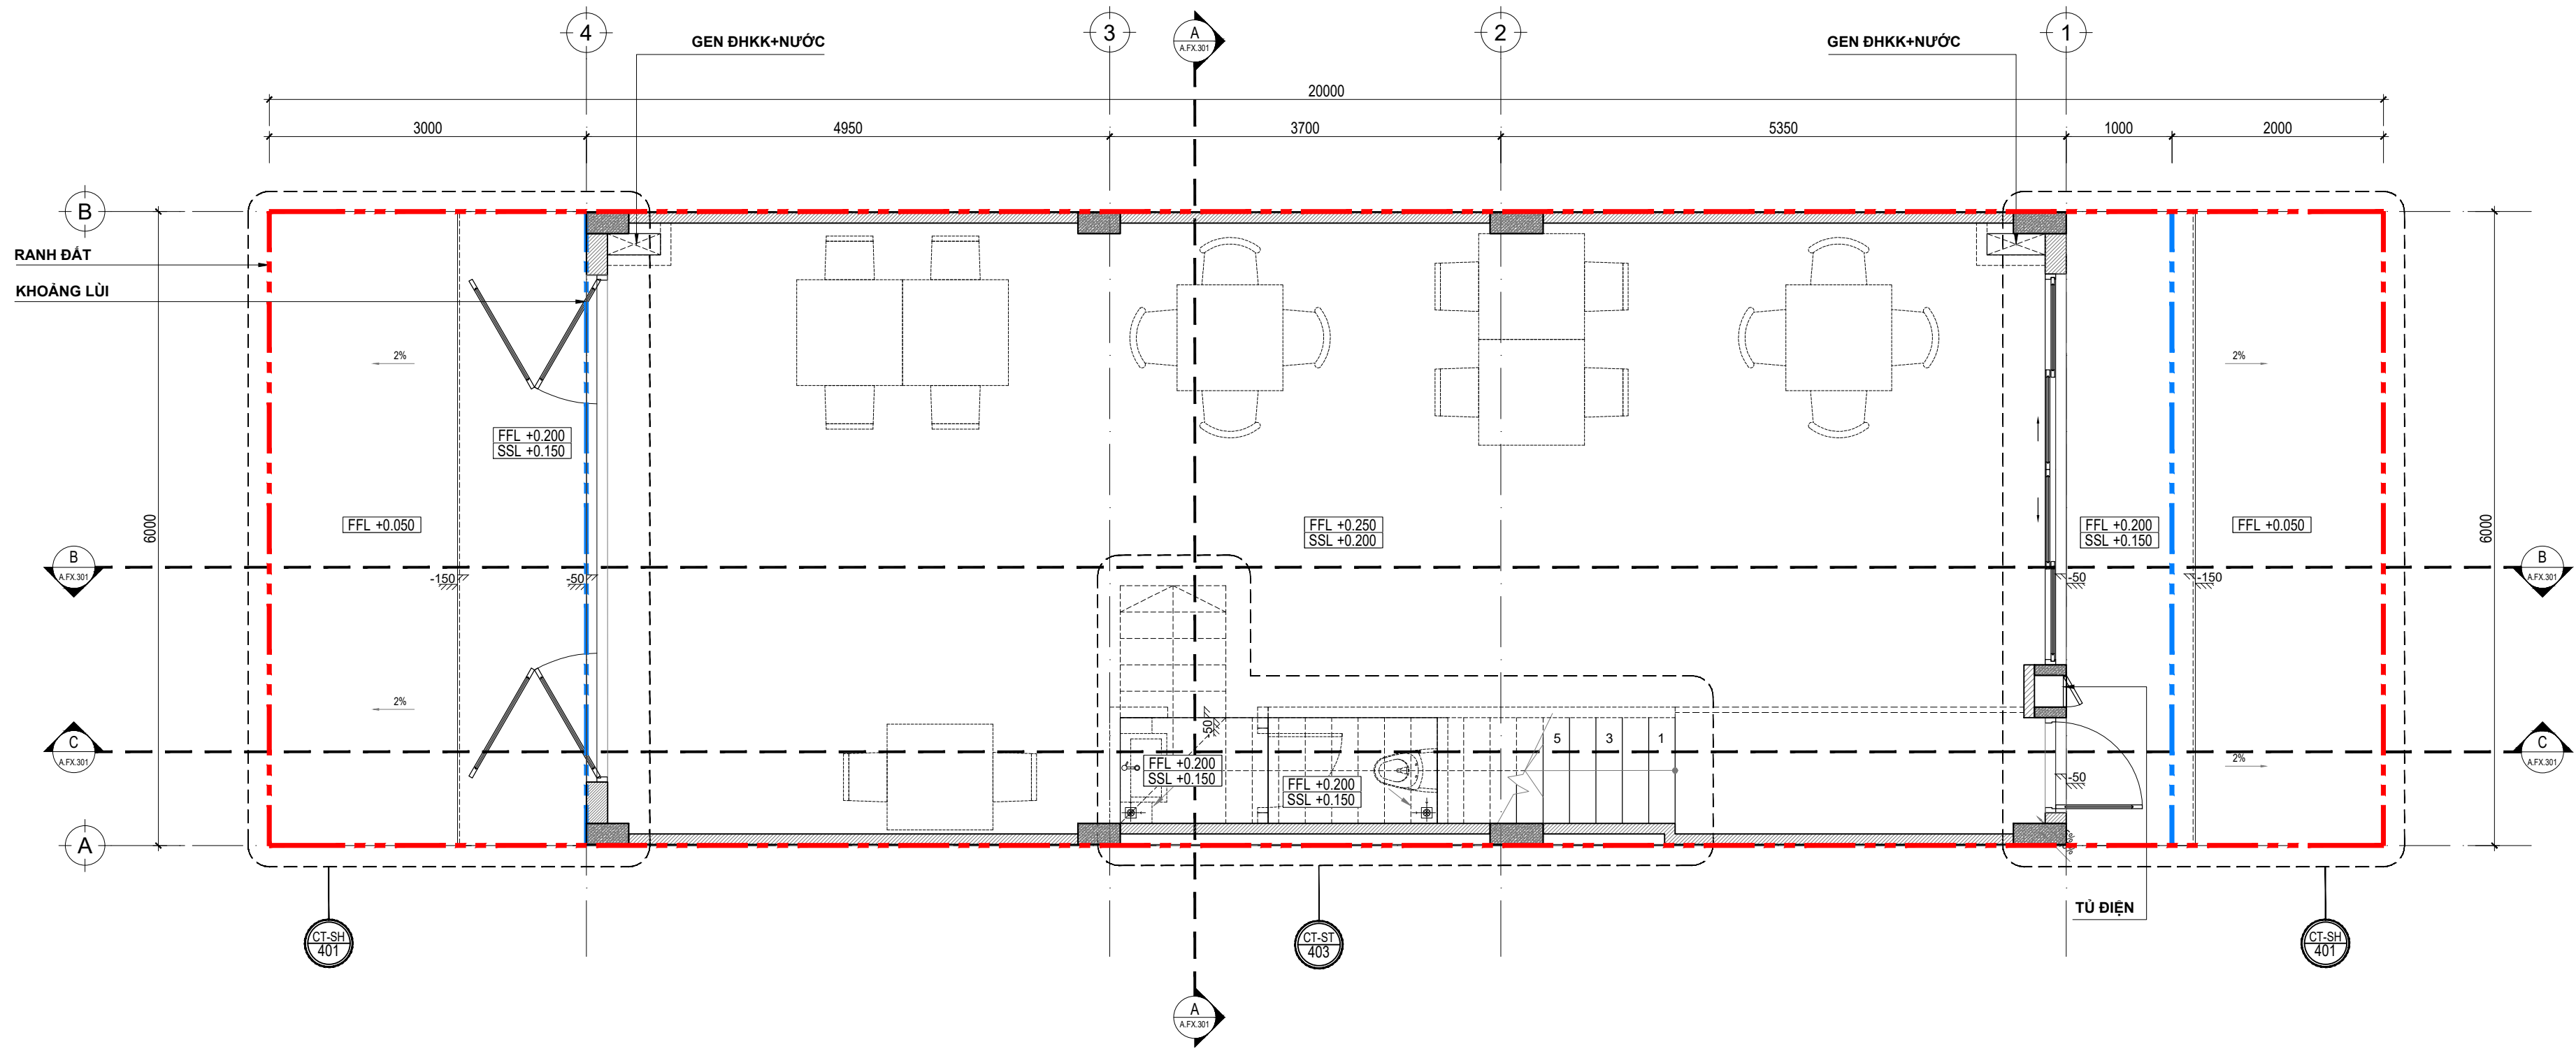


MẶT BẰNG KIẾN TRÚC TẦNG 1 _ TL:1/50

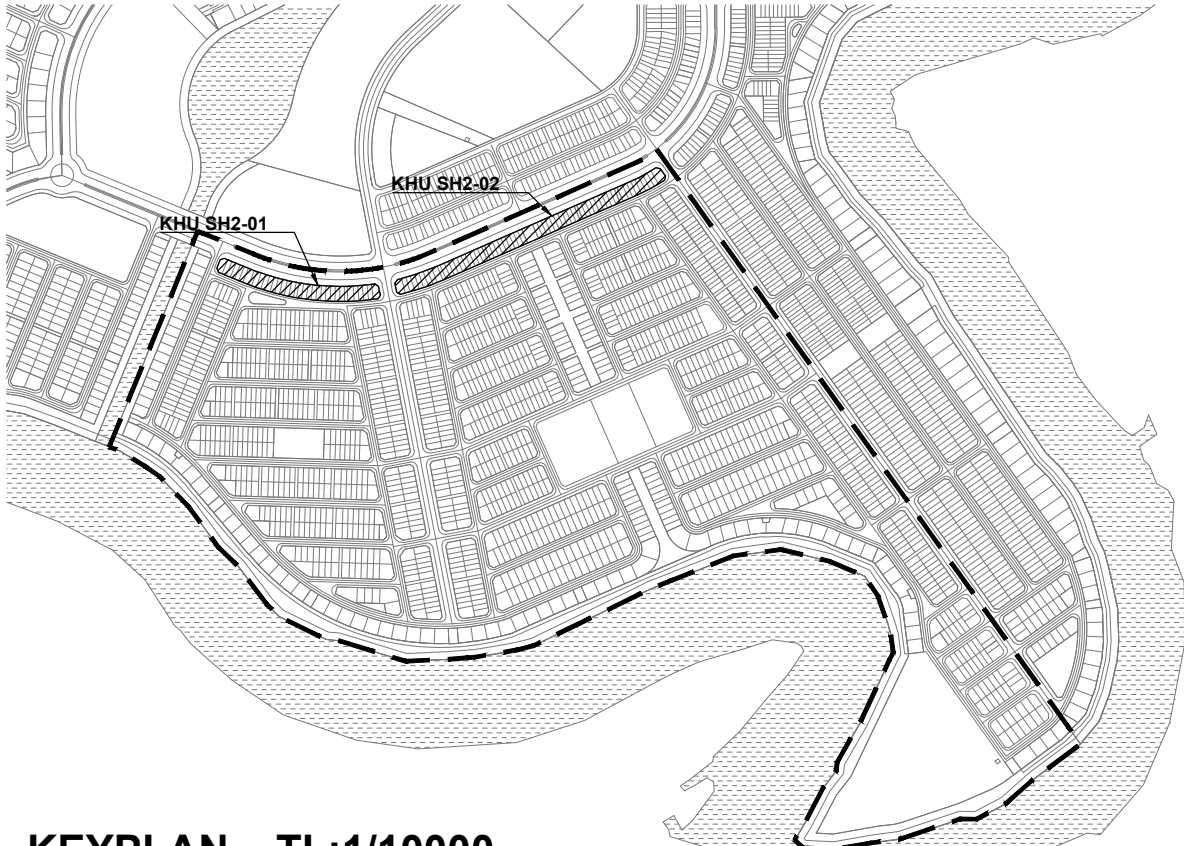


KEYPLAN _ TL:1/10000

GHI CHÚ: CAO ĐỘ ±0.00 TRONG BẢN VẼ TƯƠNG ỨNG CAO ĐỘ HÒN DẦU TẠI VĨA HÉ. CAO ĐỘ VĨA HÉ "VUI LÒNG XEM CÁC BẢN VẼ "THIẾT KẾ HẠ TẦNG"

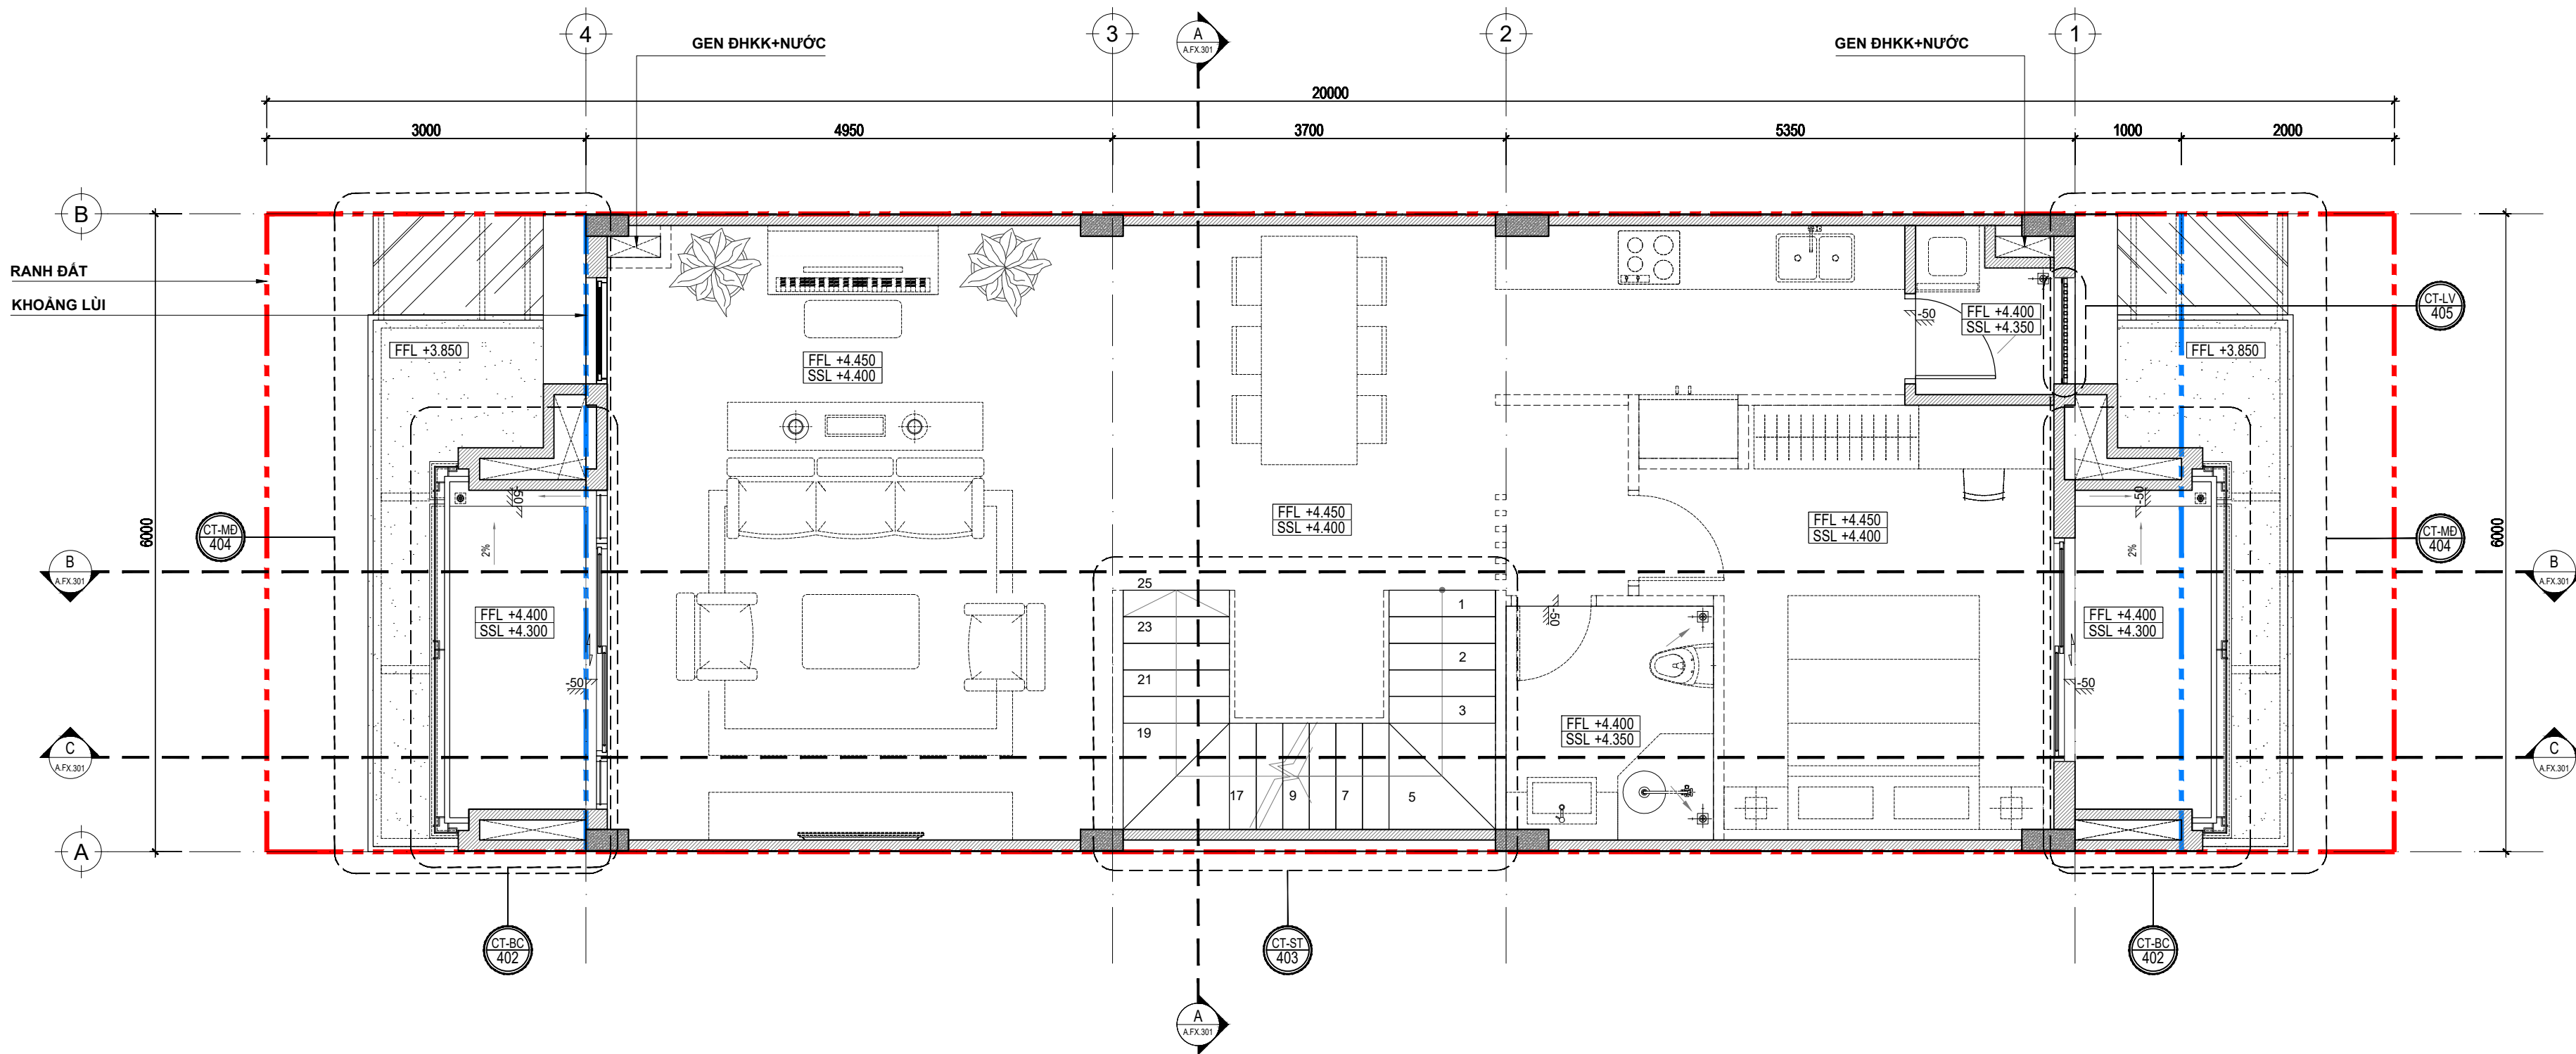


MẶT BẰNG KIẾN TRÚC TẦNG 2 _ TL:1/50

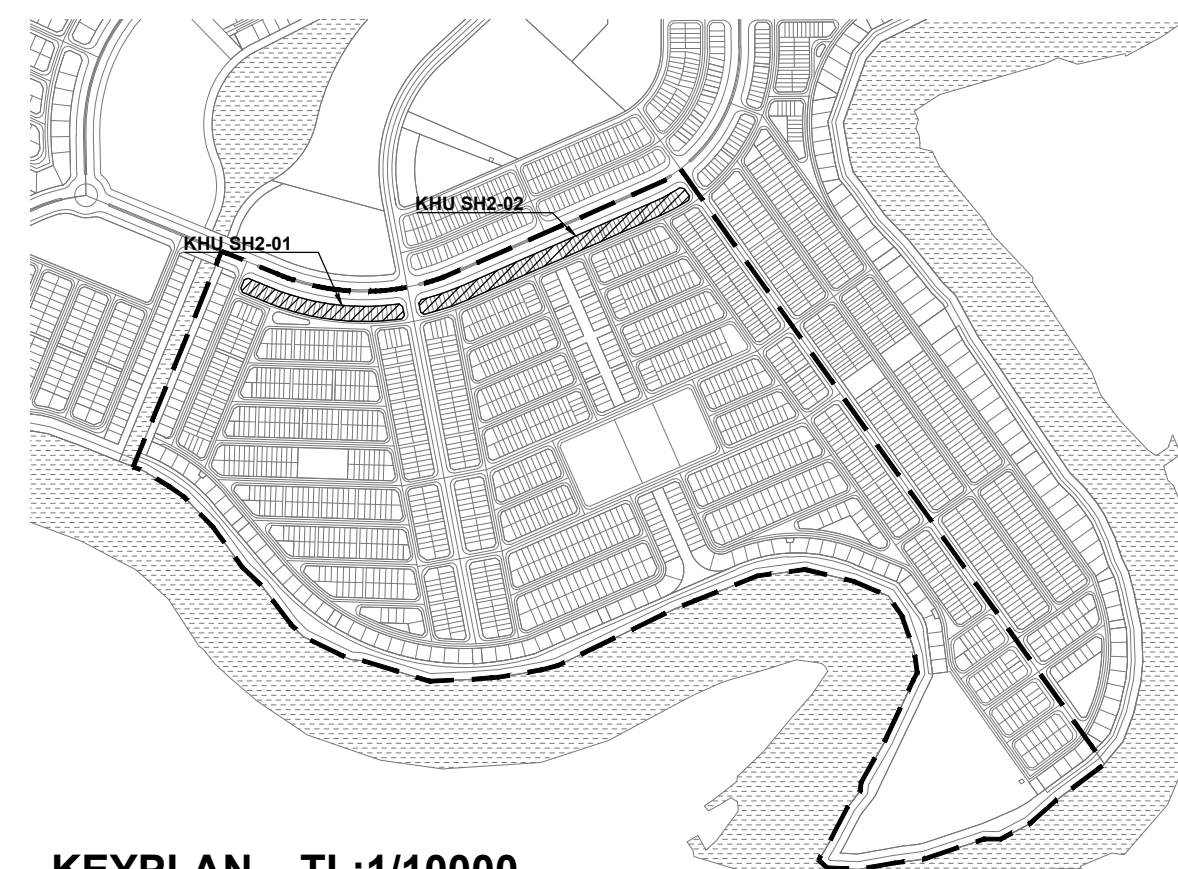


KEYPLAN _ TL:1/10000

GHI CHÚ: CAO ĐỘ ±0.00 TRONG BẢN VẼ TƯƠNG ỨNG CAO ĐỘ HỒN DẦU TẠI VĨA HÉ. CAO ĐỘ VĨA HÉ "VUI LÒNG XEM CÁC BẢN VẼ "THIẾT KẾ HẠ TẦNG"

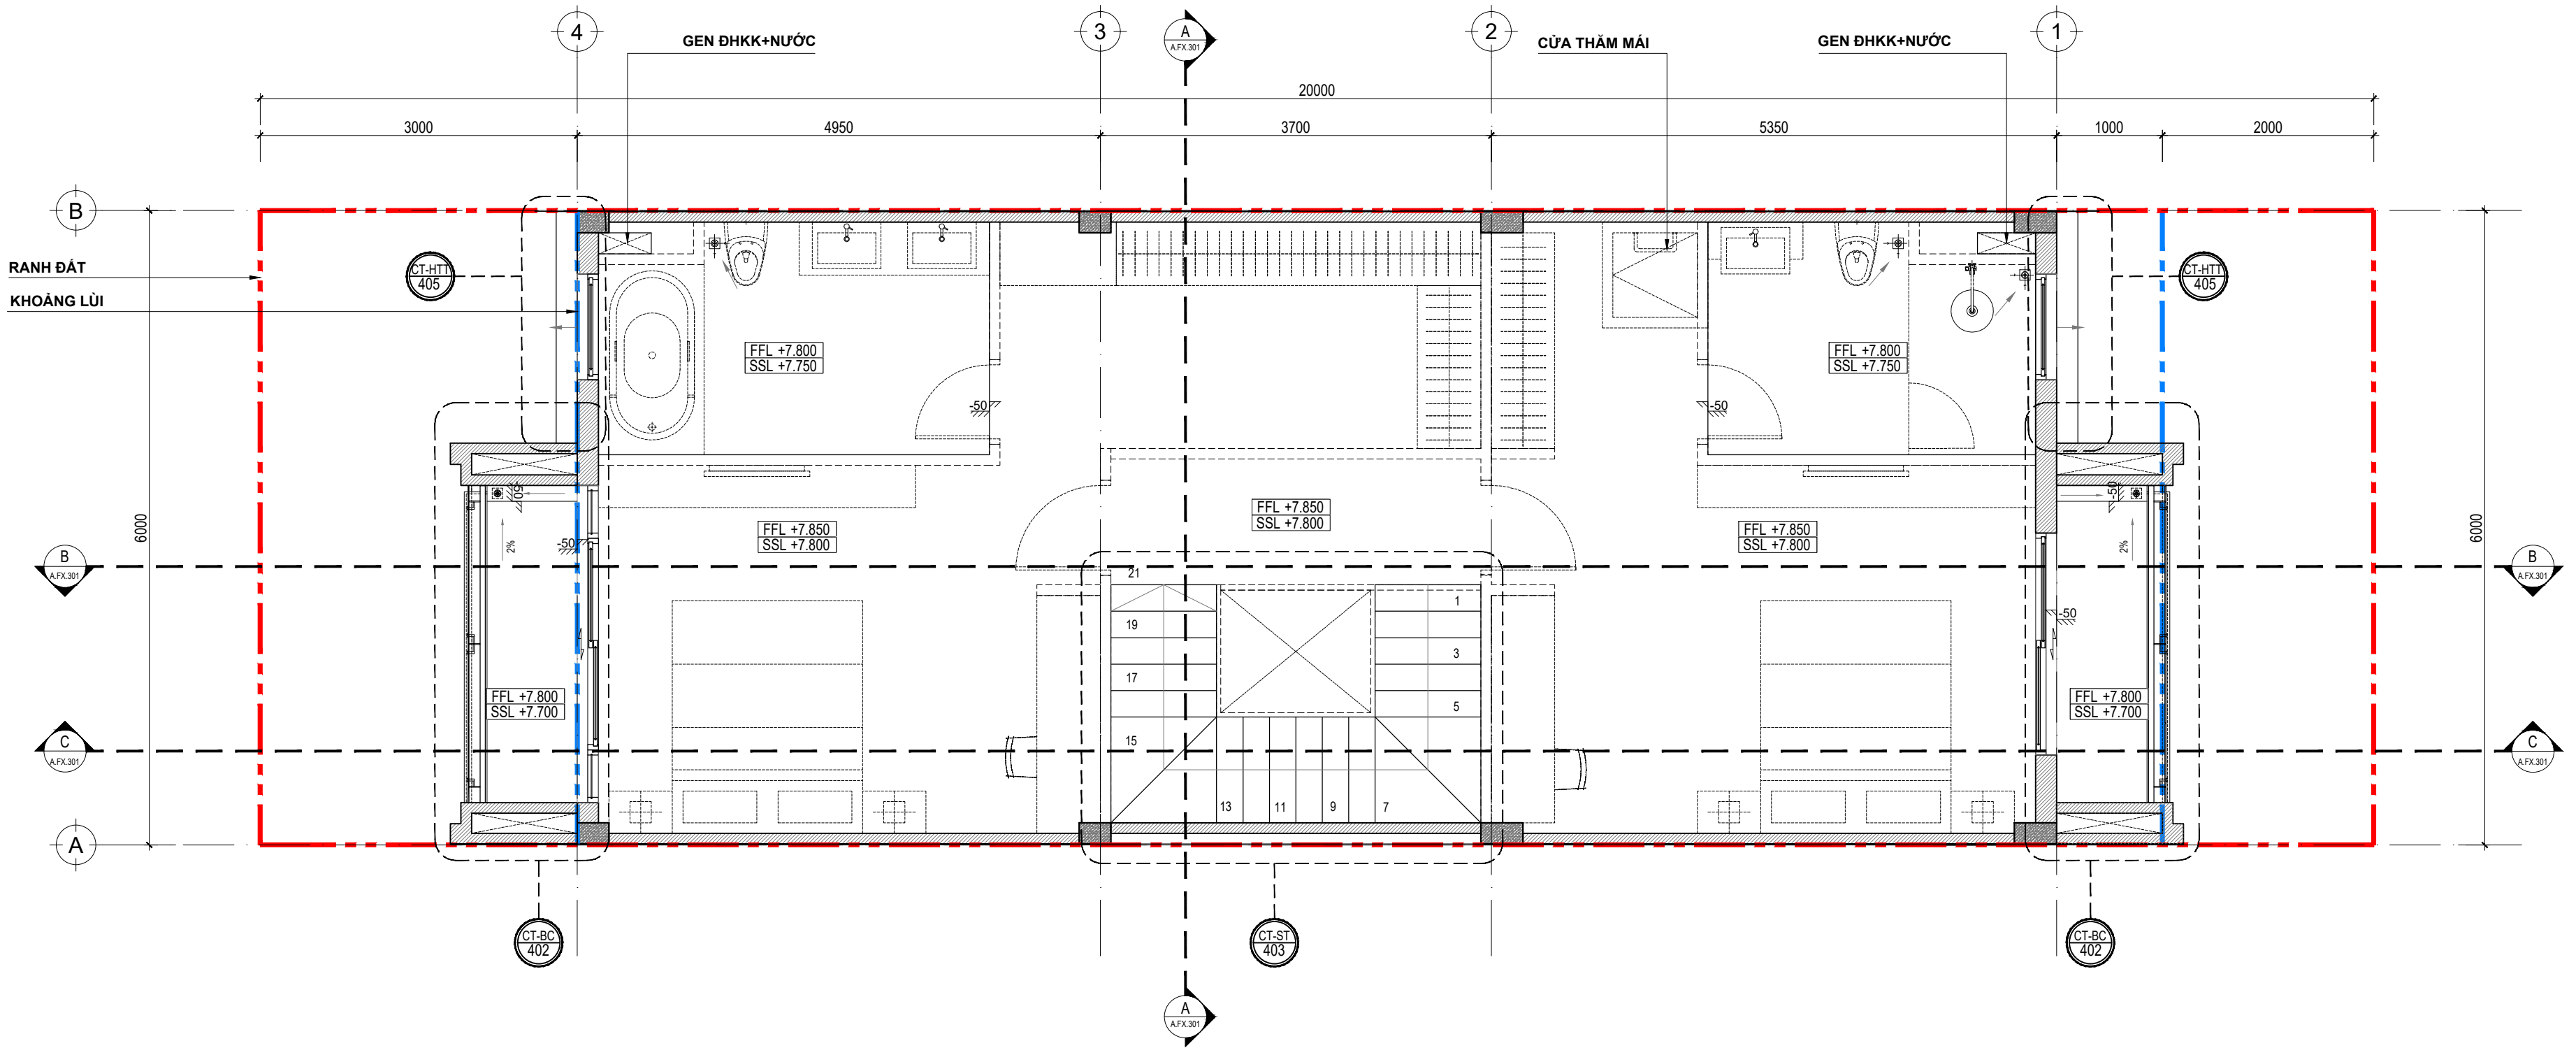


MẶT BẰNG KIẾN TRÚC TẦNG 3 _ TL:1/50

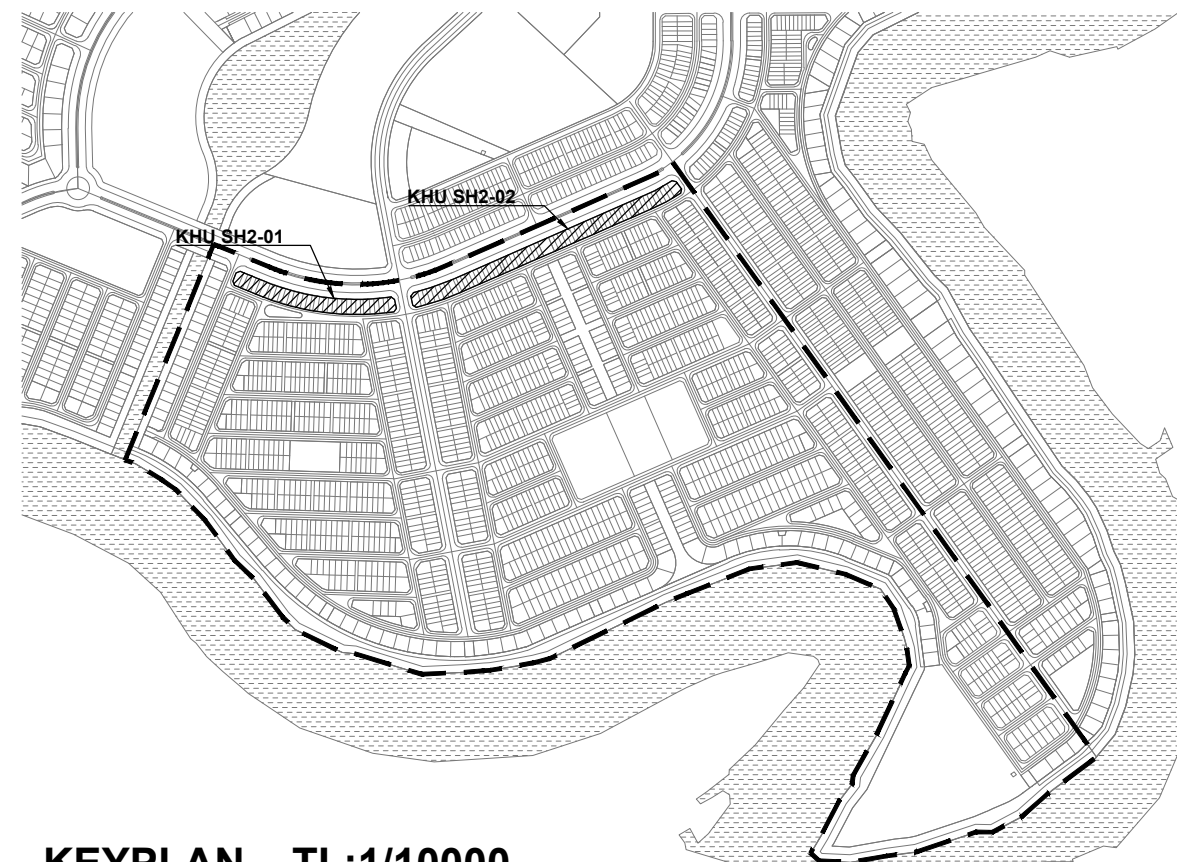


KEYPLAN _ TL:1/10000

GHI CHÚ: CAO ĐỘ ±0.00 TRONG BẢN VẼ TƯƠNG ỨNG CAO ĐỘ HỒN DẦU TẠI VÍA HÉ. CAO ĐỘ VÍA HÉ "VUI LÒNG XEM CÁC BẢN VẼ "THIẾT KẾ HẠ TẦNG"

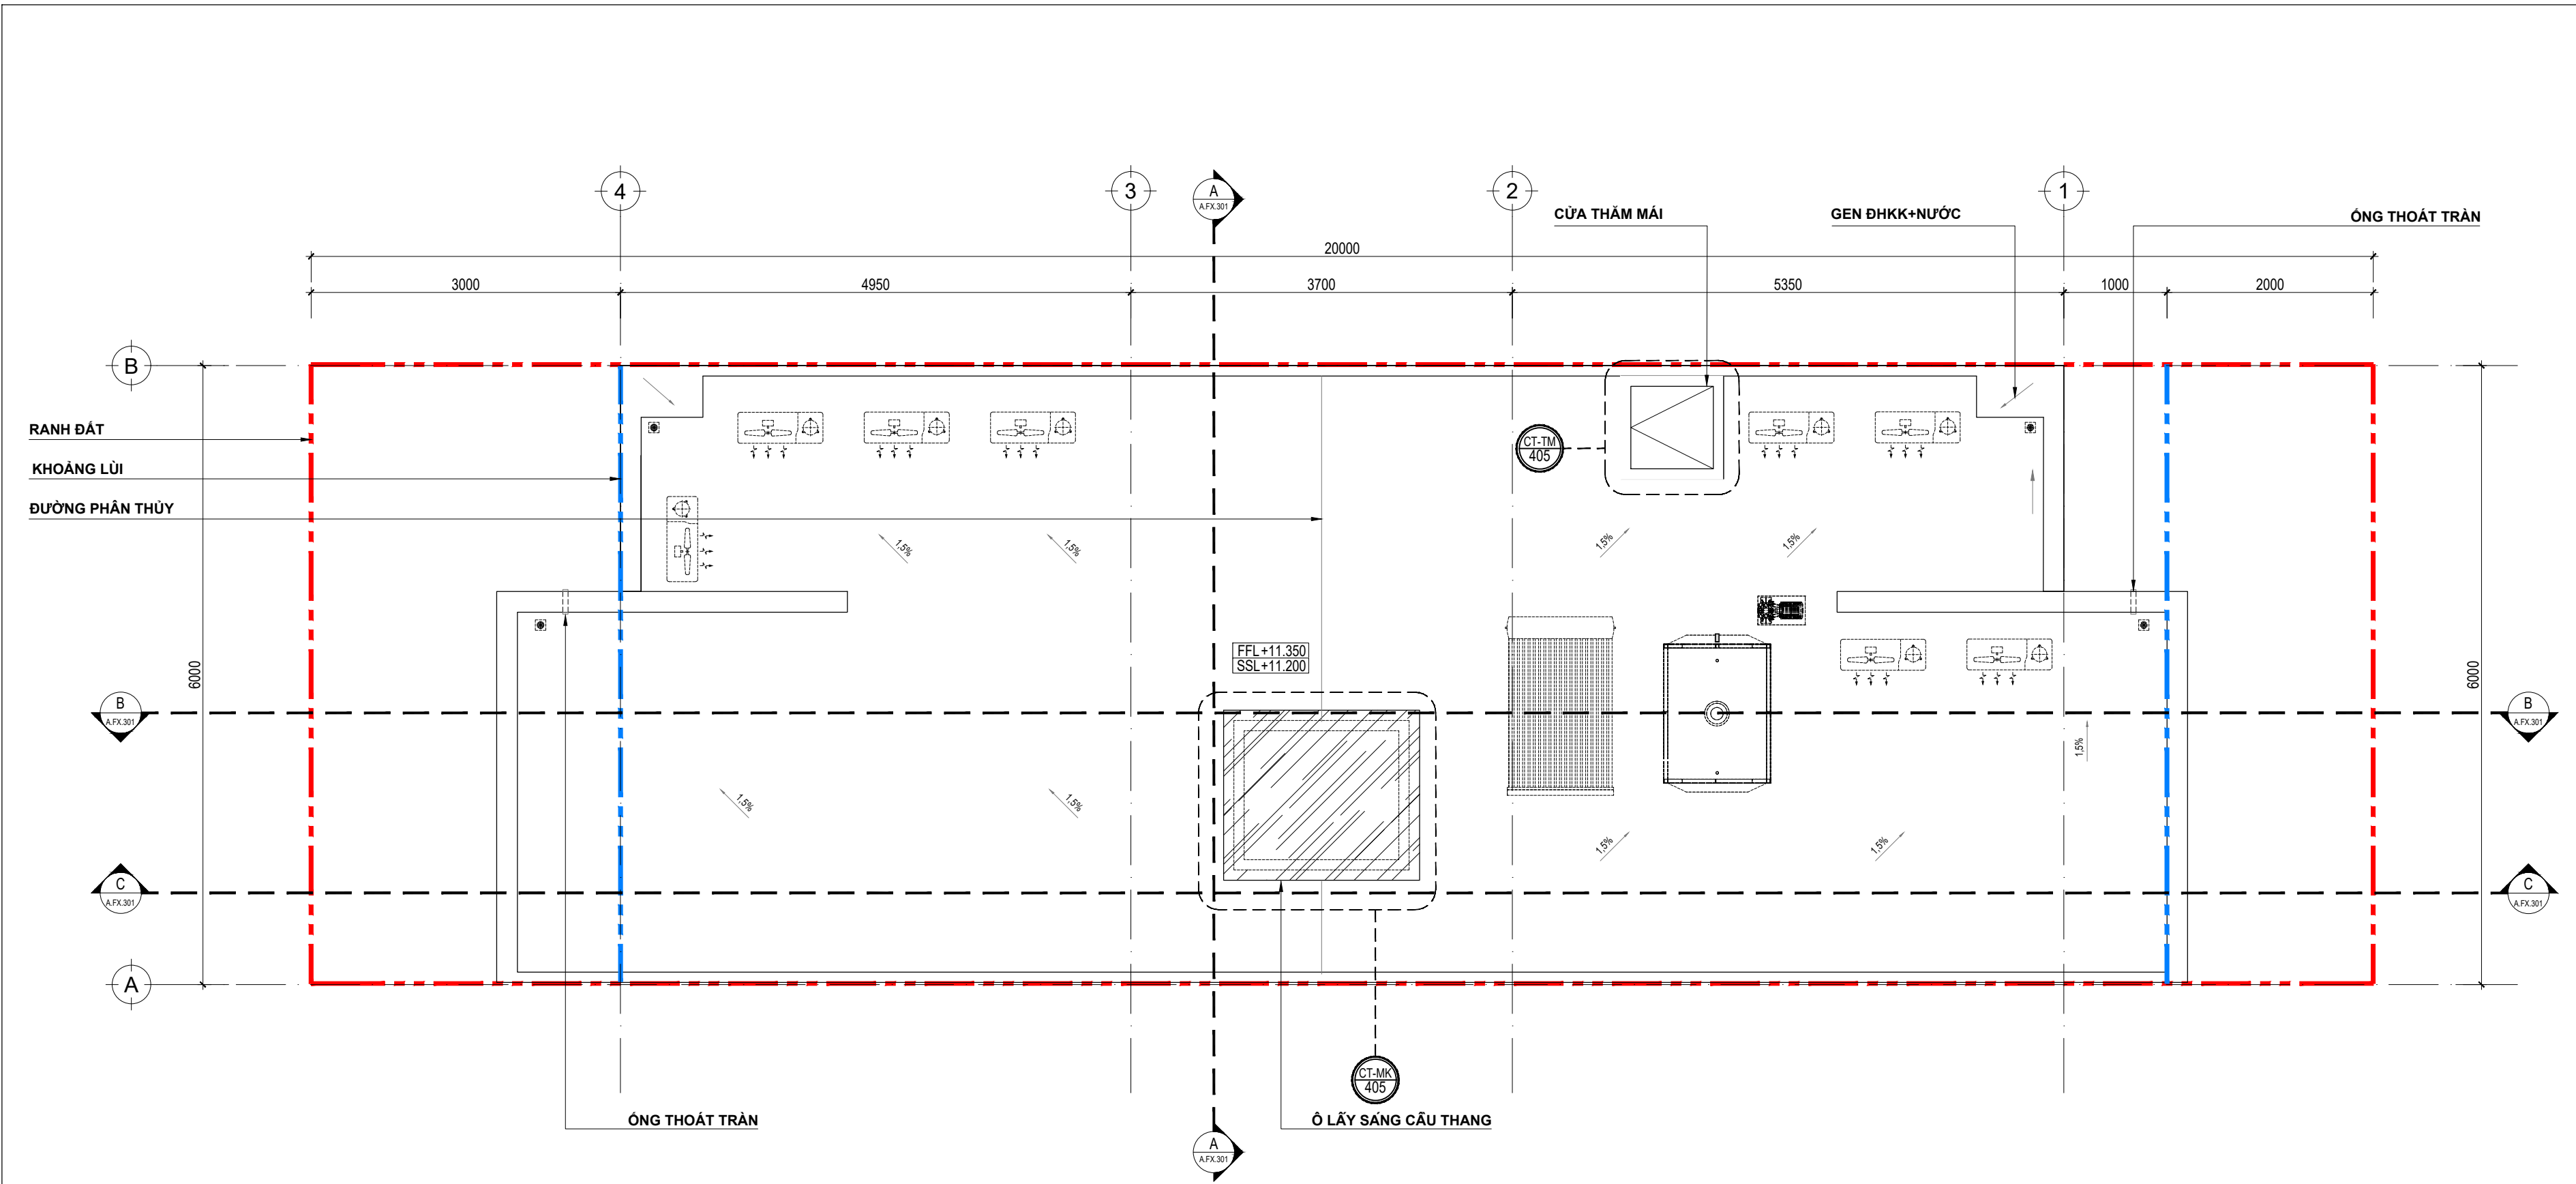

MẶT BẰNG KIẾN TRÚC TẦNG MÁI_ TL:1/50

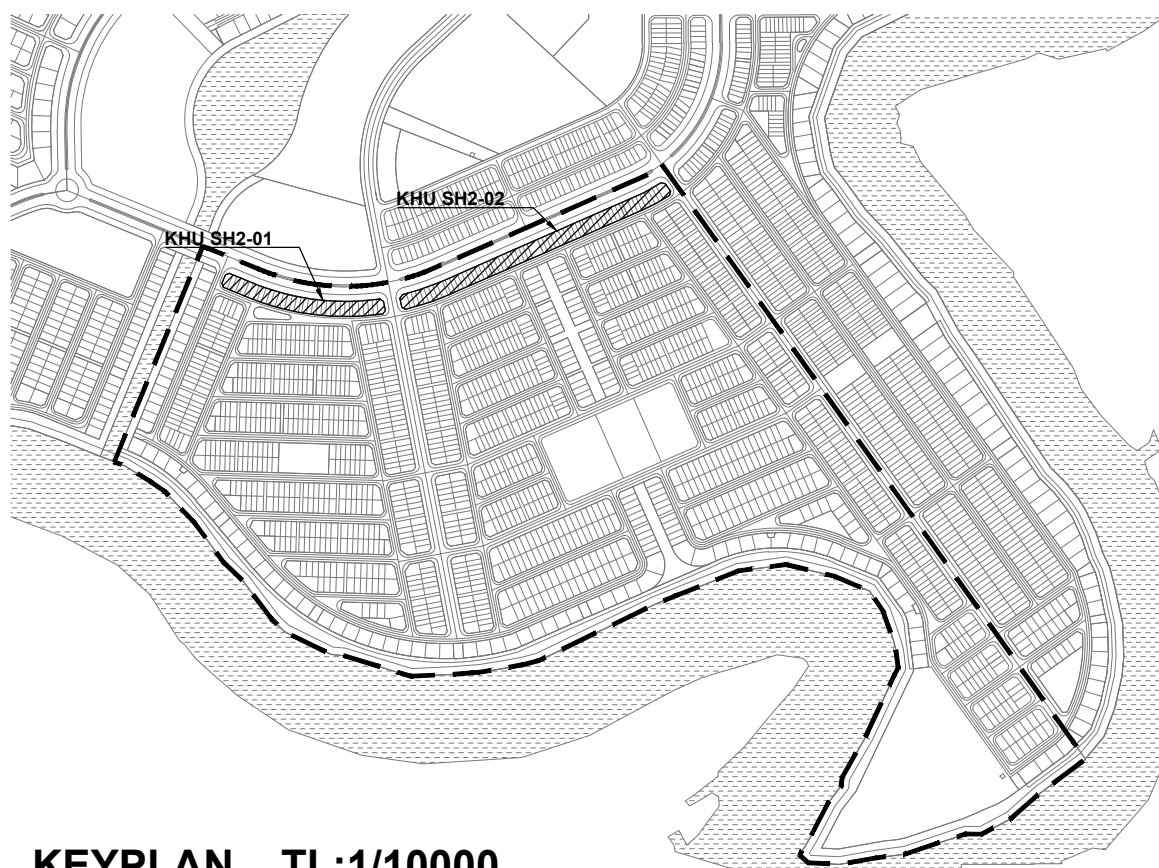


KEYPLAN_ TL:1/10000

GHI CHÚ: CAO ĐỘ ±0.00 TRONG BẢN VẼ TƯƠNG ỨNG CAO ĐỘ HẸN ĐẦU TẠI VÍA HÉ. CAO ĐỘ VÍA HÉ "VUI LÒNG XEM CÁC BẢN VẼ "THIẾT KẾ HẠ TẦNG"




	CHỐNG MỐI NỀN
	HÀO CHỐNG MỐI TRONG, NGOÀI

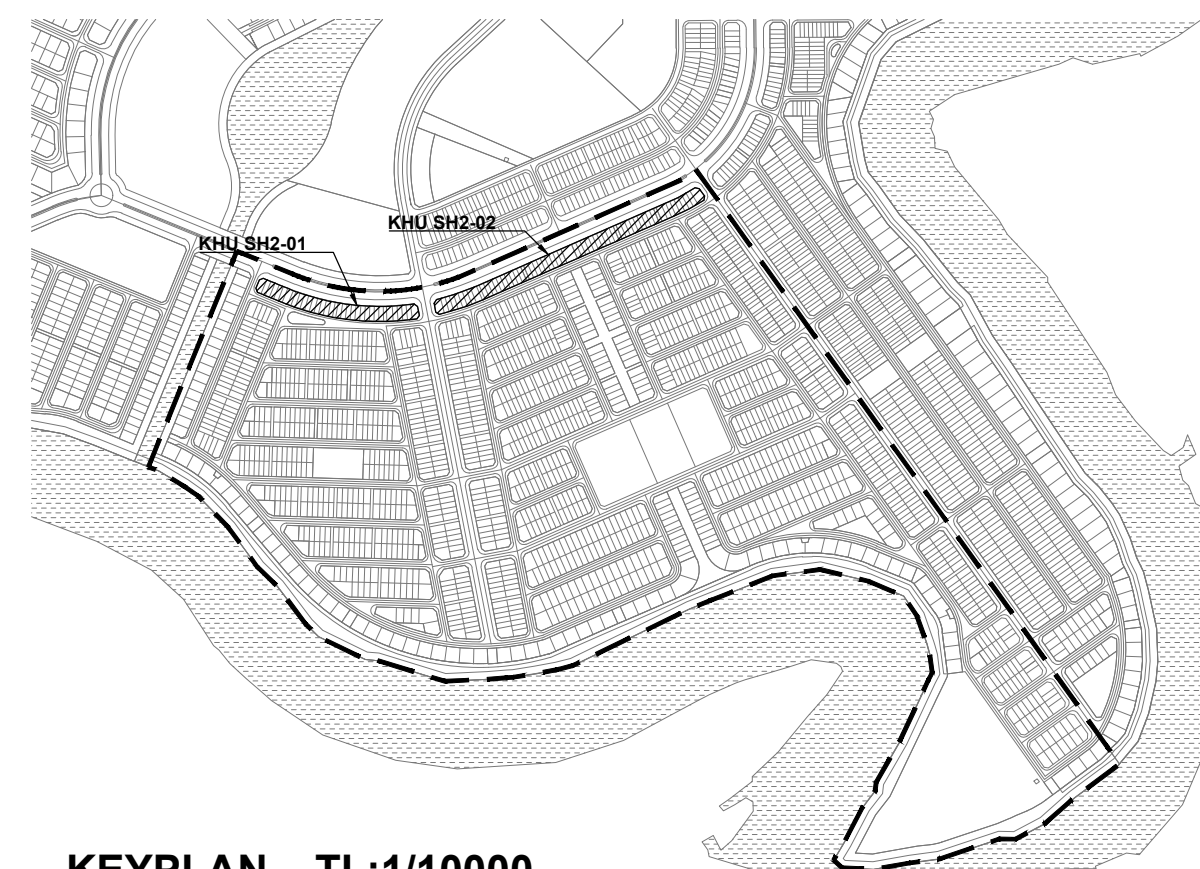


KEYPLAN _ TL:1/10000

GHI CHÚ: CAO ĐỘ ± 0.00 TRONG BẢN VẼ TƯƠNG ỨNG CAO ĐỘ HÒN DẦU TẠI VĨA HÉ. CAO ĐỘ VĨA HÉ VUI LÒNG XEM CÁC BẢN VẼ "THIẾT KẾ HẠ TẦNG"

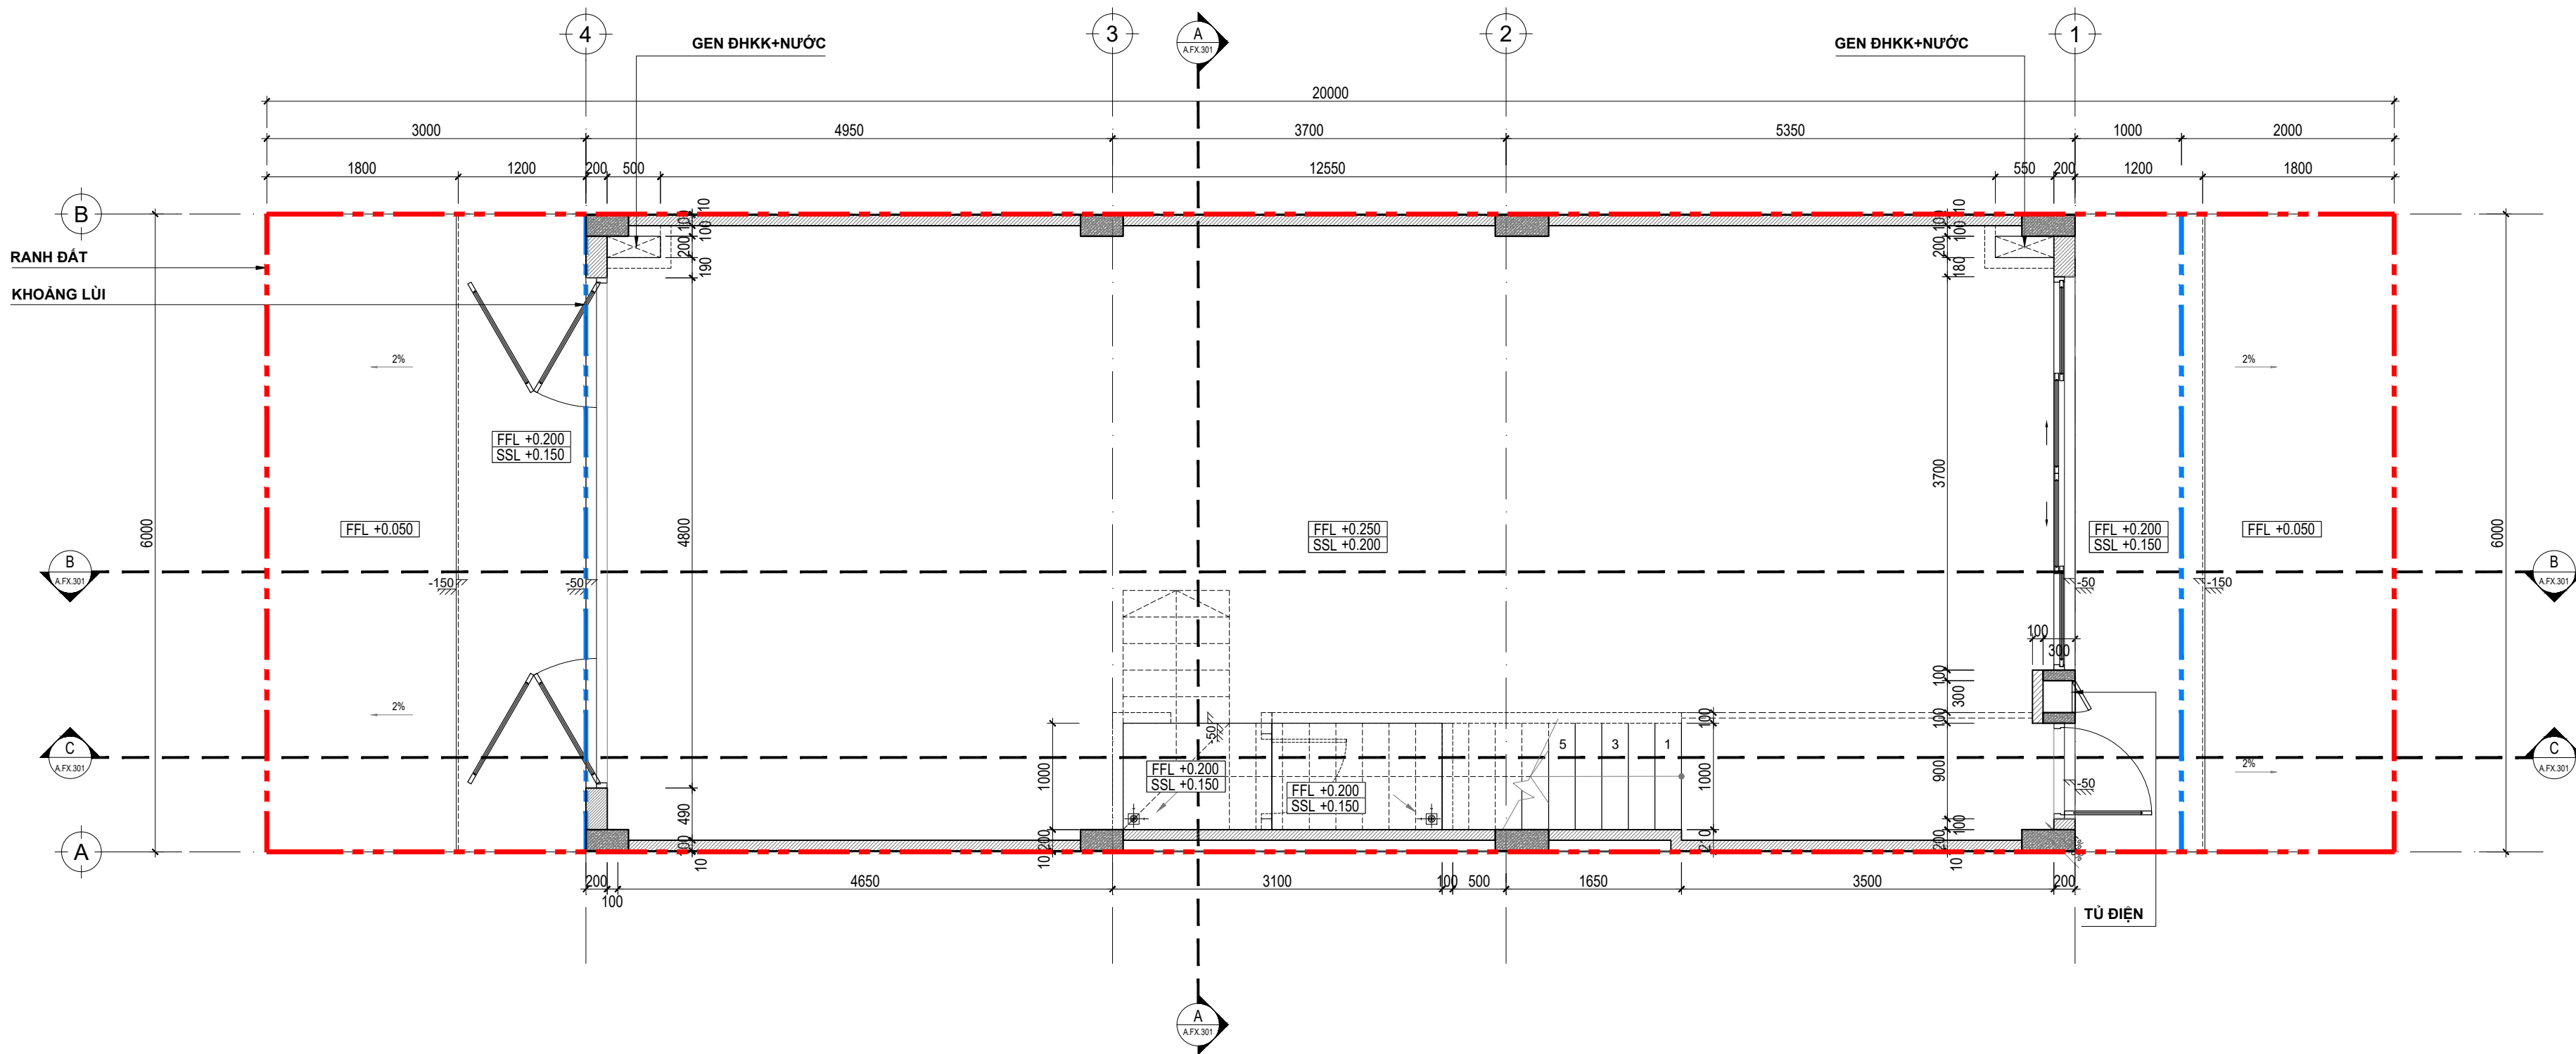


MẶT BẰNG KÍCH THƯỚC TẦNG 1 _ TL:1/50

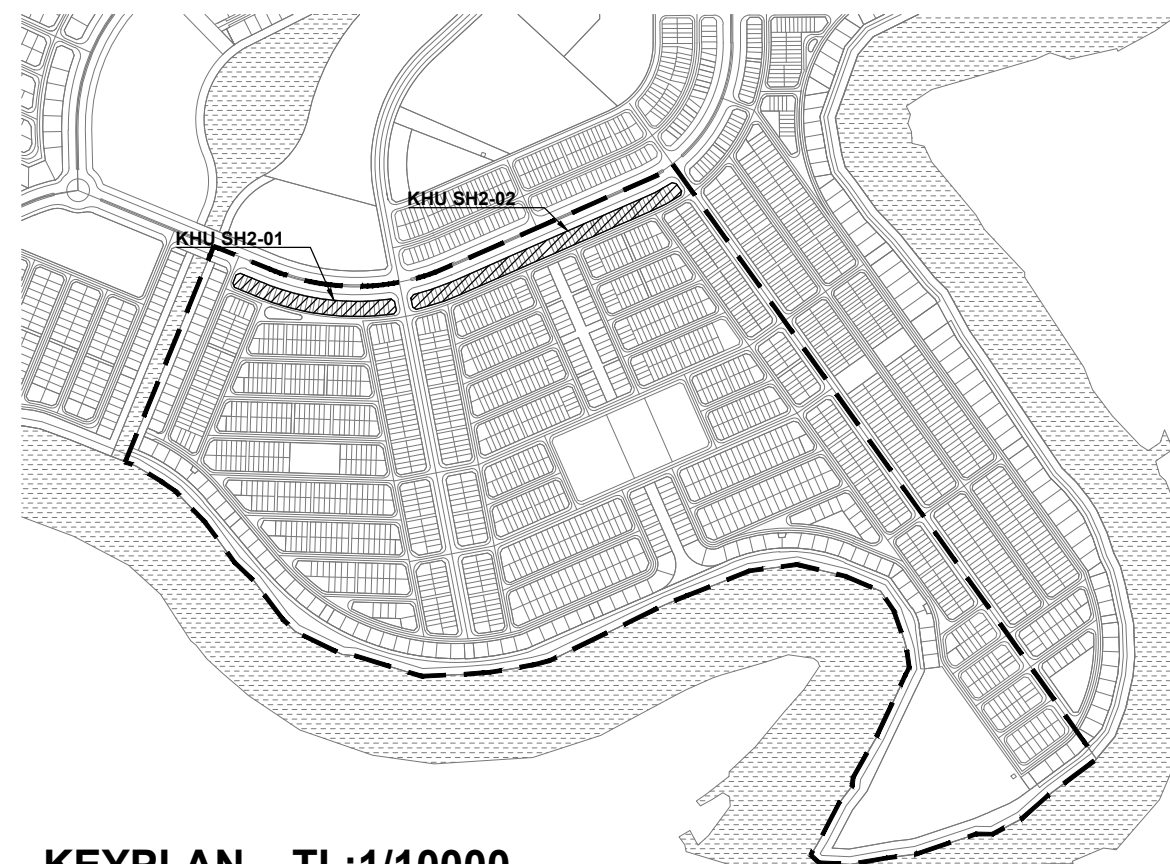


KEYPLAN _ TL:1/10000

GHI CHÚ: CAO ĐỘ ±0.00 TRONG BẢN VẼ TƯƠNG ỨNG CAO ĐỘ HẸN ĐẦU TẠI VÍA HÉ. CAO ĐỘ VÍA HÉ "VUI LÒNG XEM CÁC BẢN VẼ "THIẾT KẾ HẠ TẦNG"

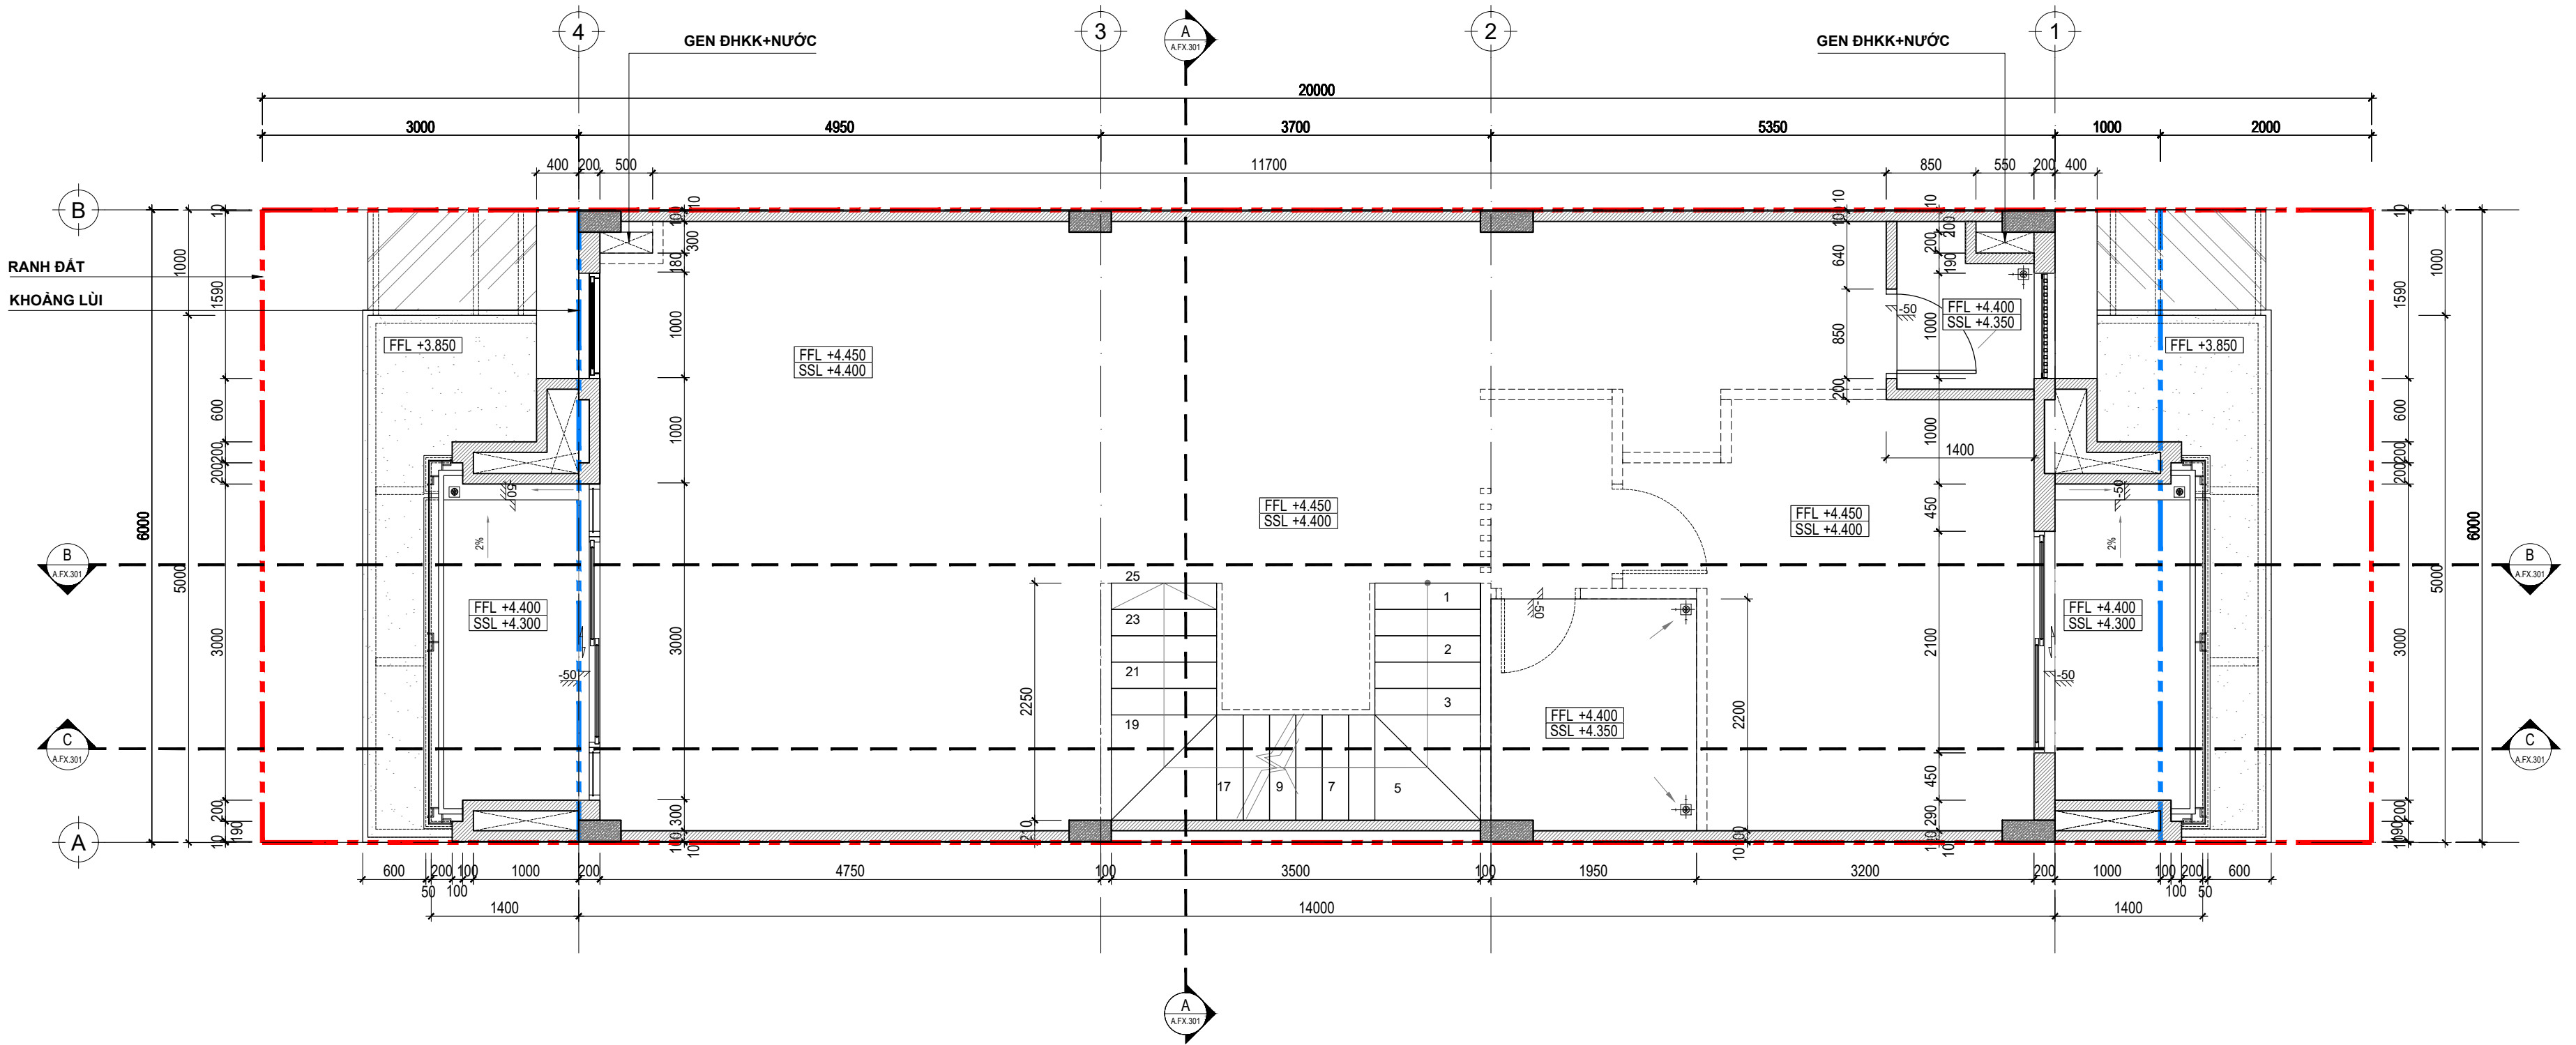


MẶT BẰNG KÍCH THƯỚC TẦNG 2_ TL:1/50

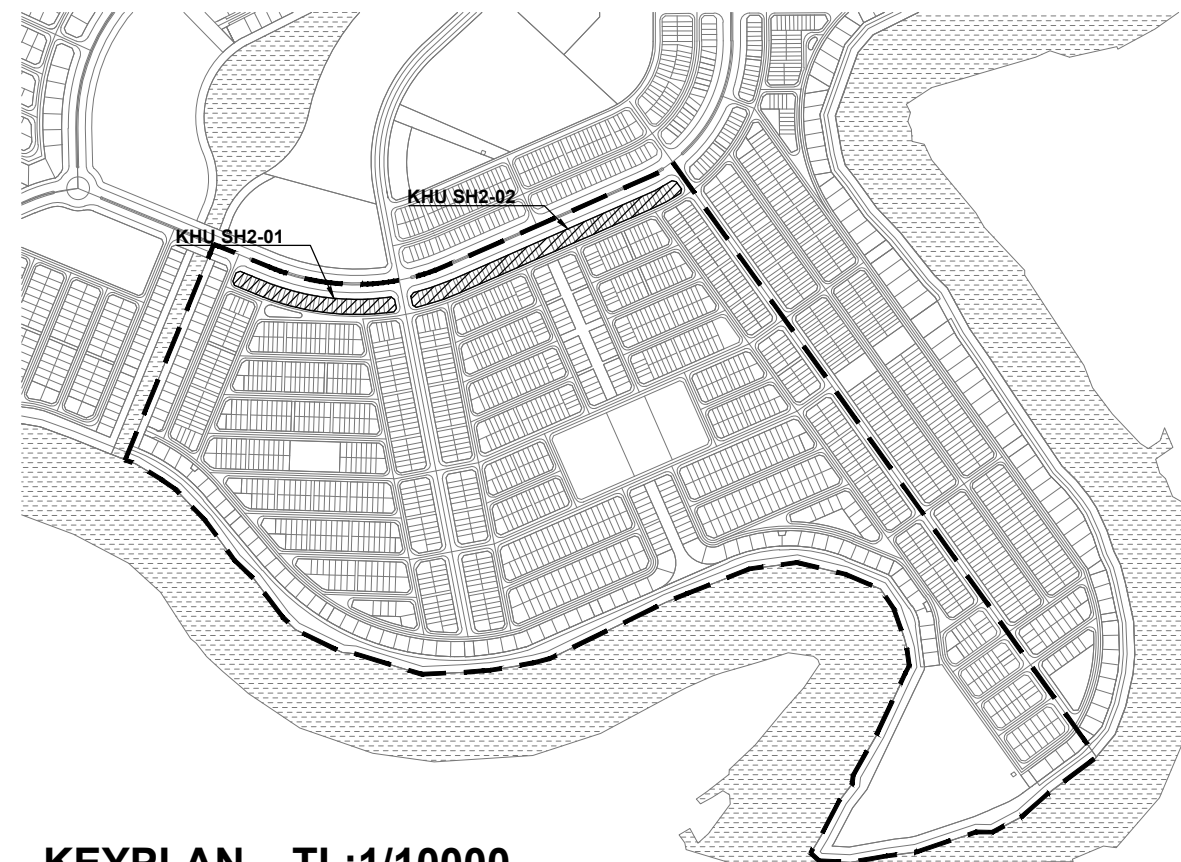


KEYPLAN_ TL:1/10000

GHI CHÚ: CAO ĐỘ ±0.00 TRONG BẢN VẼ TƯƠNG ỨNG CAO ĐỘ HÒN DẦU TẠI VÍA HÉ. CAO ĐỘ VÍA HÉ "VUI LÒNG XEM CÁC BẢN VẼ "THIẾT KẾ HẠ TẦNG"

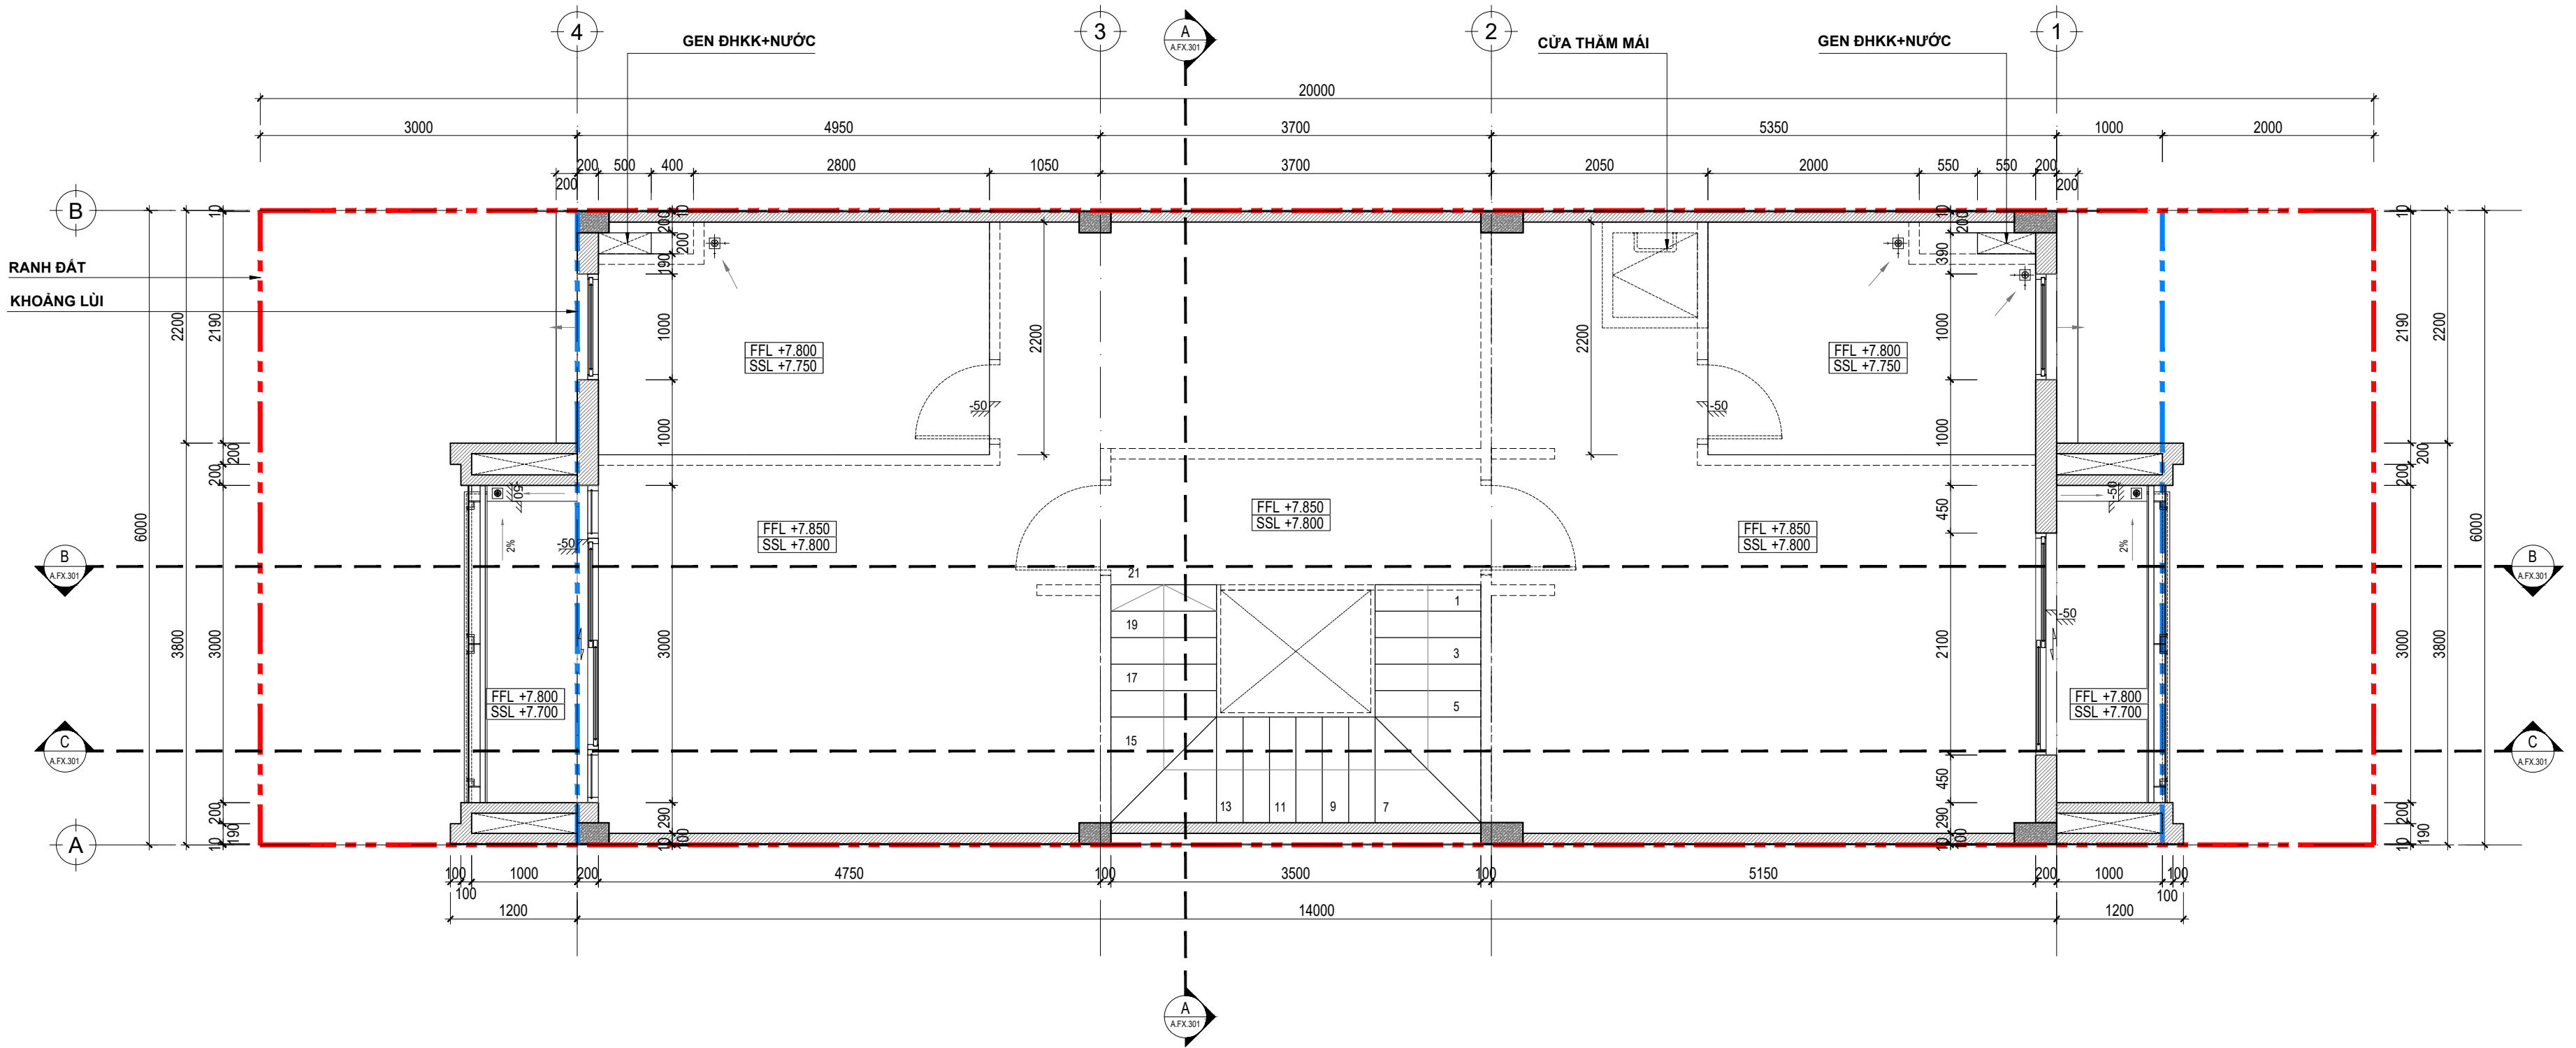


MẶT BẰNG KÍCH THƯỚC TẦNG 3 _ TL:1/50

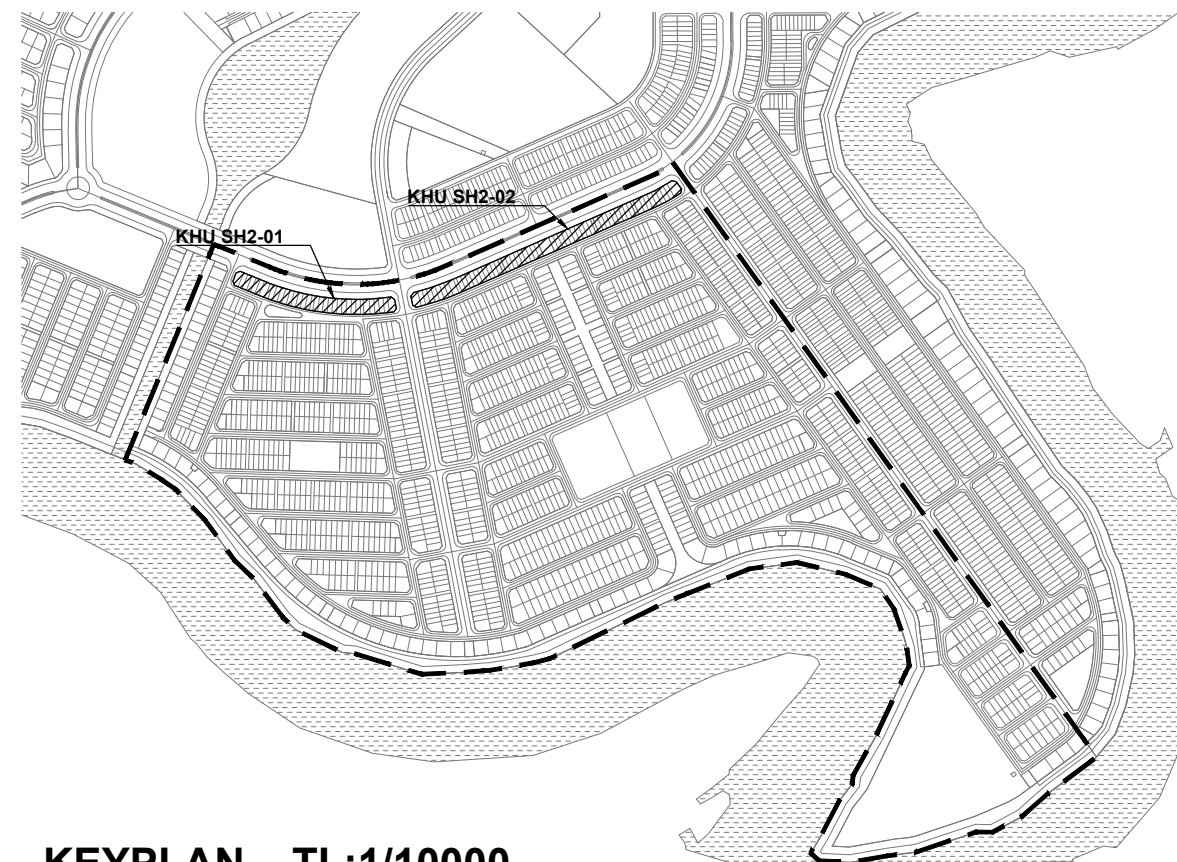


KEYPLAN _ TL:1/10000

GHI CHÚ: CAO ĐỘ ±0.00 TRONG BẢN VẼ TƯƠNG ỨNG CAO ĐỘ HÒN DẦU TẠI VÍA HÉ. CAO ĐỘ VÍA HÉ "VUI LÒNG XEM CÁC BẢN VẼ "THIẾT KẾ HẠ TẦNG"

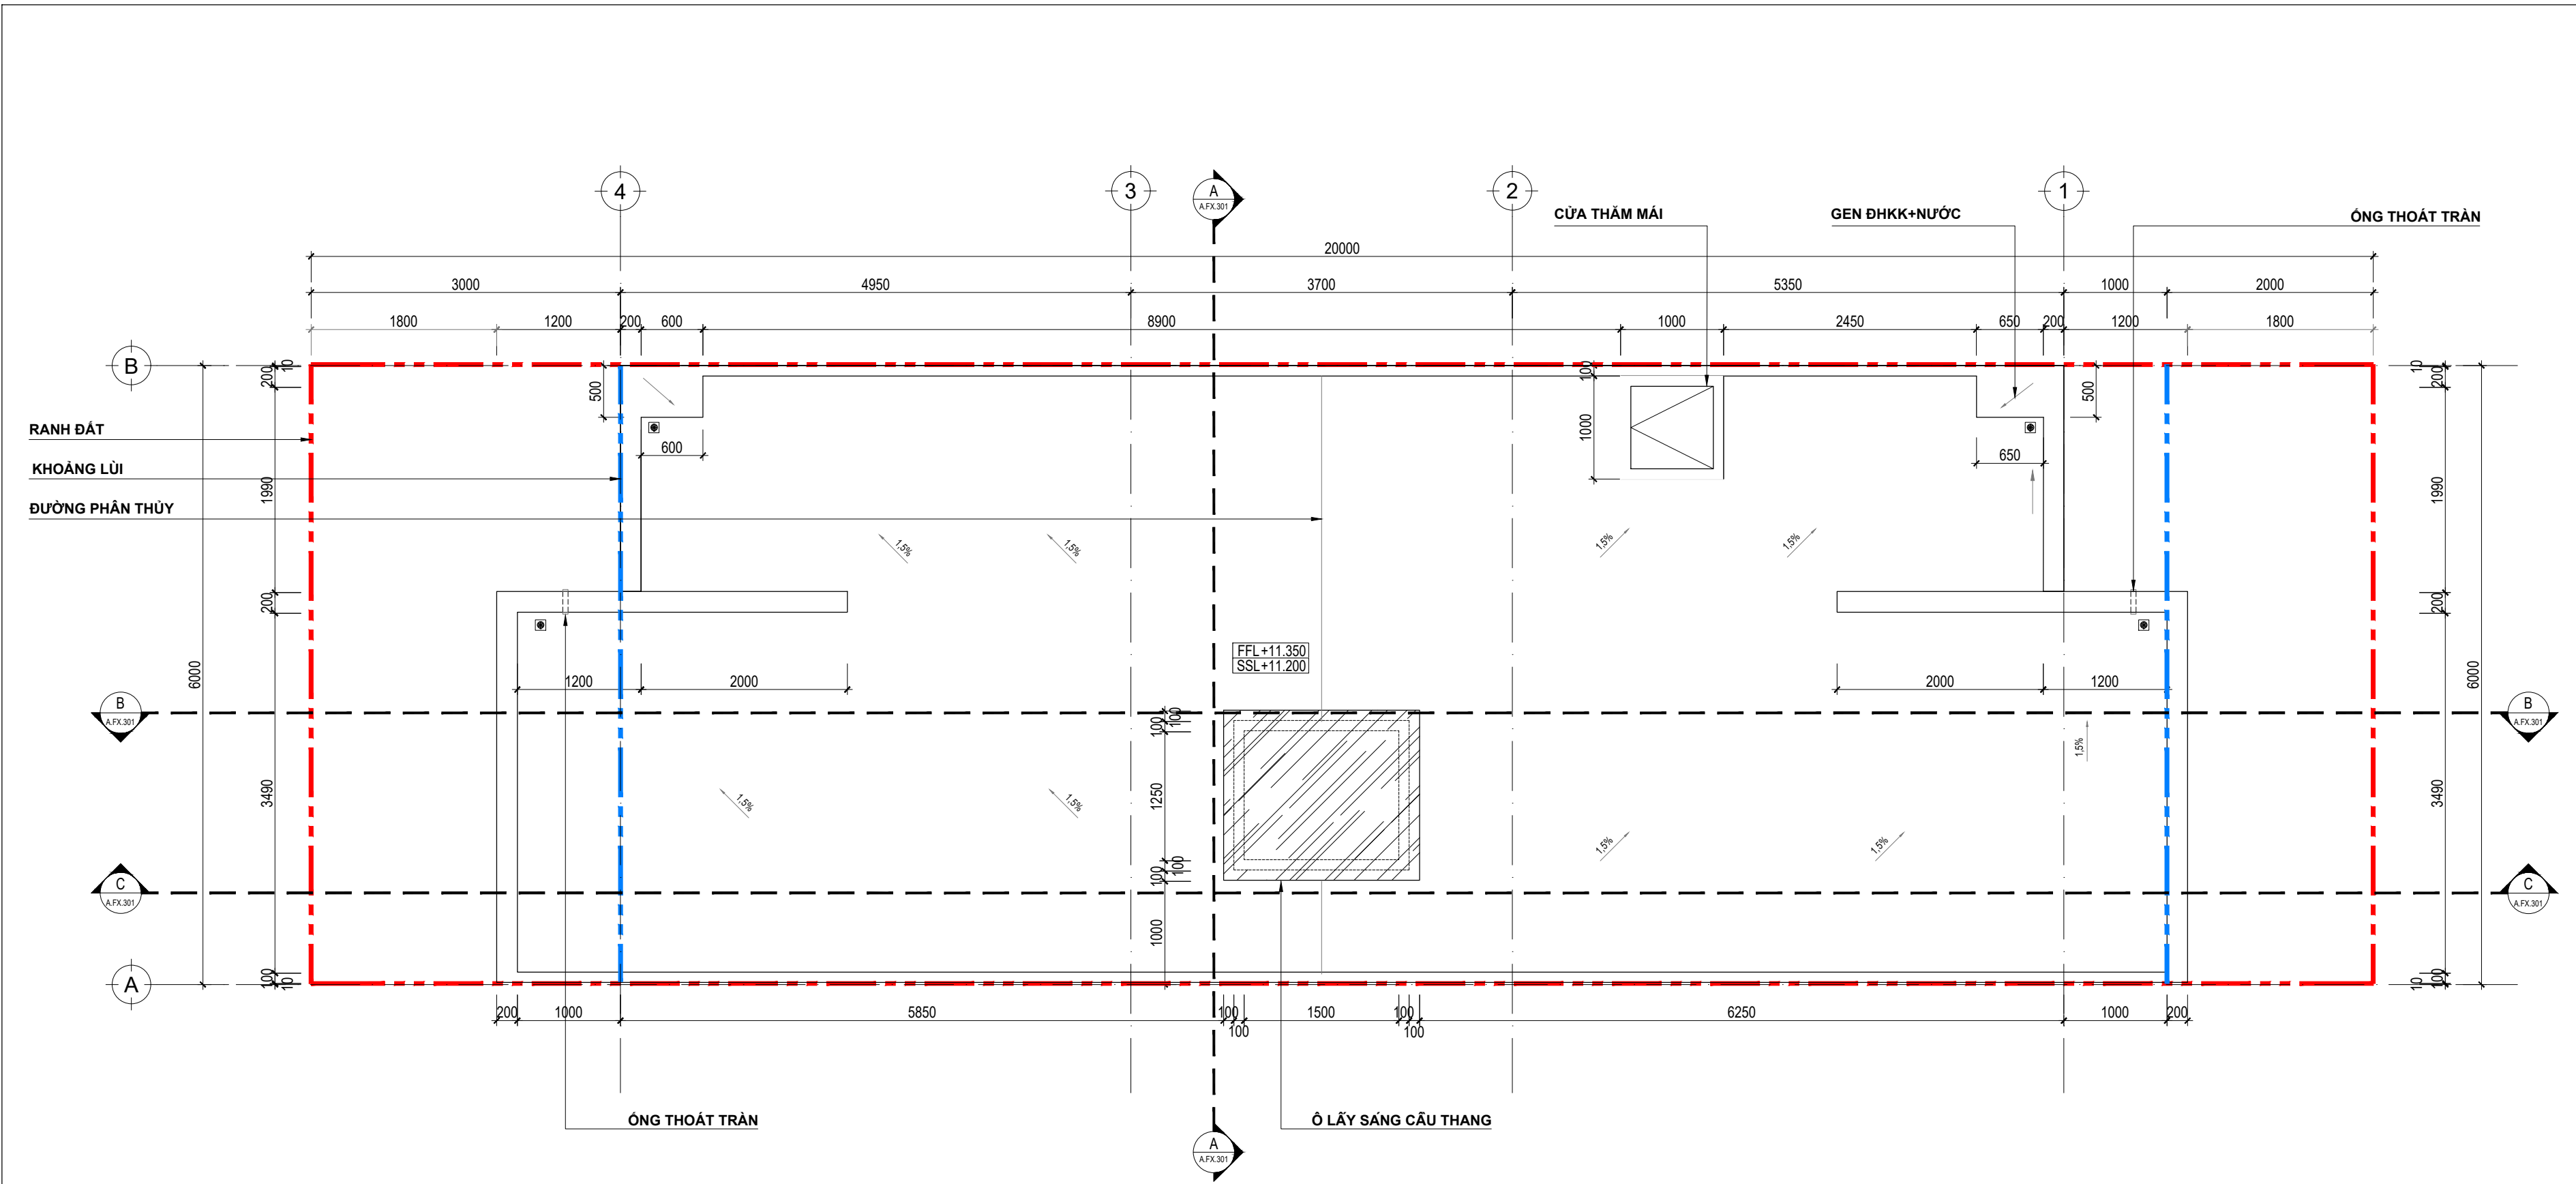


MẶT BẰNG KÍCH THƯỚC TẦNG MÁI _ TL:1/50

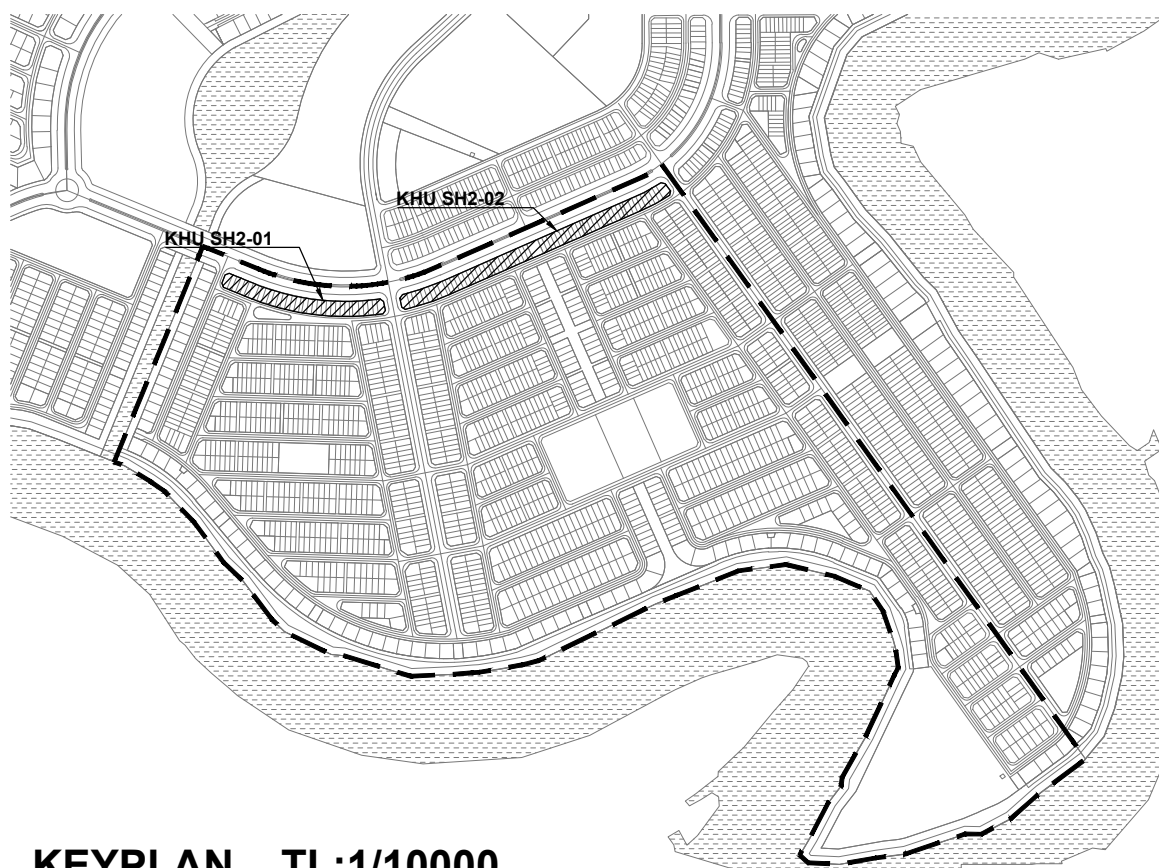


KEYPLAN _ TL:1/10000

GHI CHÚ: CAO ĐỘ ±0.00 TRONG BẢN VẼ TƯƠNG ỨNG CAO ĐỘ HẸN ĐẦU TẠI VÍA HÉ. CAO ĐỘ VÍA HÉ "VUI LÒNG XEM CÁC BẢN VẼ "THIẾT KẾ HẠ TẦNG"

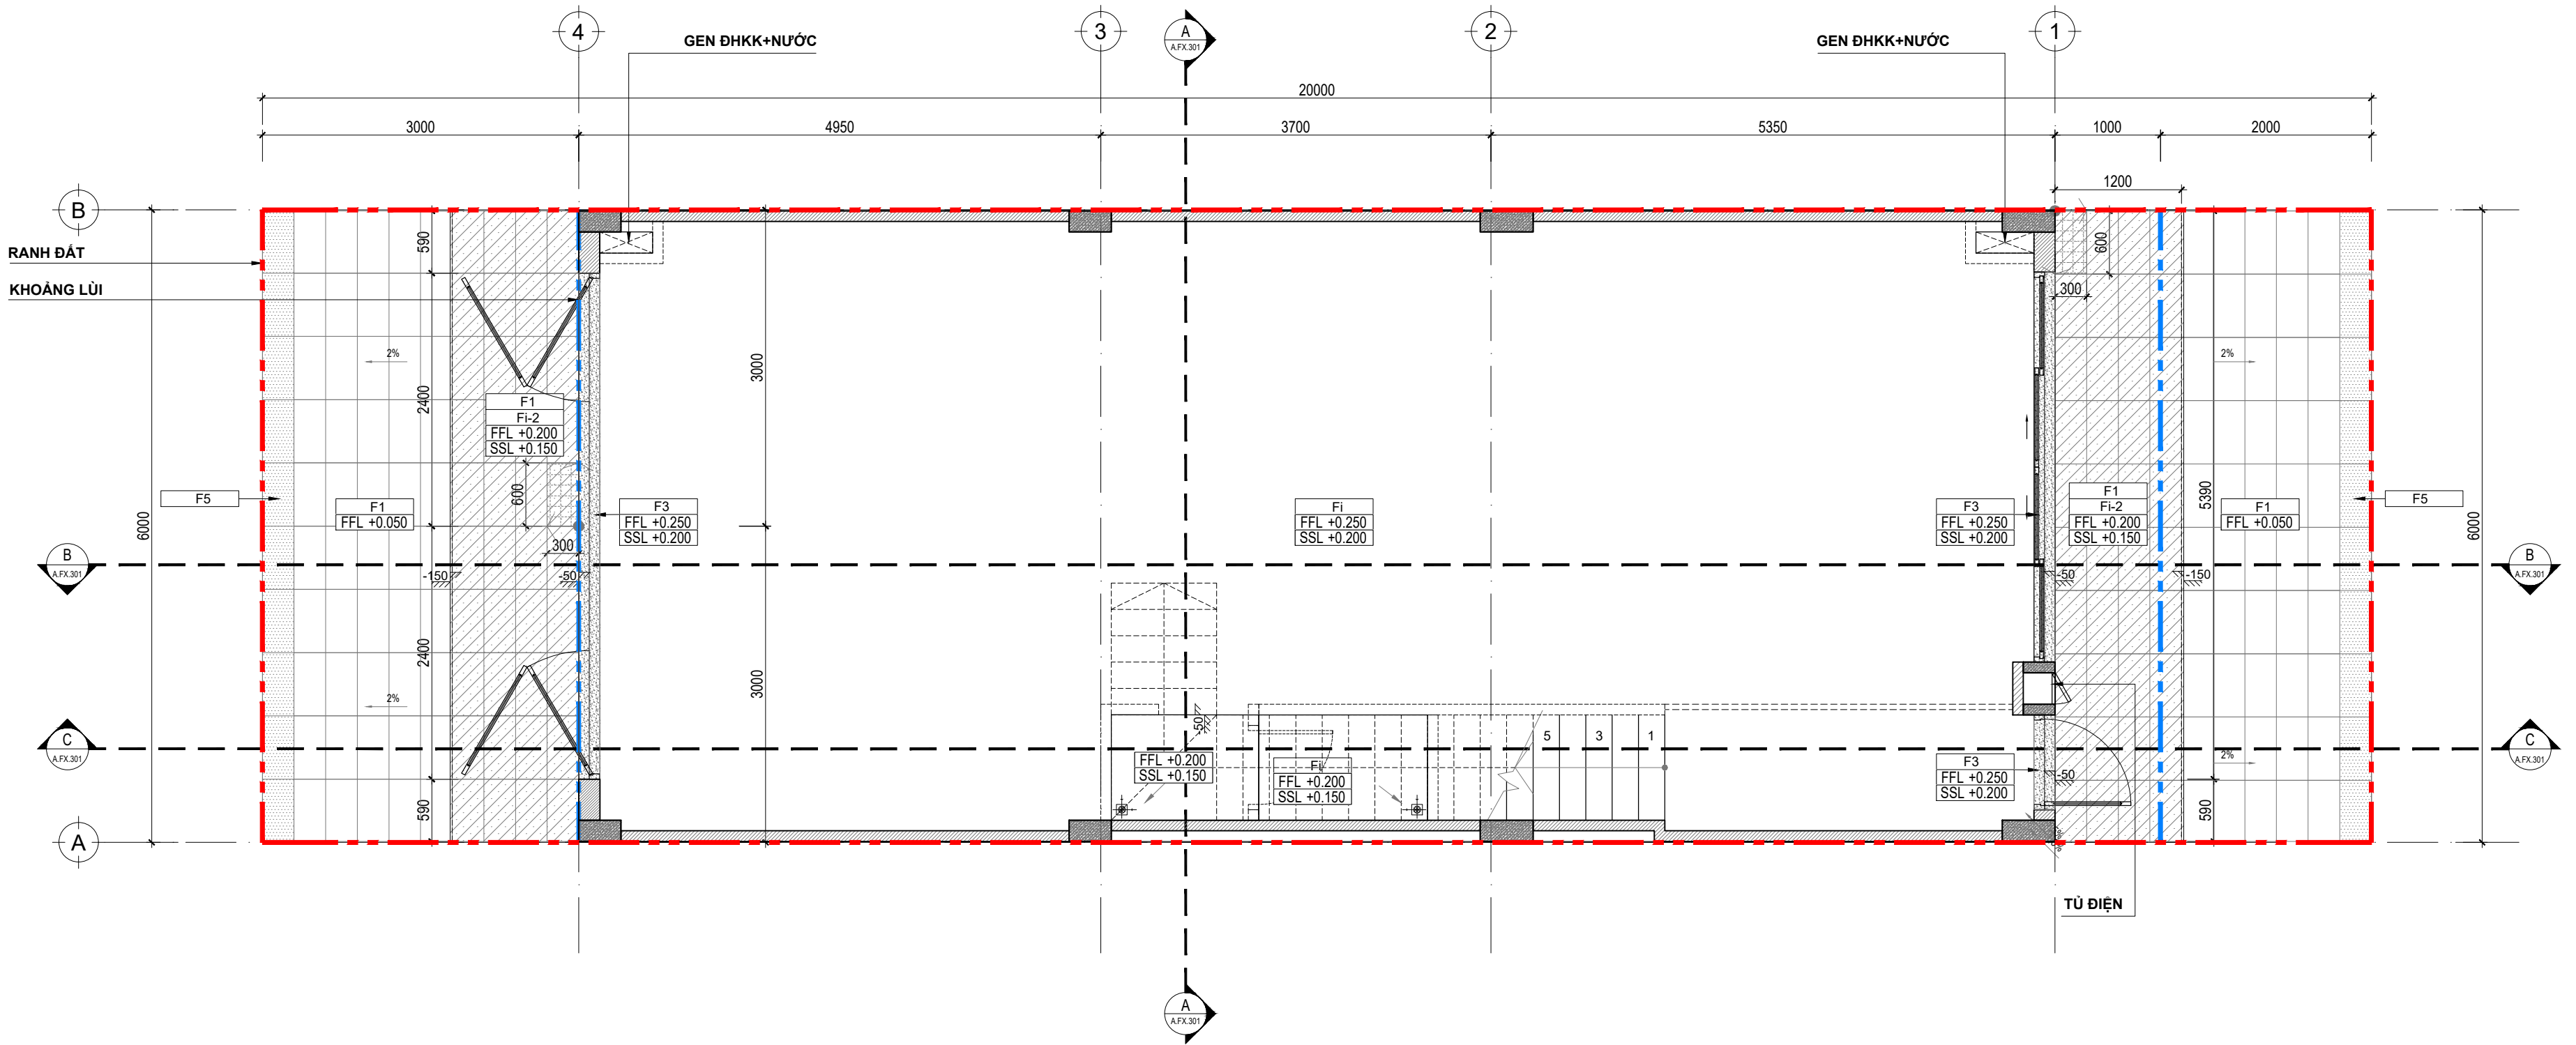


MẶT BẰNG HOÀN THIỆN SÀN TẦNG 1 _ TL:1/50

GHI CHÚ VẬT LIỆU SÀN NGOẠI THẤT					
TÊN	KÍ HIỆU	CHÚ THÍCH	TÊN	KÍ HIỆU	CHÚ THÍCH
Fi		SÀN BÊ TÔNG CỐT THÉP THÔ			
Fi-2		SÀN BÊ TÔNG CỐT THÉP, CHỐNG THÂM			
F1		GẠCH PORCELAIN 300x600mm, CHÔNG TRƯỢT, NGOẠI THẤT			
F2		ĐÁ ĐÁ GRANITE DÂY 20mm CHÔNG TRƯỢT 600x600mm			VIÊN GẠCH ĐUÔI
F3		ĐÁ ĐÁ GRANITE DÂY 20mm LÁT NGÁCH CỬA			
F4		GẠCH ĐỒNG NHẤT CHÔNG TRƯỢT, MÀU SÁNG 300x300			
F5		ĐÁ BAZAN 300X600			ĐIỂM MỐC CODE CAO ĐỘ
					CODE HOÀN THIỆN

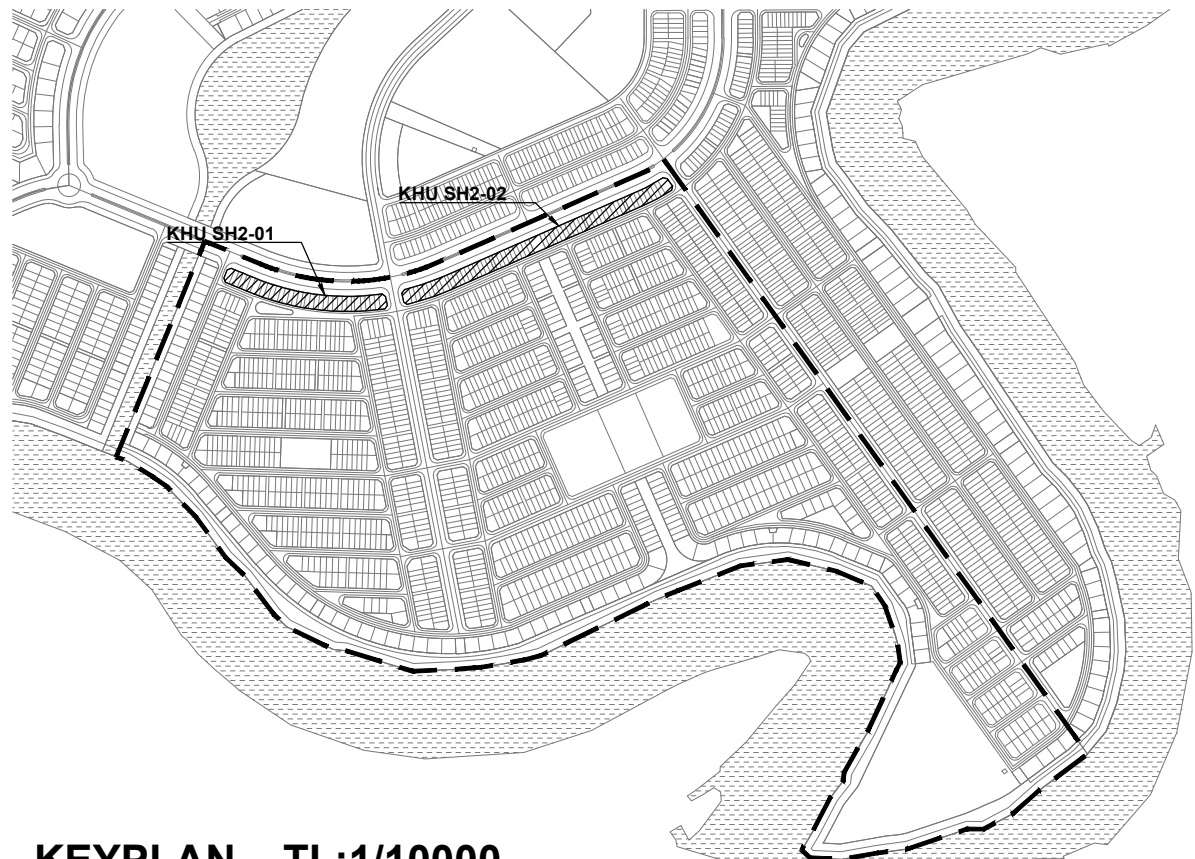


KEYPLAN _ TL:1/10000

GHI CHÚ: CAO ĐỘ ±0.00 TRONG BẢN VẼ TƯƠNG ỨNG CAO ĐỘ HỒN DẦU TẠI VĨA HÉ. CAO ĐỘ VĨA HÉ "VUI LÒNG XEM CÁC BẢN VẼ "THIẾT KẾ HẠ TẦNG"

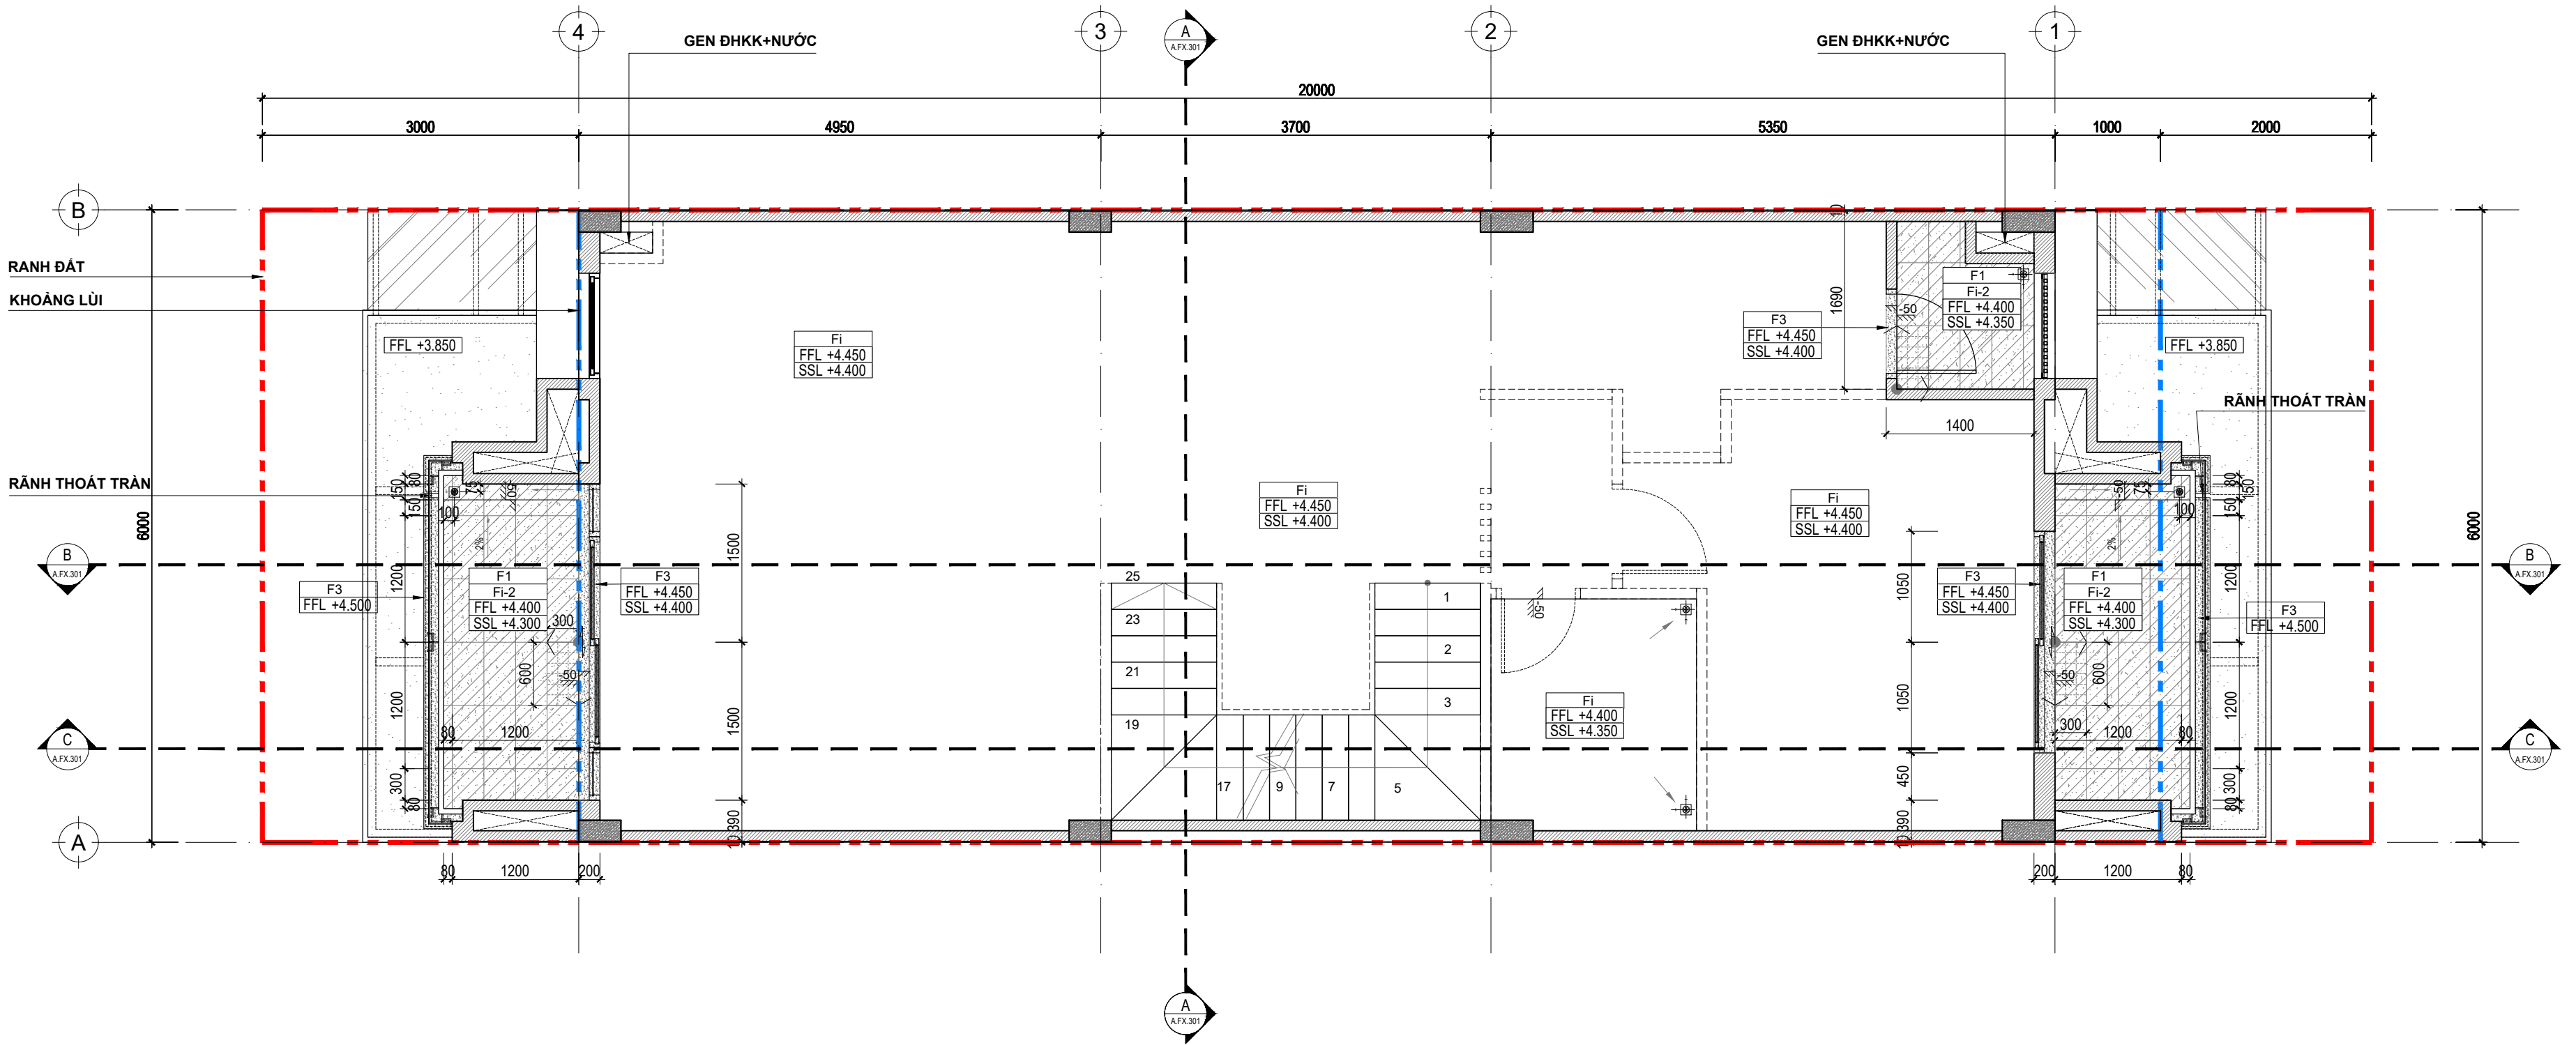


MẶT BẰNG HOÀN THIỆN SÀN TẦNG 2 _ TL:1/50

GHI CHÚ VẬT LIỆU SÀN NGOẠI THẤT					
TÊN	KÍ HIỆU	CHÚ THÍCH	TÊN	KÍ HIỆU	CHÚ THÍCH
F1		SÀN BÊ TÔNG CỐT THÉP THÔ			
Fi-2		SÀN BÊ TÔNG CỐT THÉP, CHỐNG THÂM			
F1		GẠCH PORCELAIN 300x600mm, CHỐNG TRƯỢT, NGOẠI THẤT			
F2		ĐÁ ĐÁ GRANITE DÀY 20mm CHỐNG TRƯỢT 600x600mm			
F3		ĐÁ ĐÁ GRANITE DÀY 20mm LÁT NGÁCH CỬA			
F4		GẠCH ĐỒNG NHẤT CHỐNG TRƯỢT, MÀU SÁNG 300x300			
F5		ĐÁ BAZAN 300X600			
					VIÊN GẠCH ĐUÔI
					CODE HOÀN THIỆN
					ĐIỂM MỐC CODE CAO ĐỘ

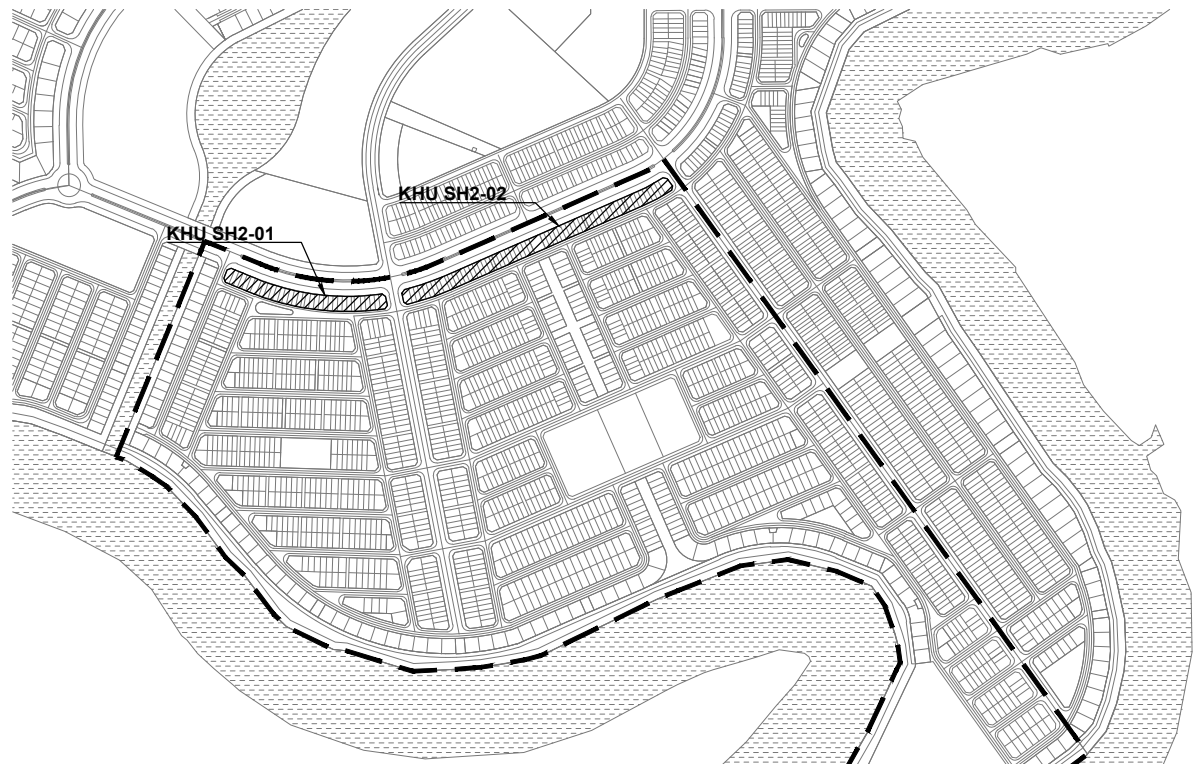


KEYPLAN _ TL:1/10000

GHI CHÚ: CAO ĐỘ ±0.00 TRONG BẢN VẼ TƯƠNG ỨNG CAO ĐỘ HỒN DẦU TẠI VĨA HÉ. CAO ĐỘ VĨA HÉ "VUI LÒNG XEM CÁC BẢN VẼ "THIẾT KẾ HẠ TẦNG"

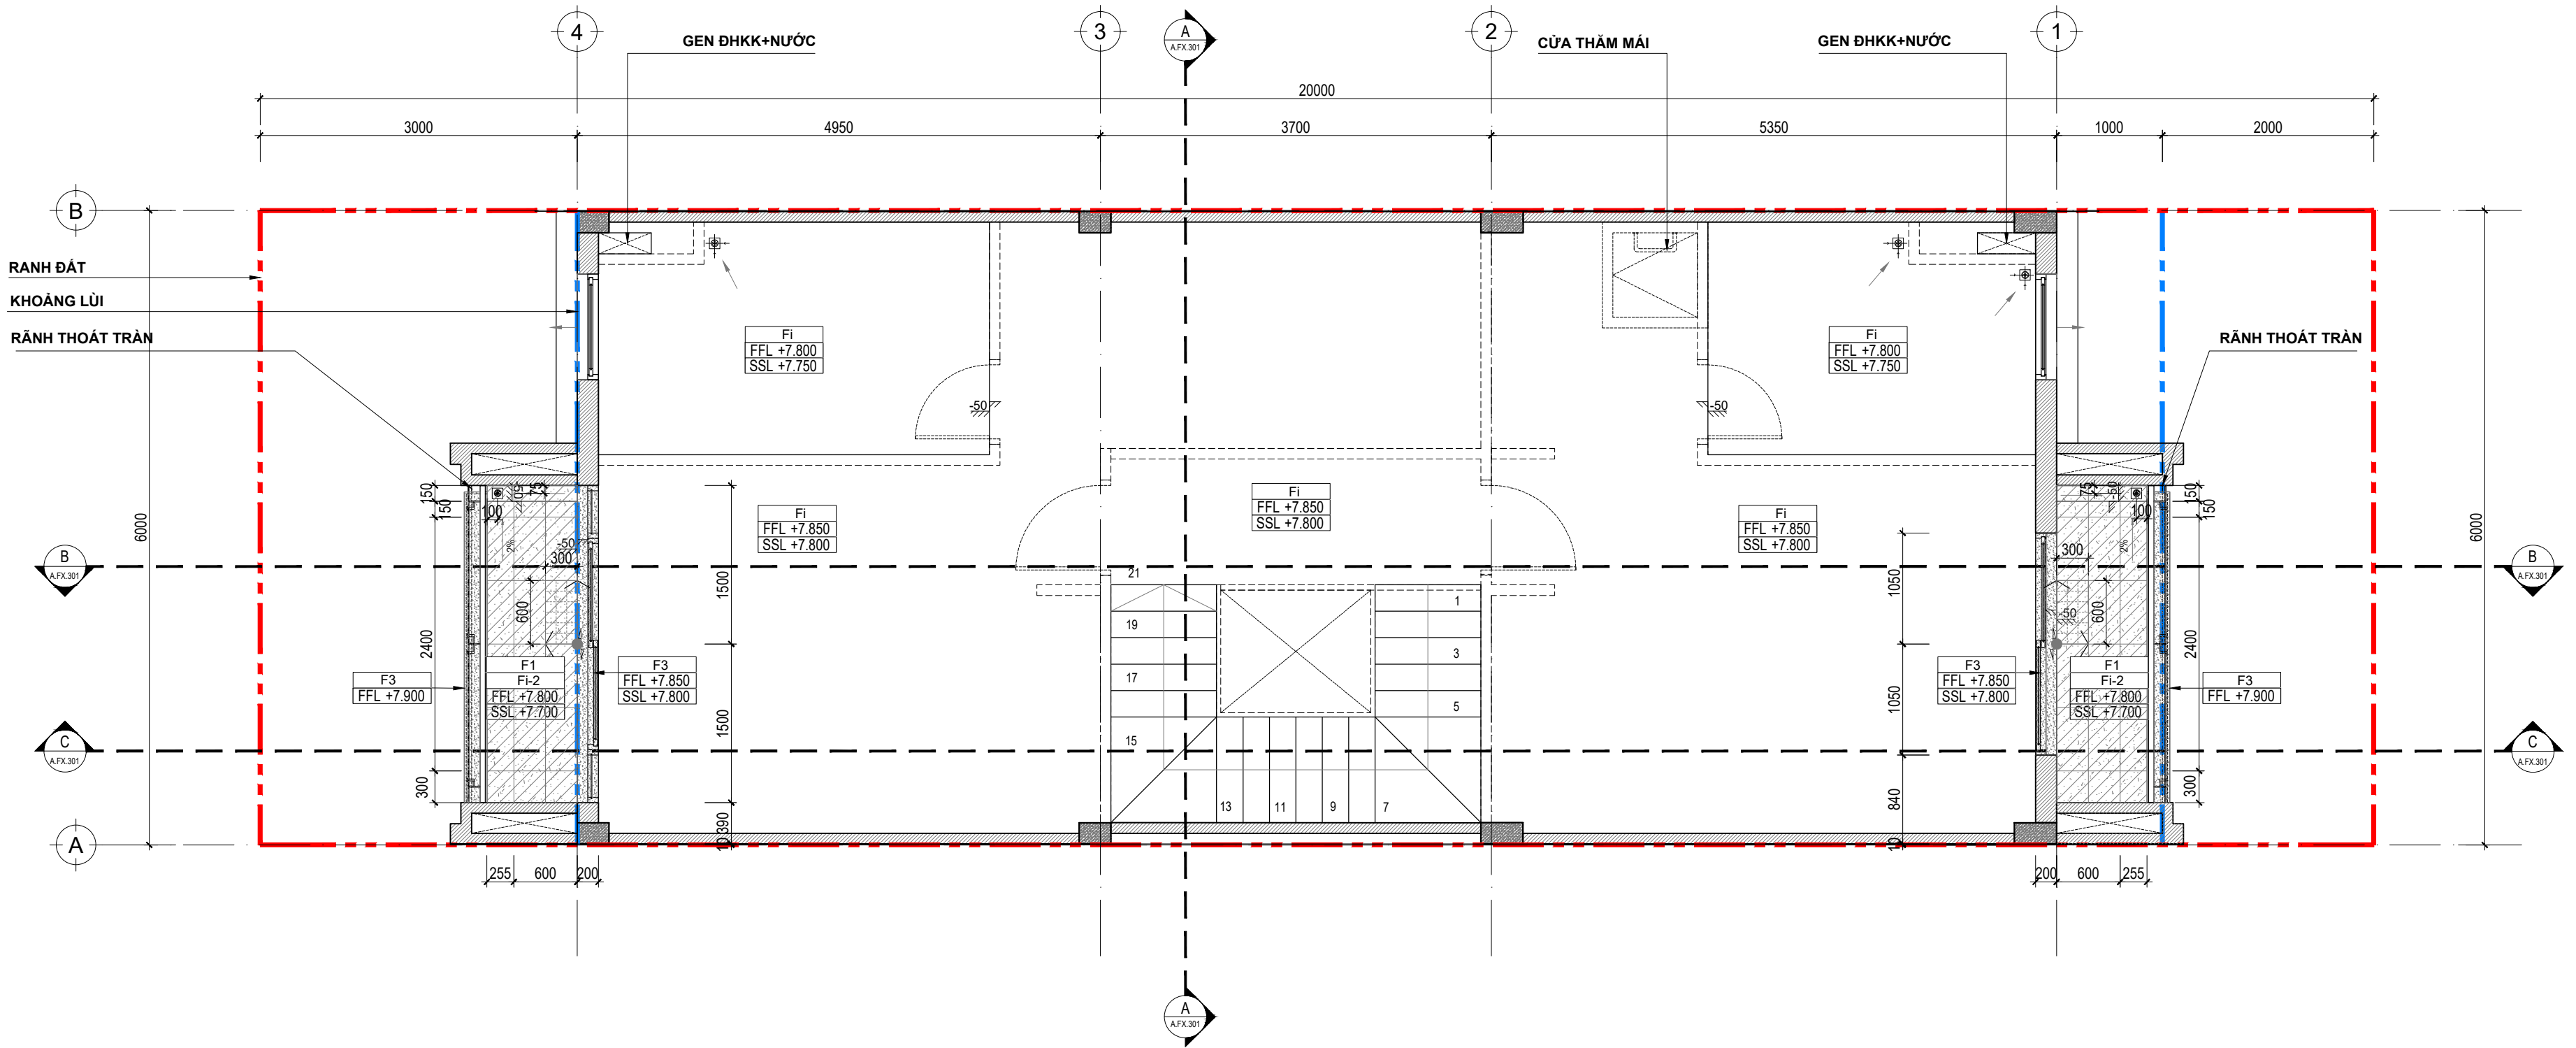


MẶT BẰNG HOÀN THIỆN SÀN TẦNG 3 _ TL:1/50

GHI CHÚ VẬT LIỆU SÀN NGOẠI THẤT					
TÊN	KÍ HIỆU	CHÚ THÍCH	TÊN	KÍ HIỆU	CHÚ THÍCH
Fi		SÀN BÊ TÔNG CỐT THÉP THÔ			
Fi-2		SÀN BÊ TÔNG CỐT THÉP, CHỐNG THÂM			
F1		GẠCH PORCELAIN 300x600mm, CHỐNG TRƯỢT, NGOẠI THẤT			
F2		ĐÁ ĐÁ GRANITE DÀY 20mm CHỐNG TRƯỢT 600x600mm			
F3		ĐÁ ĐÁ GRANITE DÀY 20mm LÁT NGÁCH CỬA			VIÊN GẠCH ĐUÔI
F4		GẠCH ĐỒNG NHẤT CHỐNG TRƯỢT, MÀU SÁNG 300x300			CODE HOÀN THIỆN
F5		ĐÁ BAZAN 300X600			ĐIỂM MỐC CODE CAO ĐỘ

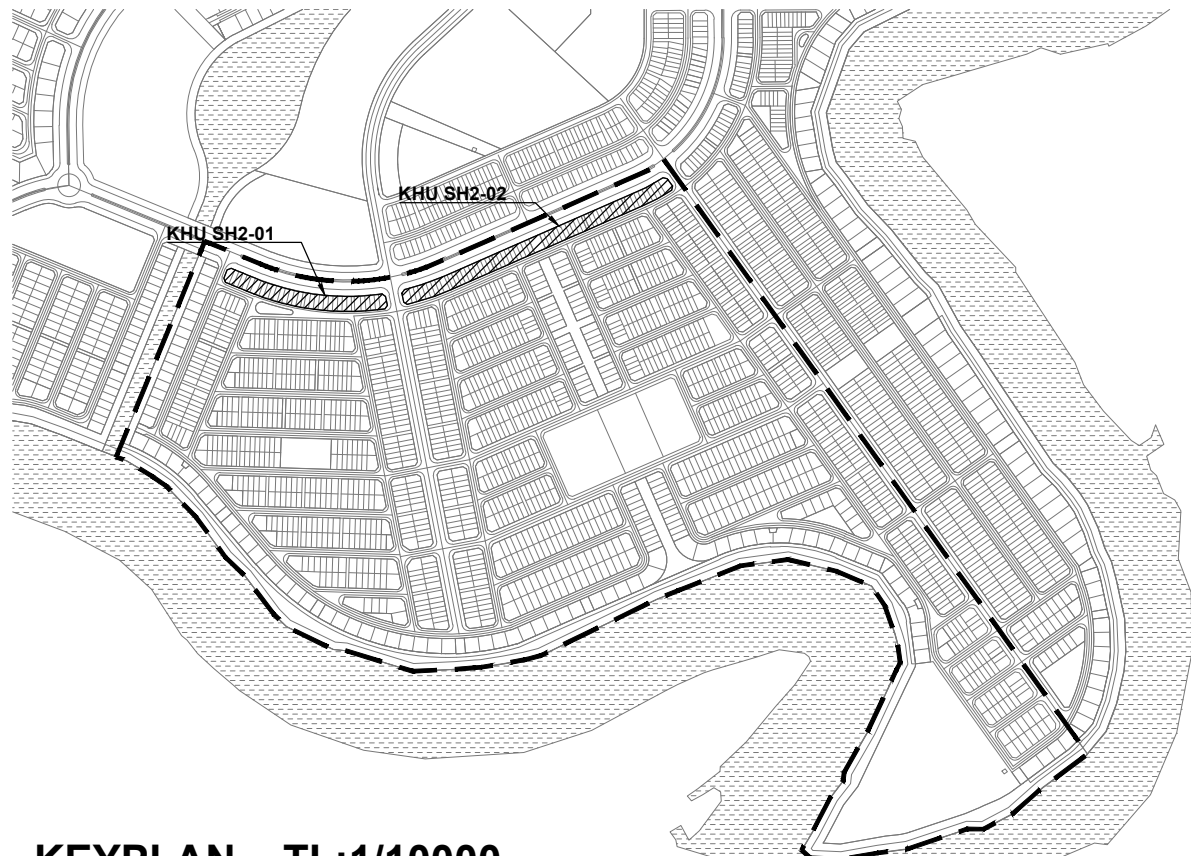


KEYPLAN _ TL:1/10000

GHI CHÚ: CAO ĐỘ ±0.00 TRONG BẢN VẼ TƯƠNG ỨNG CAO ĐỘ HỒN DẦU TẠI VĨA HÉ. CAO ĐỘ VĨA HÉ "VUI LÒNG XEM CÁC BẢN VẼ "THIẾT KẾ HẠ TẦNG"


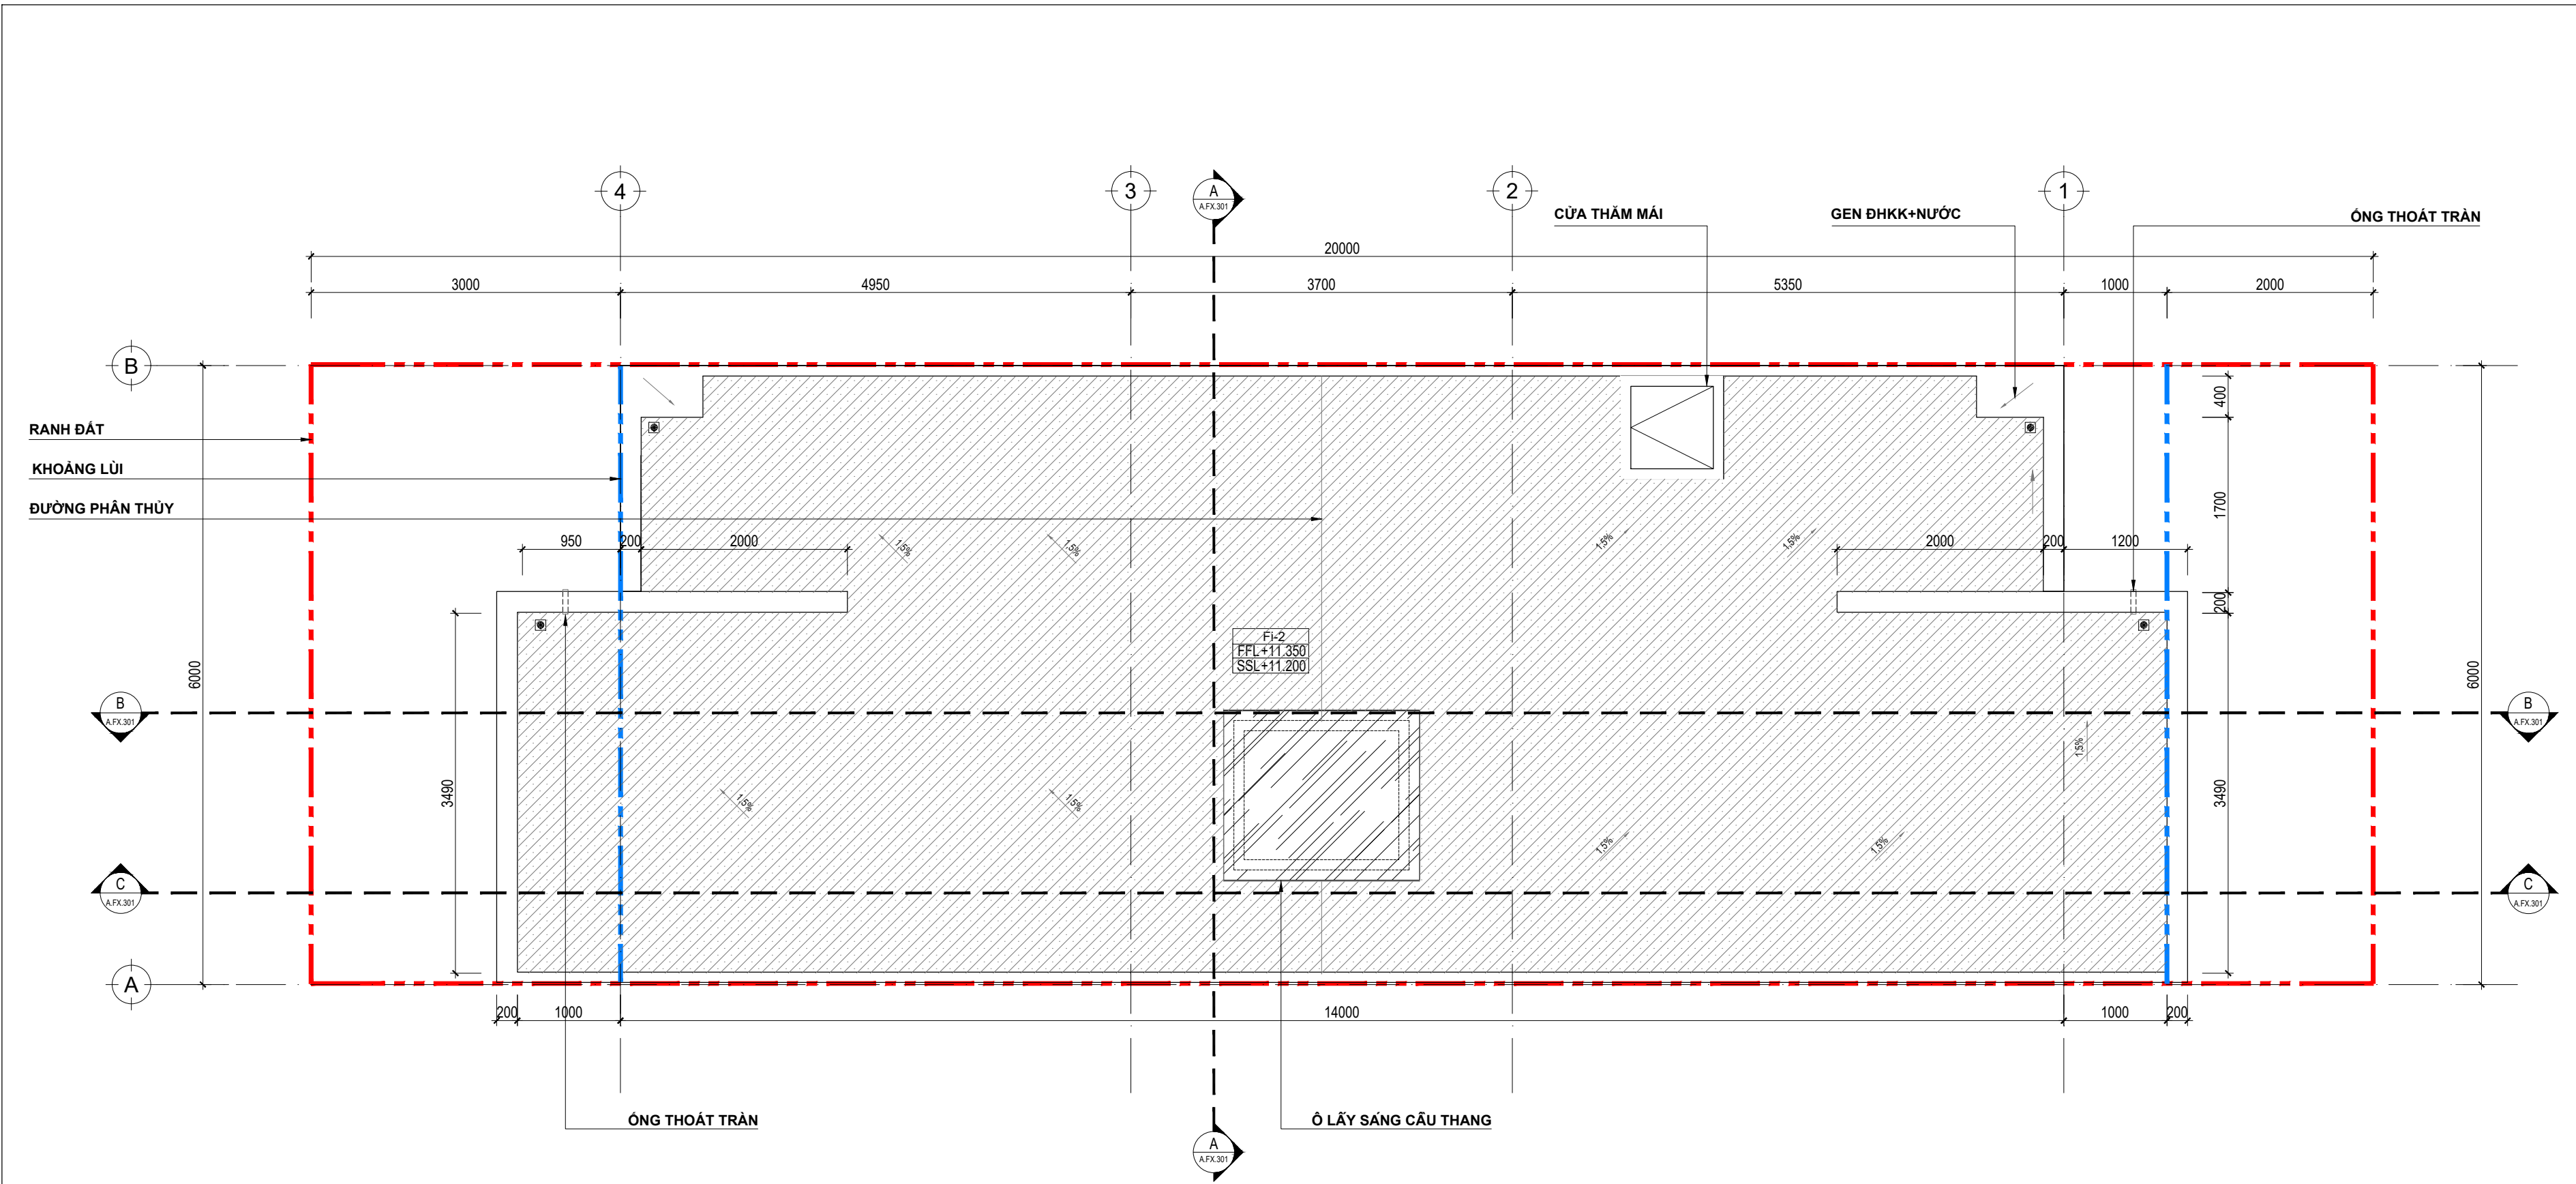


MẶT BẰNG HOÀN THIỆN SÀN TẦNG MÁI _ TL:1/50

GHI CHÚ VẬT LIỆU SÀN NGOẠI THẤT					
TÊN	KÍ HIỆU	CHÚ THÍCH	TÊN	KÍ HIỆU	CHÚ THÍCH
FI		SÀN BÊ TÔNG CỐT THÉP THÔ			
FI-2		SÀN BÊ TÔNG CỐT THÉP, CHÔNG THÂM			
F1		GẠCH PORCELAIN 300x600mm,CHÔNG TRƯỢT, NGOẠI THẤT			
F2		ĐÁ ĐÁ GRANITE DÂY 20mm CHÔNG TRƯỢT 600x600mm			VIÊN GẠCH ĐUÔI
F3		ĐÁ ĐÁ GRANITE DÂY 20mm LÁT NGẠCH CỬA			
F4		GẠCH ĐỒNG NHẤT CHÔNG TRƯỢT, MÀU SÁNG 300x300			CODE HOÀN THIỆN
F5		ĐÁ BAZAN 300X600			ĐIỂM MỐC CODE CAO ĐỘ

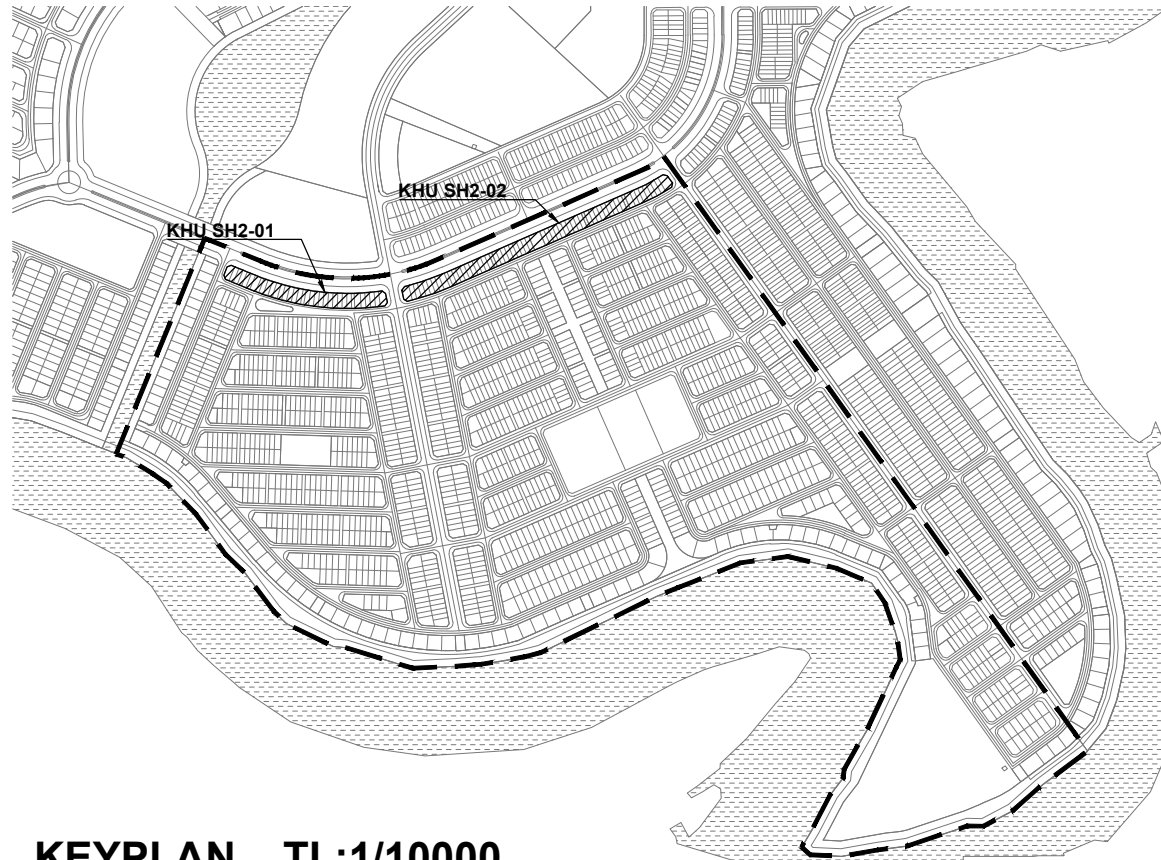


KEYPLAN _ TL:1/10000

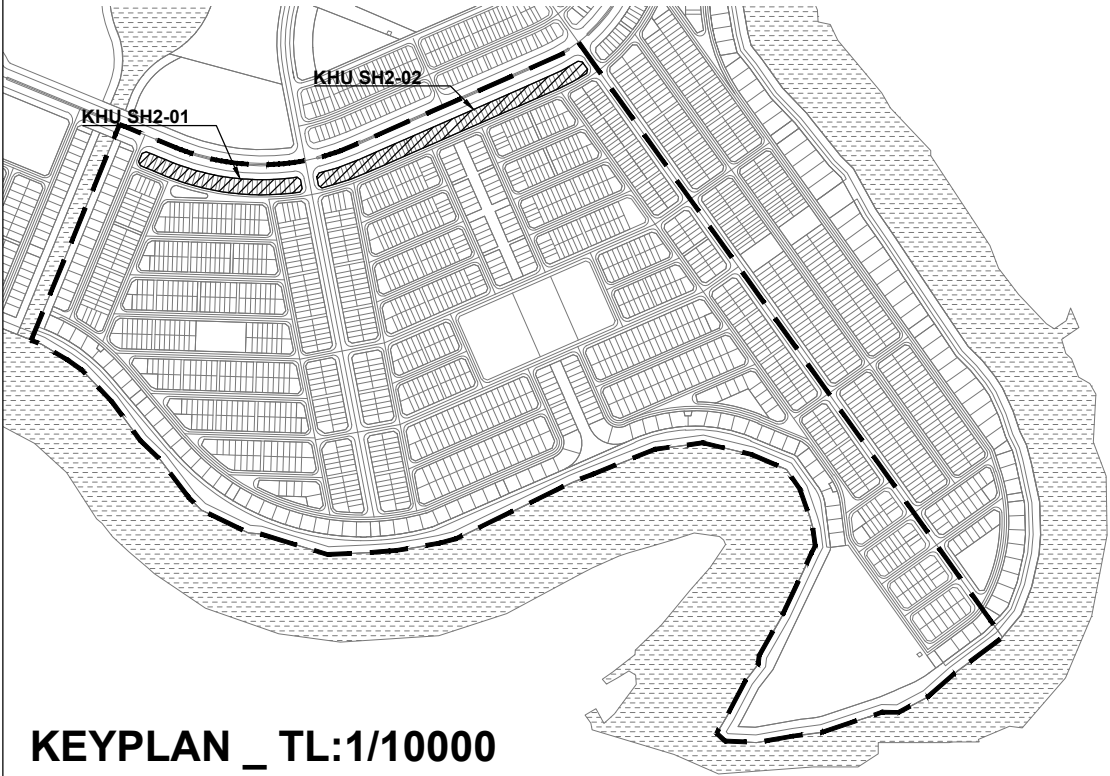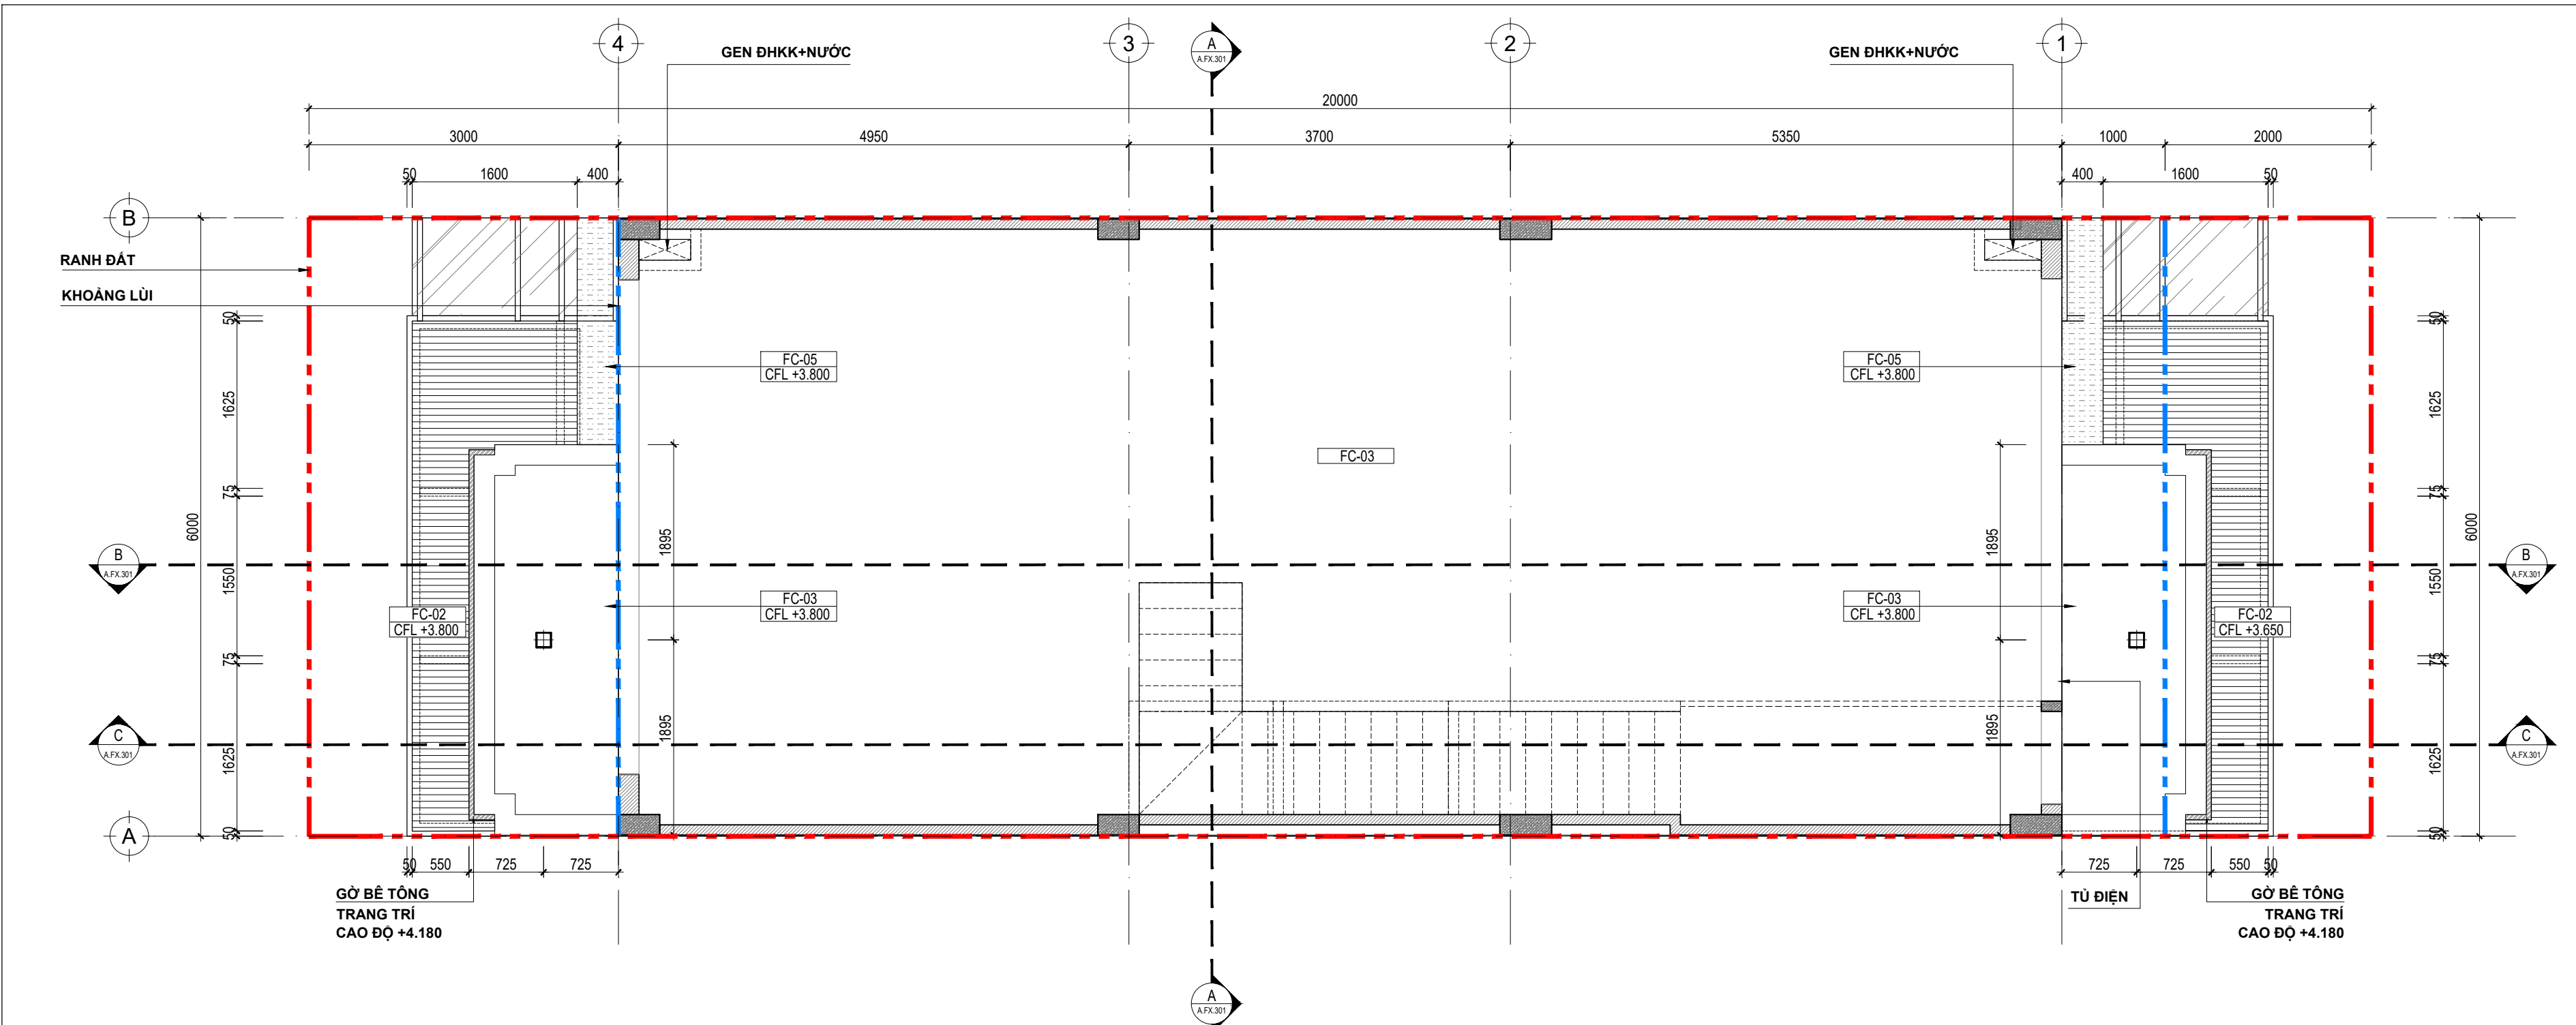

ĐÈN NGOẠI THẤT	
KÝ HIỆU	MÔ TẢ
	ĐÈN ÁP TRẦN NGOẠI THẤT, 12W, ÁNH SÁNG 3700K
	ĐÈN GẮN TƯỜNG NGOẠI THẤT ÁNH SÁNG 3700K, CÔNG SUẤT 15W
	ĐÈN TRỤ CÔNG ÁNH SÁNG 3000K, CÔNG SUẤT 9W


VẬT LIỆU HOÀN THIỆN TRẦN			VẬT LIỆU HOÀN THIỆN TRẦN		
KÝ HIỆU	MÔ TẢ		KÝ HIỆU	MÔ TẢ	
	FC-01	TRẦN CEMBOARD HOÀN THIỆN SƠN NƯỚC MÀU TRẮNG		FC-05	TRẦN BÊ TÔNG TRÁT VỮA HOÀN THIỆN SƠN NƯỚC (MÀU THEO MẪU)
	FC-02	TRẦN GỖ NHỰA MÀU NÂU ĐẬM		FC-06	TRẦN CEMBOARD HOÀN THIỆN SƠN NƯỚC MÀU HỒNG NÂU
	FC-03	TRẦN ĐẼ THÔ			
	FC-04	DẦM BÊ TÔNG TRÁT VỮA HOÀN THIỆN SƠN NƯỚC (MÀU THEO MẪU)			

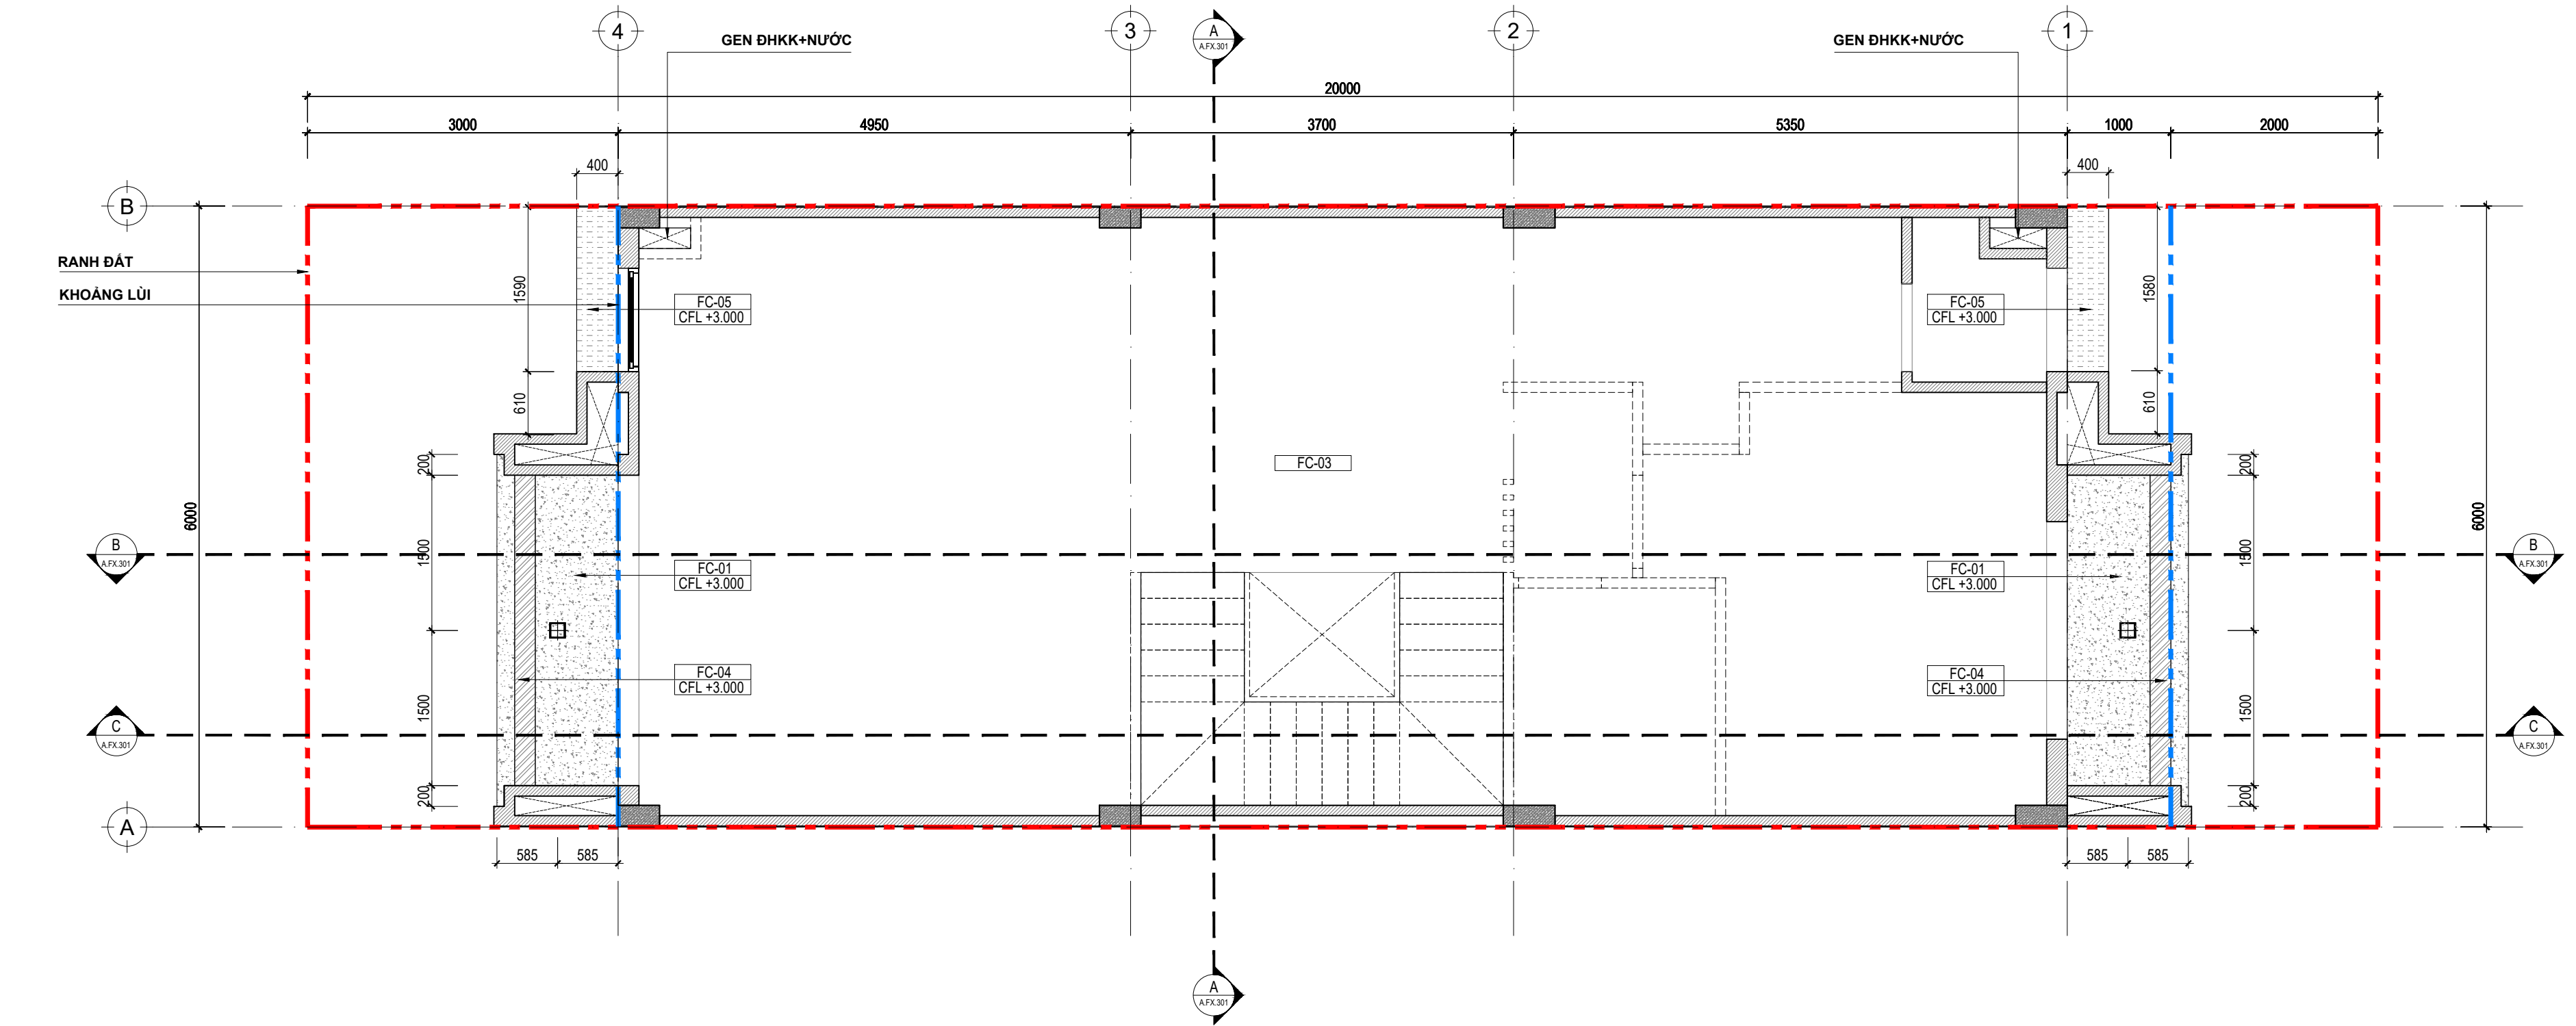

MẶT BẰNG TRẦN TẦNG 2_ TL:1/50


ĐÈN NGOẠI THẤT	
KÝ HIỆU	MÔ TẢ
	ĐÈN ẮP TRẦN NGOẠI THẤT, 12W, ÁNH SÁNG 3700K
	ĐÈN GẮN TƯỜNG NGOẠI THẤT ÁNH SÁNG 3700K, CÔNG SUẤT 15W
	ĐÈN TRỤ CÔNG ÁNH SÁNG 3000K, CÔNG SUẤT 9W

VẬT LIỆU HOÀN THIỆN TRẦN			VẬT LIỆU HOÀN THIỆN TRẦN		
KÝ HIỆU	MÔ TẢ		KÝ HIỆU	MÔ TẢ	
	FC-01	TRẦN CEMBOARD HOÀN THIỆN SƠN NƯỚC MÀU TRẮNG		FC-05	TRẦN BÊ TÔNG TRÁT VỮA HOÀN THIỆN SƠN NƯỚC (MÀU THEO MẪU)
	FC-02	TRẦN GỖ NHỰA MÀU NÂU ĐẬM		FC-06	TRẦN CEMBOARD HOÀN THIỆN SƠN NƯỚC MÀU HỒNG NÂU
	FC-03	TRẦN ĐỂ THÔ			
	FC-04	DẦM BÊ TÔNG TRÁT VỮA HOÀN THIỆN SƠN NƯỚC (MÀU THEO MẪU)			

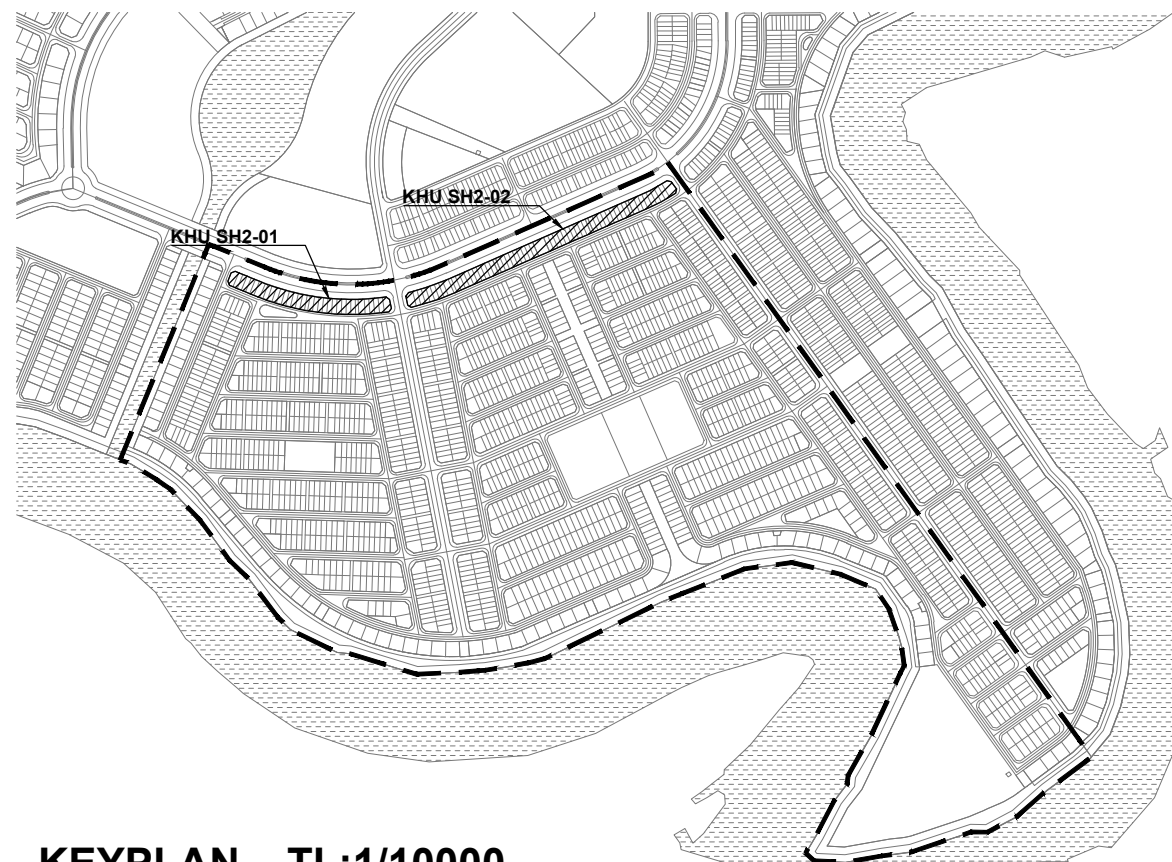

KEYPLAN_ TL:1/10000


GHI CHÚ: CAO ĐỘ ±0.00 TRONG BẢN VẼ TƯƠNG ỨNG CAO ĐỘ HỒN DẦU TẠI VÍA HÉ. CAO ĐỘ VÍA HÉ "VUI LÒNG XEM CÁC BẢN VẼ "THIẾT KẾ HẠ TẦNG"

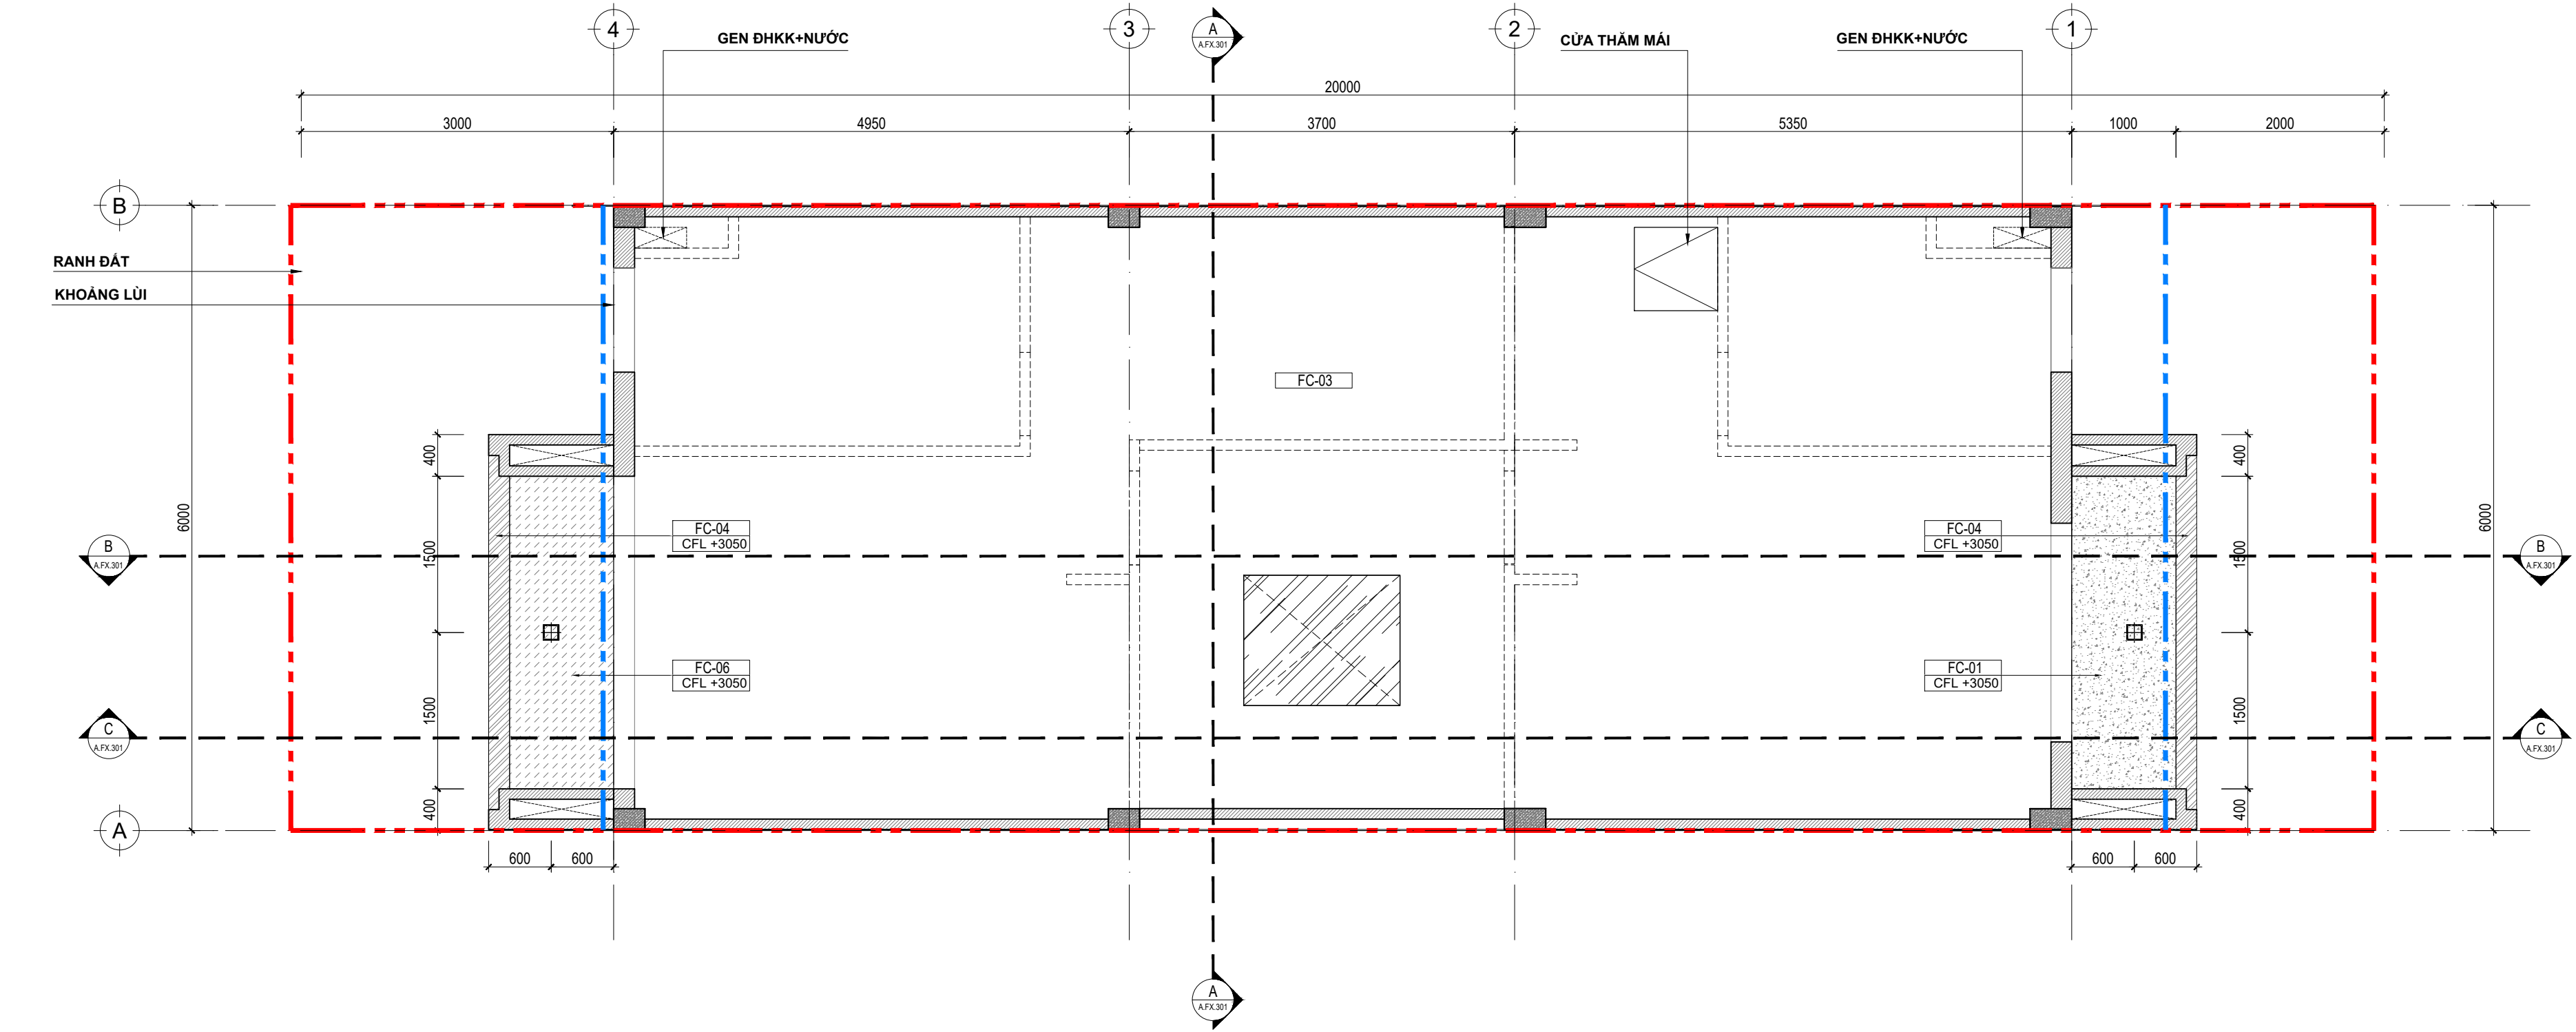


MẶT BẰNG TRẦN TẦNG 3 _ TL:1/50

ĐÈN NGOẠI THẤT	
KÝ HIỆU	MÔ TẢ
	ĐÈN ÁP TRẦN NGOẠI THẤT, 12W, ÁNH SÁNG 3700K
	ĐÈN GÁN TƯỜNG NGOẠI THẤT ÁNH SÁNG 3700K, CÔNG SUẤT 15W
	ĐÈN TRỤ CÔNG ÁNH SÁNG 3000K, CÔNG SUẤT 9W

VẬT LIỆU HOÀN THIỆN TRẦN			VẬT LIỆU HOÀN THIỆN TRẦN		
KÝ HIỆU	MÔ TẢ		KÝ HIỆU	MÔ TẢ	
	FC-01	TRẦN CEMBOARD HOÀN THIỆN SƠN NƯỚC MÀU TRẮNG		FC-05	TRẦN BÊ TÔNG TRÁT VỮA HOÀN THIỆN SƠN NƯỚC (MÀU THEO MẪU)
	FC-02	TRẦN GỖ NHỰA MÀU NÂU ĐẬM		FC-06	TRẦN CEMBOARD HOÀN THIỆN SƠN NƯỚC MÀU HỒNG NÂU
	FC-03	TRẦN ĐỂ THÔ			
	FC-04	DẦM BÊ TÔNG TRÁT VỮA HOÀN THIỆN SƠN NƯỚC (MÀU THEO MẪU)			

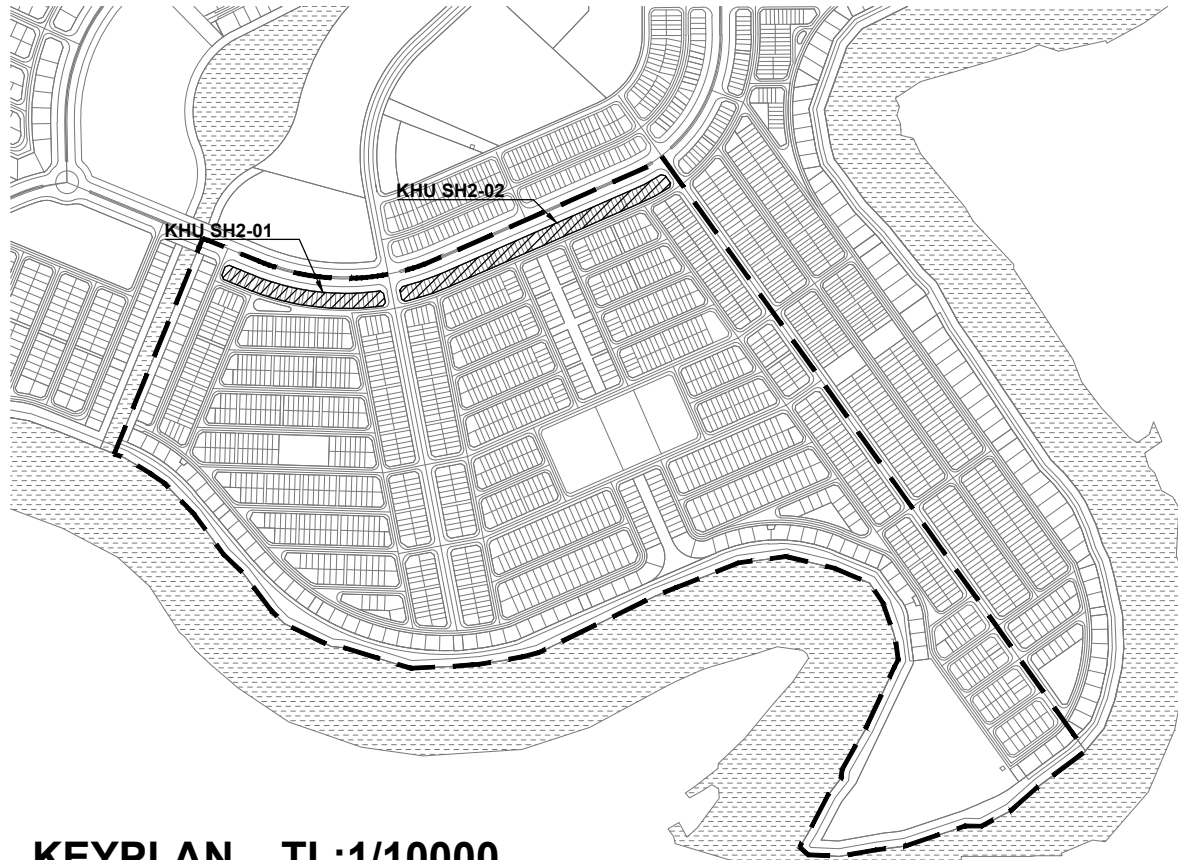


KEYPLAN _ TL:1/10000
GHI CHÚ: CAO ĐỘ ±0.00 TRONG BẢN VẼ TƯƠNG ỨNG CAO ĐỘ HỒN DẦU TẠI VĨA HÉ. CAO ĐỘ VĨA HÉ "VUI LÒNG XEM CÁC BẢN VẼ "THIẾT KẾ HẠ TẦNG"

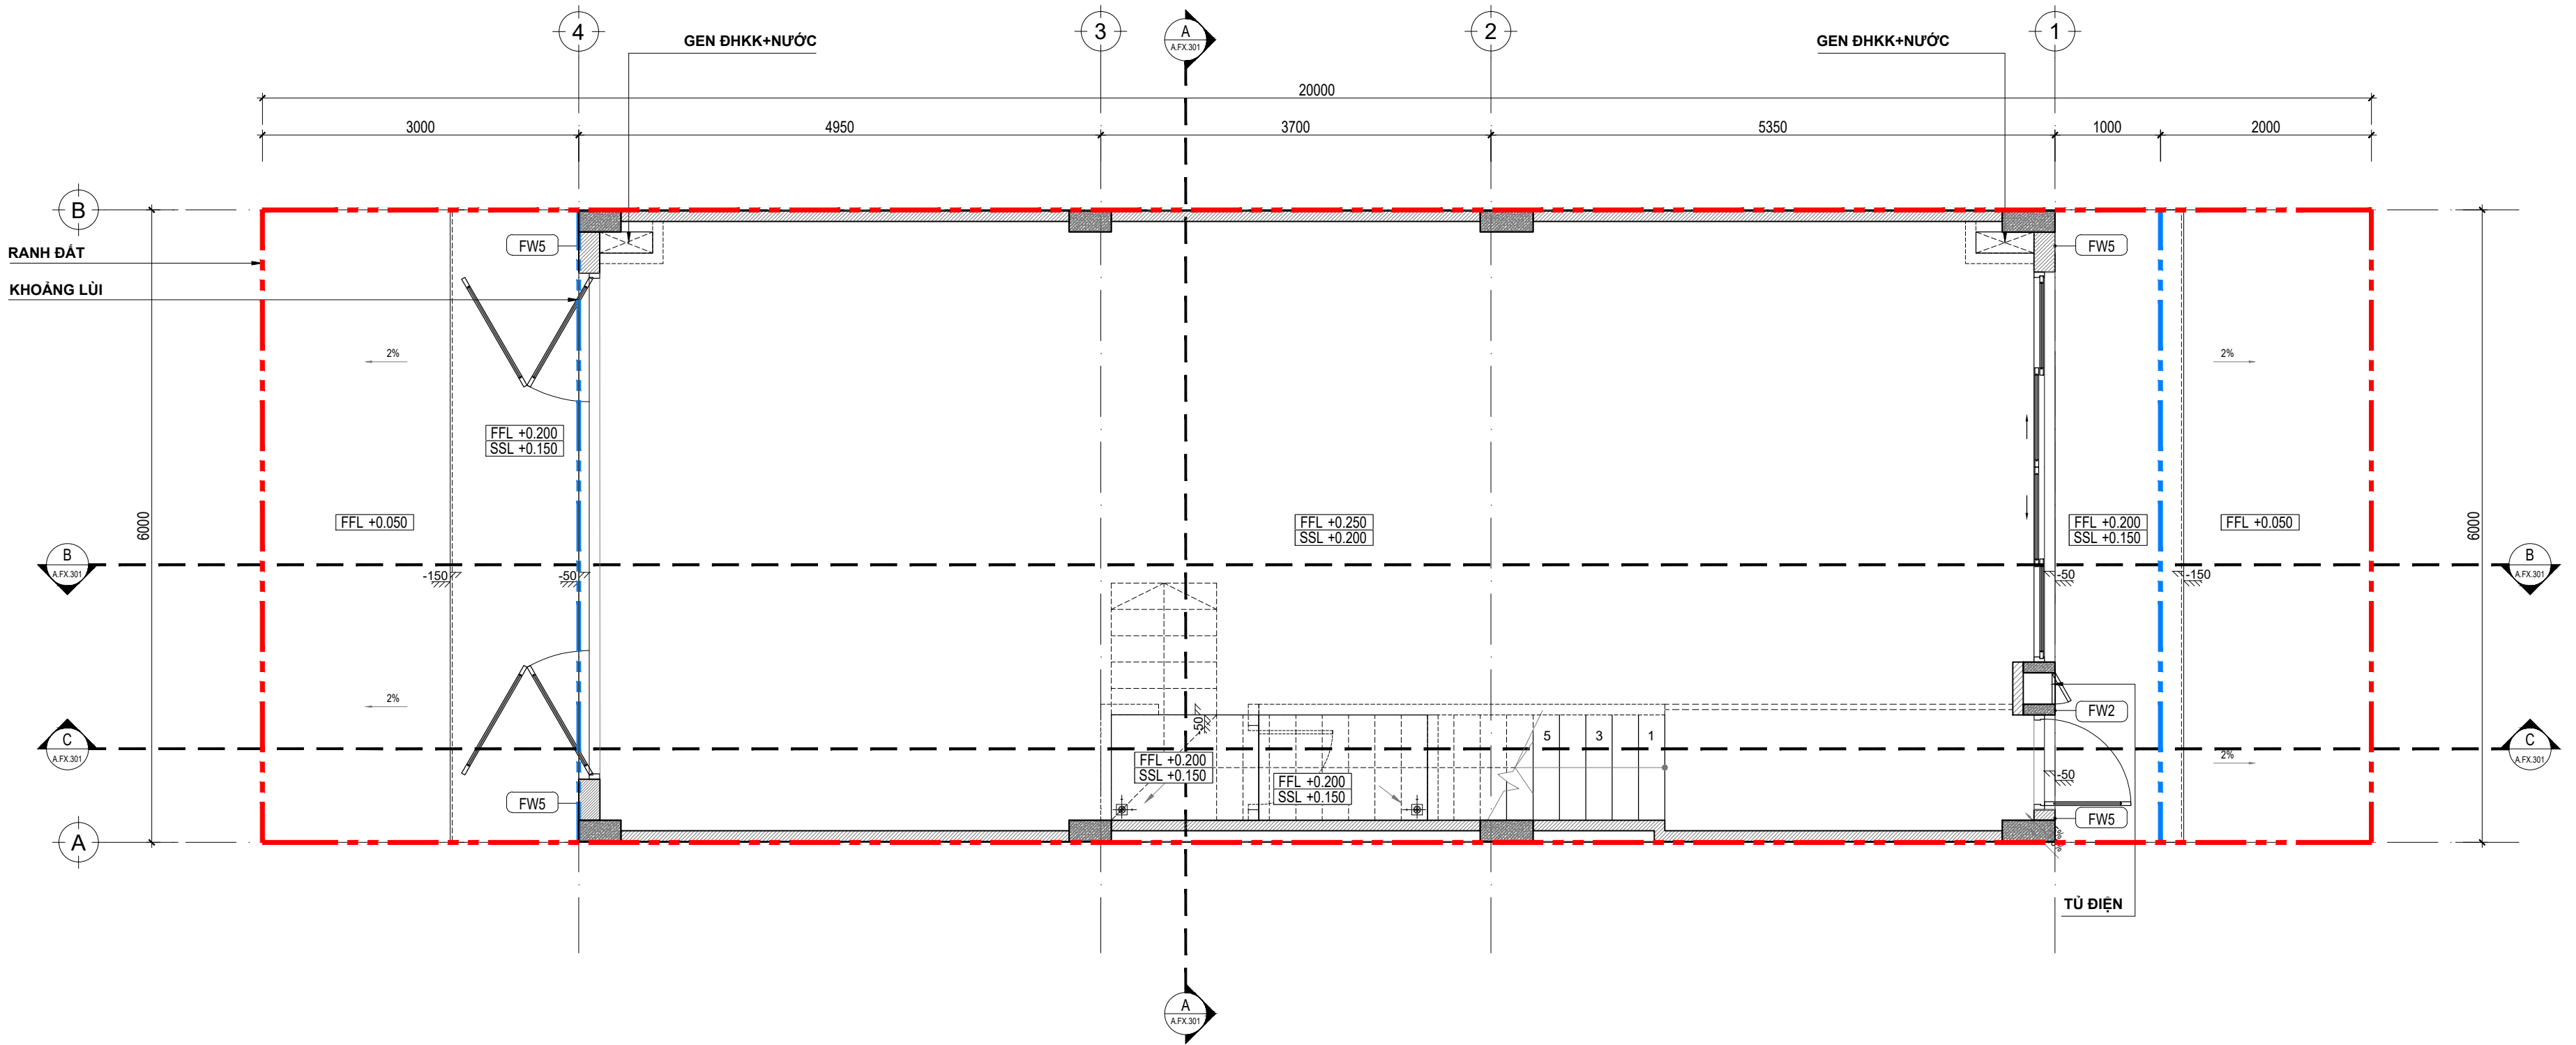


MẶT BẰNG HOÀN THIỆN TƯỜNG TẦNG 1 _ TL:1/50

VẬT LIỆU HOÀN THIỆN TƯỜNG		
KÝ HIỆU	MÔ TẢ	
FW1	TƯỜNG HOÀN THIỆN SƠN NƯỚC MÀU TRẮNG - RAL 9003	
FW2	TƯỜNG HOÀN THIỆN SƠN NƯỚC MÀU XẮM ĐẬM - RAL 7022	
FW3	TƯỜNG HOÀN THIỆN SƠN NƯỚC MÀU HỒNG NẤU - RAL 4009	
FW4	TƯỜNG HOÀN THIỆN SƠN NƯỚC MÀU VÀNG NHẠT - RAL 1015	
FW5	TƯỜNG HOÀN THIỆN SƠN NƯỚC MÀU XẮM - RAL 7042	
L1	LEN CHÂN TƯỜNG GẠCH PORCELAIN 300X600mm,CHÔNG THẨM TỎI MÀU	

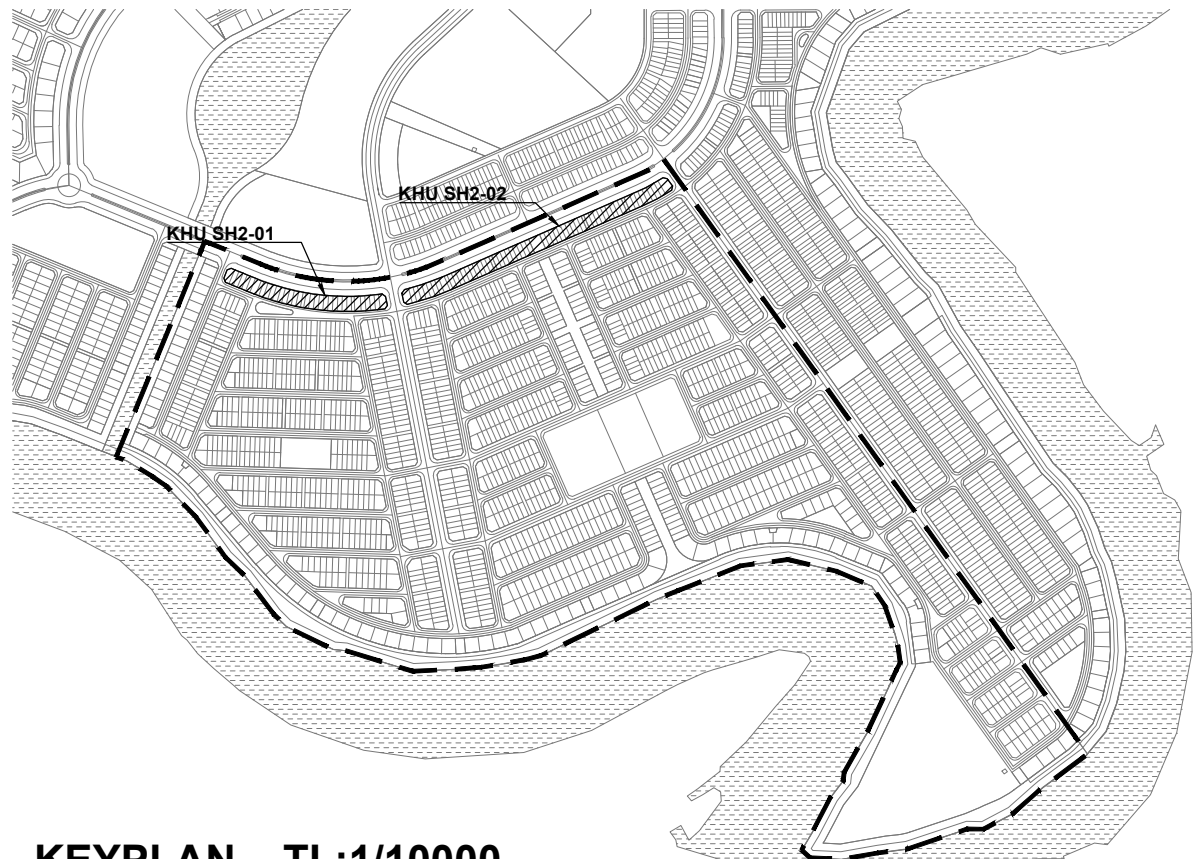


KEYPLAN _ TL:1/10000

GHI CHÚ: CAO ĐỘ ±0.00 TRONG BẢN VẼ TƯƠNG ỨNG CAO ĐỘ HỒN DẦU TẠI VÍA HÉ. CAO ĐỘ VÍA HÉ "VUI LÒNG XEM CÁC BẢN VẼ "THIẾT KẾ HẠ TẦNG"

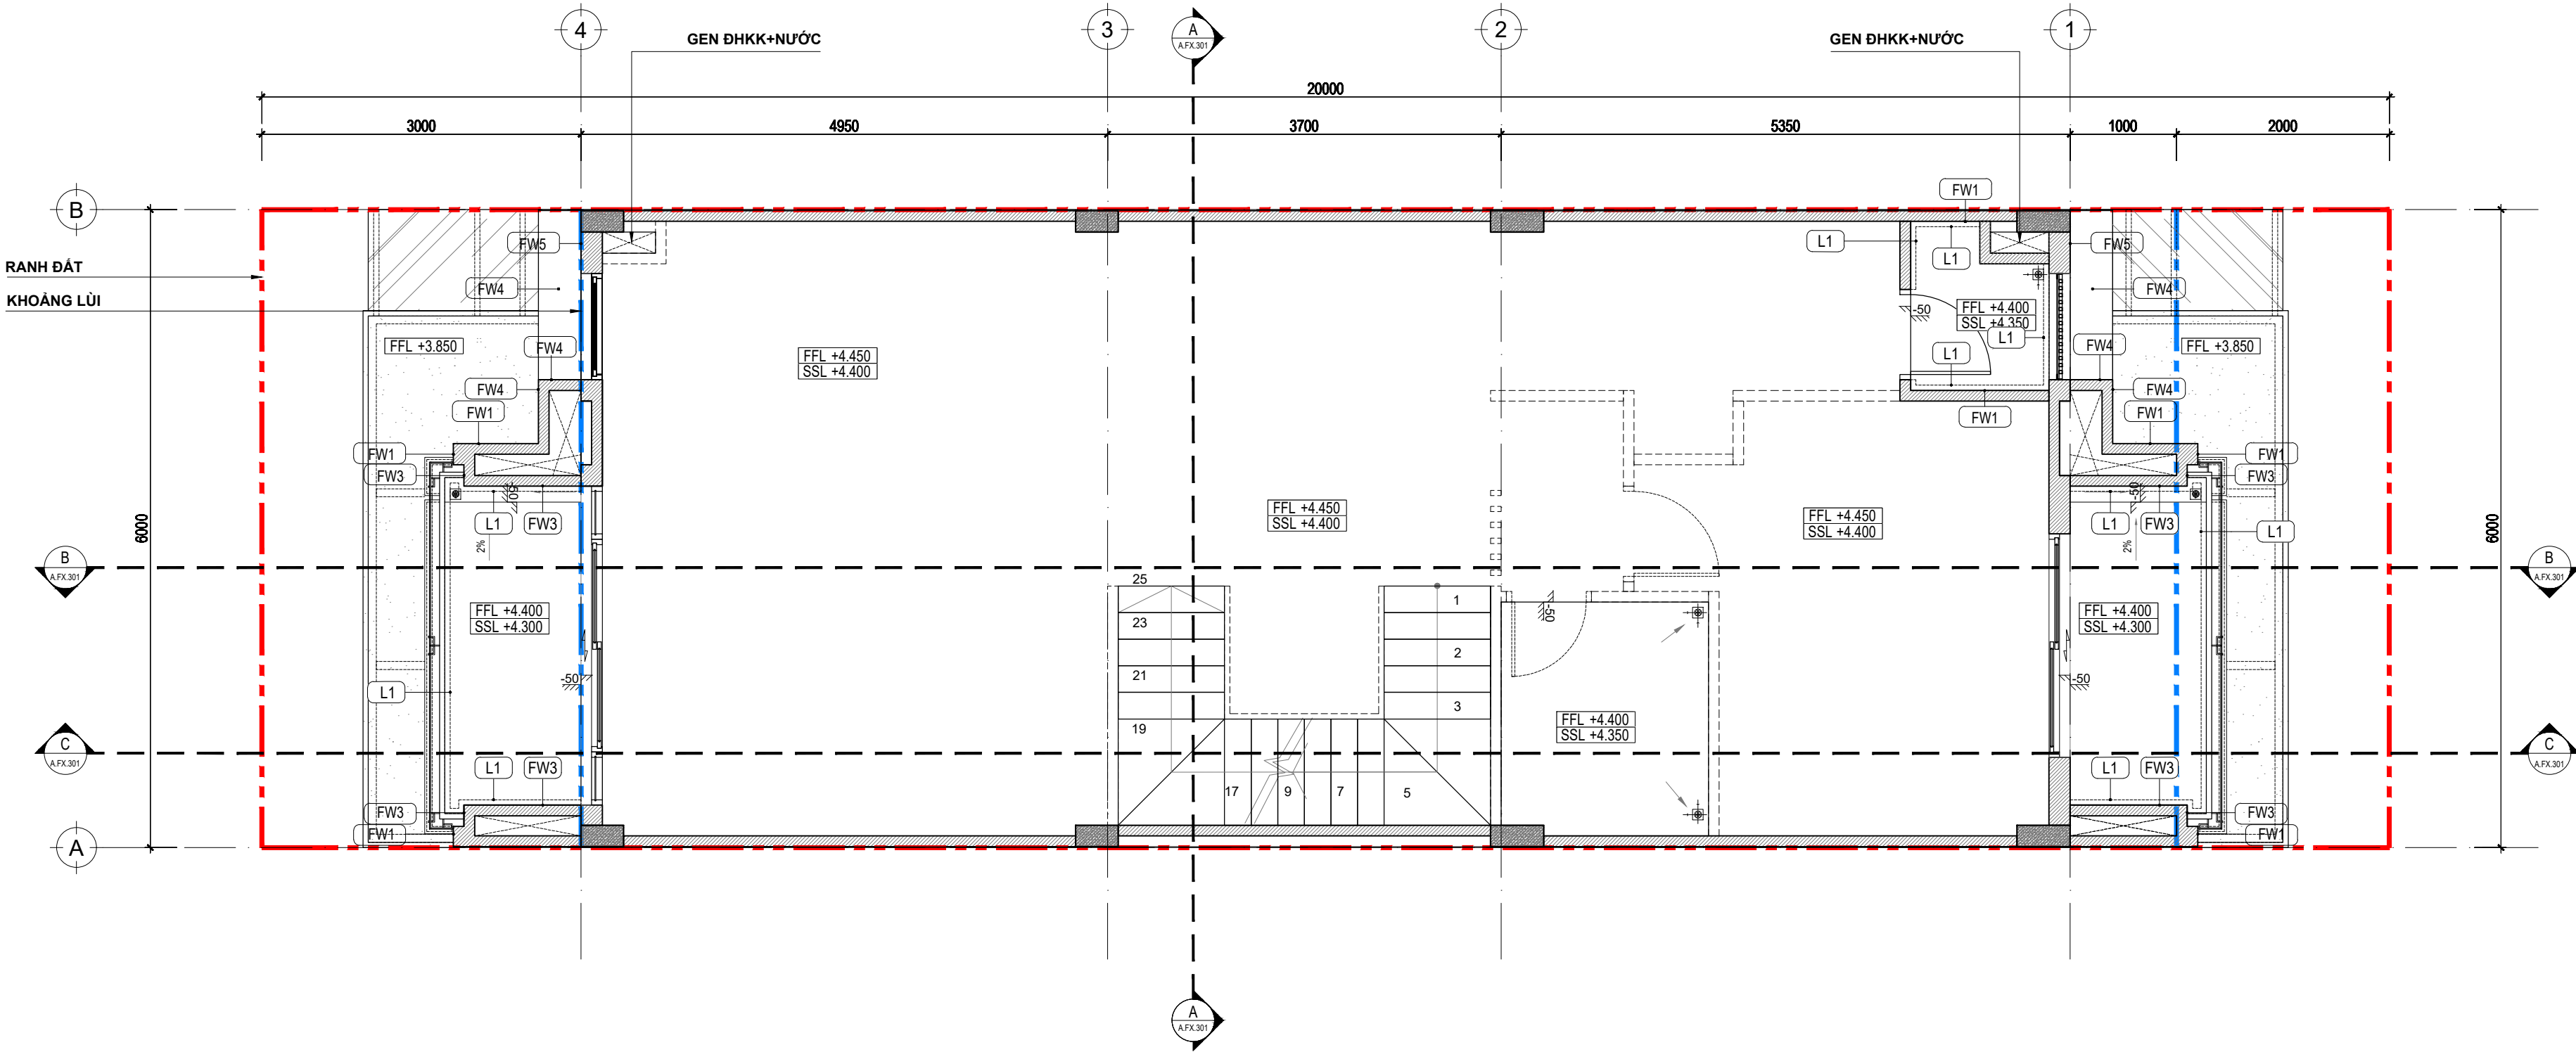


MẶT BẰNG HOÀN THIỆN TƯỜNG TẦNG 2 _ TL:1/50

VẬT LIỆU HOÀN THIỆN TƯỜNG		
KÝ HIỆU	MÔ TẢ	
FW1	TƯỜNG HOÀN THIỆN SƠN NƯỚC MÀU TRẮNG - RAL 9003	
FW2	TƯỜNG HOÀN THIỆN SƠN NƯỚC MÀU XẮM ĐẬM - RAL 7022	
FW3	TƯỜNG HOÀN THIỆN SƠN NƯỚC MÀU HỒNG NẤU - RAL 4009	
FW4	TƯỜNG HOÀN THIỆN SƠN NƯỚC MÀU VÀNG NHẠT - RAL 1015	
FW5	TƯỜNG HOÀN THIỆN SƠN NƯỚC MÀU XẮM - RAL 7042	
L1	LEN CHÂN TƯỜNG GẠCH PORCELAIN 300X600mm,CHÔNG THÂM TỐI MÀU	

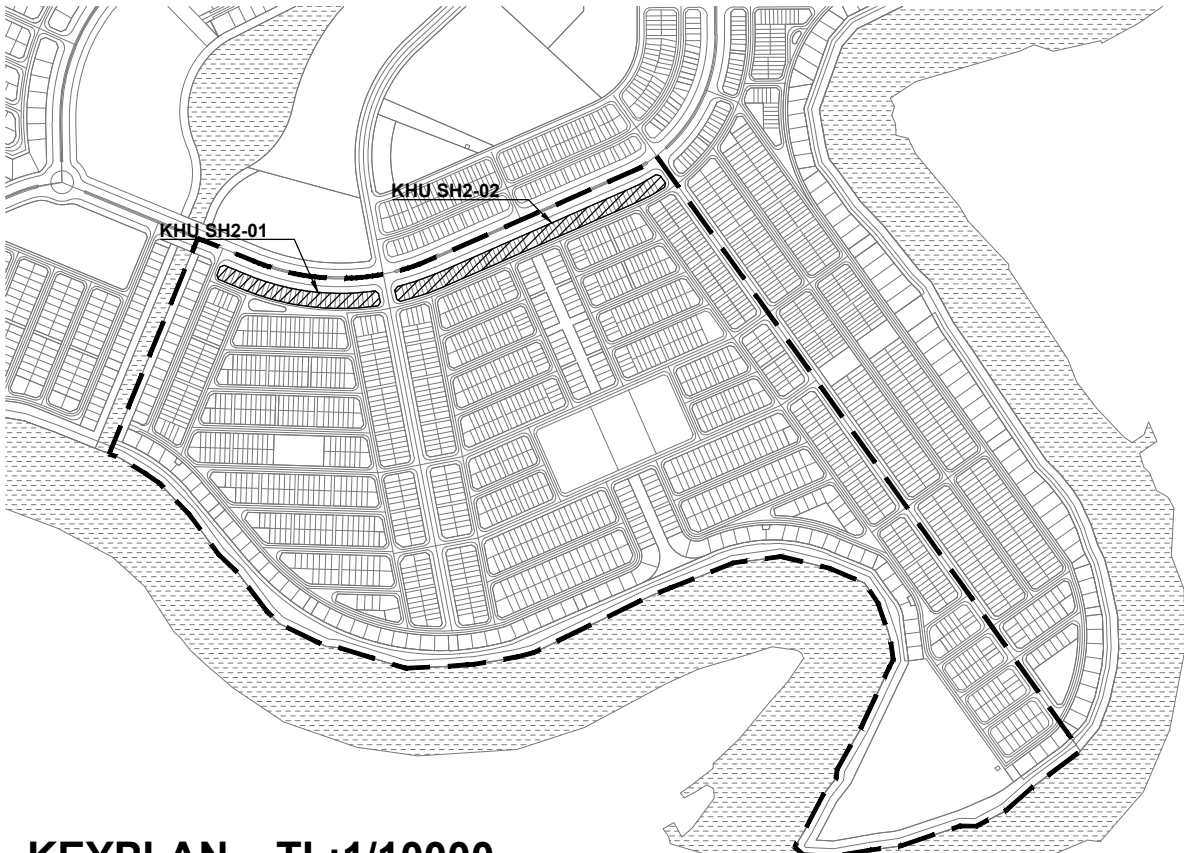


KEYPLAN _ TL:1/10000

GHI CHÚ: CAO ĐỘ ±0.00 TRONG BẢN VẼ TƯƠNG ỨNG CAO ĐỘ HỒN DẦU TẠI VÍA HÉ. CAO ĐỘ VÍA HÉ "VUI LÒNG XEM CÁC BẢN VẼ "THIẾT KẾ HẠ TẦNG"

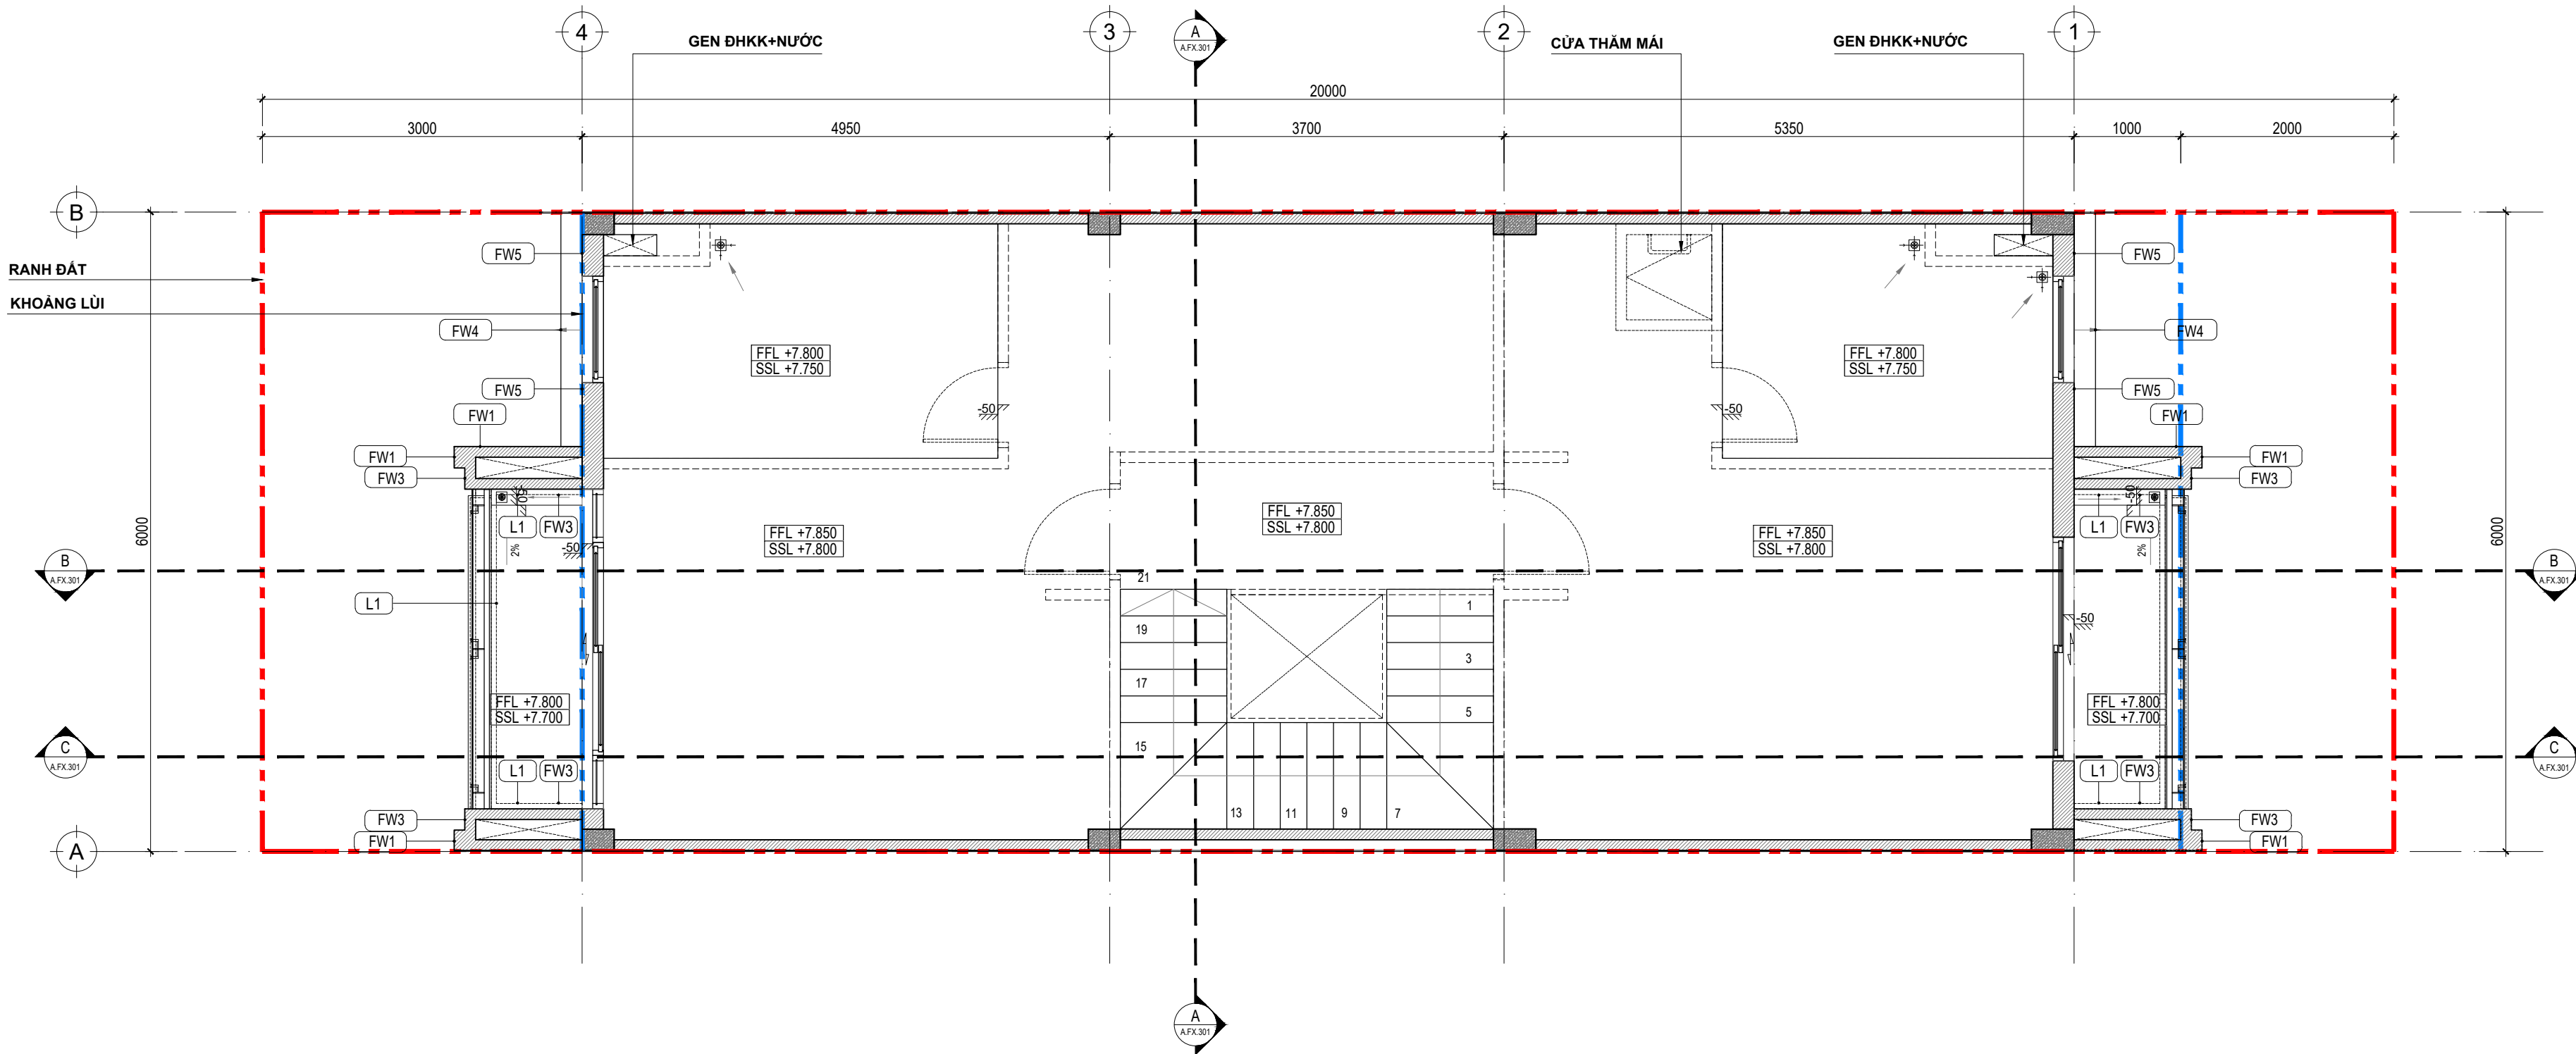


MẶT BẰNG HOÀN THIỆN TƯỜNG TẦNG 3 _ TL:1/50

VẬT LIỆU HOÀN THIỆN TƯỜNG		
KÝ HIỆU	MÔ TẢ	
FW1	TƯỜNG HOÀN THIỆN SƠN NƯỚC MÀU TRẮNG - RAL 9003	
FW2	TƯỜNG HOÀN THIỆN SƠN NƯỚC MÀU XẮM ĐẬM - RAL 7022	
FW3	TƯỜNG HOÀN THIỆN SƠN NƯỚC MÀU HỒNG NẤU - RAL 4009	
FW4	TƯỜNG HOÀN THIỆN SƠN NƯỚC MÀU VÀNG NHẠT - RAL 1015	
FW5	TƯỜNG HOÀN THIỆN SƠN NƯỚC MÀU XẮM - RAL 7042	
L1	LEN CHÂN TƯỜNG GẠCH PORCELAIN 300X600mm,CHÔNG THÂM TÓI MÀU	

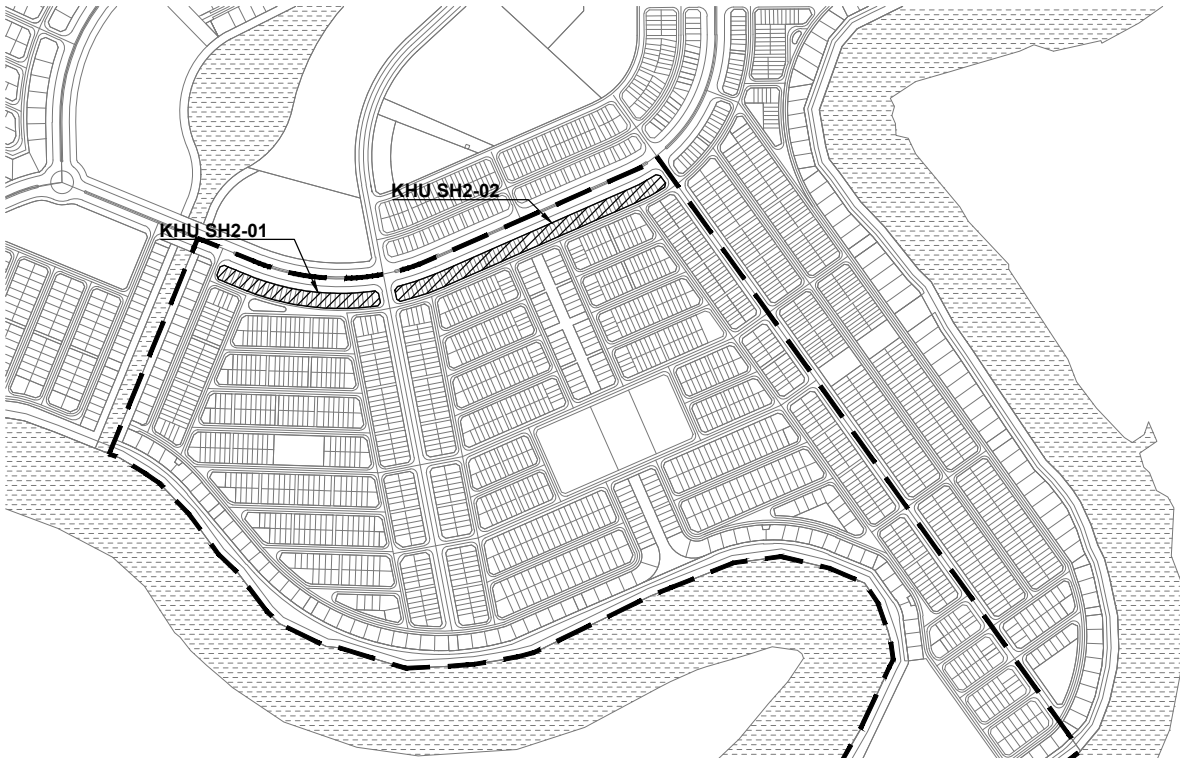


KEYPLAN _ TL:1/10000

GHI CHÚ: CAO ĐỘ ±0.00 TRONG BẢN VẼ TƯƠNG ỨNG CAO ĐỘ HỒN DẦU TẠI VÍA HÉ. CAO ĐỘ VÍA HÉ "VUI LÒNG XEM CÁC BẢN VẼ "THIẾT KẾ HẠ TẦNG"

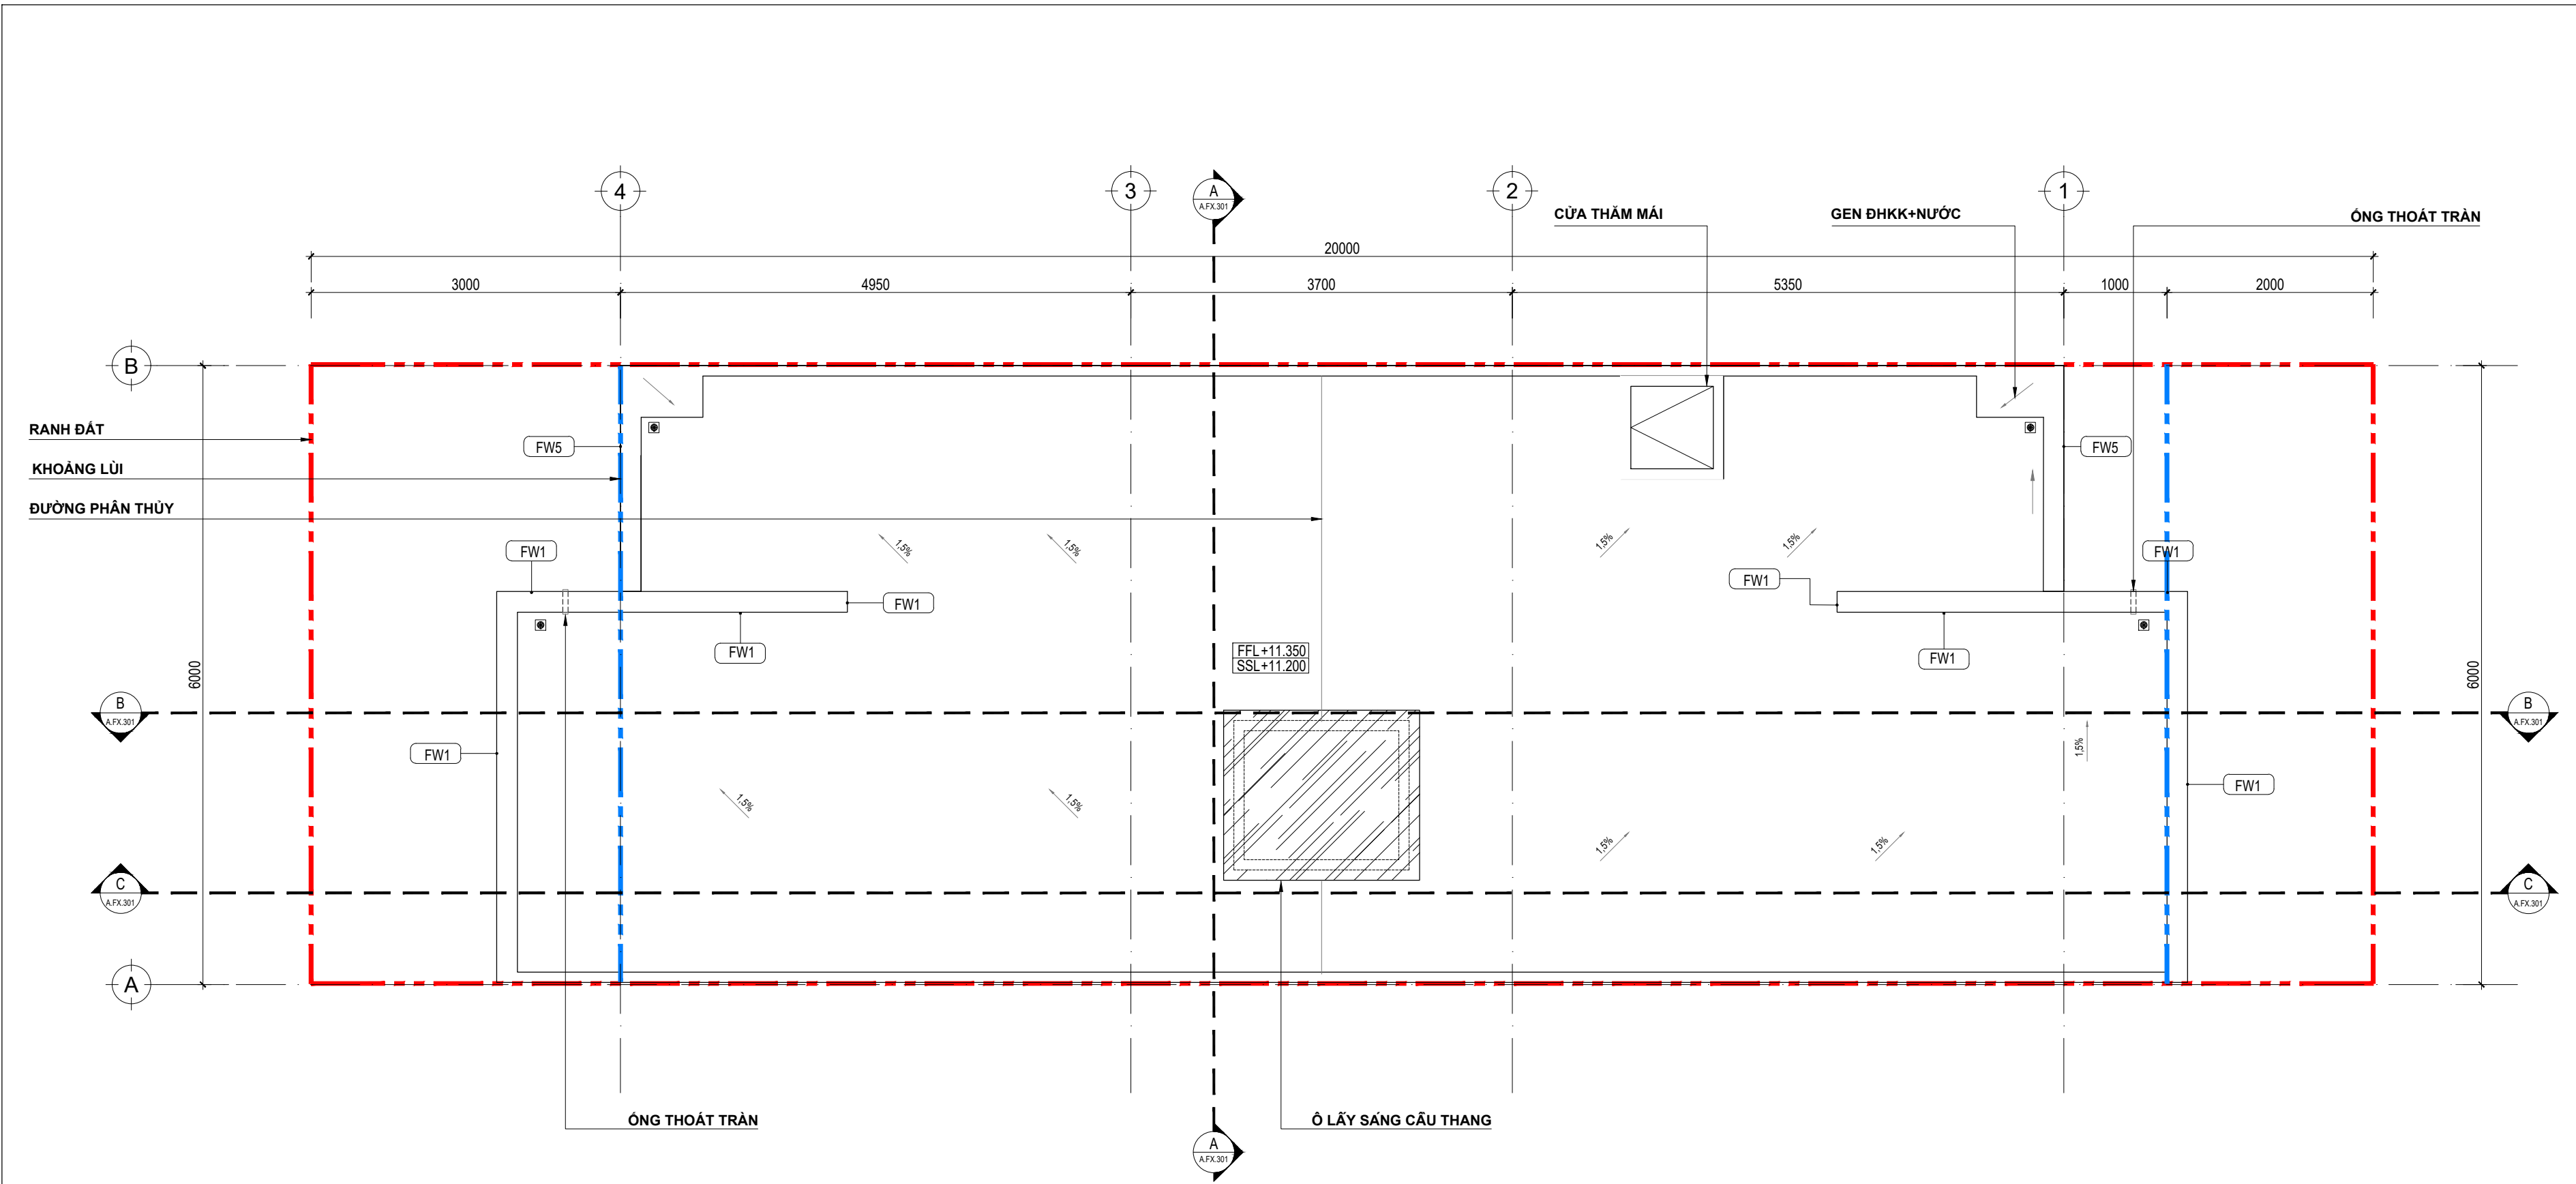


MẶT BẰNG HOÀN THIỆN TƯỜNG TẦNG MÁI _ TL:1/50

VẬT LIỆU HOÀN THIỆN TƯỜNG		
KÝ HIỆU	MÔ TẢ	
FW1	TƯỜNG HOÀN THIỆN SƠN NƯỚC MÀU TRẮNG - RAL 9003	
FW2	TƯỜNG HOÀN THIỆN SƠN NƯỚC MÀU XÁM ĐẬM - RAL 7022	
FW3	TƯỜNG HOÀN THIỆN SƠN NƯỚC MÀU HỒNG NẤU - RAL 4009	
FW4	TƯỜNG HOÀN THIỆN SƠN NƯỚC MÀU VÀNG NHẠT - RAL 1015	
FW5	TƯỜNG HOÀN THIỆN SƠN NƯỚC MÀU XÁM - RAL 7042	
L1	LEN CHÂN TƯỜNG GẠCH PORCELAIN 300X600mm,CHÔNG THẨM TỎI MÀU	

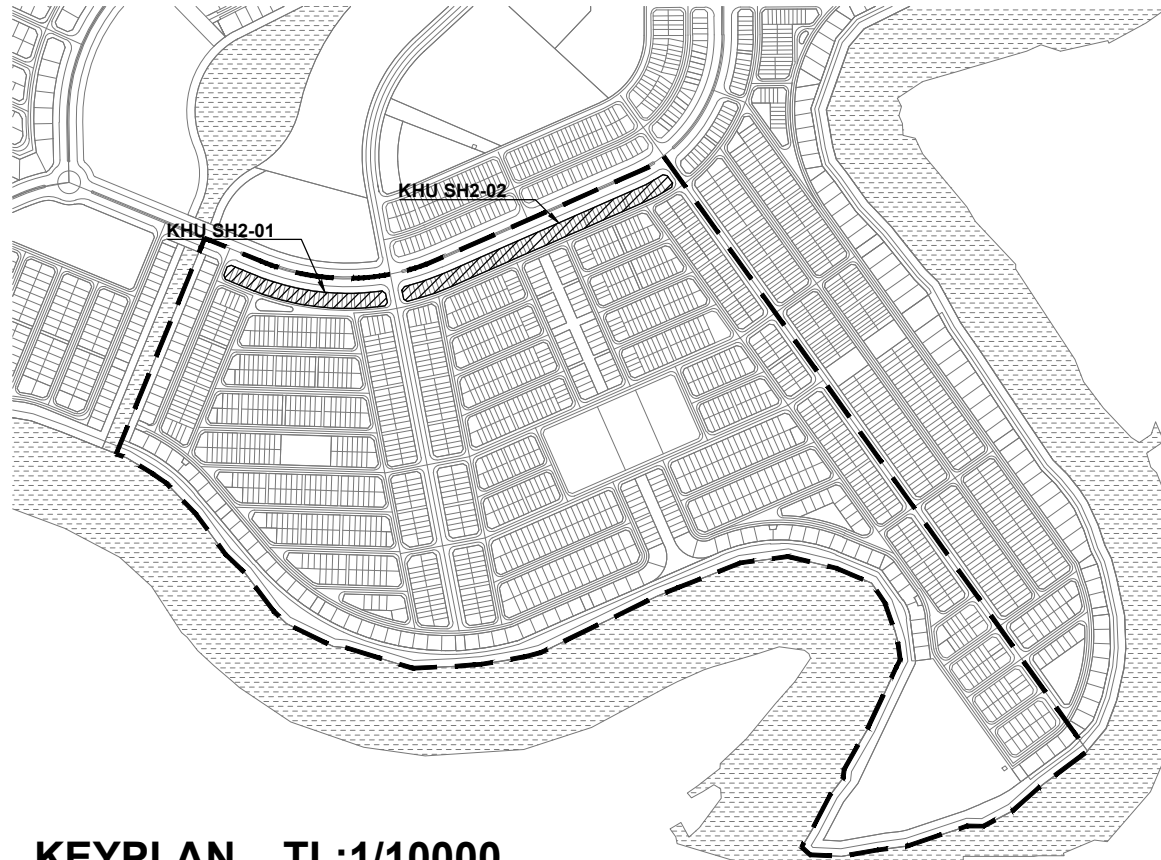


KEYPLAN _ TL:1/10000

GHI CHÚ: CAO ĐỘ ±0.00 TRONG BẢN VẼ TƯƠNG ỨNG CAO ĐỘ HỒN DẦU TẠI VÍA HÉ. CAO ĐỘ VÍA HÉ "VUI LÒNG XEM CÁC BẢN VẼ "THIẾT KẾ HẠ TẦNG"

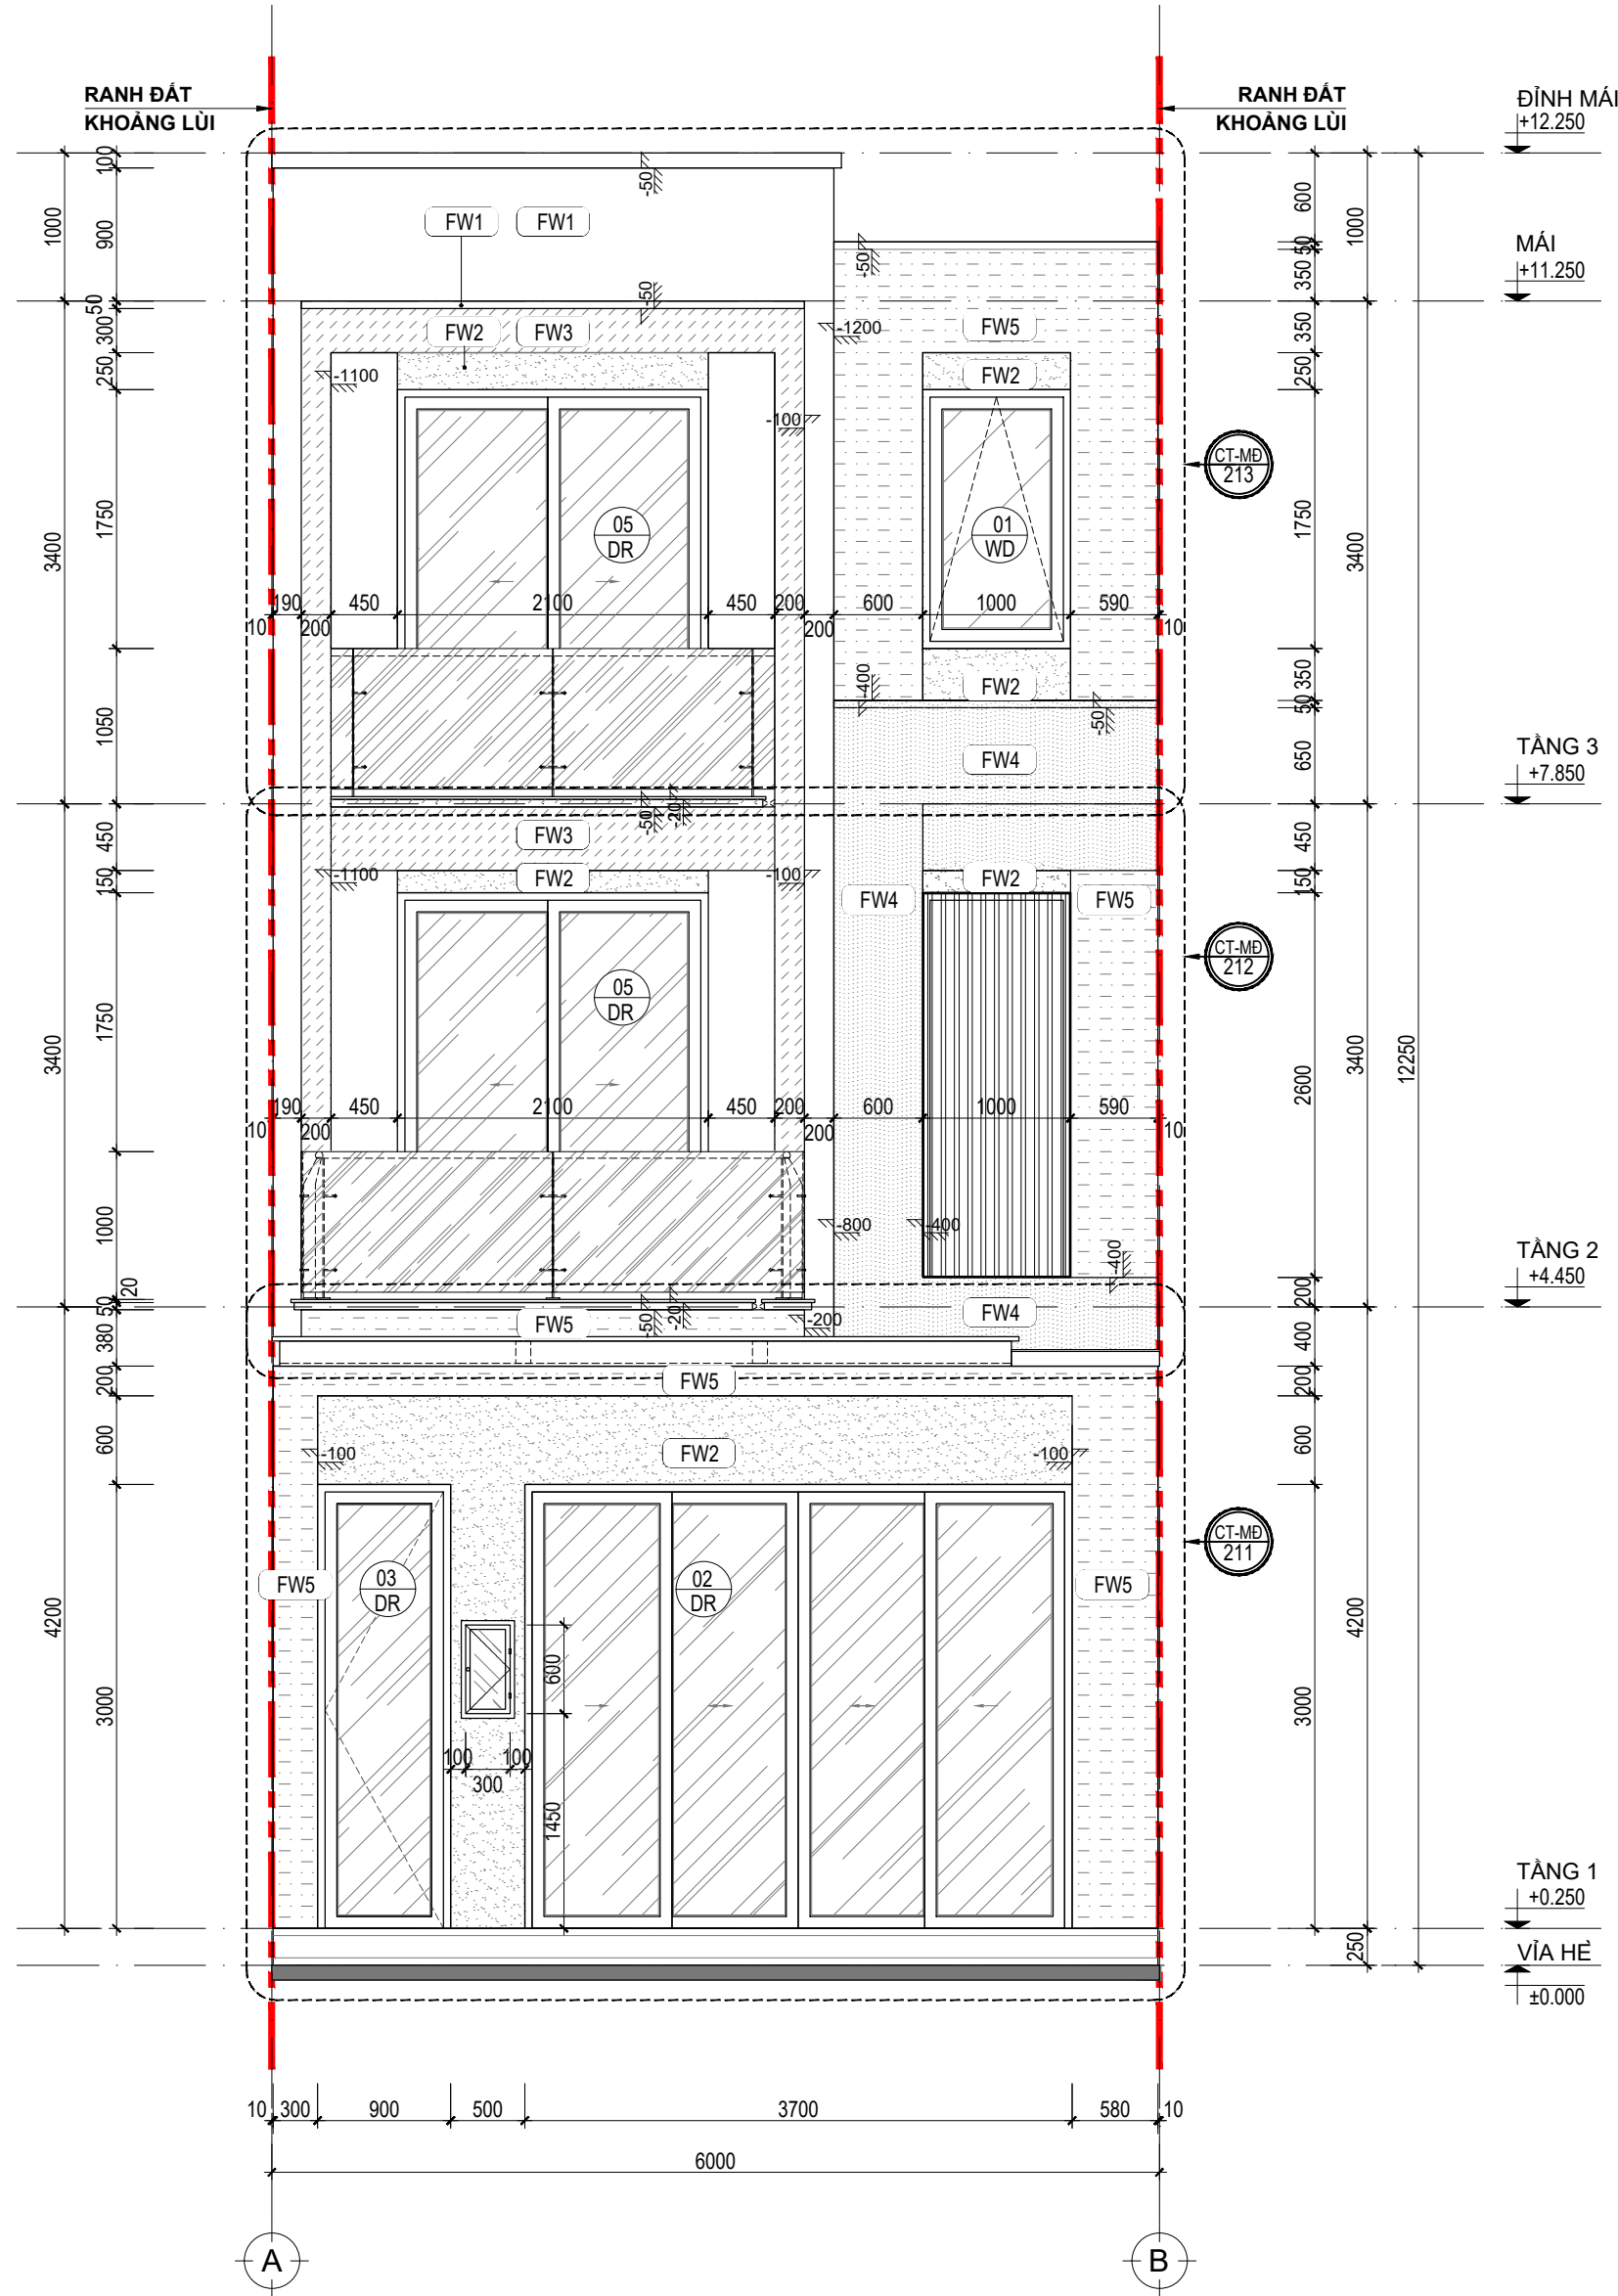


VẬT LIỆU HOÀN THIỆN TƯỜNG		
KÝ HIỆU	MÔ TẢ	
FW1	TƯỜNG HOÀN THIỆN SƠN NƯỚC MÀU TRẮNG - RAL 9003	
FW2	TƯỜNG HOÀN THIỆN SƠN NƯỚC MÀU XÁM ĐẬM - RAL 7022	
FW3	TƯỜNG HOÀN THIỆN SƠN NƯỚC MÀU HỒNG NẬU - RAL 4009	
FW4	TƯỜNG HOÀN THIỆN SƠN NƯỚC MÀU VÀNG NHẠT - RAL 1015	
FW5	TƯỜNG HOÀN THIỆN SƠN NƯỚC MÀU XÁM - RAL 7042	
L1	LEN CHÂN TƯỜNG GẠCH PORCELAIN 300X600mm,CHÔNG THÂM TÓI MÀU	

MẶT ĐƯNG A-B _ TL:1/50

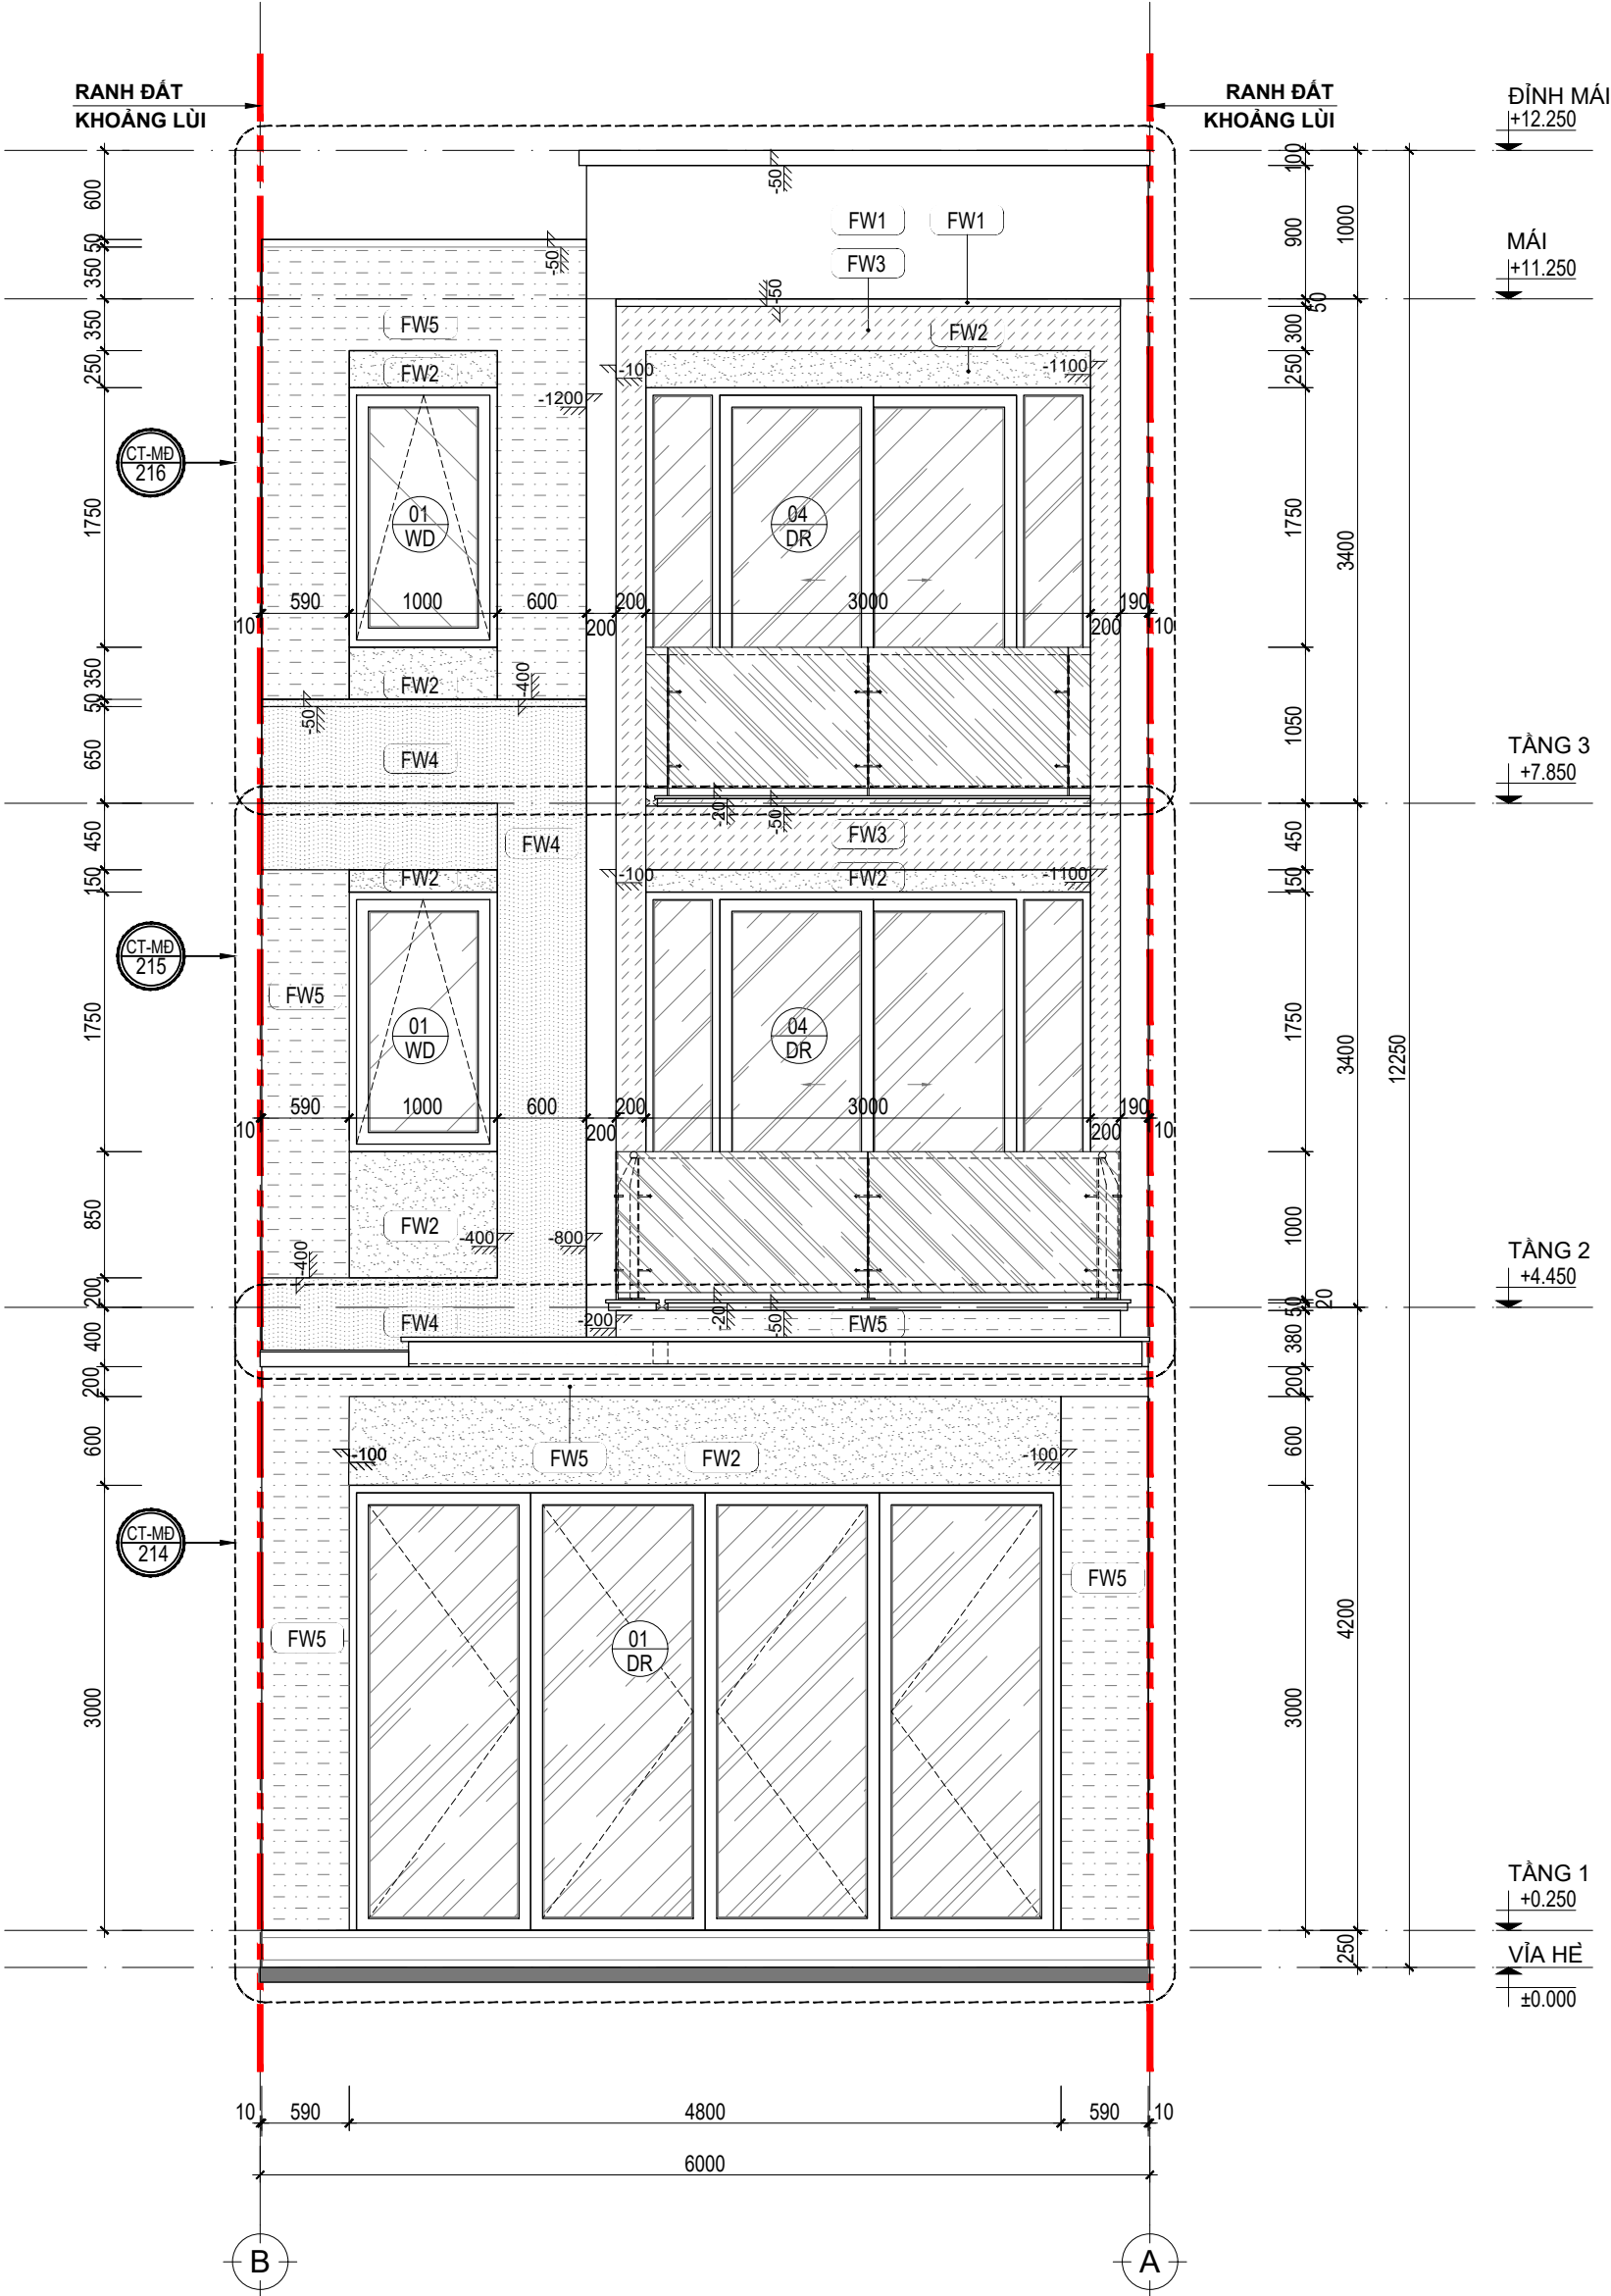


MẶT ĐỨNG B-A _ TL:1/50


VẬT LIỆU HOÀN THIỆN TƯỜNG		
KÝ HIỆU	MÔ TẢ	
FW1	TƯỜNG HOÀN THIỆN SƠN NƯỚC MÀU TRẮNG - RAL 9003	
FW2	TƯỜNG HOÀN THIỆN SƠN NƯỚC MÀU XÁM ĐẬM - RAL 7022	
FW3	TƯỜNG HOÀN THIỆN SƠN NƯỚC MÀU HỒNG NẬU - RAL 4009	
FW4	TƯỜNG HOÀN THIỆN SƠN NƯỚC MÀU VÀNG NHẠT - RAL 1015	
FW5	TƯỜNG HOÀN THIỆN SƠN NƯỚC MÀU XÁM - RAL 7042	
L1	LEN CHÂN TƯỜNG GẠCH PORCELAIN 300X600mm,CHỐNG THẤM TÓI MÀU	

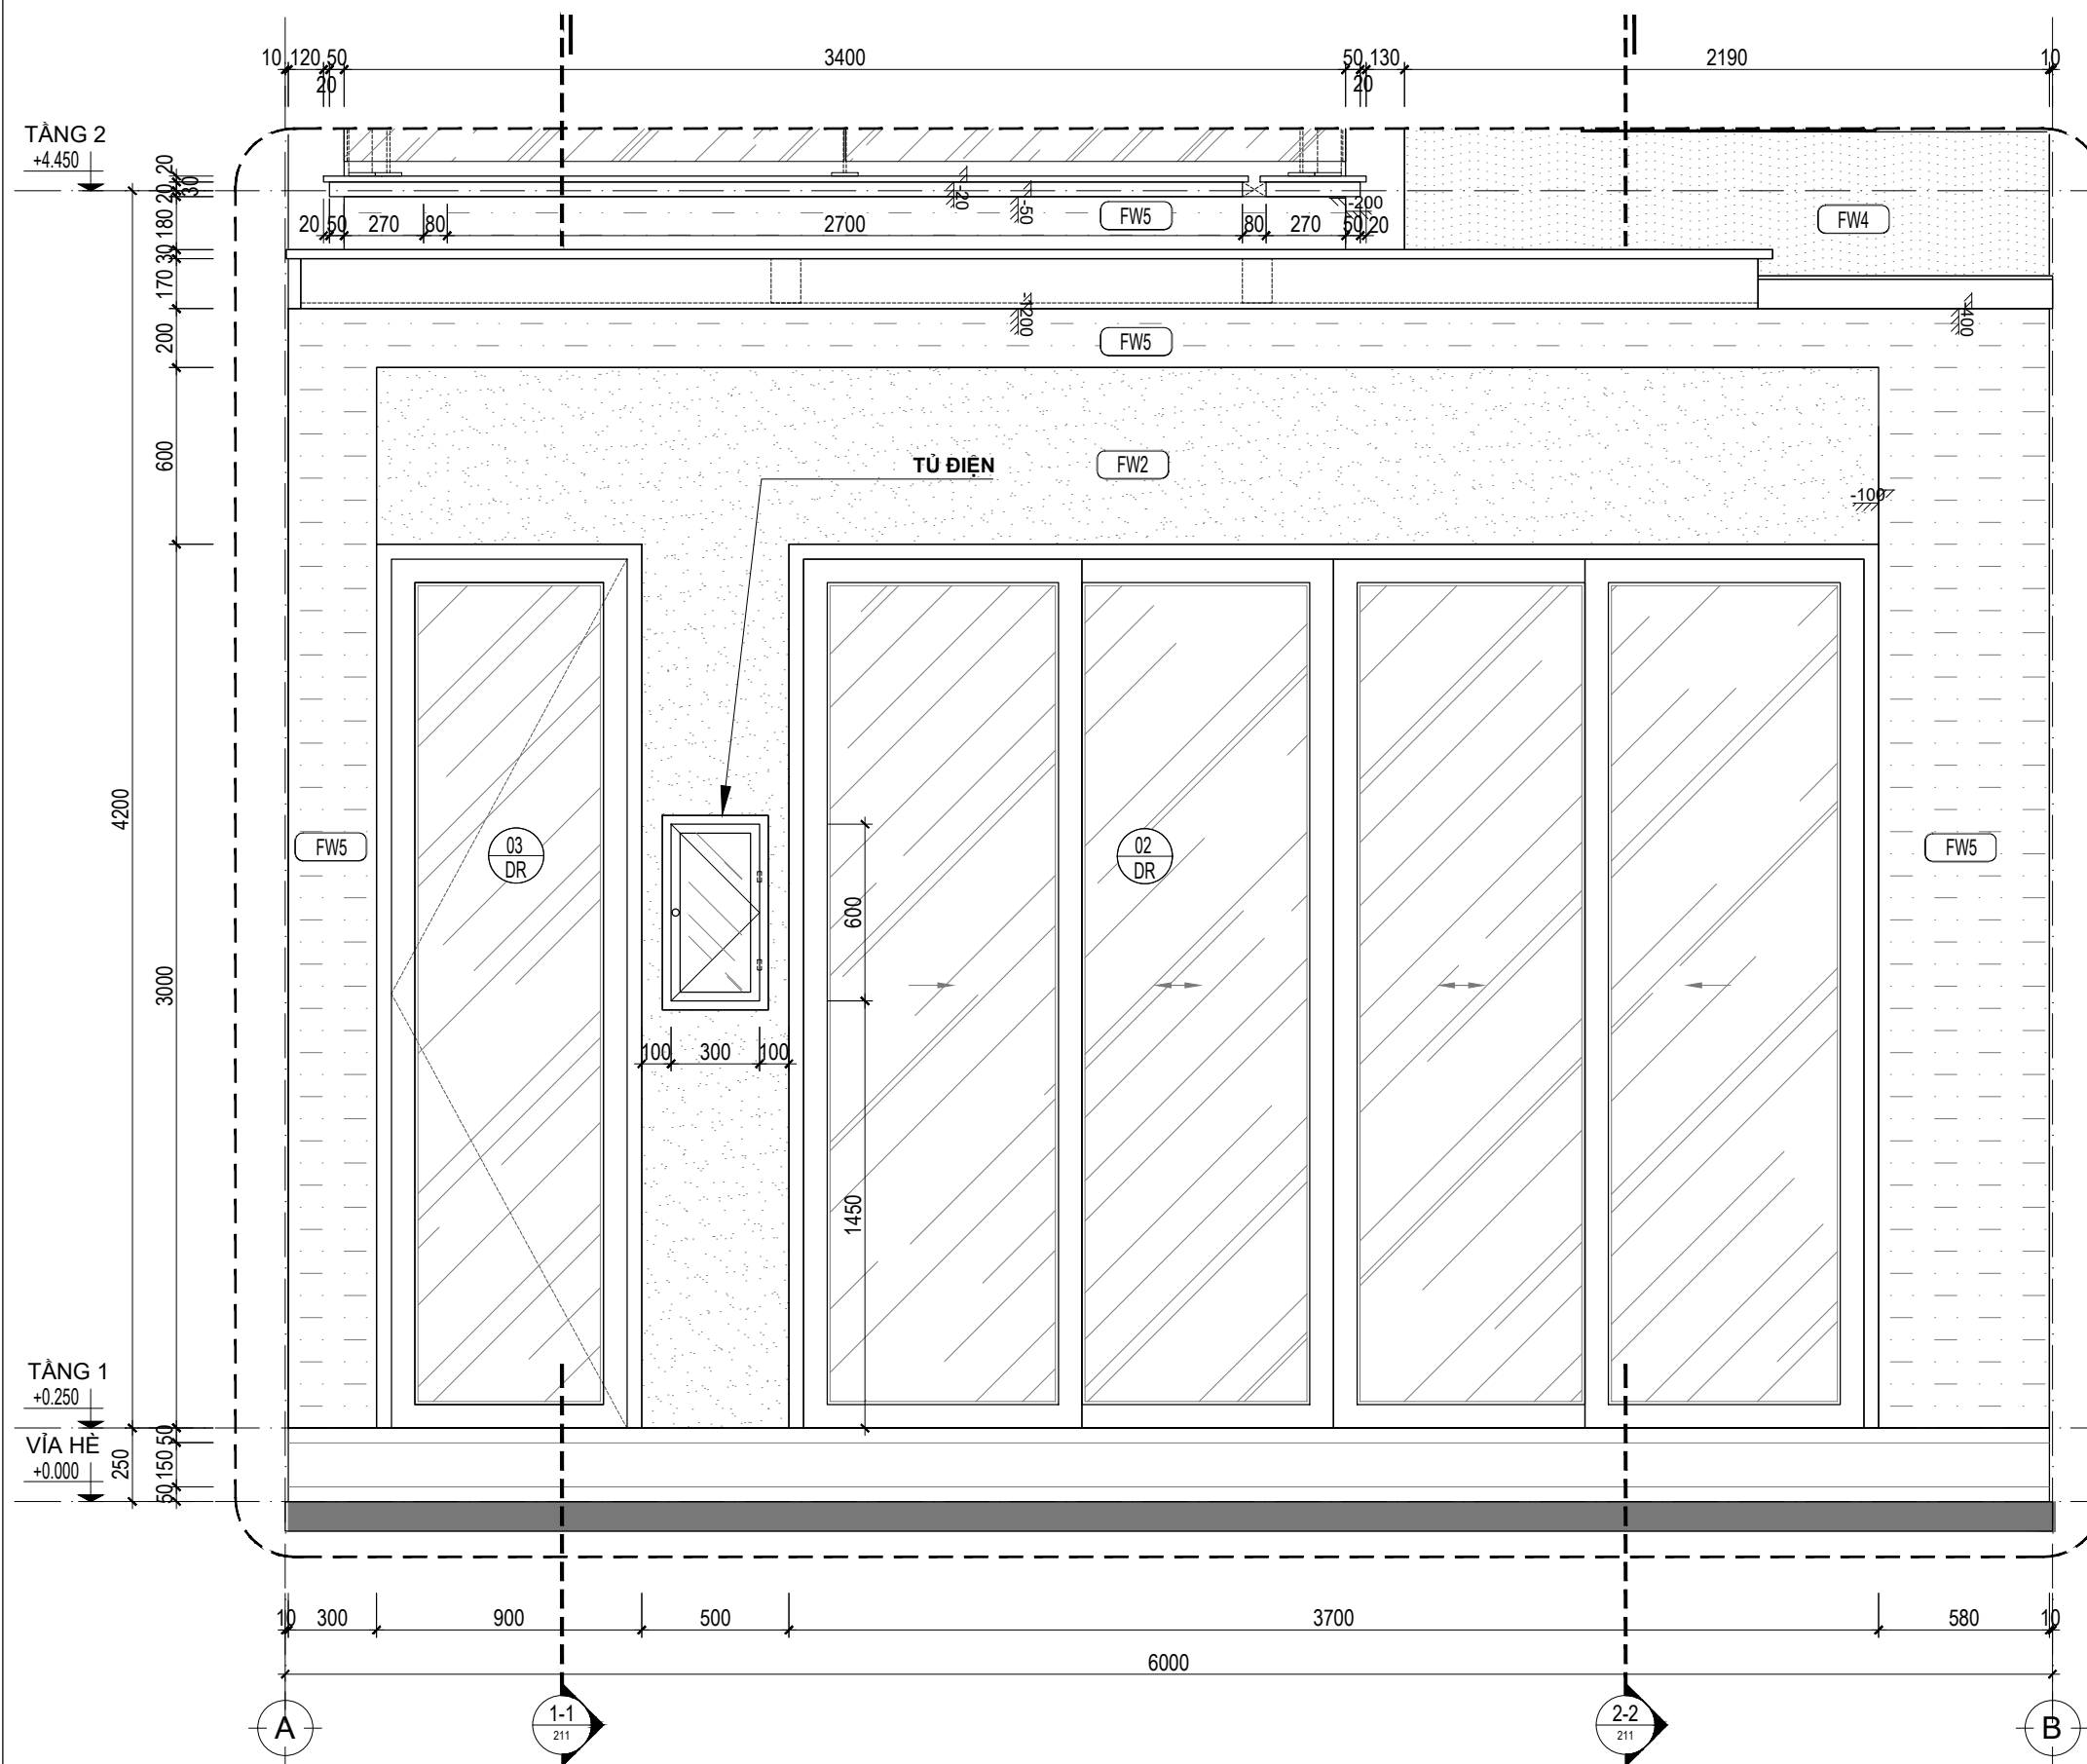


MẶT ĐỨNG TRÍCH ĐOẠN A-B - TẦNG 1_TL:1/25

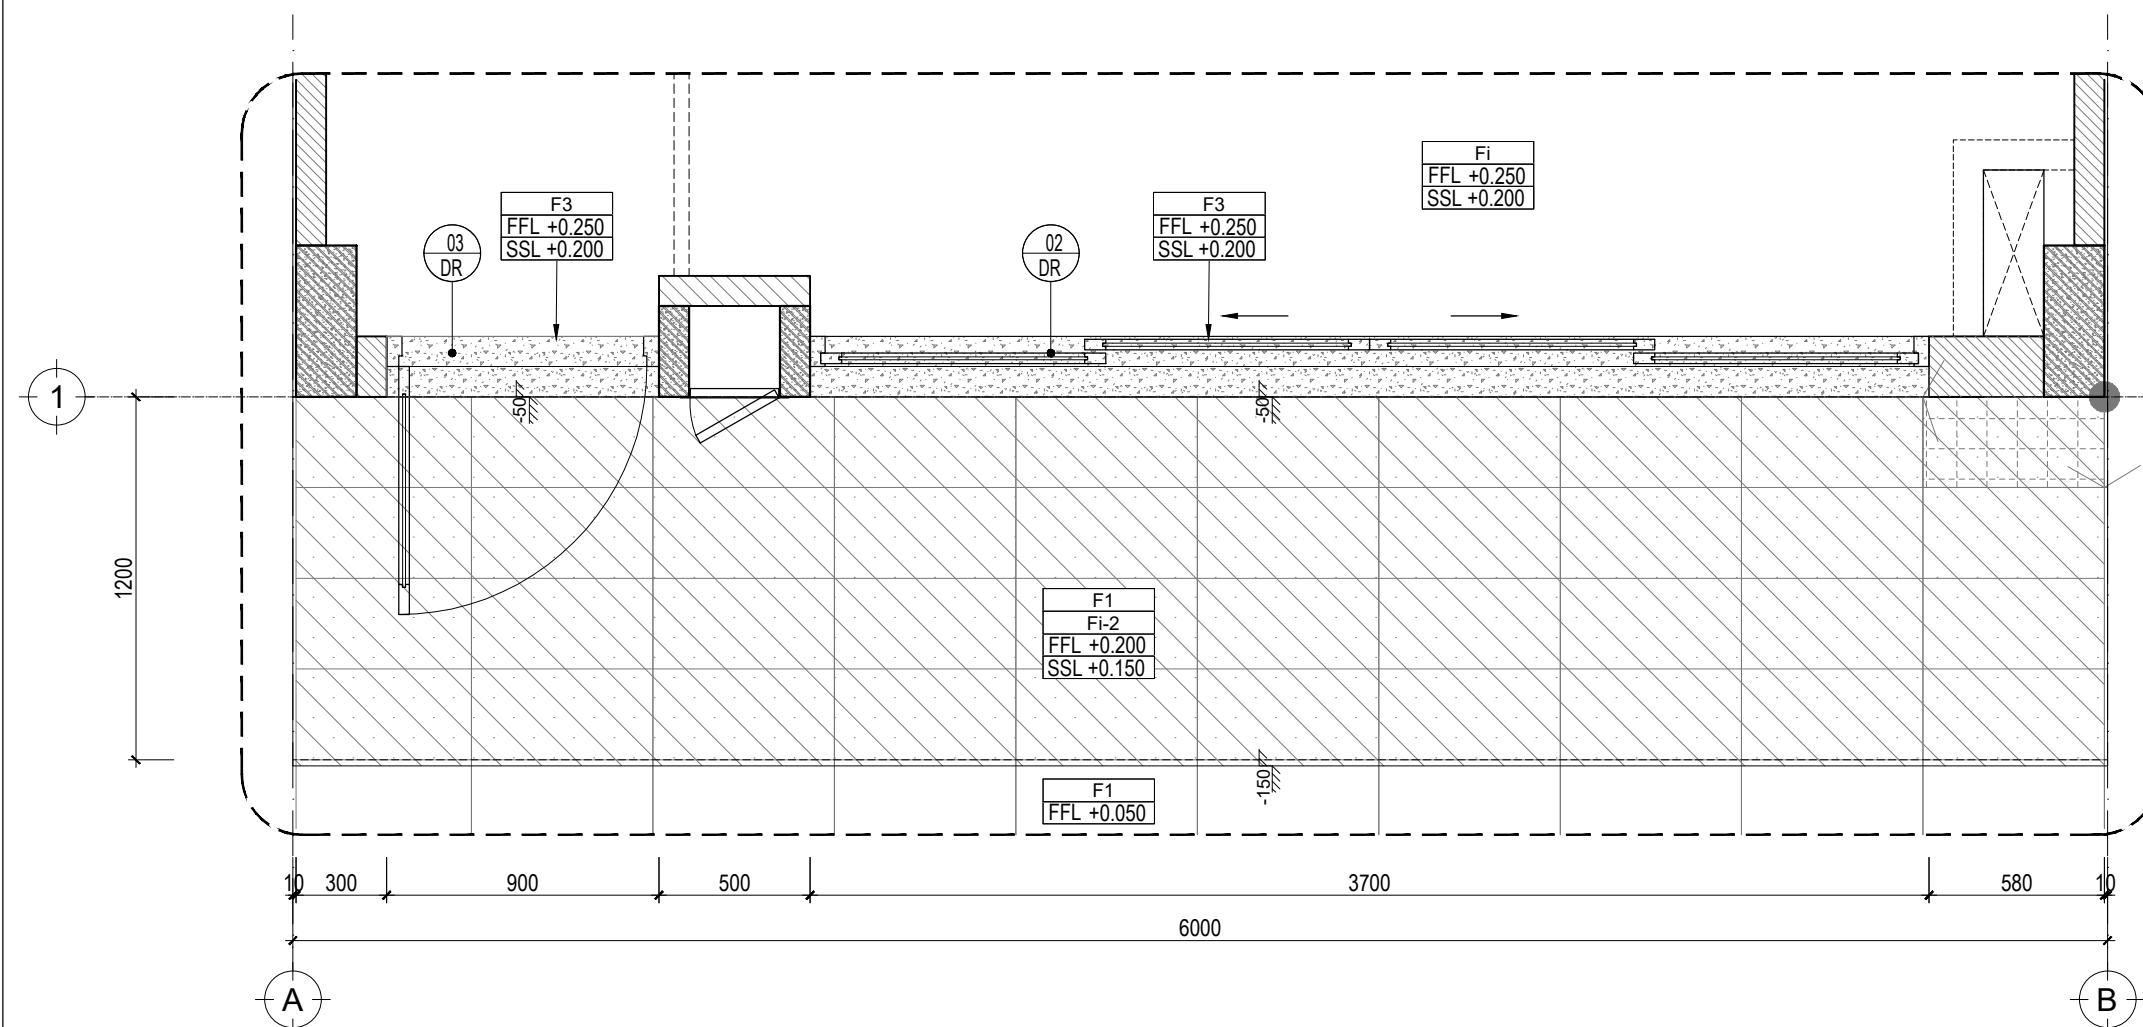

MẶT BẰNG TRÍCH ĐOẠN A-B- TẦNG 1_TL:1/25

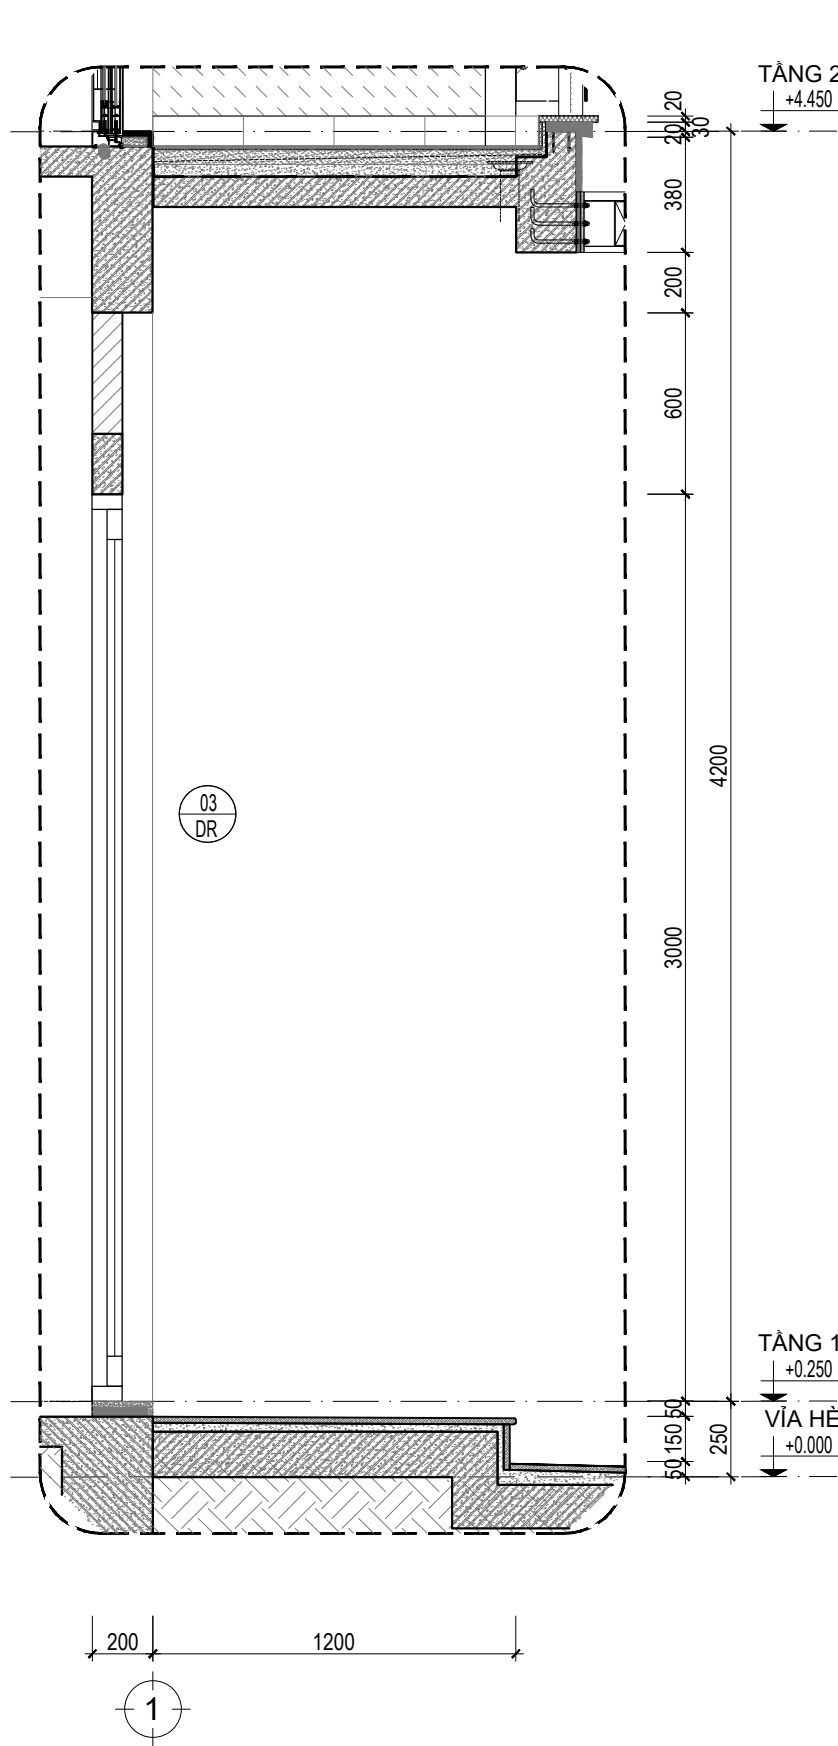


M. CẮT TRÍCH ĐOẠN 1-1_TL:1/25

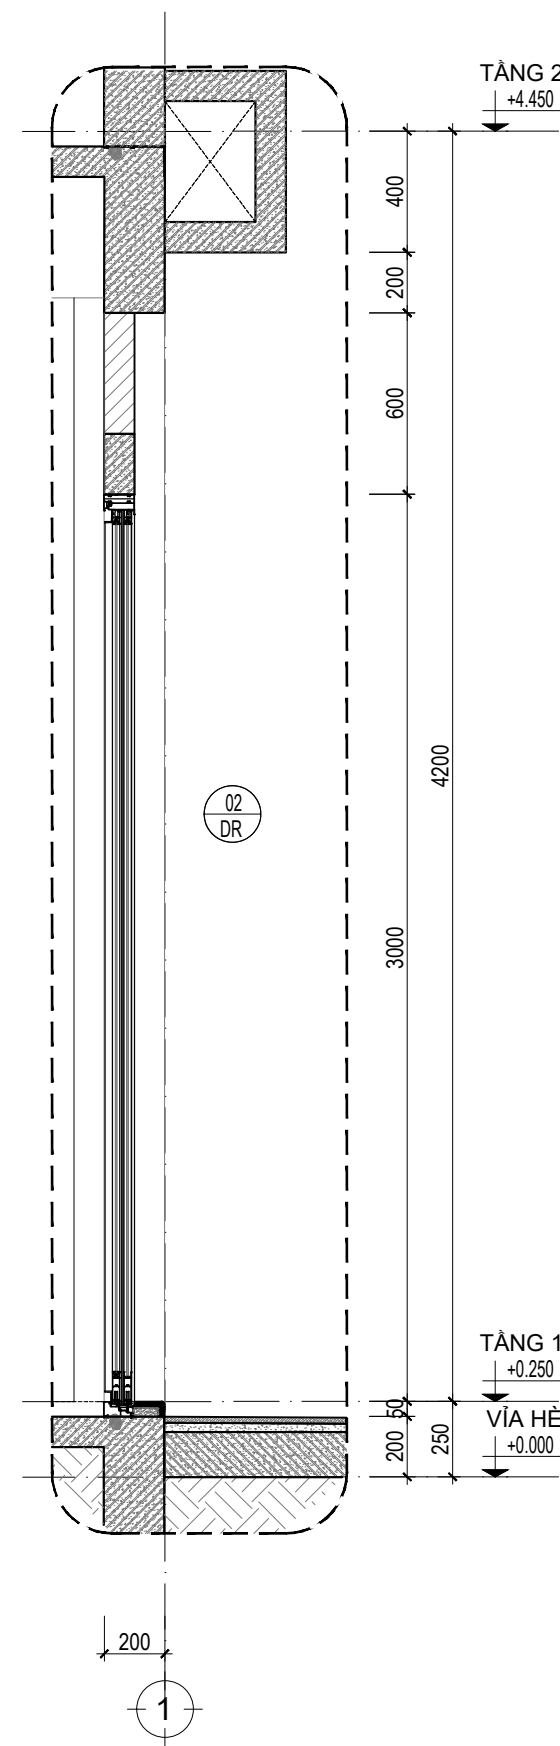


M. CẮT TRÍCH ĐOẠN 2-2_TL:1/25

VẬT LIỆU HOÀN THIỆN TƯỜNG	
KÝ HIỆU	MÔ TẢ
FW1	TƯỜNG HOÀN THIỆN SƠN NƯỚC MÀU TRẮNG - RAL 9003
FW2	TƯỜNG HOÀN THIỆN SƠN NƯỚC MÀU XẮM ĐẬM - RAL 7022
FW3	TƯỜNG HOÀN THIỆN SƠN NƯỚC MÀU HỒNG NÂU - RAL 4009
FW4	TƯỜNG HOÀN THIỆN SƠN NƯỚC MÀU VÀNG NHẠT - RAL 1015
FW5	TƯỜNG HOÀN THIỆN SƠN NƯỚC MÀU XẮM - RAL 7042
L1	LEN CHÂN TƯỜNG GẠCH PORCELAIN 300X600mm,CHÔNG THÂM TỐI MÀU

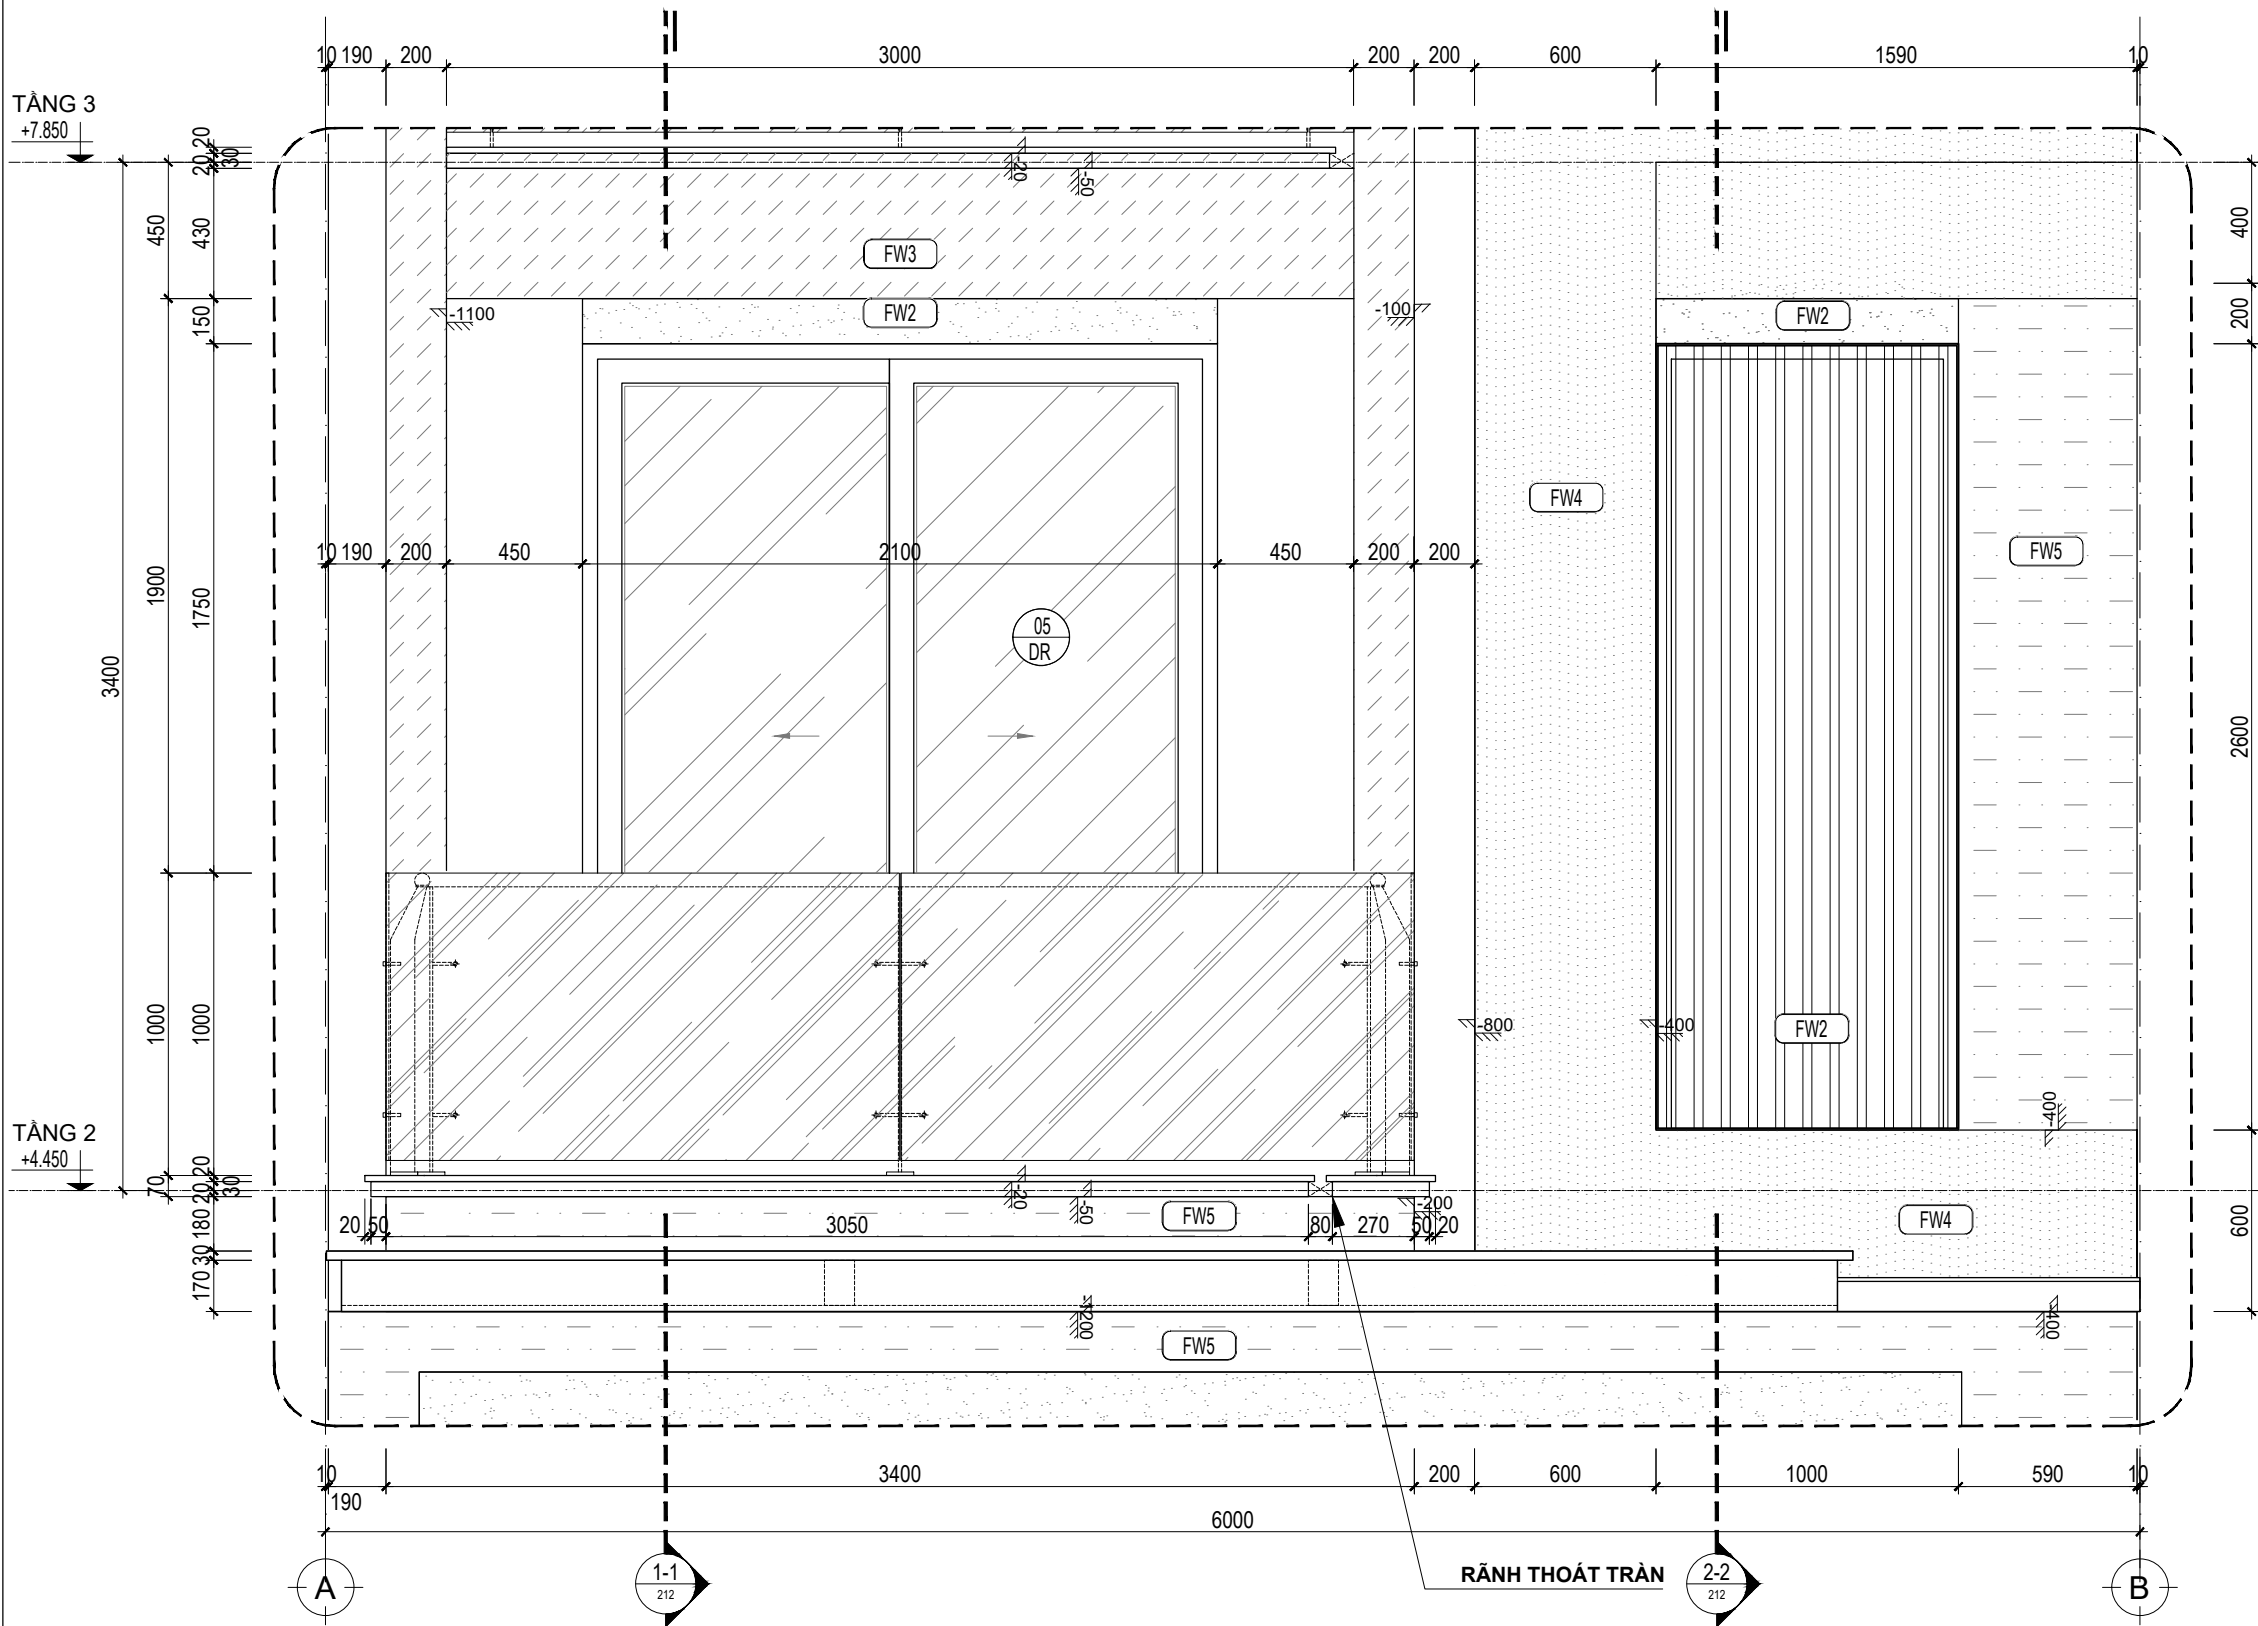


MẶT ĐƯNG TRÍCH ĐOẠN A-B - TẦNG 2_TL:1/25

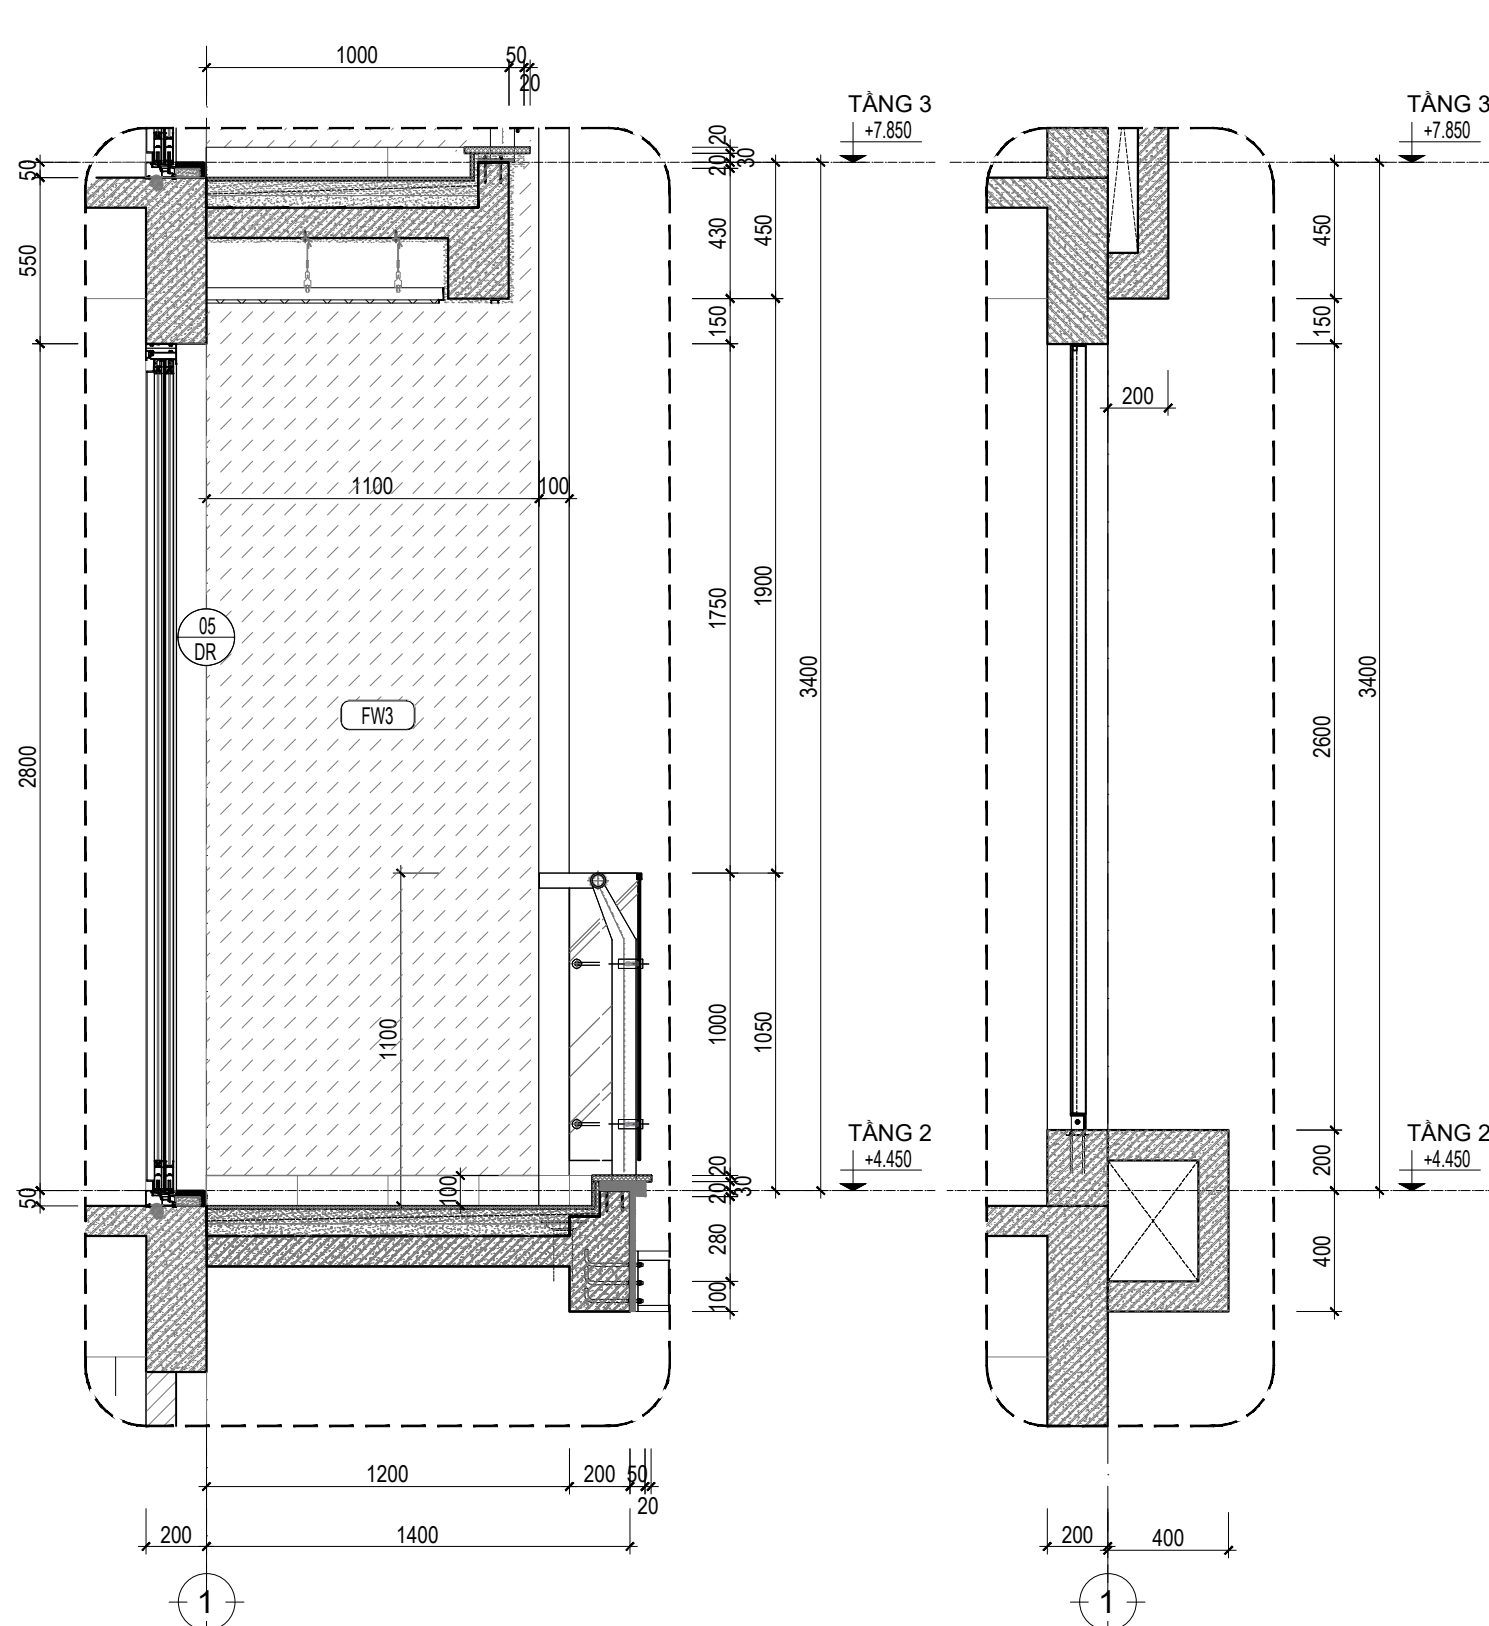


M. CẮT TRÍCH ĐOẠN 1-1_TL:1/25

M. CẮT TRÍCH ĐOẠN 2-2_TL:1/2

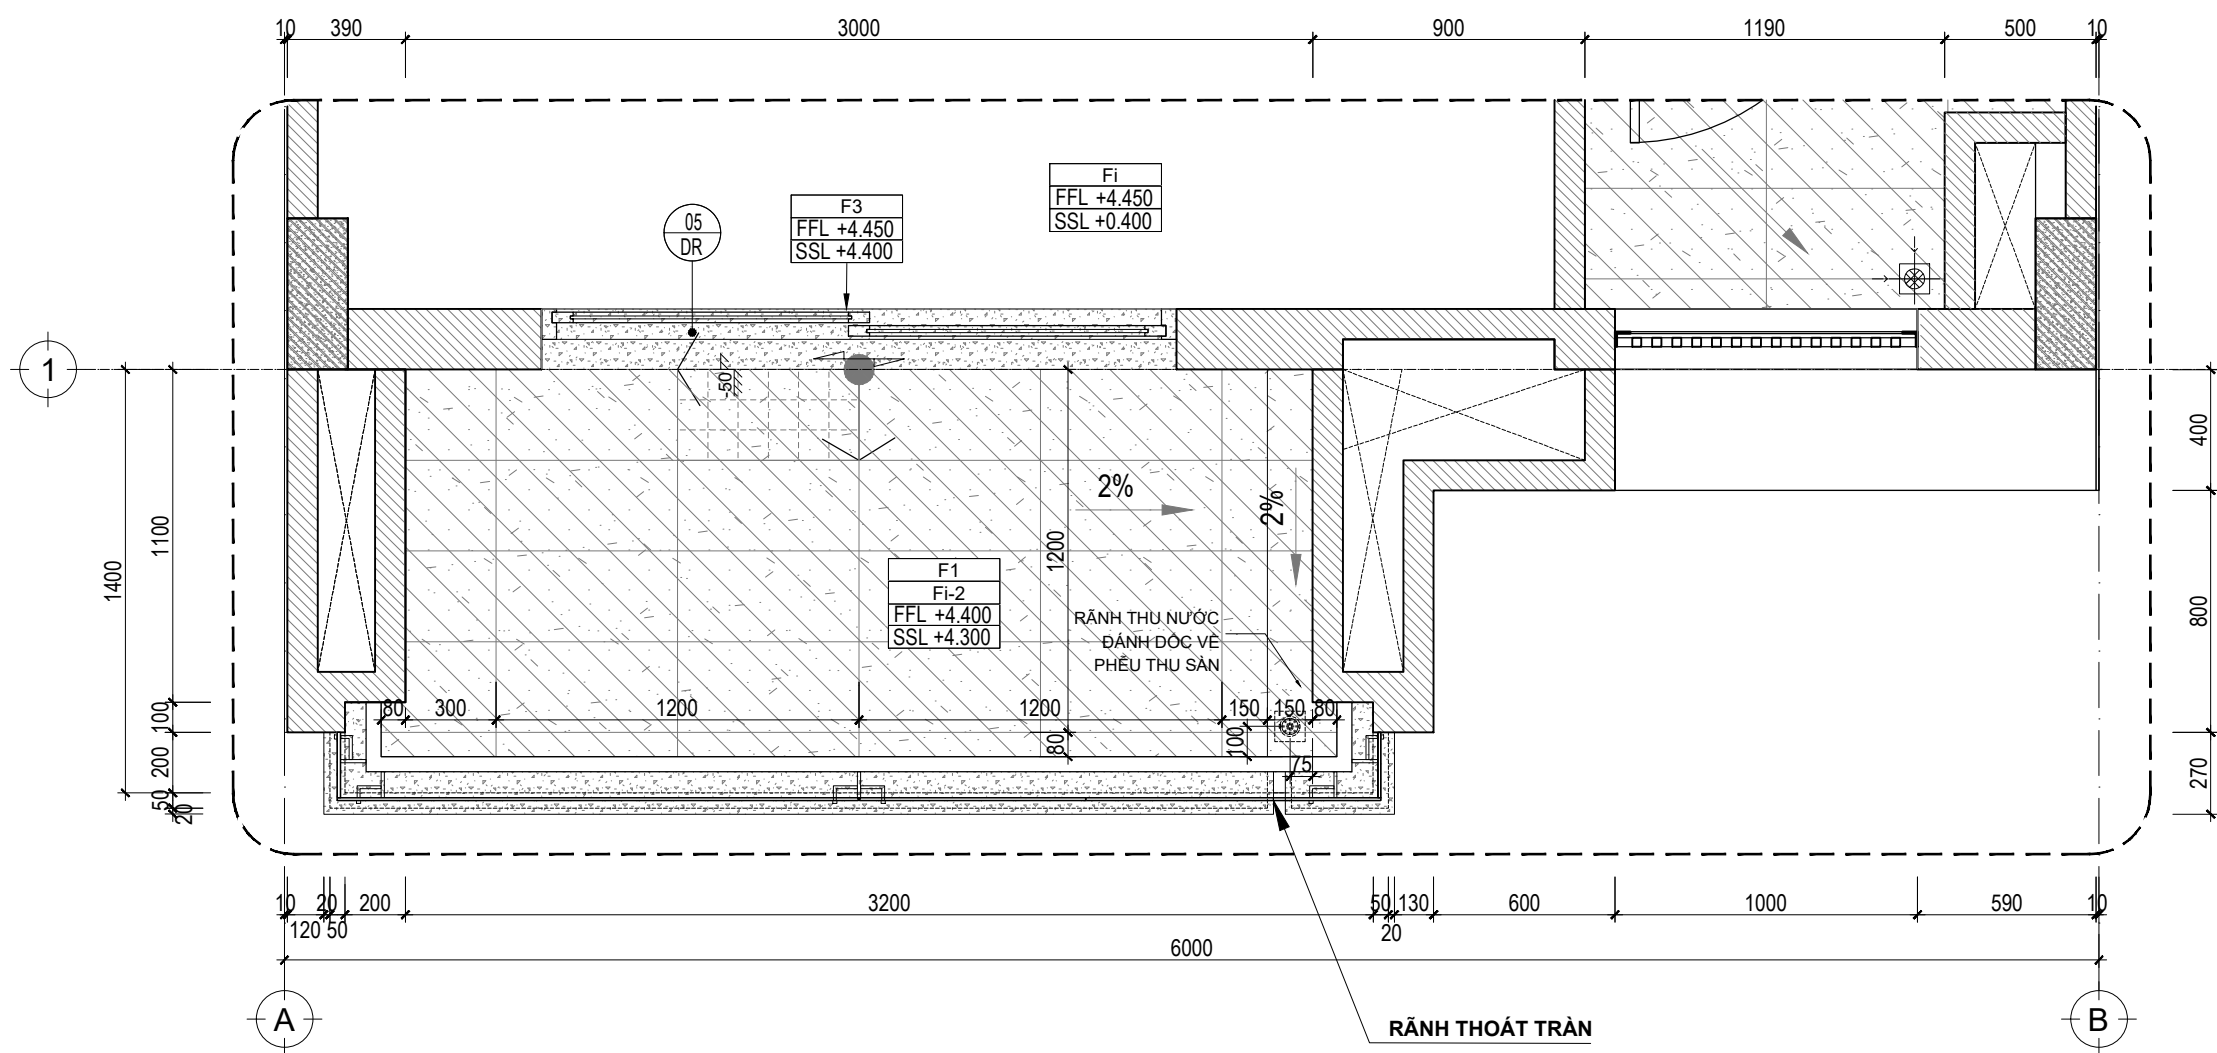


MẶT BẰNG TRÍCH ĐOẠN A-B - TẦNG 2_TL:1/25

VẬT LIỆU HOÀN THIỆN TƯỜNG		
KÝ HIỆU	MÔ TẢ	
FW1	TƯỜNG HOÀN THIỆN SƠN NƯỚC MÀU TRẮNG - RAL 9003	
FW2	TƯỜNG HOÀN THIỆN SƠN NƯỚC MÀU XÁM ĐẬM - RAL 7022	
FW3	TƯỜNG HOÀN THIỆN SƠN NƯỚC MÀU HỒNG NÂU - RAL 4009	
FW4	TƯỜNG HOÀN THIỆN SƠN NƯỚC MÀU VÀNG NHẠT - RAL 1015	
FW5	TƯỜNG HOÀN THIỆN SƠN NƯỚC MÀU XÁM - RAL 7042	
L1	LEN CHÂN TƯỜNG GẠCH PORCELAIN 300X600mm,CHỐNG THẤM TỐI MÀU	

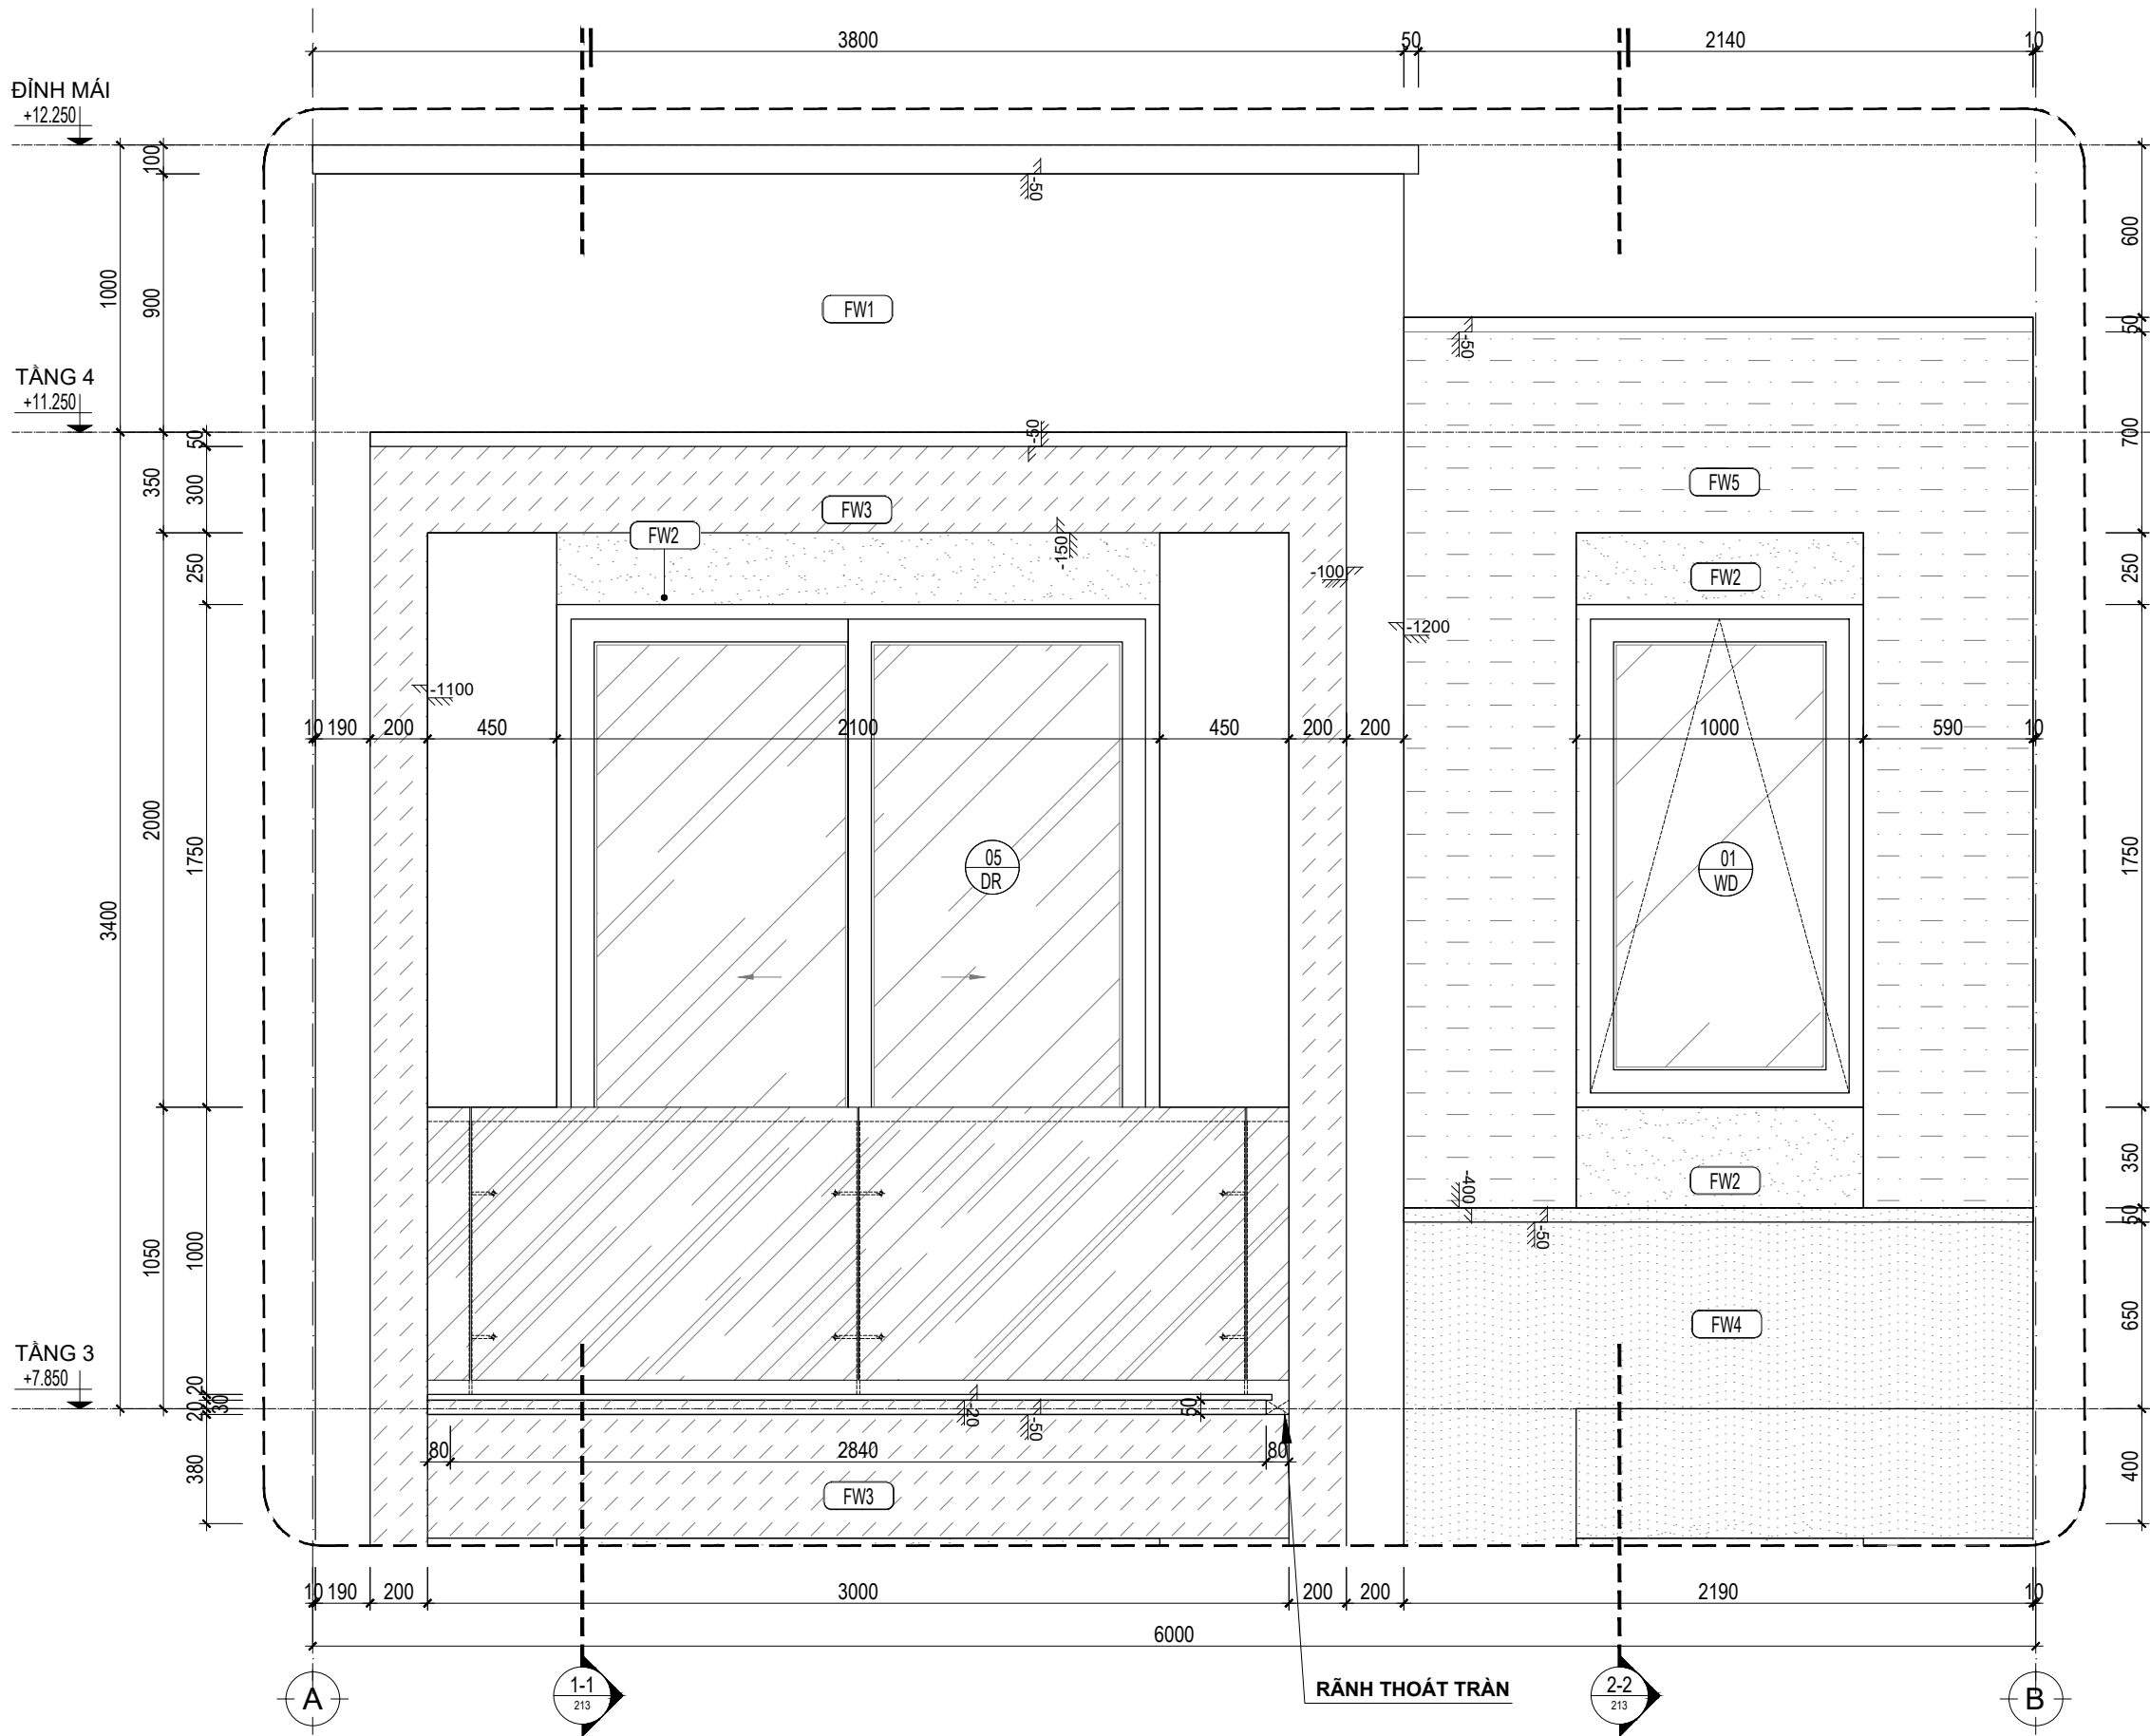


MẶT ĐỨNG TRÍCH ĐOẠN A-B - TẦNG 3_TL:1/25

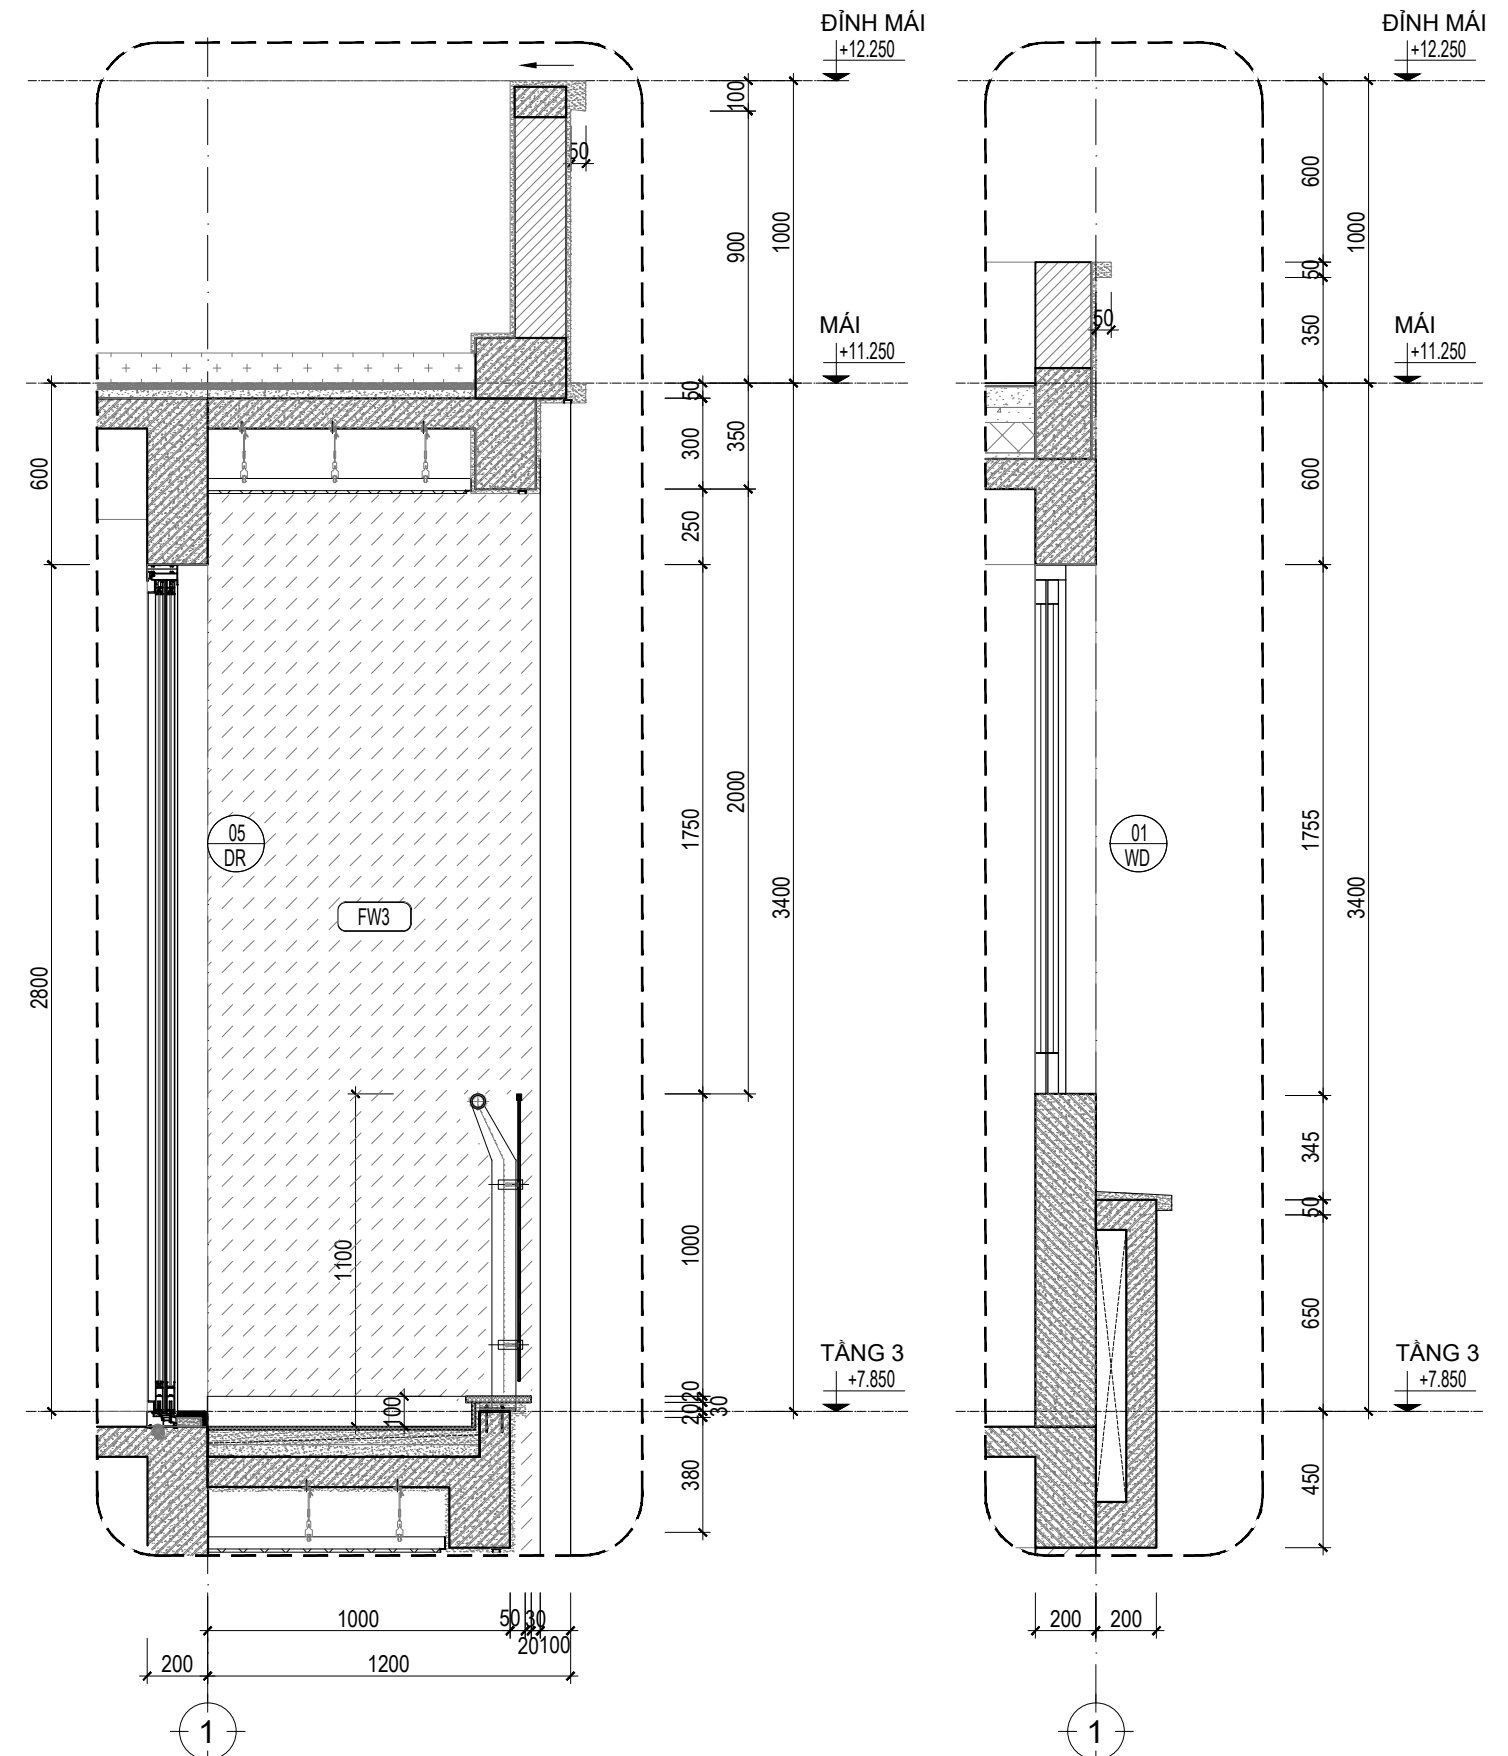


M. CẮT TRÍCH ĐOẠN 1-1_TL:1/25

M. CẮT TRÍCH ĐOẠN 2-2_TL:1/25

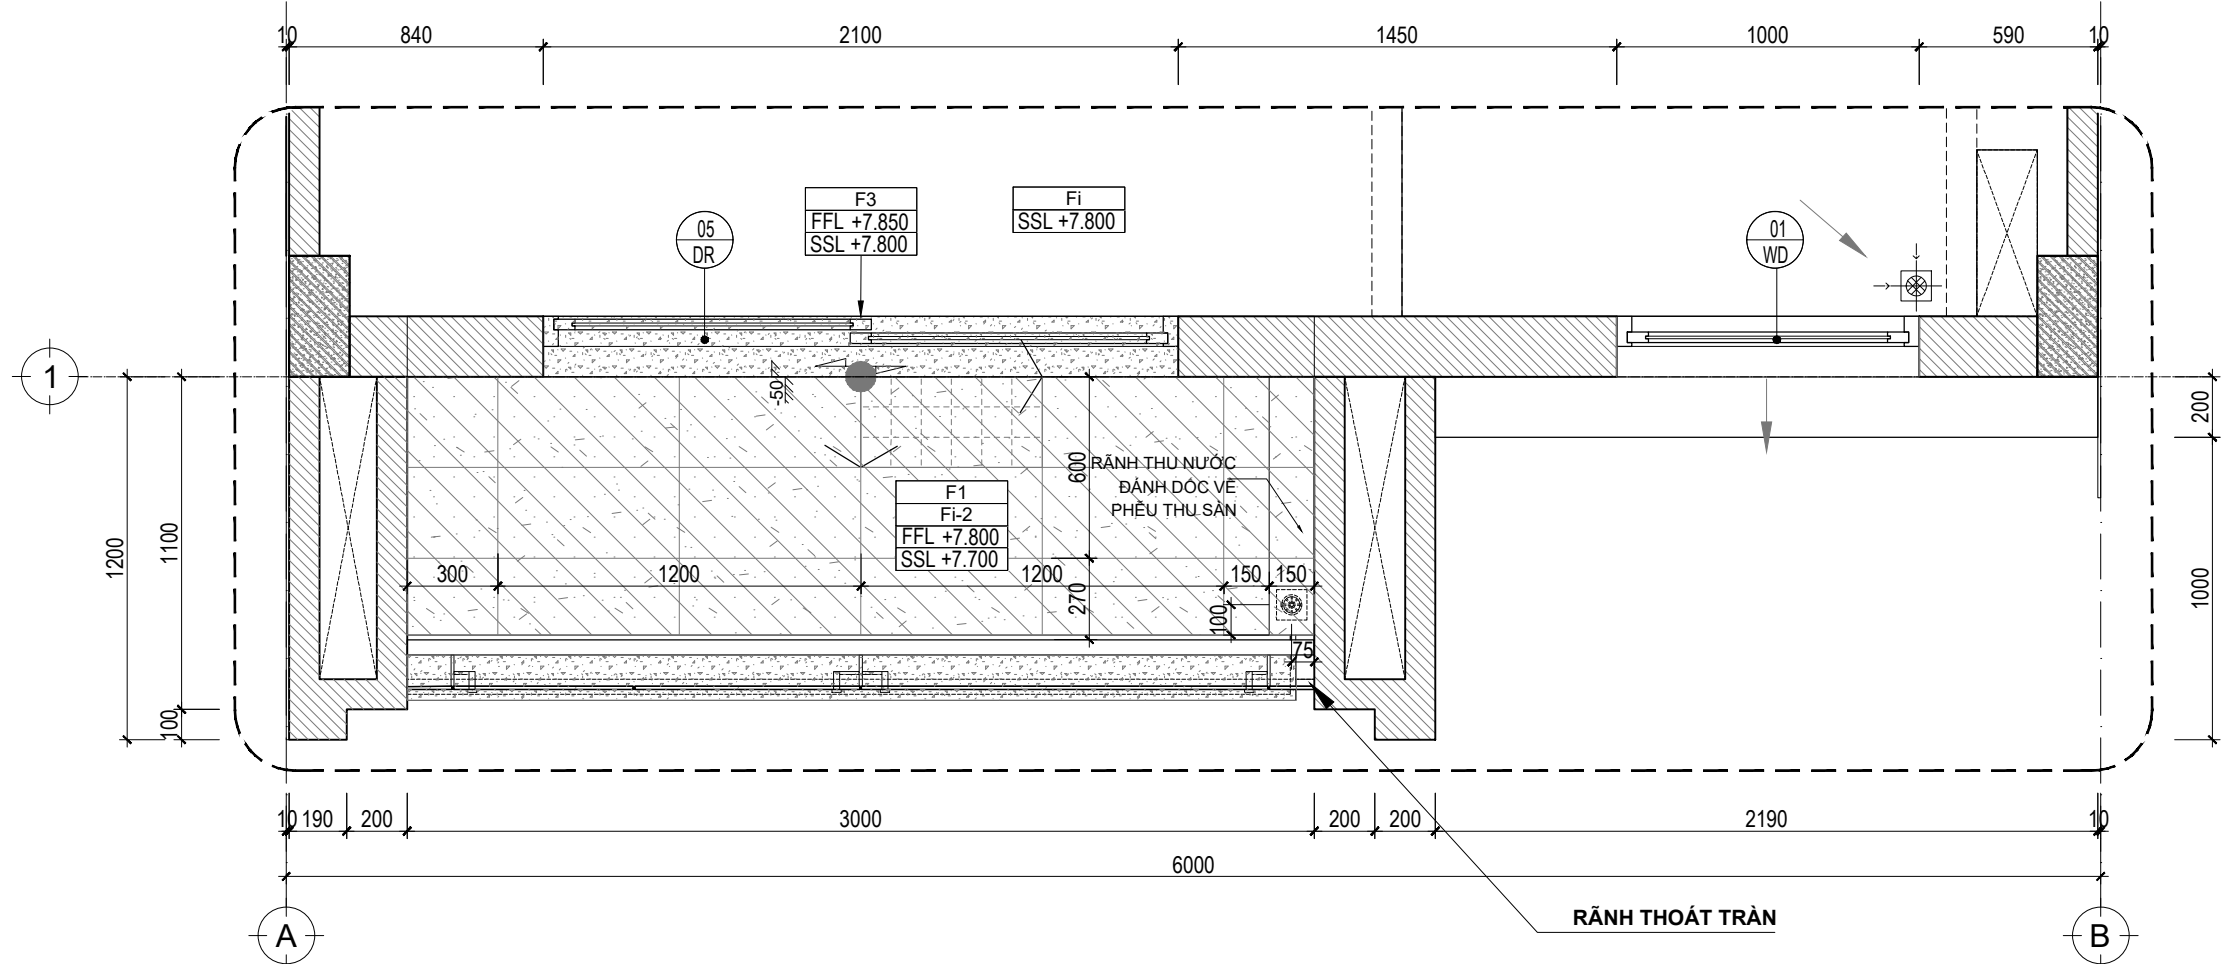


MẶT BẰNG TRÍCH ĐOẠN A-B - TẦNG 3_TL:1/25


VẬT LIỆU HOÀN THIỆN TƯỜNG		
KÝ HIỆU	MÔ TẢ	
FW1	TƯỜNG HOÀN THIỆN SƠN NƯỚC MÀU TRẮNG - RAL 9003	
FW2	TƯỜNG HOÀN THIỆN SƠN NƯỚC MÀU XÁM ĐẬM - RAL 7022	
FW3	TƯỜNG HOÀN THIỆN SƠN NƯỚC MÀU HỒNG NÂU - RAL 4009	
FW4	TƯỜNG HOÀN THIỆN SƠN NƯỚC MÀU VÀNG NHẠT - RAL 1015	
FW5	TƯỜNG HOÀN THIỆN SƠN NƯỚC MÀU XÁM - RAL 7042	
L1	LEN CHÂN TƯỜNG GẠCH PORCELAIN 300X600mm,CHỐNG THẤM TỐI MÀU	

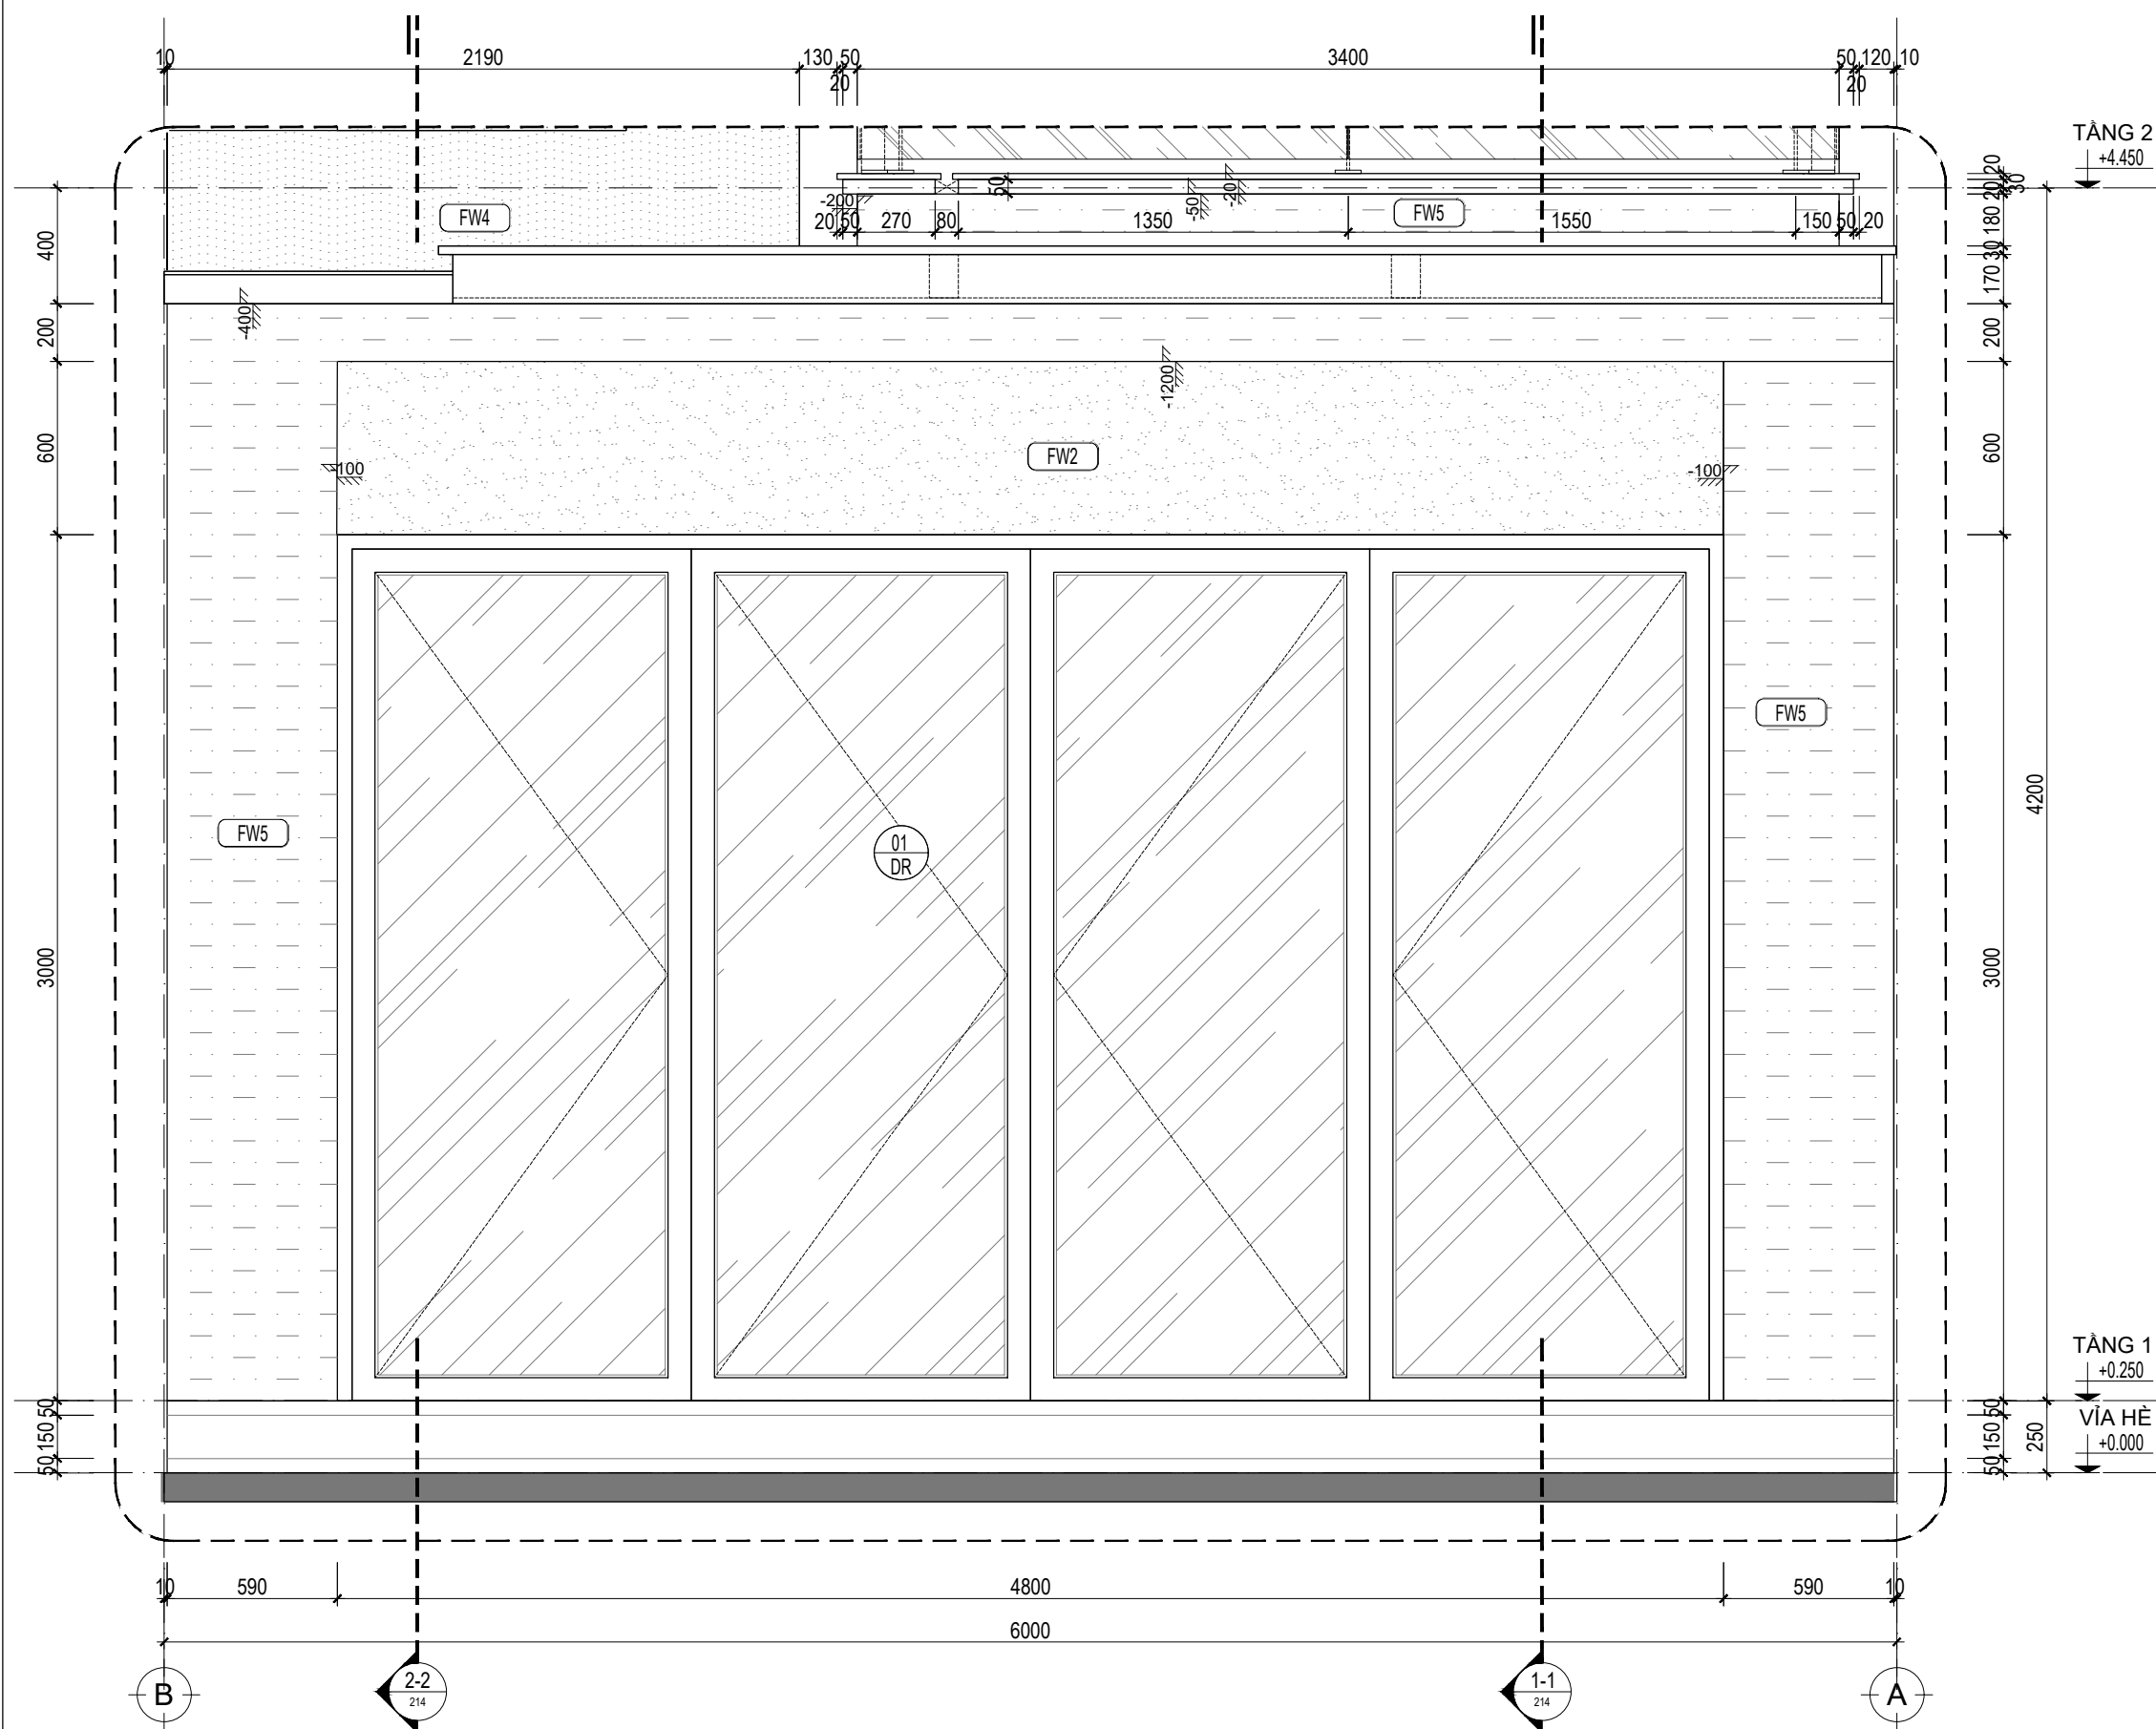

MẶT ĐƯNG TRÍCH ĐOẠN B-A - TẦNG 1_TL:1/25

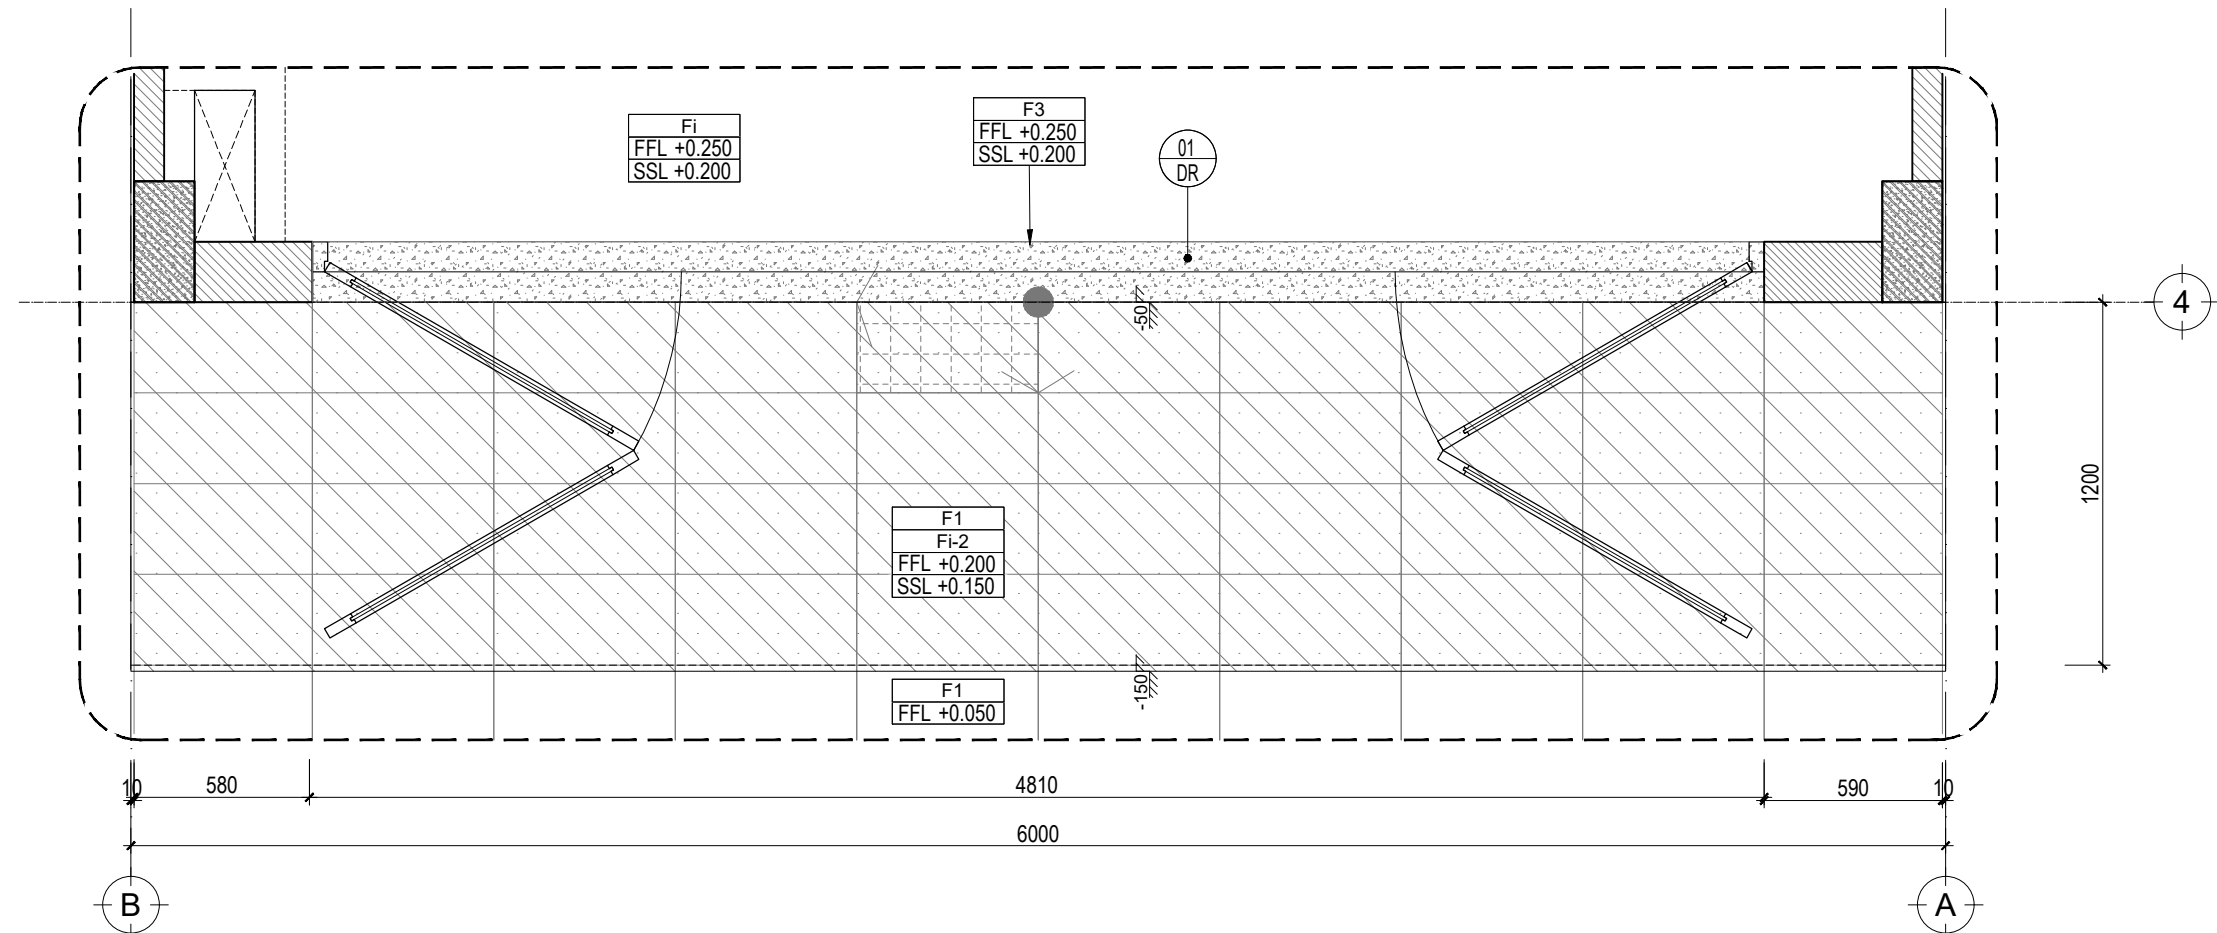





MẶT BẰNG TRÍCH ĐOẠN B-A - TẦNG 1_TL:1/25

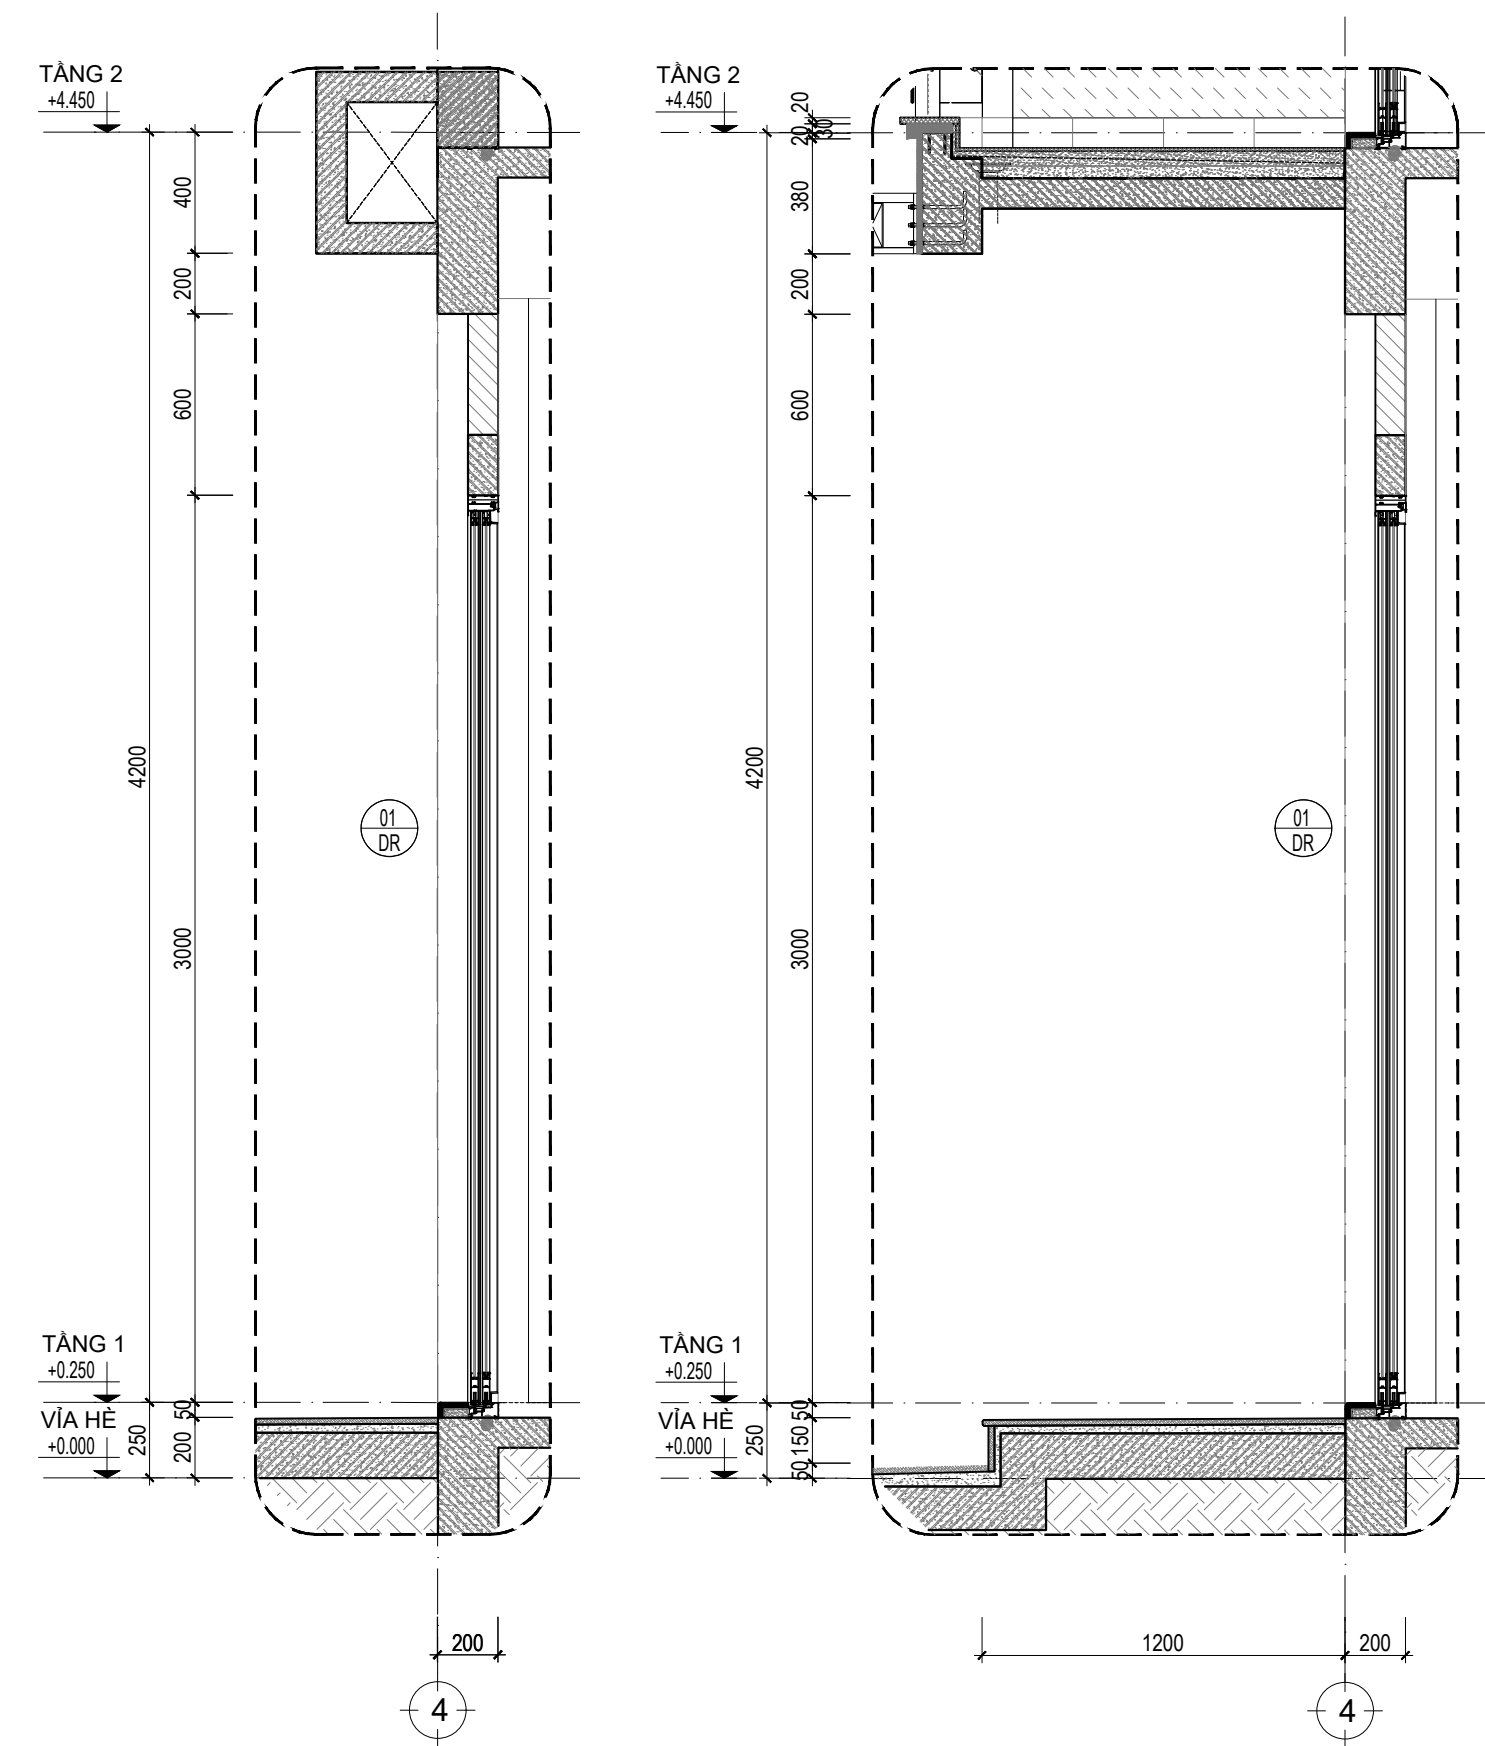


M. CẮT TRÍCH ĐOẠN 2-2_TL:1/25

M. CẮT TRÍCH ĐOẠN 1-1_TL:1/25


VẬT LIỆU HOÀN THIỆN TƯỜNG		
KÝ HIỆU	MÔ TẢ	
FW1	TƯỜNG HOÀN THIỆN SƠN NƯỚC MÀU TRẮNG - RAL 9003	
FW2	TƯỜNG HOÀN THIỆN SƠN NƯỚC MÀU XÁM ĐẬM - RAL 7022	
FW3	TƯỜNG HOÀN THIỆN SƠN NƯỚC MÀU HỒNG NÂU - RAL 4009	
FW4	TƯỜNG HOÀN THIỆN SƠN NƯỚC MÀU VÀNG NHẠT - RAL 1015	
FW5	TƯỜNG HOÀN THIỆN SƠN NƯỚC MÀU XÁM - RAL 7042	
L1	LEN CHÂN TƯỜNG GẠCH PORCELAIN 300X600mm,CHỐNG THẤM TỐI MÀU	

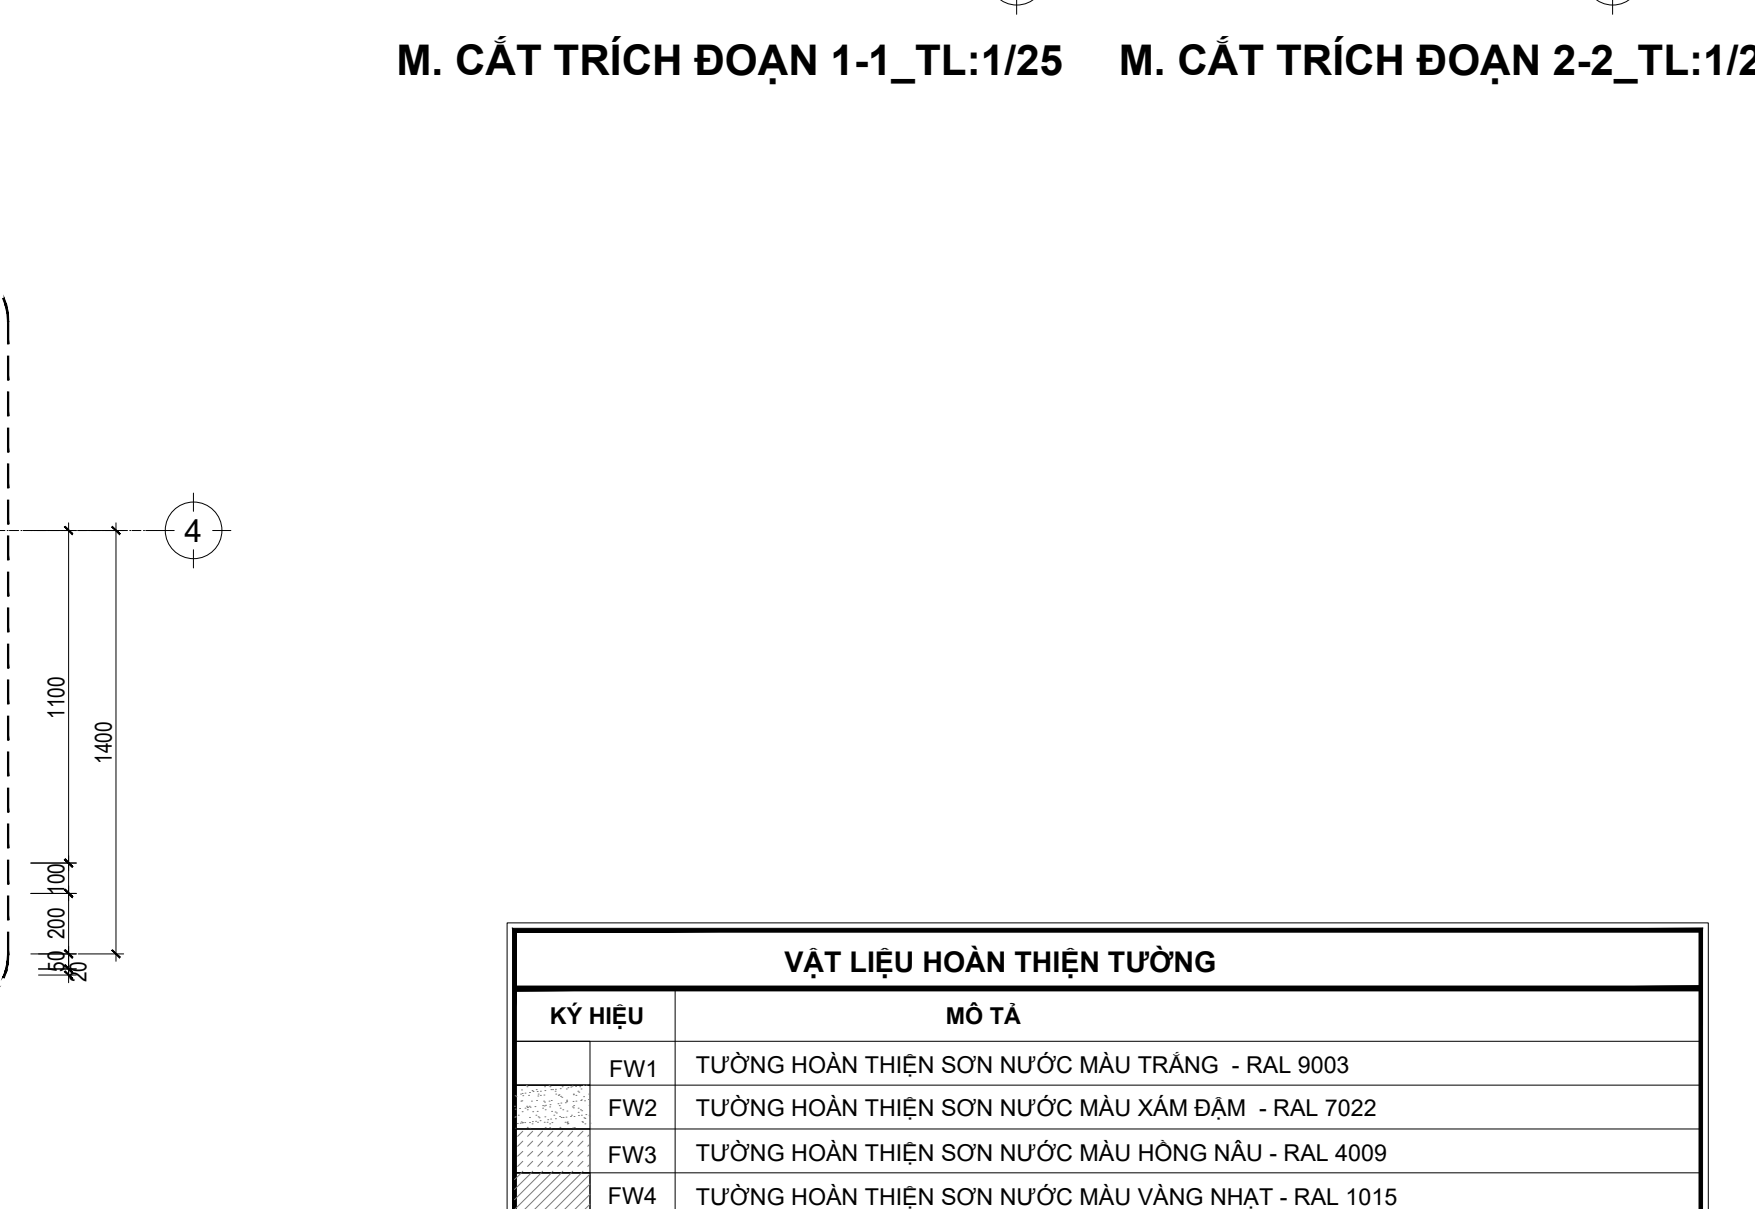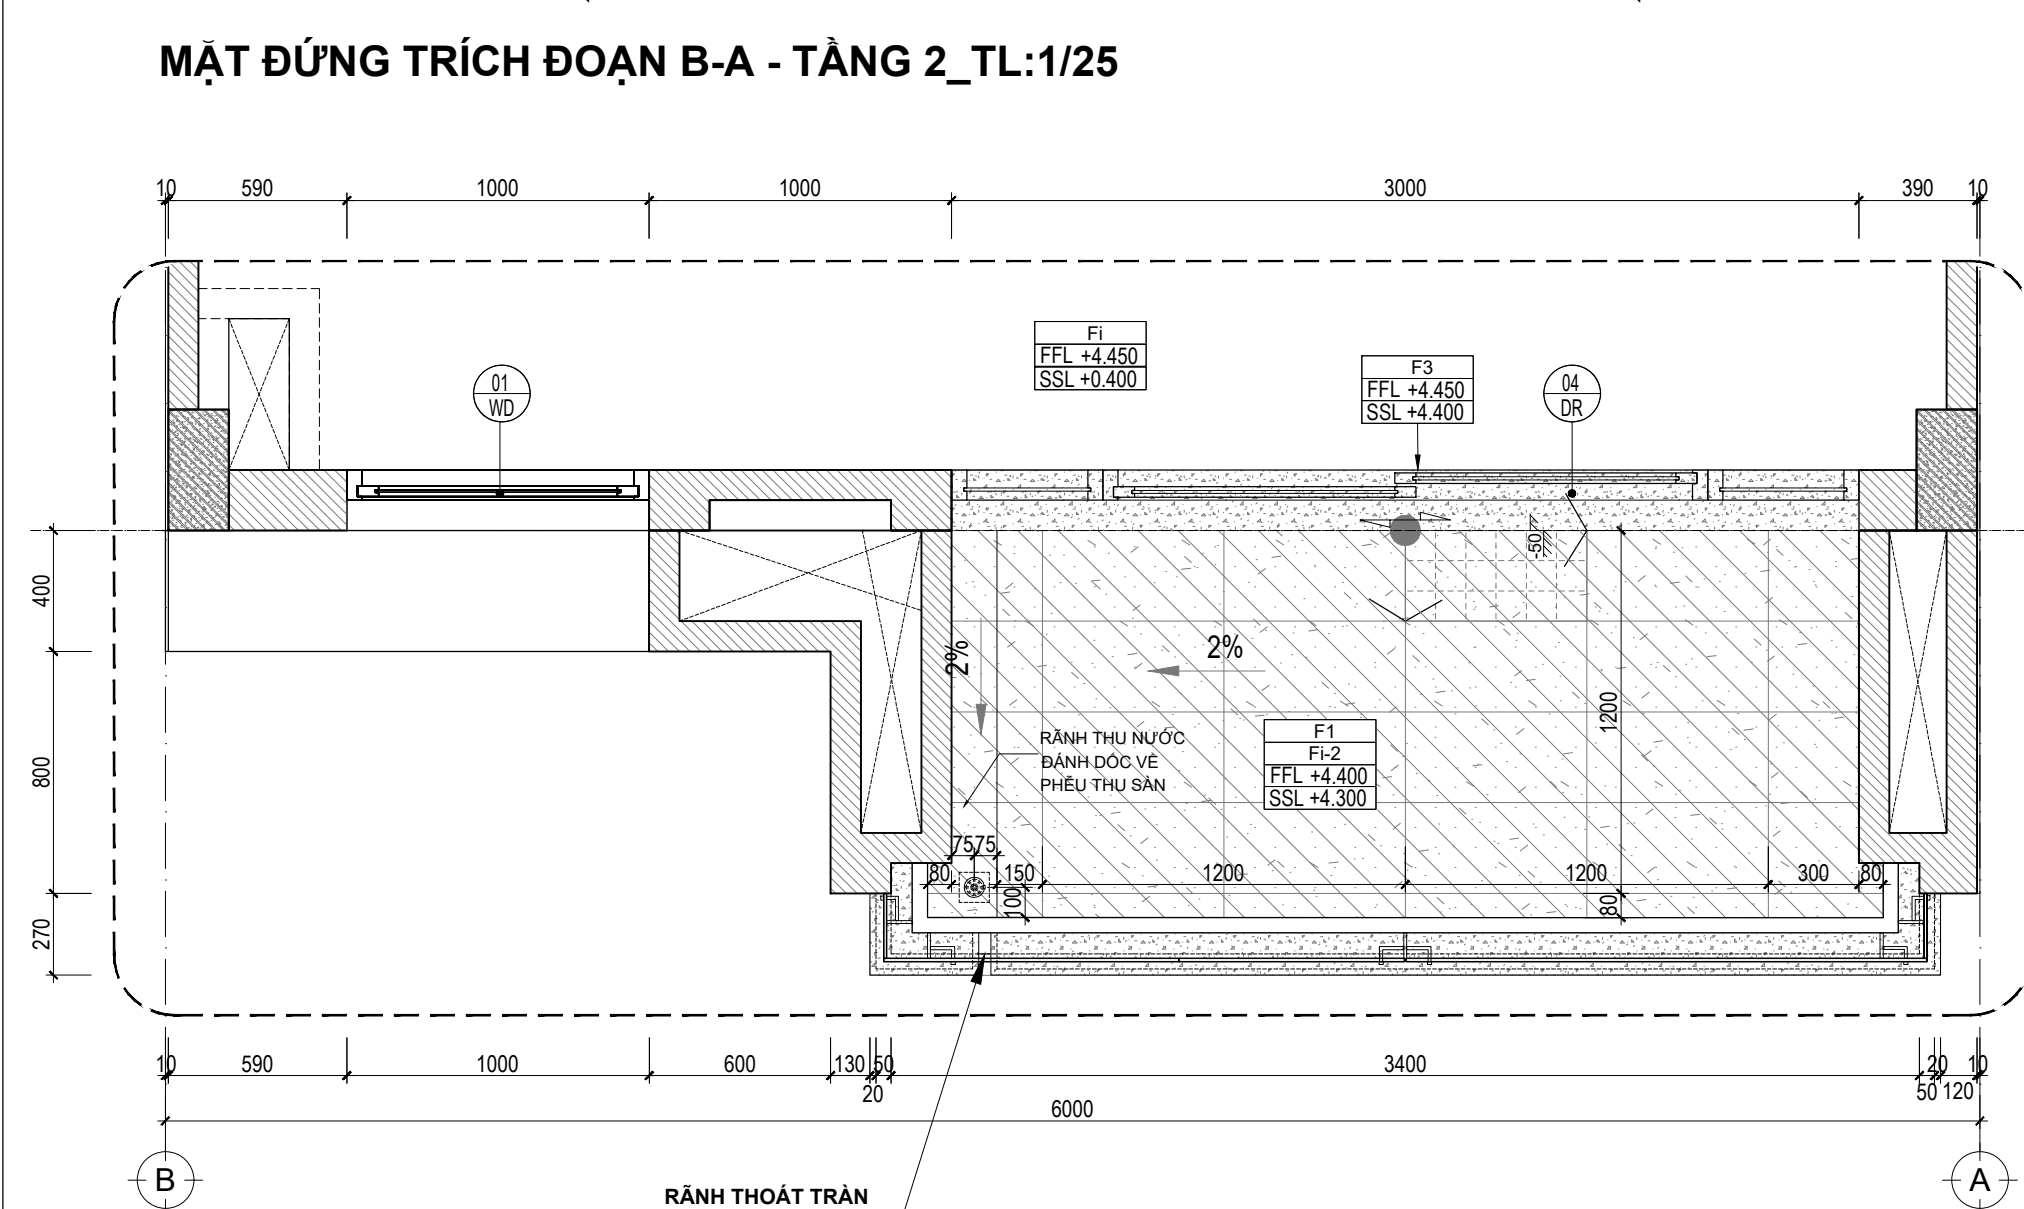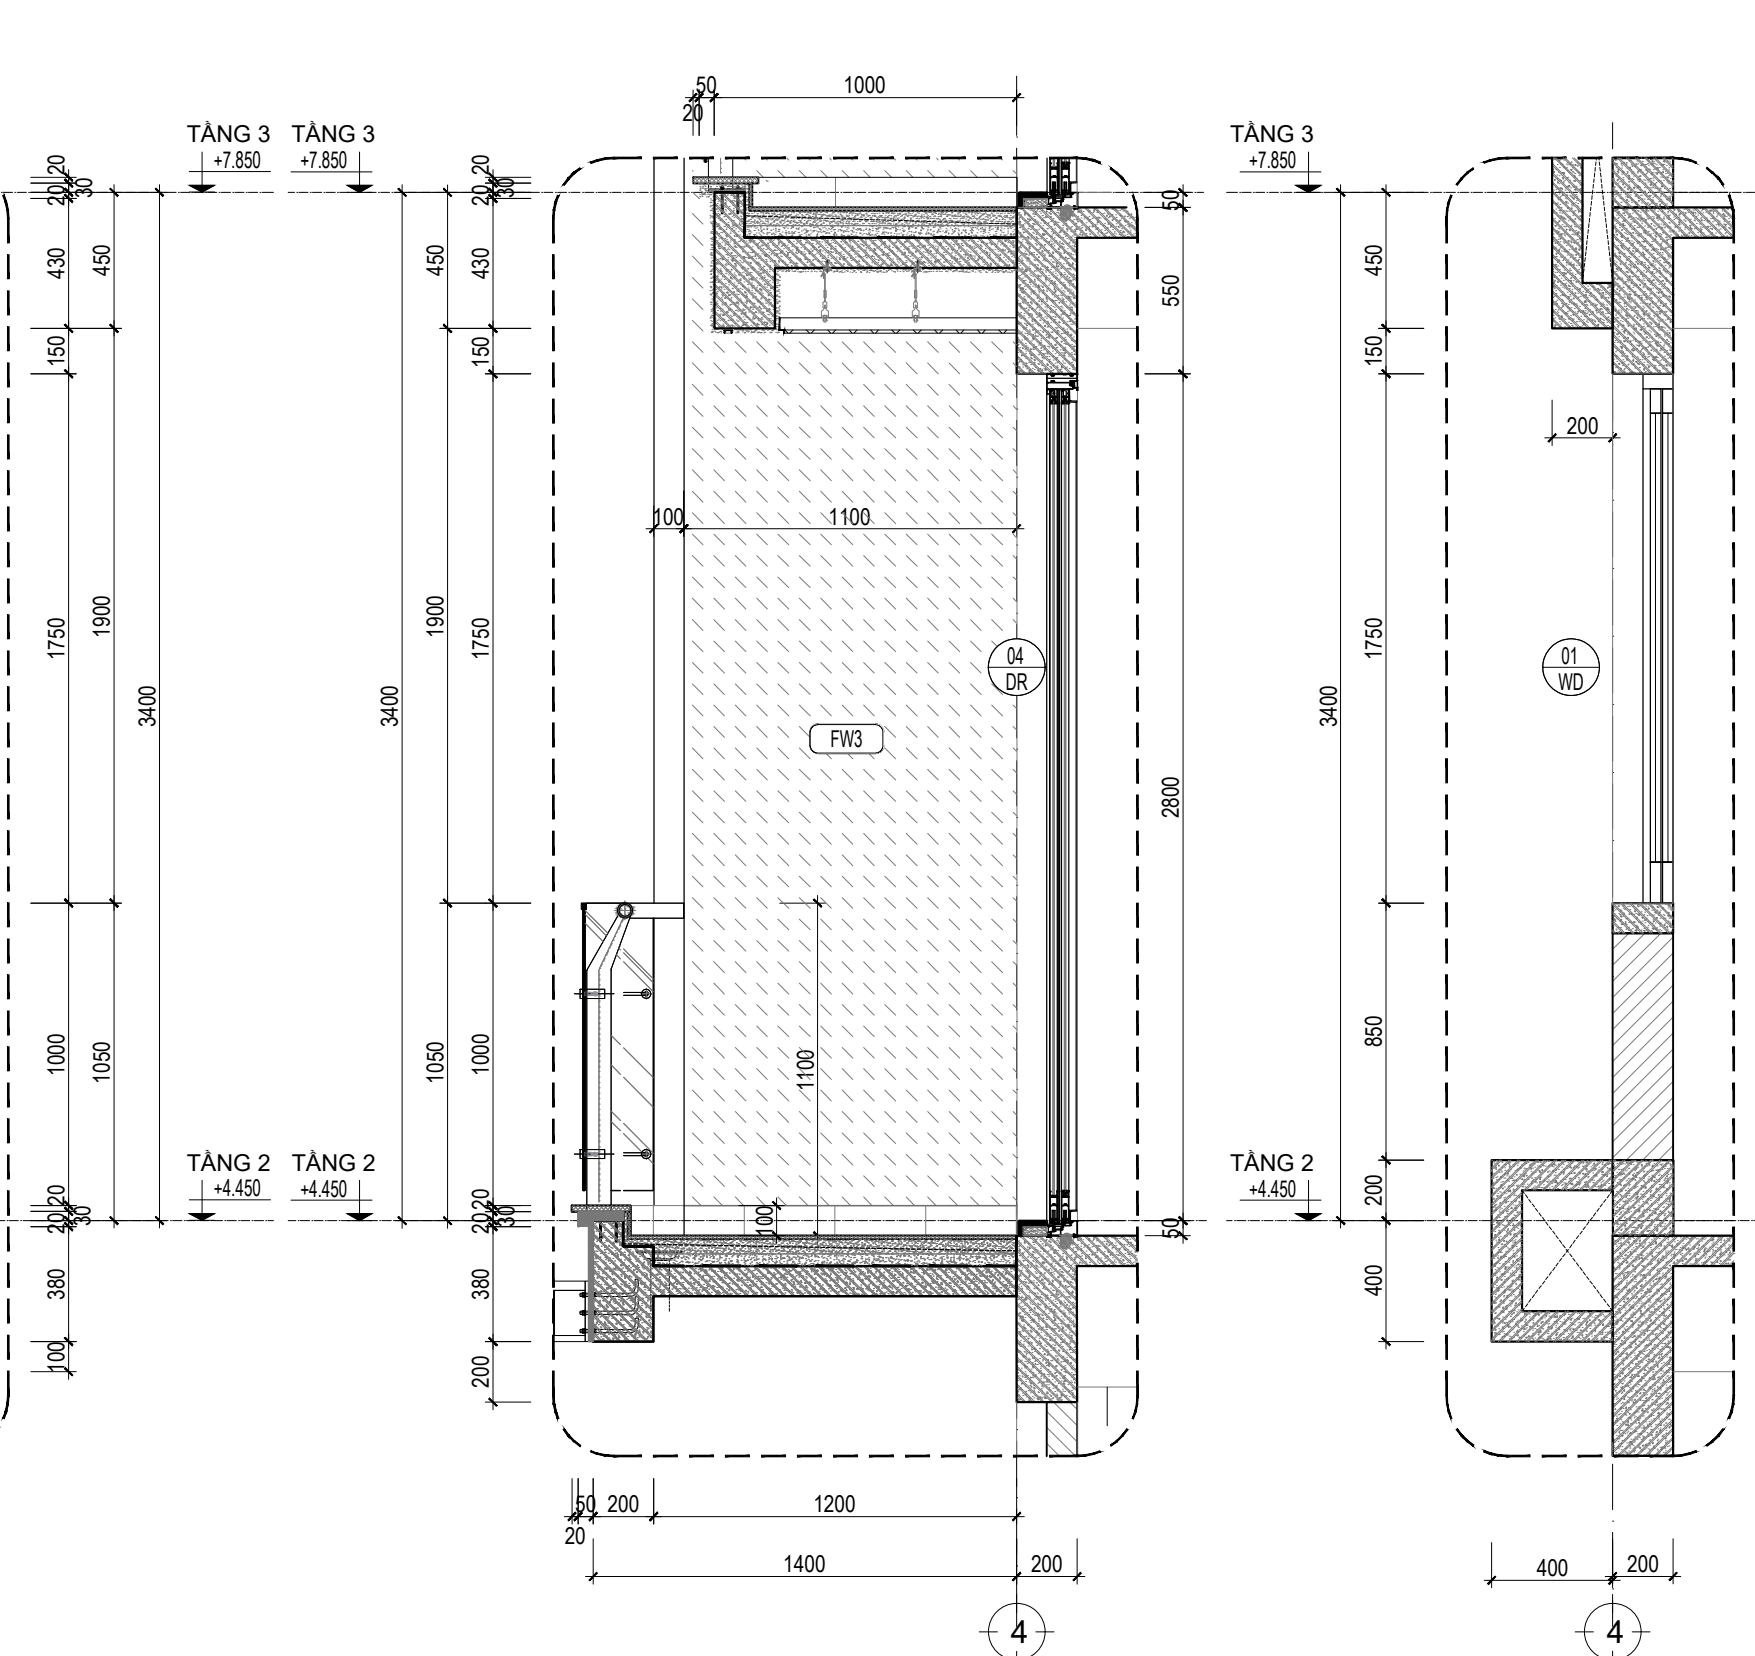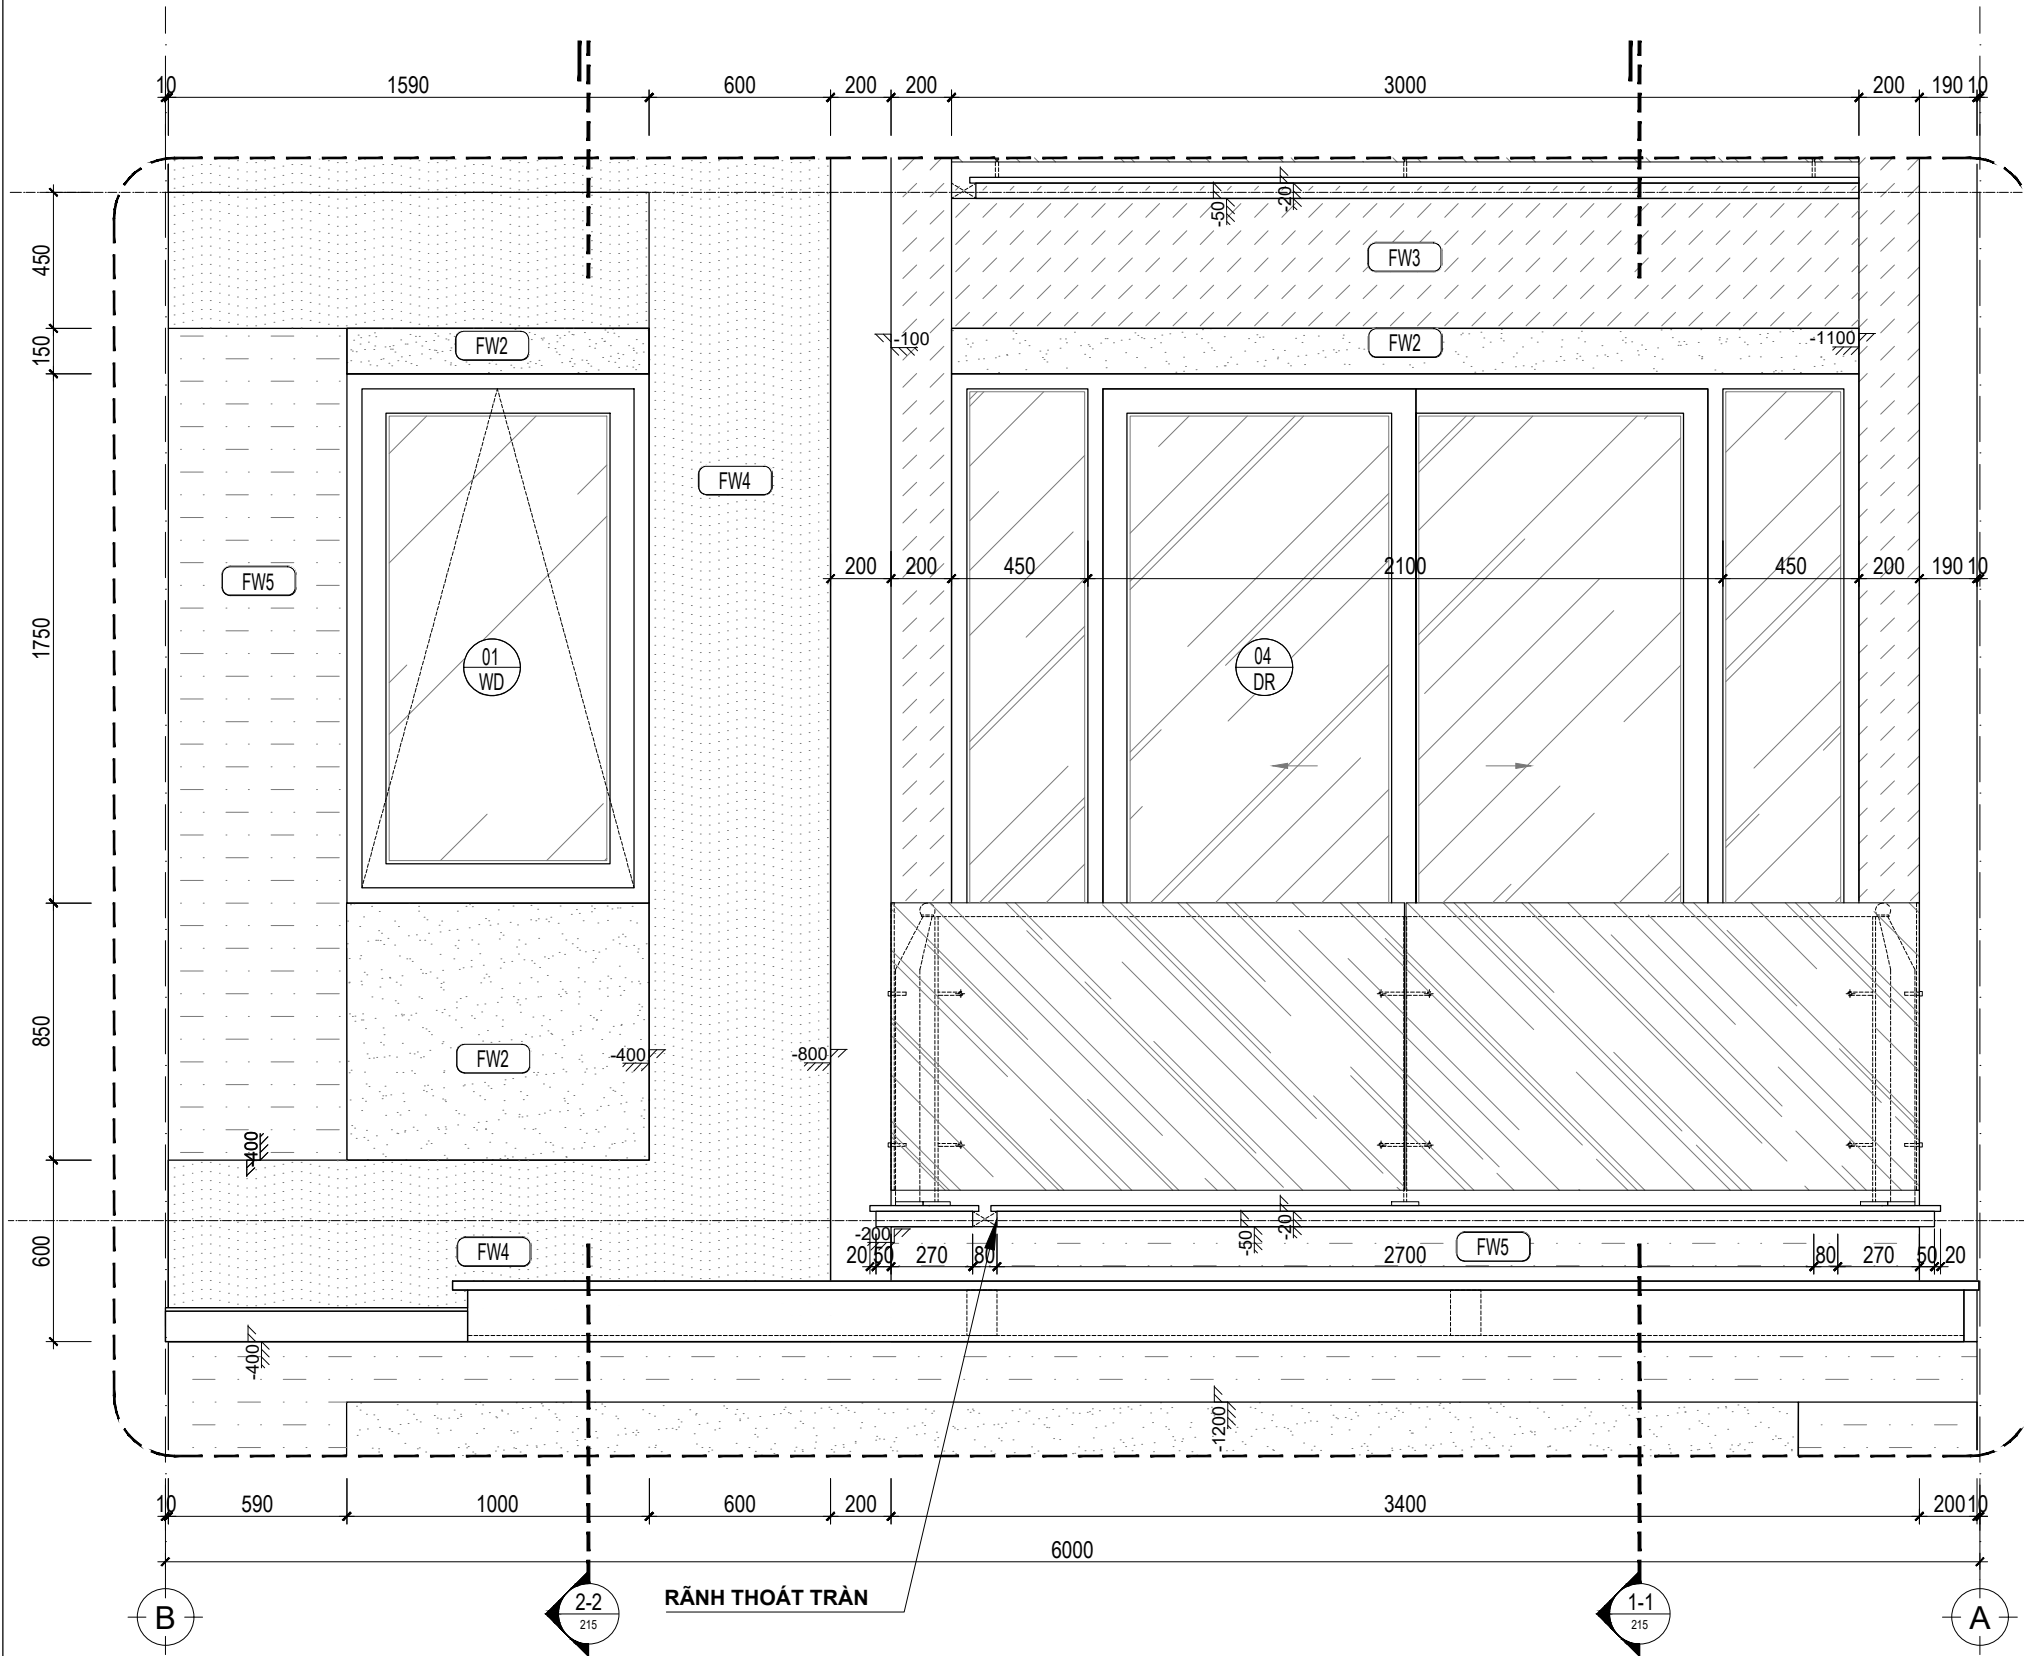


VẬT LIỆU HOÀN THIỆN TƯỜNG	
KÝ HIỆU	MÔ TẢ
FW1	TƯỜNG HOÀN THIỆN SƠN NƯỚC MÀU TRẮNG - RAL 9003
FW2	TƯỜNG HOÀN THIỆN SƠN NƯỚC MÀU XÁM ĐẬM - RAL 7022
FW3	TƯỜNG HOÀN THIỆN SƠN NƯỚC MÀU HỒNG NÂU - RAL 4009
FW4	TƯỜNG HOÀN THIỆN SƠN NƯỚC MÀU VÀNG NHẠT - RAL 1015
FW5	TƯỜNG HOÀN THIỆN SƠN NƯỚC MÀU XÁM - RAL 7042
L1	LEN CHÂN TƯỜNG GẠCH PORCELAIN 300X600mm, CHỐNG THÂM TÓI MÀU

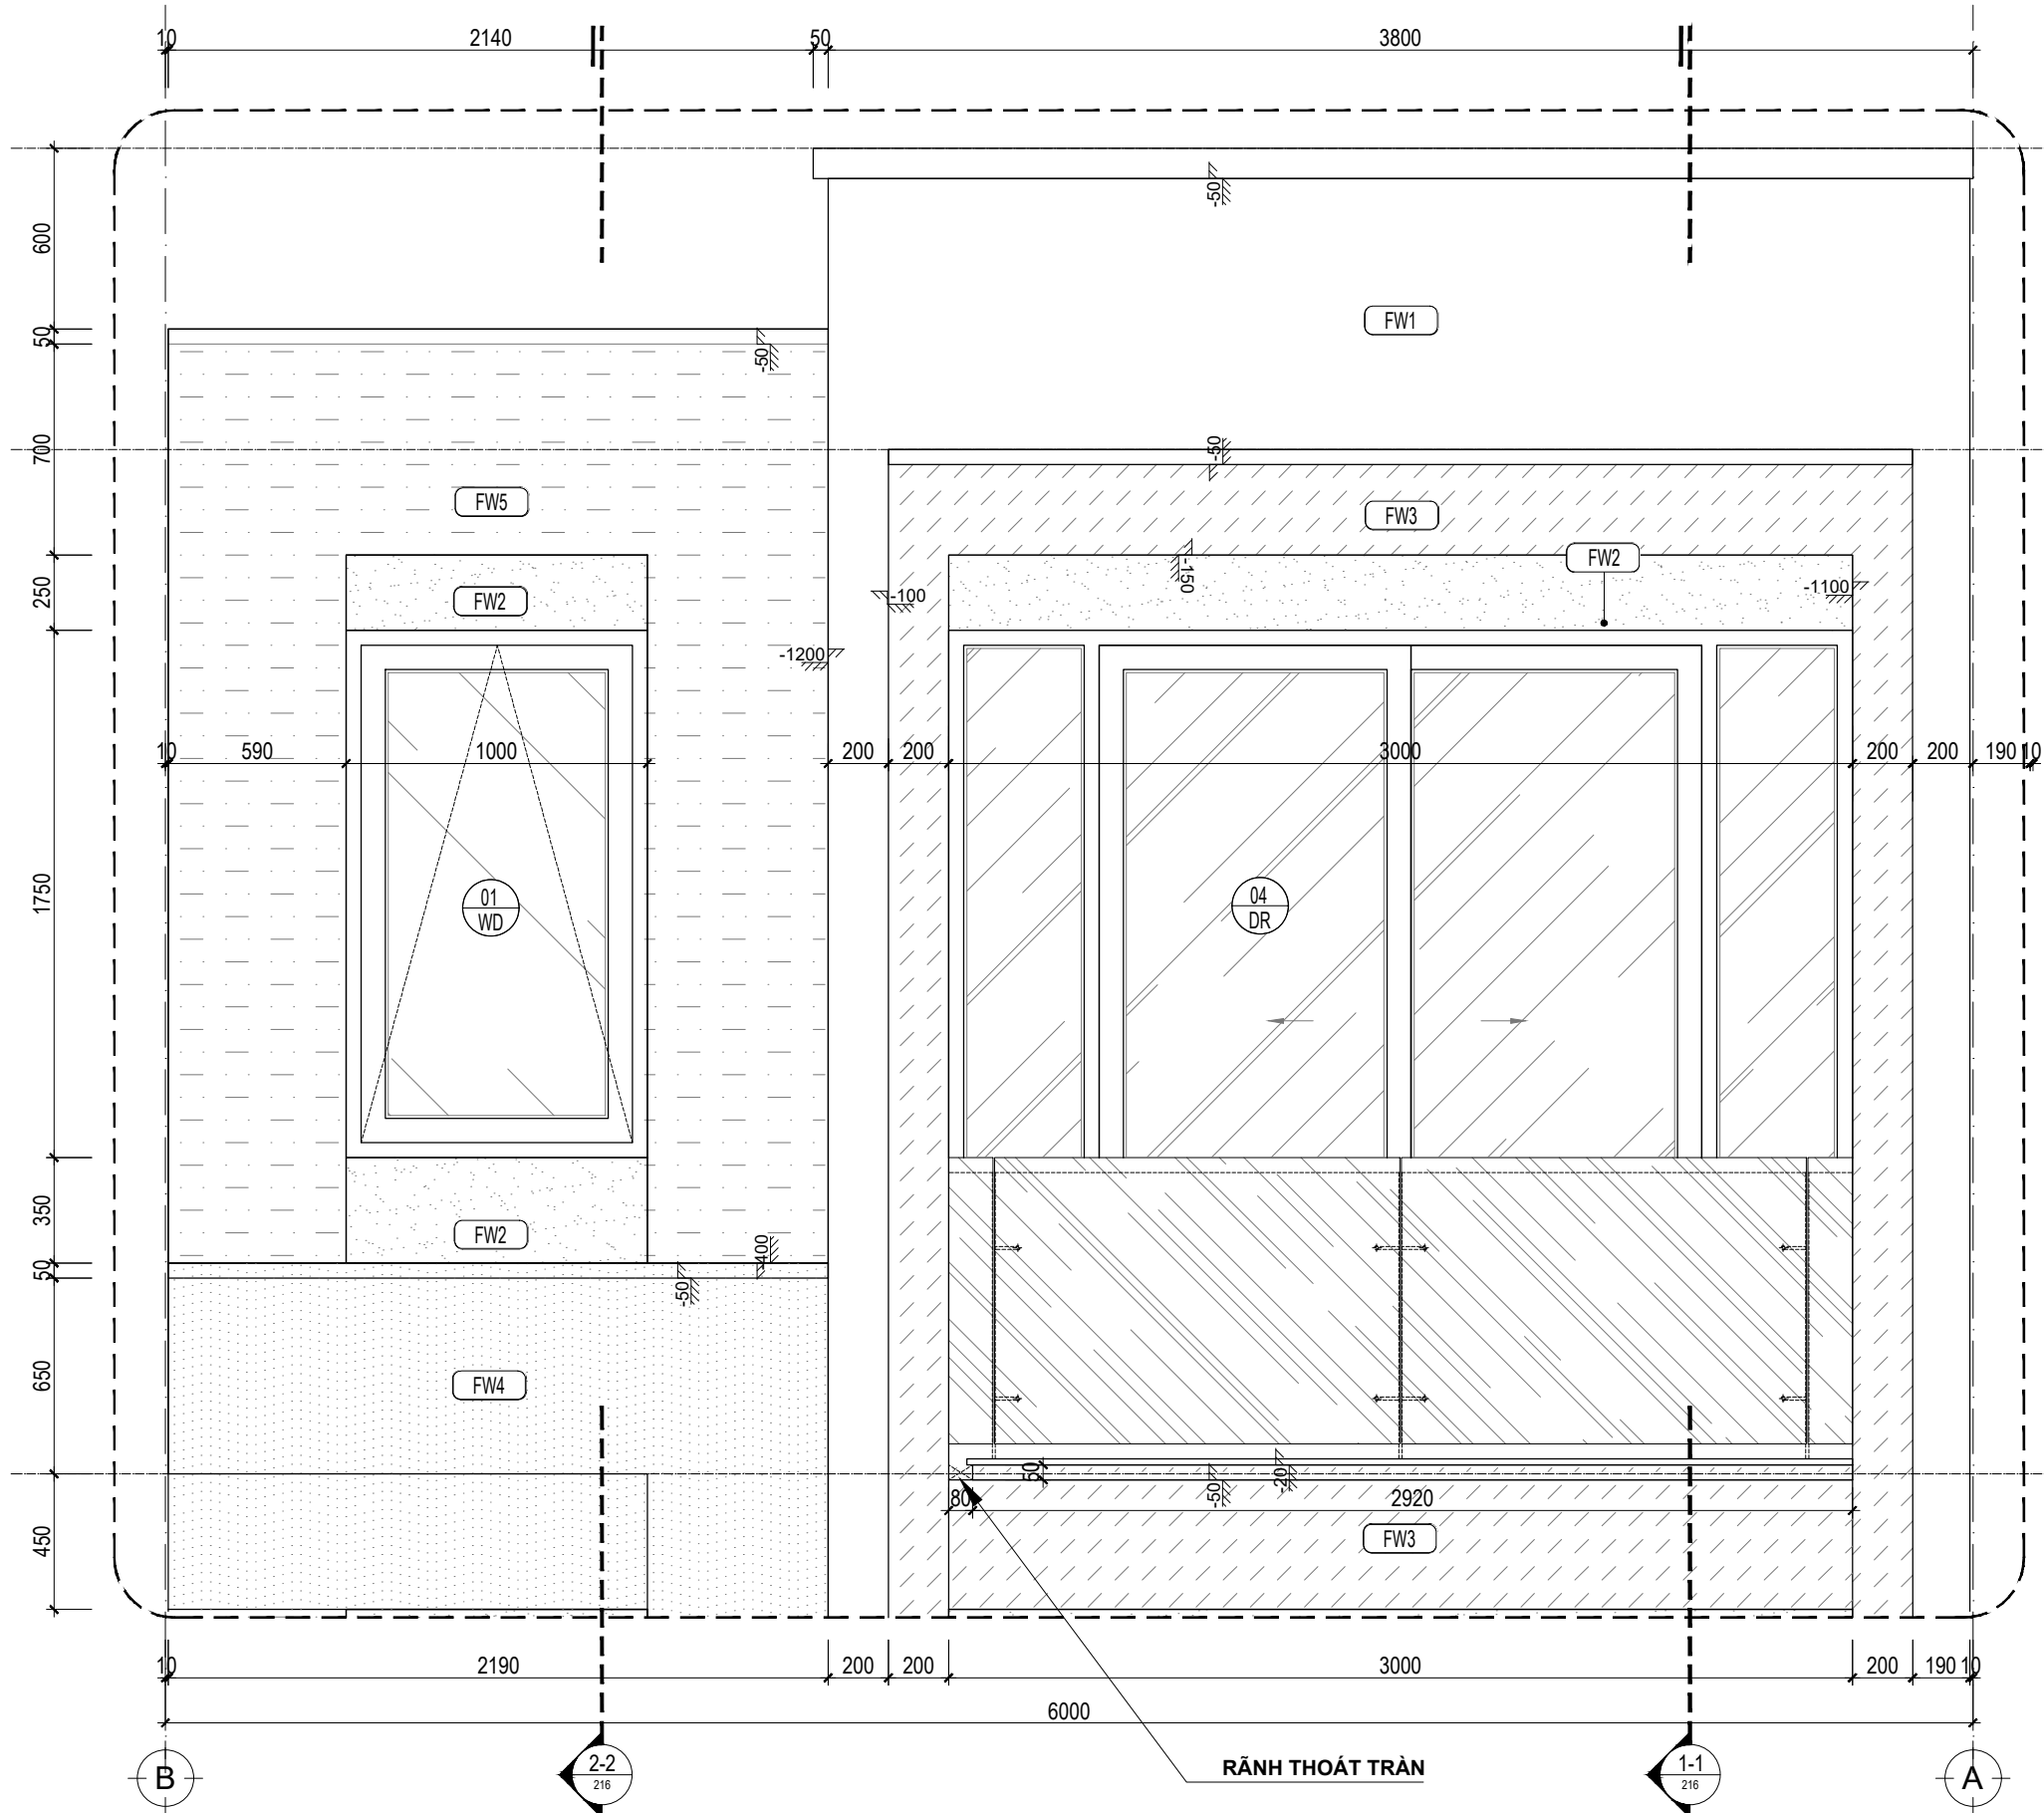

MẶT ĐỨNG TRÍCH ĐOẠN B-A - TẦNG 3_TL:1/25

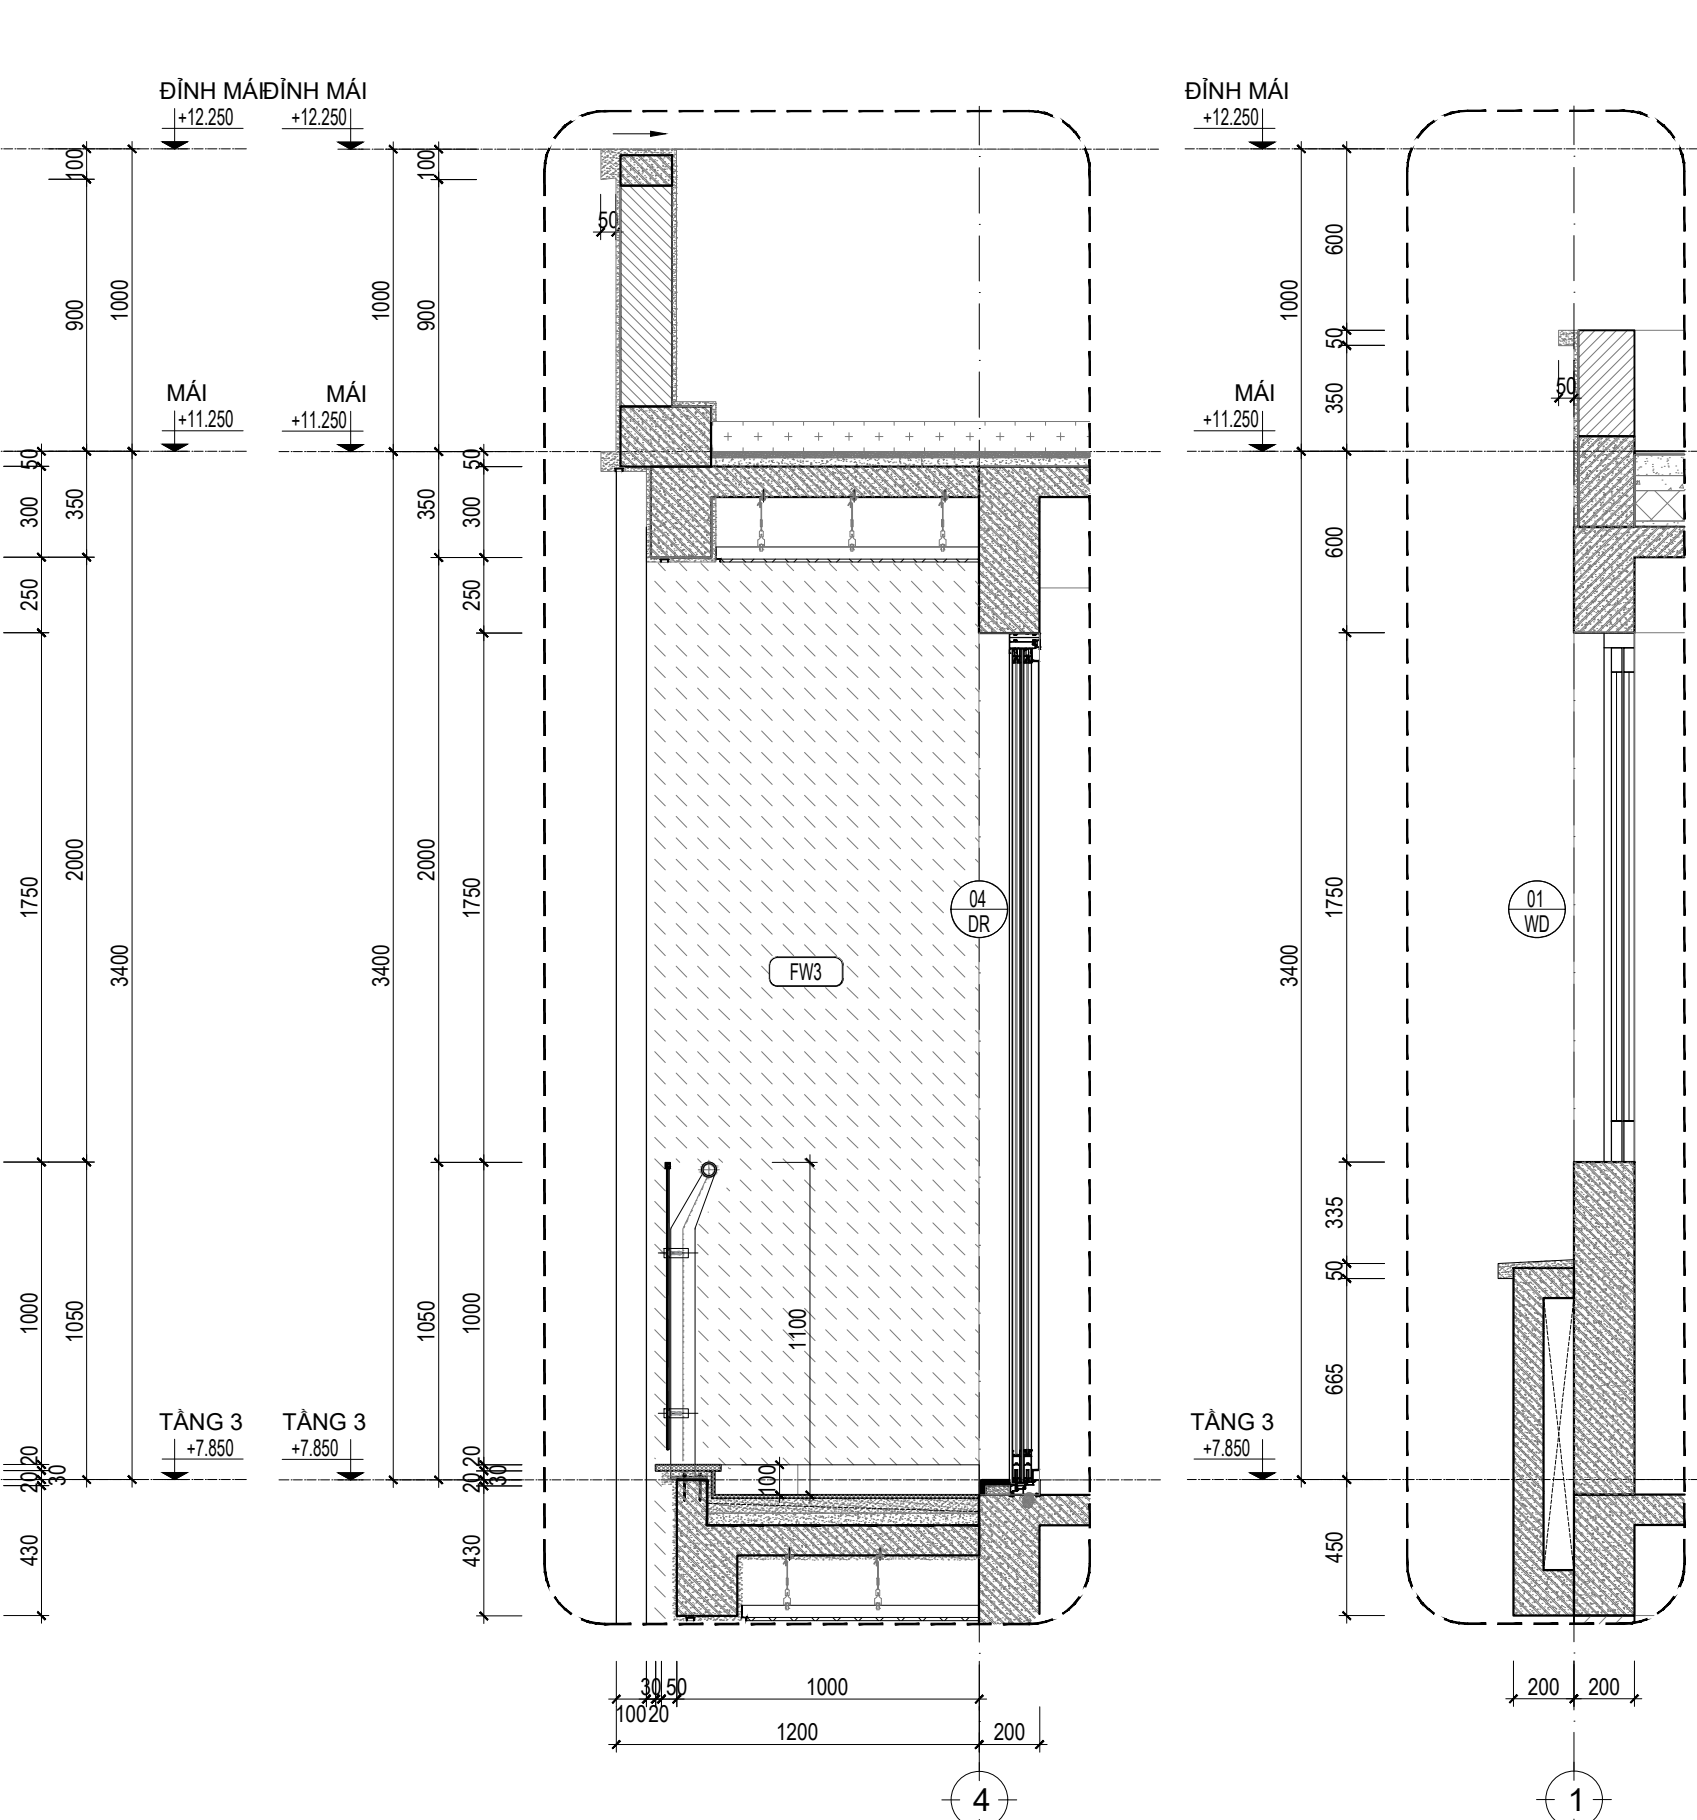


M. CẮT TRÍCH ĐOẠN 1-1_TL:1/25 M. CẮT TRÍCH ĐOẠN 2-2_TL:1/25

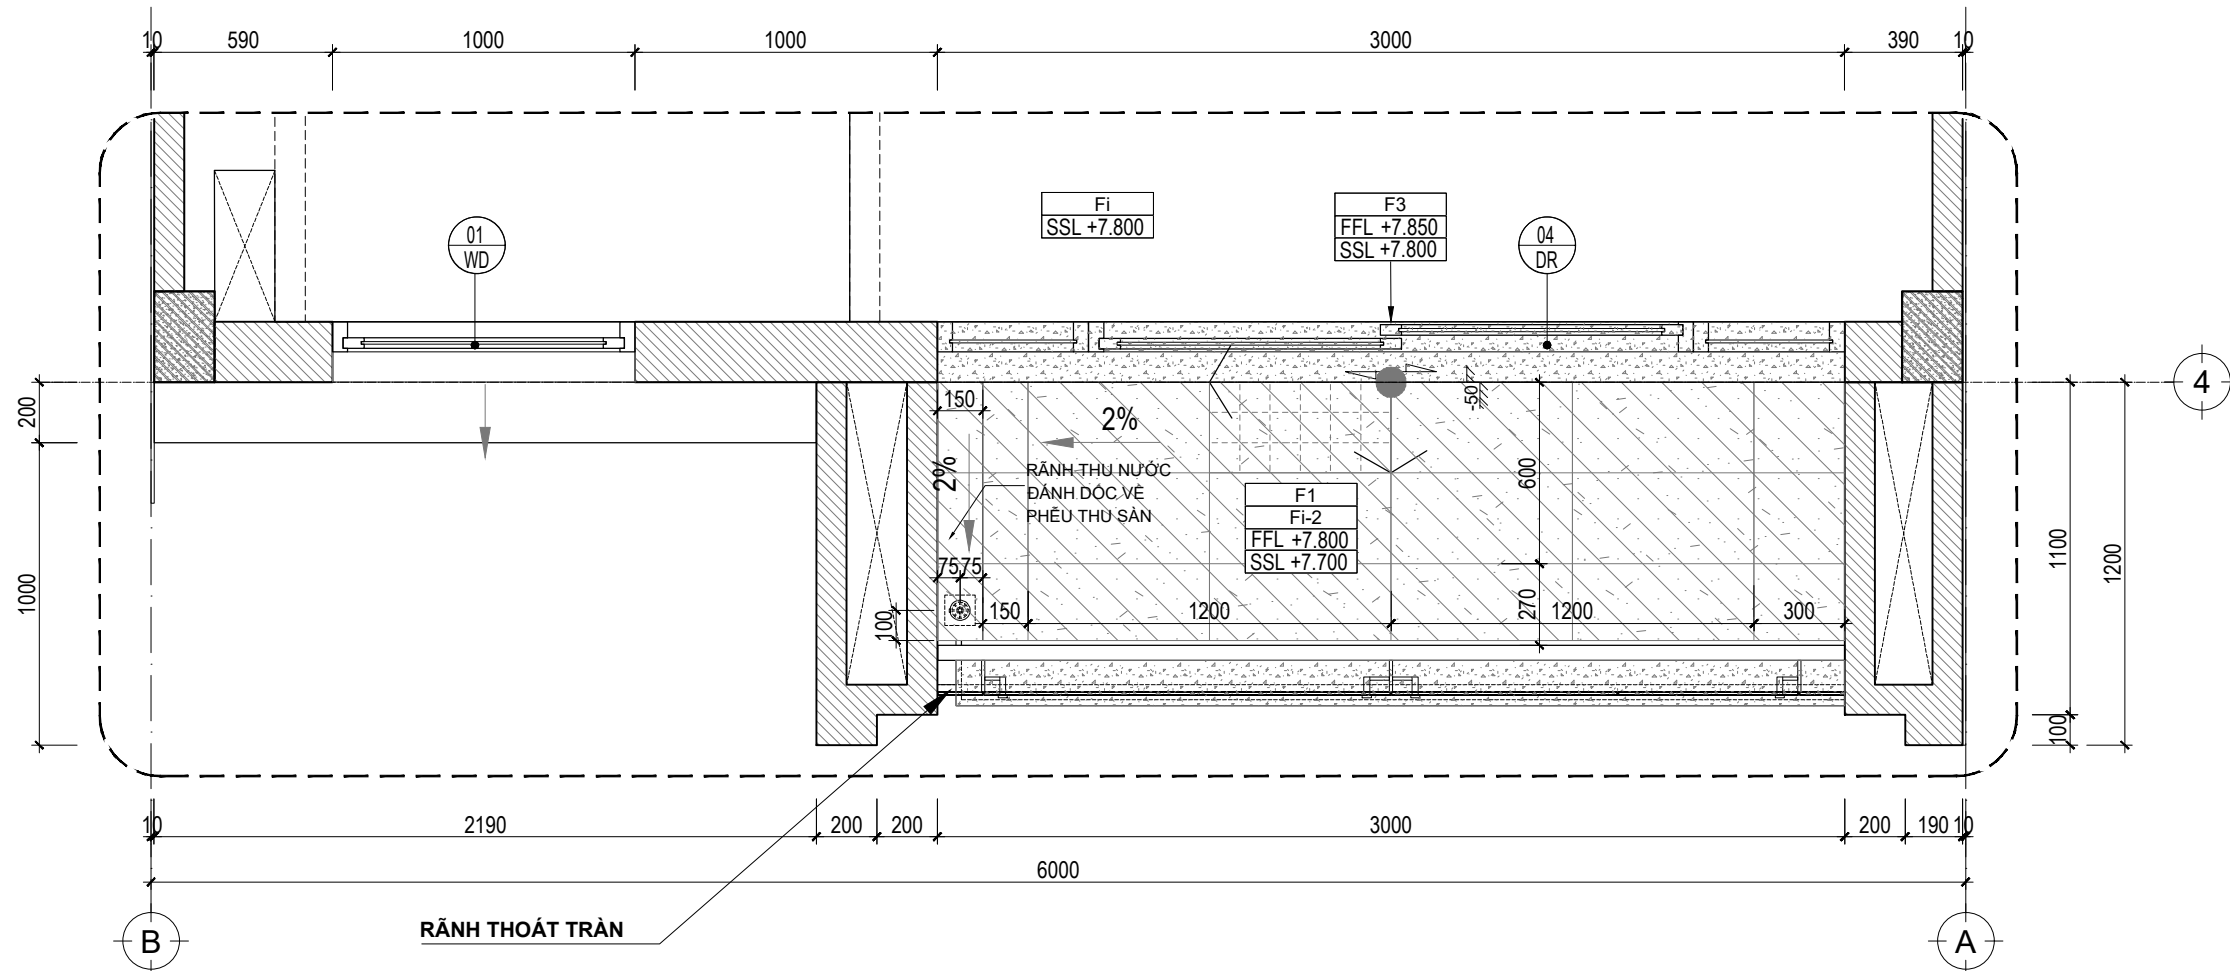

MẶT BẰNG TRÍCH ĐOẠN B-A - TẦNG 3_TL:1/25

VẬT LIỆU HOÀN THIỆN TƯỜNG		
KÝ HIỆU	MÔ TẢ	
FW1	TƯỜNG HOÀN THIỆN SƠN NƯỚC MÀU TRẮNG - RAL 9003	
FW2	TƯỜNG HOÀN THIỆN SƠN NƯỚC MÀU XÁM ĐẬM - RAL 7022	
FW3	TƯỜNG HOÀN THIỆN SƠN NƯỚC MÀU HỒNG NÂU - RAL 4009	
FW4	TƯỜNG HOÀN THIỆN SƠN NƯỚC MÀU VÀNG NHẠT - RAL 1015	
FW5	TƯỜNG HOÀN THIỆN SƠN NƯỚC MÀU XÁM - RAL 7042	
L1	LEN CHÂN TƯỜNG GẠCH PORCELAIN 300X600mm,CHỐNG THẤM TỐI MÀU	

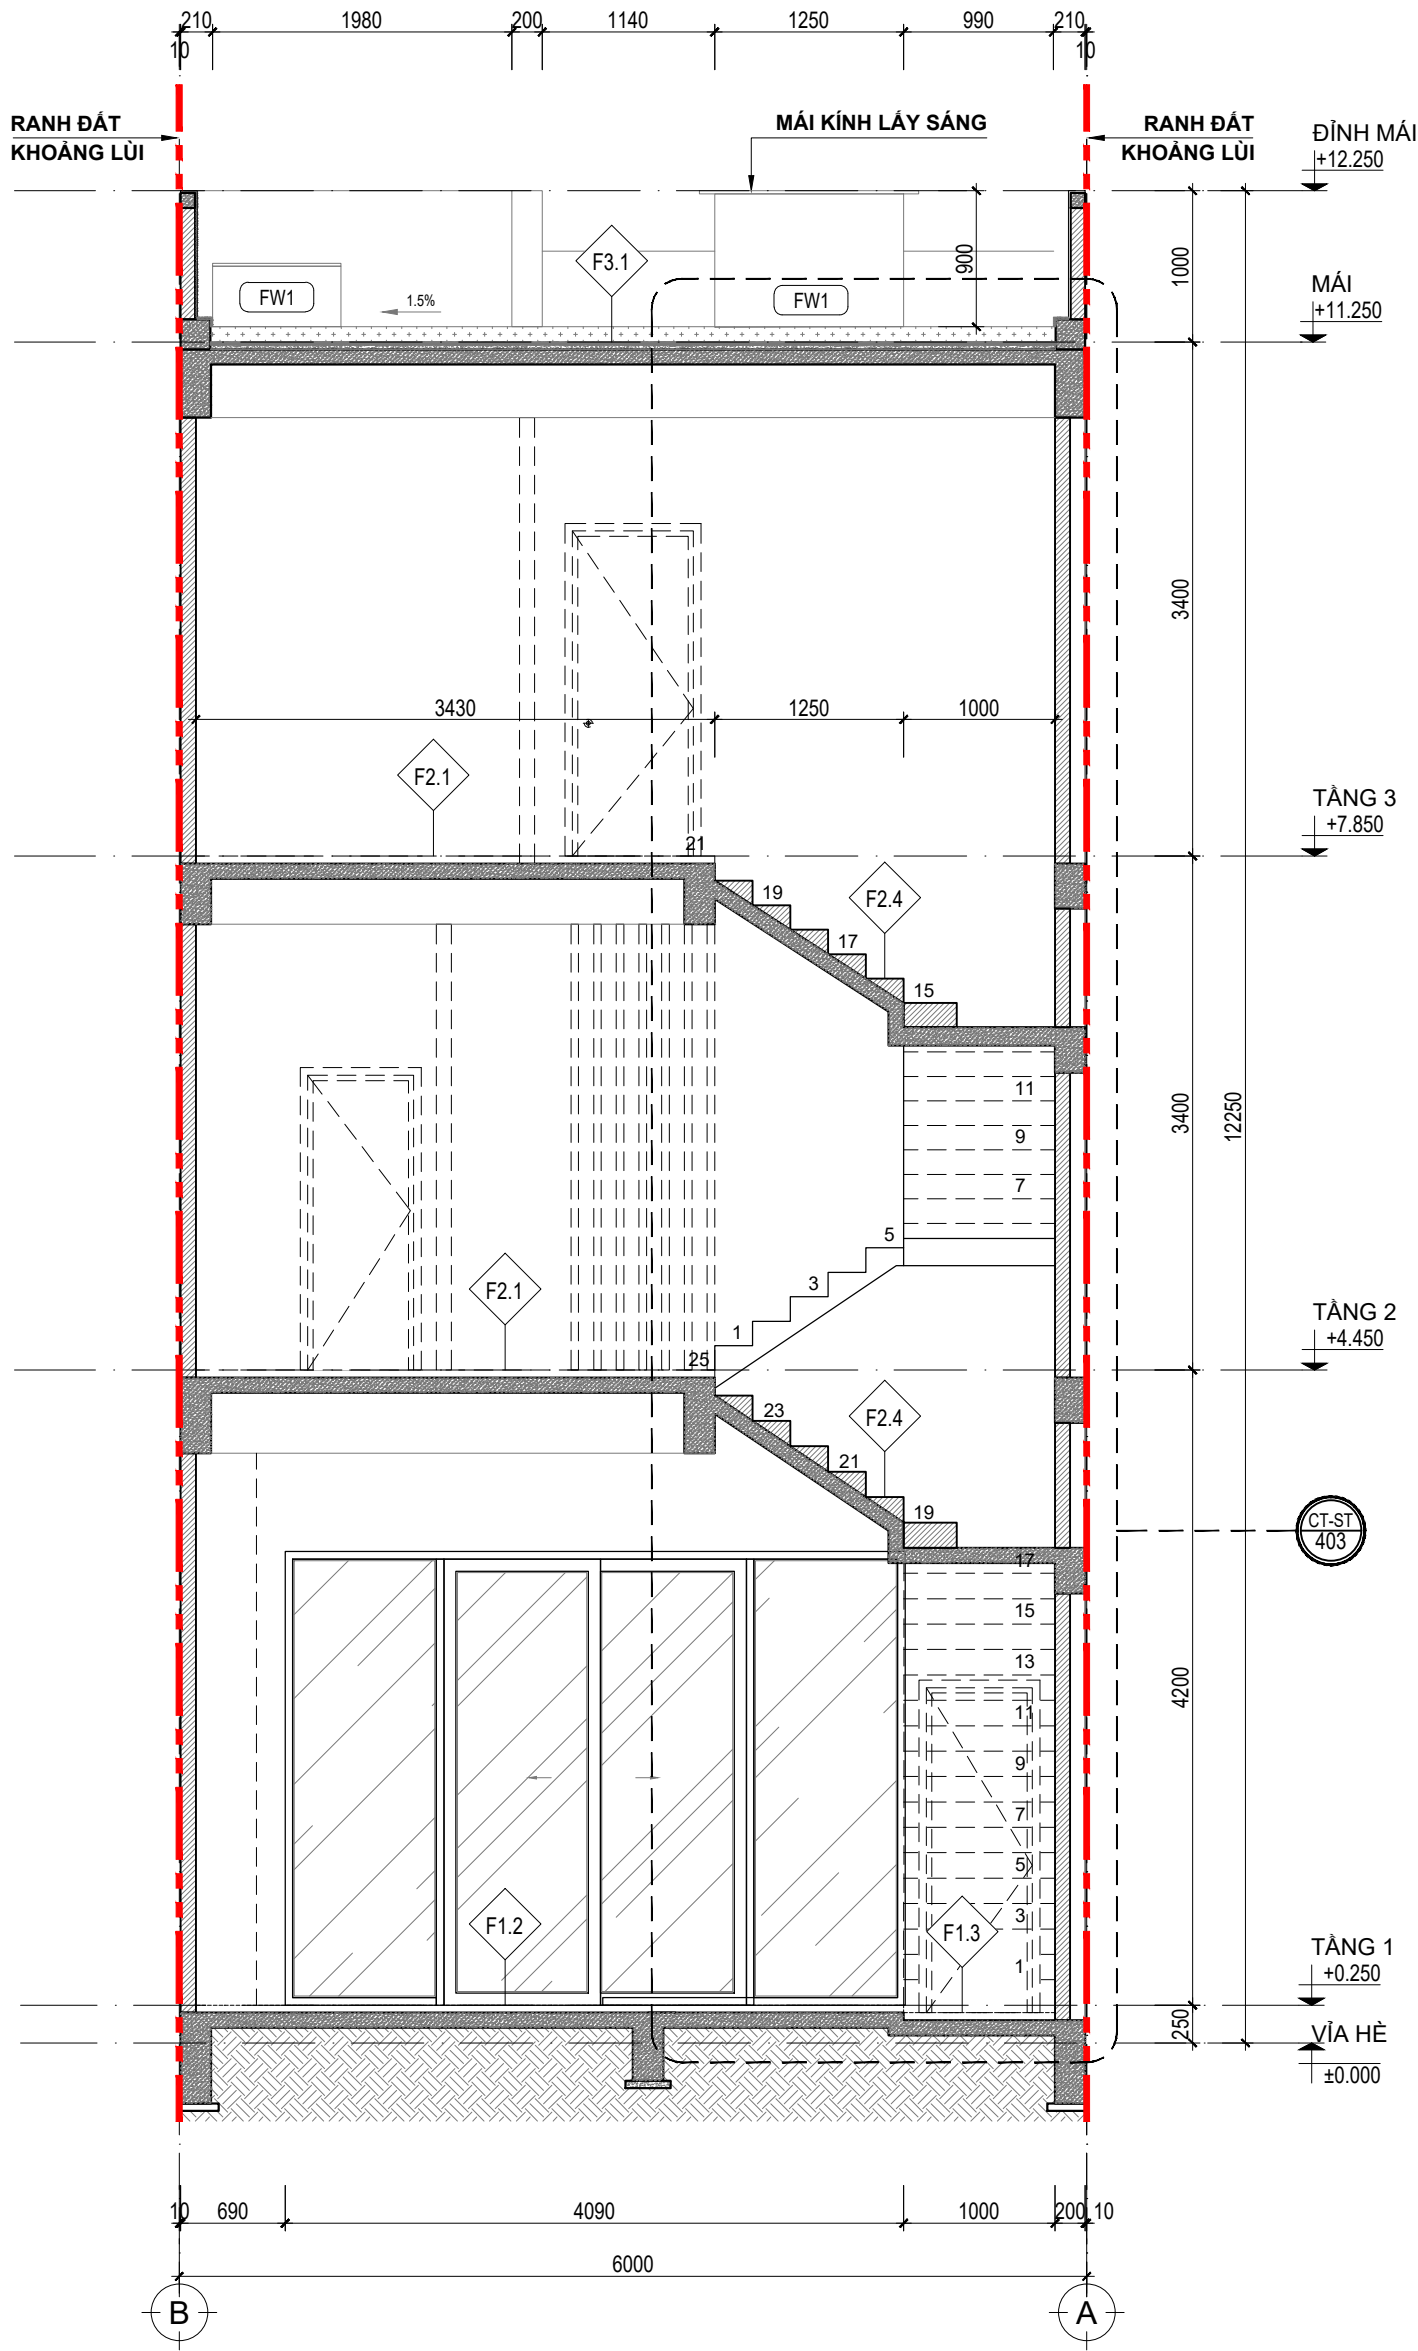


MẶT CẮT A-A _ TL:1/50

BẢNG THỐNG KÊ CẤU TẠO SÀN

	KÍ HIỆU	VỊ TRÍ	CHI TIẾT	MÔ TẢ CÁC LỚP CẤU TẠO		KÍ HIỆU	VỊ TRÍ	CHI TIẾT	MÔ TẢ CÁC LỚP CẤU TẠO		KÍ HIỆU	VỊ TRÍ	CHI TIẾT	MÔ TẢ CÁC LỚP CẤU TẠO
TẦNG 1	F1.1	SÁNH HIỆN		- ĐÁ BÀ GRANITE DÀY 20mm HOÀN THIÊN - LỚP VỮA CÁN NỀN M75 ĐÁNH ĐỐC - LỚP CHỐNG THẤM CUỐN LÊN CHÂN TƯỜNG 300mm - SÀN BTCT(xem BVKC) - LỚP BÊ TÔNG LỖT(XEM BVKC) - ĐẤT TỰ NHIÊN ĐÁM CHẤT XỬ LÍ CHỐNG MỠI ĐỒNG THỜI	TẦNG 2,3	F2.1	SÀN NỘI THẤT SÀN WC		SÀN BTCT(xem BVKC)	MÁI	F3.1	SÀN MÁI		- LỚP VỮA TẠO PHẪNG DÀY 10MM - LỚP BÊ TÔNG ĐÁ MỈ M200, LƯỚI THÉP D6@200, DÀY MÍN 50mm, TẠO ĐỐC 1.5% VỀ PHẪU THU - LỚP CHỐNG THẤM GÓC PU CUỐN LÊN CHÂN TƯỜNG 300mm - SÀN BTCT(xem BVKC)
	F1.2	SÀN NỘI THẤT		- SÀN BTCT(xem BVKC) - LỚP BÊ TÔNG LỖT(xem BVKC) - ĐẤT TỰ NHIÊN ĐÁM CHẤT XỬ LÍ CHỐNG MỠI ĐỒNG THỜI		F2.2	BÀN CÔNG SÀN THƯƠNG SÀN P. GIẶT		- GẠCH PORCELAIN CHỐNG TRƯỢT HOÀN THIÊN - LỚP VỮA CÁN NỀN M75 ĐÁNH ĐỐC VÉ RÀNH THỦ - LỚP CHỐNG THẤM CUỐN LÊN CHÂN TƯỜNG 300mm - LỚP ĐÓN NỀN - SÀN BTCT(xem BVKC) - HOÀN THIÊN SƠN NƯỚC NGOÀI THẬT THEO SPEC					
	F1.3	SÀN WC TẦNG 1		- SÀN BTCT(xem BVKC) - LỚP BÊ TÔNG LỖT(xem BVKC) - ĐẤT TỰ NHIÊN ĐÁM CHẤT XỬ LÍ CHỐNG MỠI ĐỒNG THỜI		F2.3	SÀN BÓN HOA		- LỚP VỮA CÁN NỀN M75 ĐÁNH ĐỐC VÉ RÀNH THỦ - LỚP CHỐNG THẤM CUỐN LÊN CAO TỐI THÀNH BÓN HOA - SÀN BTCT(xem BVKC) - HOÀN THIÊN SƠN NƯỚC NGOÀI THẬT THEO SPEC					
						F2.4	CẦU THANG		- LỚP VỮA TẠO PHẪNG DÀY 8-10mm - LỚP GẠCH ĐÌNH XÂY TẠO BẮC - SÀN THANG BTCT(xem BVKC)					
GHI CHÚ: CAO ĐỘ ±0.00 TRONG BẢN VẼ TƯƠNG ỨNG CAO ĐỘ HỒN DẦU TẠI VĨA HỀ. CAO ĐỘ VĨA HỀ VUI LÒNG XEM CÁC BẢN VẼ "THIẾT KẾ HẠ TẦNG"														

GHI CHÚ: CAO ĐỘ ±0.00 TRONG BẢN VẼ TƯƠNG ỨNG CAO ĐỘ HỒN DẦU TẠI VÍA HÈ. CAO ĐỘ VÍA HÈ VUI LÒNG XEM CÁC BẢN VẼ "THIẾT KẾ HẠ TẦNG"

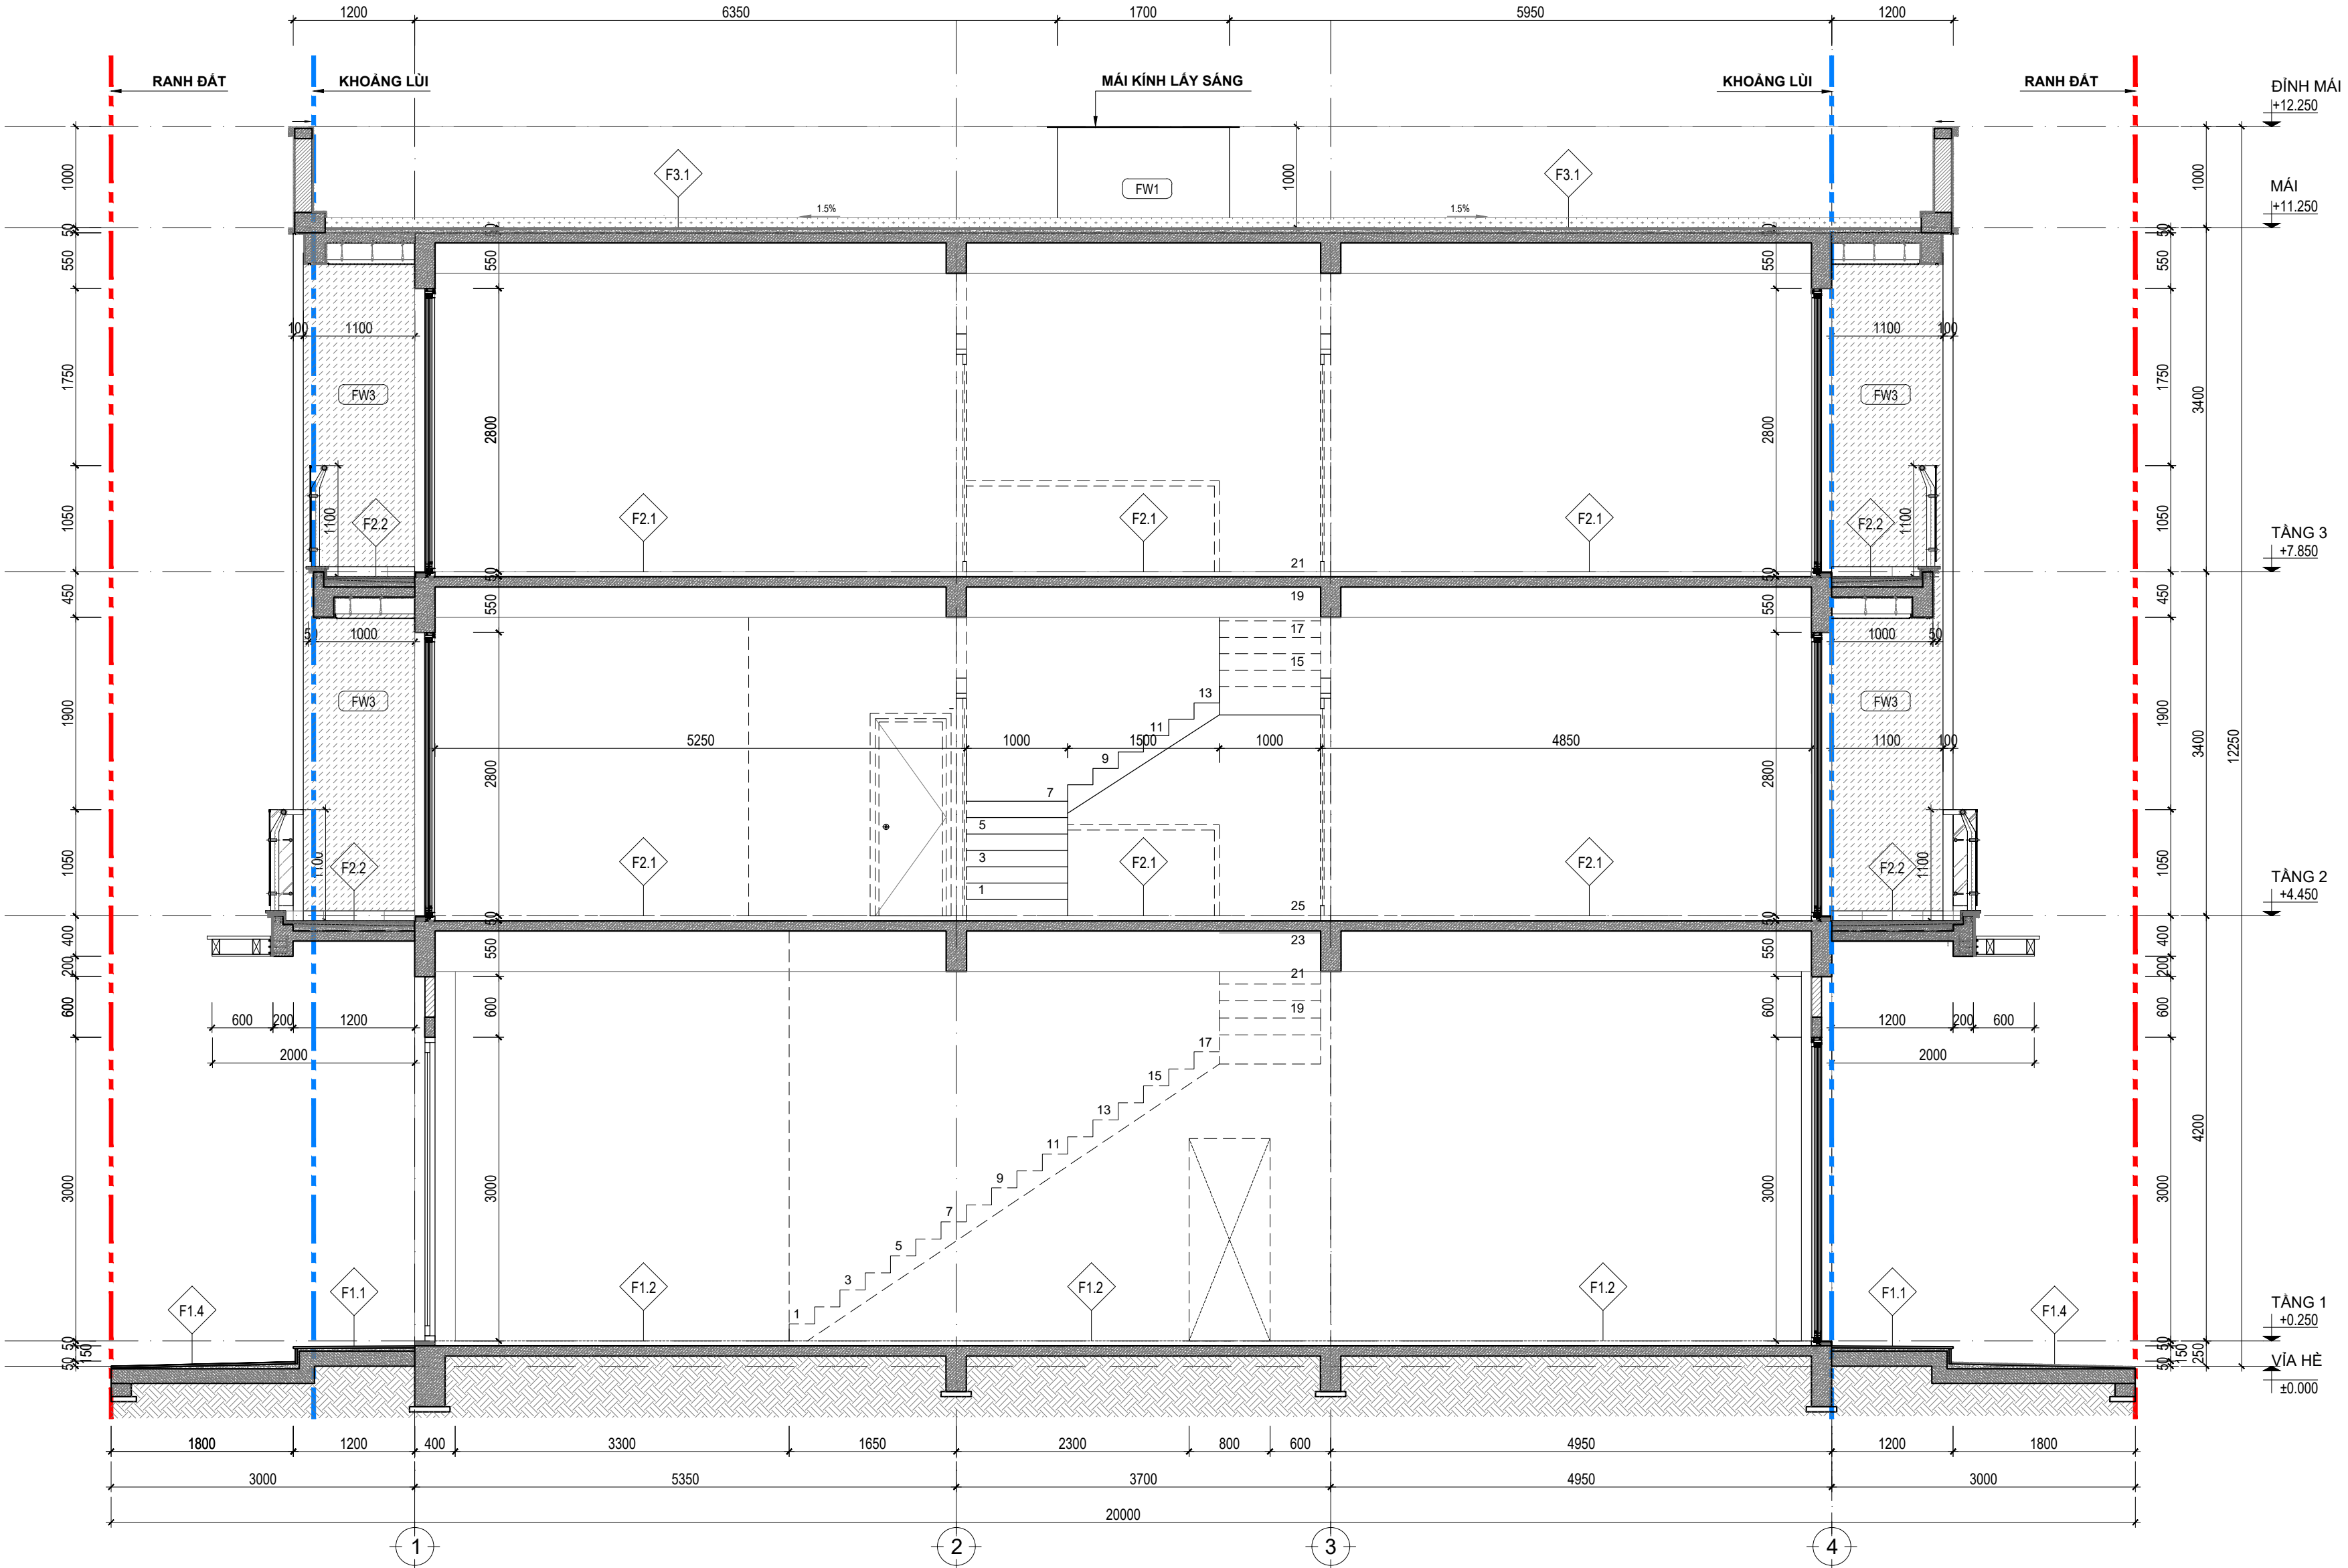


MẶT CẮT B-B _ TL:1/50

BẢNG THÔNG KÊ CẤU TẠO SÀN

	KÍ HIỆU	VỊ TRÍ	CHI TIẾT	MÔ TẢ CÁC LỚP CẤU TẠO		KÍ HIỆU	VỊ TRÍ	CHI TIẾT	MÔ TẢ CÁC LỚP CẤU TẠO		KÍ HIỆU	VỊ TRÍ	CHI TIẾT	MÔ TẢ CÁC LỚP CẤU TẠO
TẦNG 1		SÂN HIỆN		- ĐÁ ĐÁ GRANITE DÀY 20mm HOÀN THIỆN - LỚP Vữa CÁN NỀN M75 ĐÁNH DỌC - LỚP CHỐNG THẤM CUỐN LÊN CHÂN TƯỜNG 300mm - SÀN BTCT (xem BVKC) - LỚP BÊ TÔNG LỖI (XEM BVKC) - ĐẤT TỰ NHIÊN ĐÁM CHẤT XỬ LÝ CHỐNG MỠI ĐỒNG THỜI	TẦNG 2,3		SÂN NỘI THẤT		SÀN BTCT (xem BVKC)	MÁI		SÂN Mái		- LỚP Vữa TẠO PHẪNG DÀY 10mm - LỚP BÊ TÔNG ĐÁ MỀM MỎI, LƯỚI THÉP D8@200, DÀY MÍN 50mm, TẠO DỐC 1.5% VỀ PHẪU THU - LỚP CHỐNG THẤM GÓC PU CUỐN LÊN CHÂN TƯỜNG 300mm - SÀN BTCT (xem BVKC)
		SÂN NỘI THẤT		- SÀN BTCT (xem BVKC) - LỚP BÊ TÔNG LỖI (xem BVKC) - ĐẤT TỰ NHIÊN ĐÁM CHẤT XỬ LÝ CHỐNG MỠI ĐỒNG THỜI			BAN CÔNG SÂN THƯỢNG SÂN P. GIÁT		- GẠCH PORCELAIN CHỐNG TRƯỢT HOÀN THIỆN - LỚP Vữa CÁN NỀN M75 ĐÁNH DỌC VÉ RÀNH THU - LỚP CHỐNG THẤM CUỐN LÊN CHÂN TƯỜNG 300mm - LỚP ĐÓN NỀN - SÀN BTCT (xem BVKC) - HOÀN THIỆN SƠN NƯỚC NGOÀI THẬT THEO SPEC					
		SÂN WC TẦNG 1		- SÀN BTCT (xem BVKC) - LỚP BÊ TÔNG LỖI (xem BVKC) - ĐẤT TỰ NHIÊN ĐÁM CHẤT XỬ LÝ CHỐNG MỠI ĐỒNG THỜI			SÂN BÓN HOA		- LỚP Vữa CÁN NỀN M75 ĐÁNH DỌC VÉ RÀNH THU - LỚP CHỐNG THẤM CUỐN LÊN CAO TỐI THỂ THÀNH BÓN HOA - SÀN BTCT (xem BVKC) - HOÀN THIỆN SƠN NƯỚC NGOÀI THẬT THEO SPEC					
							CẦU THANG		- LỚP Vữa TẠO PHẪNG DÀY 8-10mm - LỚP GẠCH BÉNH XÂY TẠO BÁC - SÀN THANG BTCT (xem BVKC)					

GHI CHÚ: CAO ĐỘ ±0.00 TRONG BẢN VẼ TƯƠNG ỨNG CAO ĐỘ HỒN DẦU TẠI VÍA HÉ. CAO ĐỘ VÍA HÉ VUI LÒNG XEM CÁC BẢN VẼ "THIẾT KẾ HẠ TẦNG"

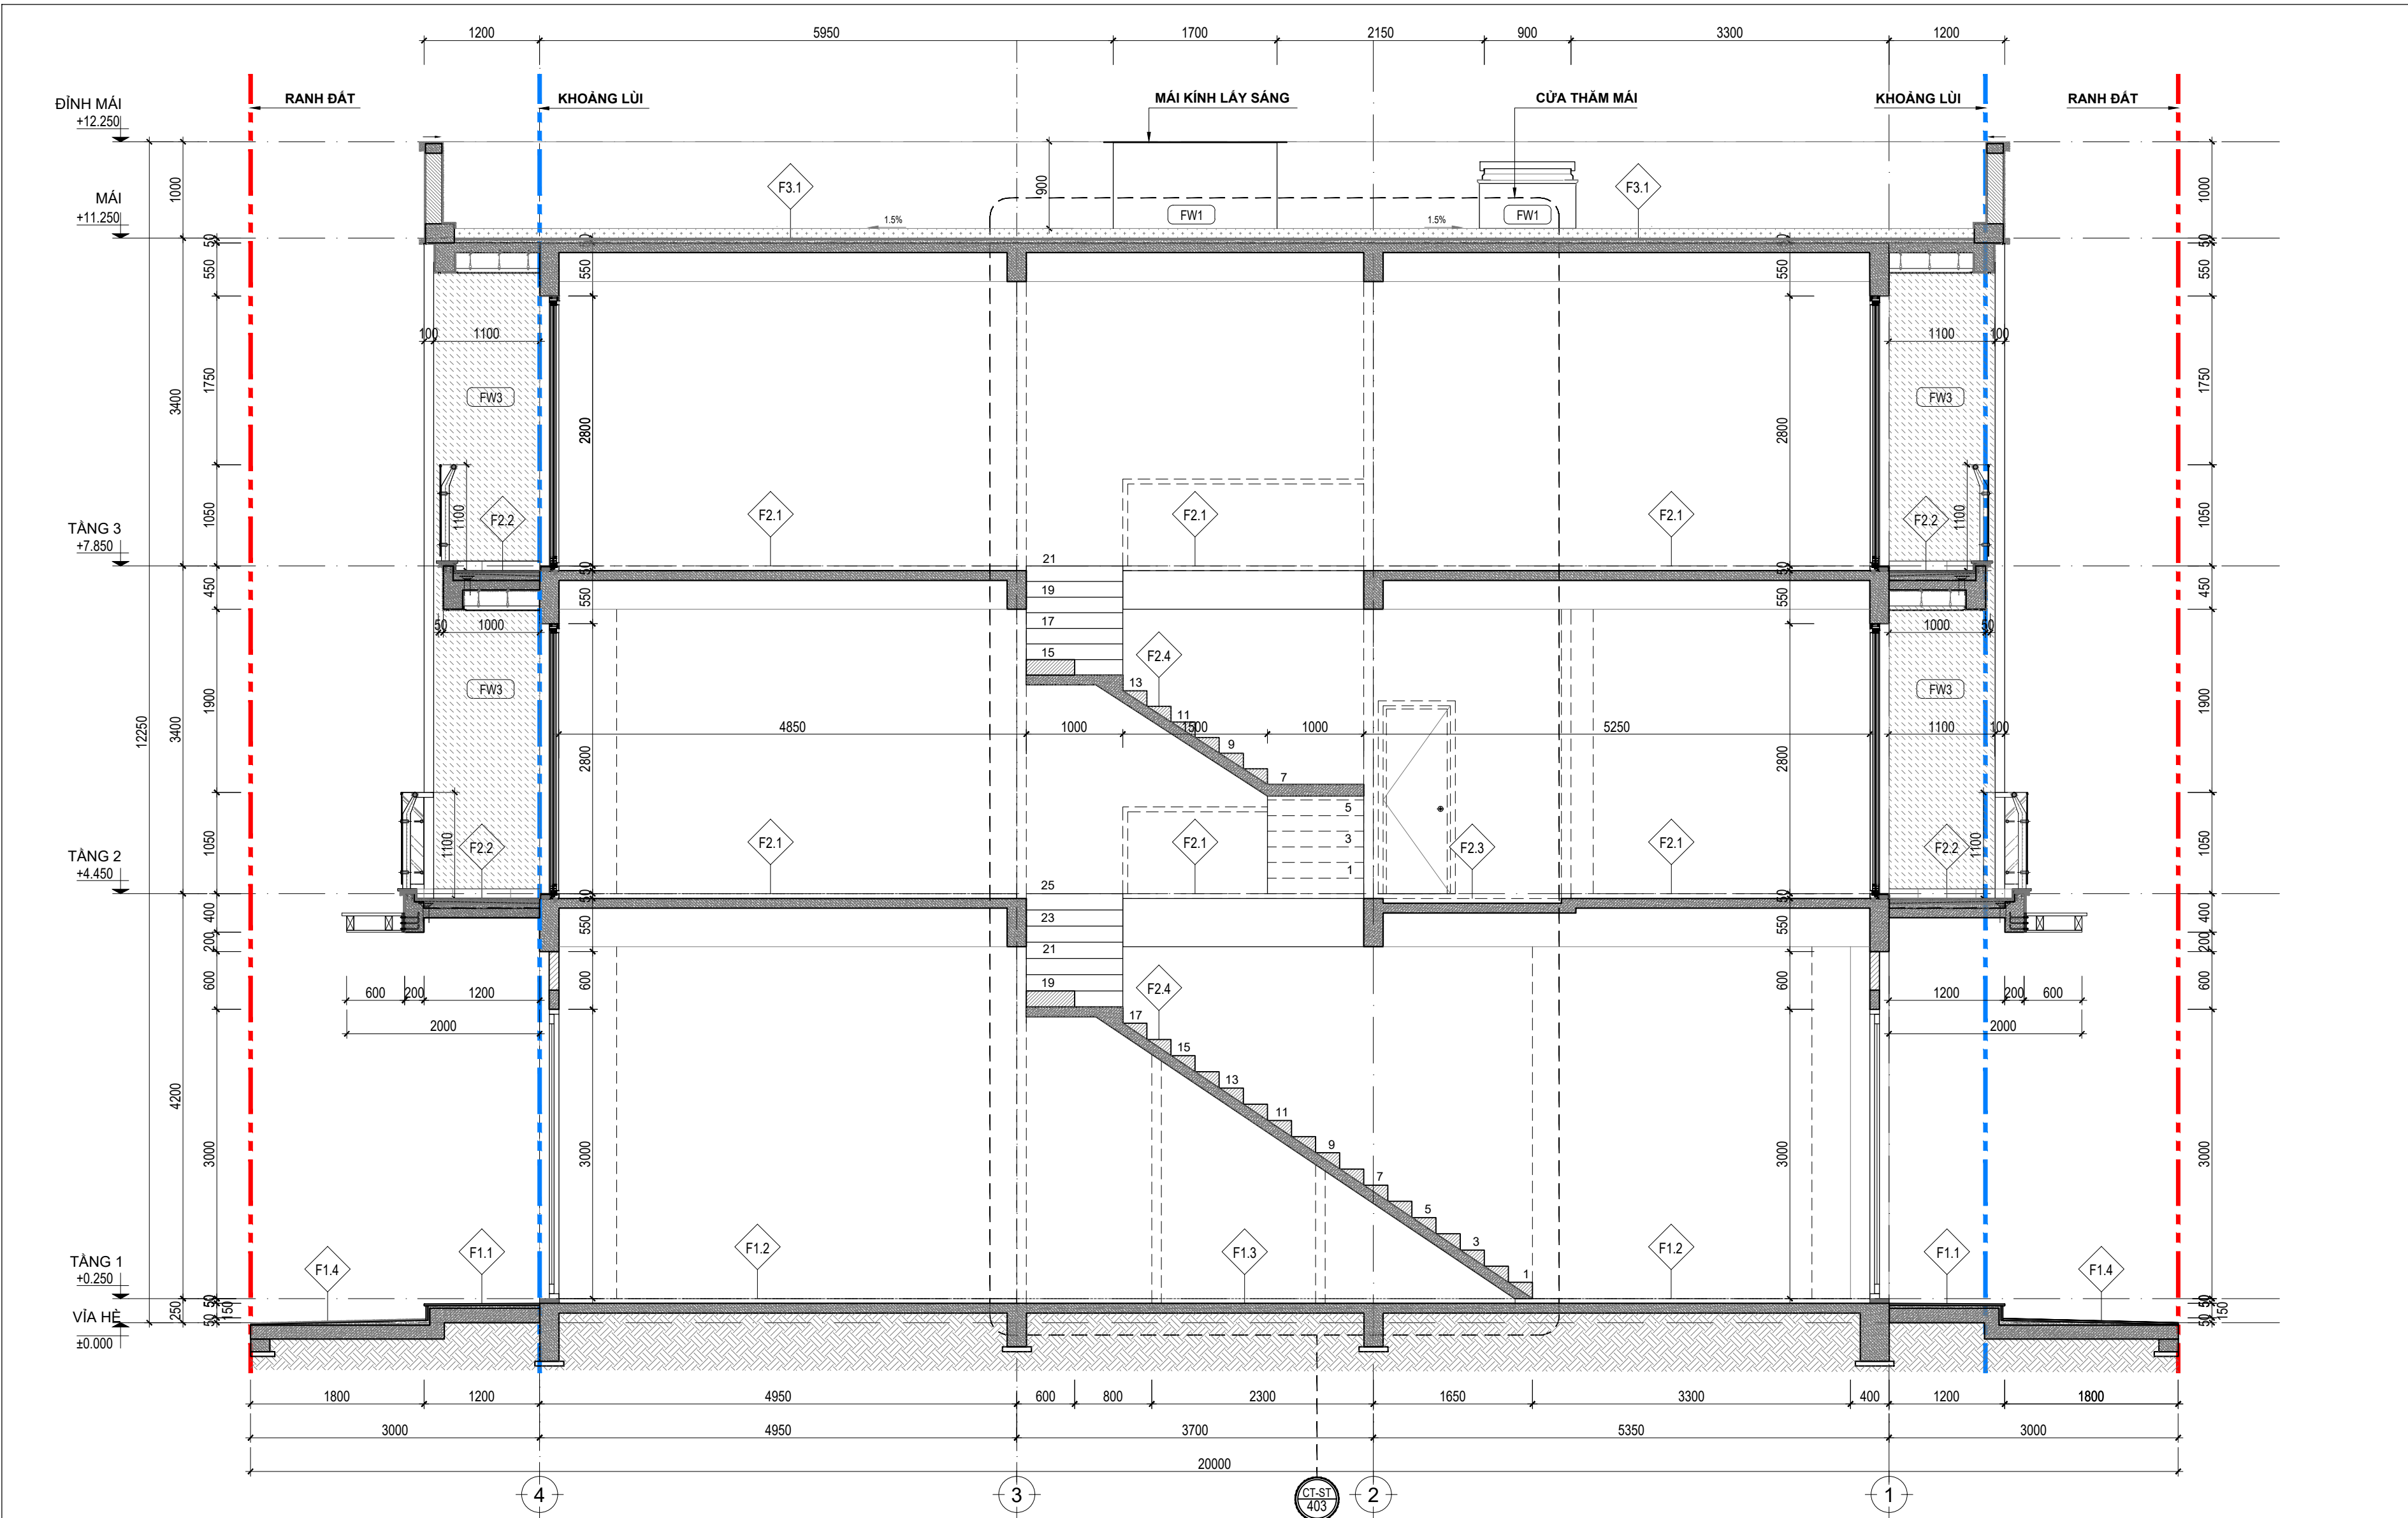


MẶT CẮT C-C _ TL:1/50

BẢNG THÔNG KÊ CẤU TẠO SÀN


	KÍ HIỆU	VỊ TRÍ	CHI TIẾT	MÔ TẢ CÁC LỚP CẤU TẠO		KÍ HIỆU	VỊ TRÍ	CHI TIẾT	MÔ TẢ CÁC LỚP CẤU TẠO		KÍ HIỆU	VỊ TRÍ	CHI TIẾT	MÔ TẢ CÁC LỚP CẤU TẠO
TẦNG 1		SÀNH HIỂN		- ĐÁ BÀ GRANITE DÀY 20mm HOÀN THIÊN - LỚP Vữa CÁN NỀN M75 ĐÁNH DỌC - LỚP CHỐNG THẤM CUỘN LÊN CHÂN TƯỜNG 300mm - SÀN BTCT (xem BVKC) - LỚP BÊ TÔNG LÓT (xem BVKC) - ĐẤT TỰ NHIÊN ĐÁM CHẤT XỬ LÝ CHỐNG MÔI ĐỒNG THỜI	TẦNG 2,3		SÀN NỘI THẤT SÀN WC		SÀN BTCT (xem BVKC)	MÁI		SÀN MÁI		- LỚP Vữa TẠO PHẪNG DÀY 10mm - LỚP BÊ TÔNG BÀ MỈ M200, LƯỚI THÉP D6@200, DÂY MÍN 50mm, TẠO DỐC 1.5% VỀ PHẪU THU - LỚP CHỐNG THẤM GÓC PU CUỘN LÊN CHÂN TƯỜNG 300mm - SÀN BTCT (xem BVKC)
		SÀN NỘI THẤT		- SÀN BTCT (xem BVKC) - LỚP BÊ TÔNG LÓT (xem BVKC) - ĐẤT TỰ NHIÊN ĐÁM CHẤT XỬ LÝ CHỐNG MÔI ĐỒNG THỜI			BAN CÔNG SÀN THƯỢNG SÀN P. GIẶT		- GẠCH PORCELAIN CHỐNG TRƯỢT HOÀN THIÊN - LỚP Vữa CÁN NỀN M75 ĐÁNH DỌC VÉ RÀNH THU - LỚP CHỐNG THẤM CUỘN LÊN CHÂN TƯỜNG 300mm - LỚP ĐÓN NỀN - SÀN BTCT (xem BVKC) - HOÀN THIÊN SƠN NƯỚC NGOÀI THẬT THEO SPEC					
		SÀN WC TẦNG 1		- SÀN BTCT (xem BVKC) - LỚP BÊ TÔNG LÓT (xem BVKC) - ĐẤT TỰ NHIÊN ĐÁM CHẤT XỬ LÝ CHỐNG MÔI ĐỒNG THỜI			SÀN BÓN HOA		- LỚP Vữa CÁN NỀN M75 ĐÁNH DỌC VÉ RÀNH THU - LỚP CHỐNG THẤM CUỘN LÊN CAO TỐI THÀNH BÓN HOA - SÀN BTCT (xem BVKC) - HOÀN THIÊN SƠN NƯỚC NGOÀI THẬT THEO SPEC					
							CẦU THANG		- LỚP Vữa TẠO PHẪNG DÀY 8-10mm - LỚP GẠCH BỀN XÂY TẠO BẮC - SÀN THANG BTCT (xem BVKC)					

GHI CHÚ: CAO ĐỘ ±0.00 TRONG BẢN VẼ TƯƠNG ỨNG CAO ĐỘ HỒN DẦU TẠI VÍA HÉ. CAO ĐỘ VÍA HÉ VUI LÒNG XEM CÁC BẢN VẼ "THIẾT KẾ HẠ TẦNG"


CHI TIẾT SÂN HIỀN

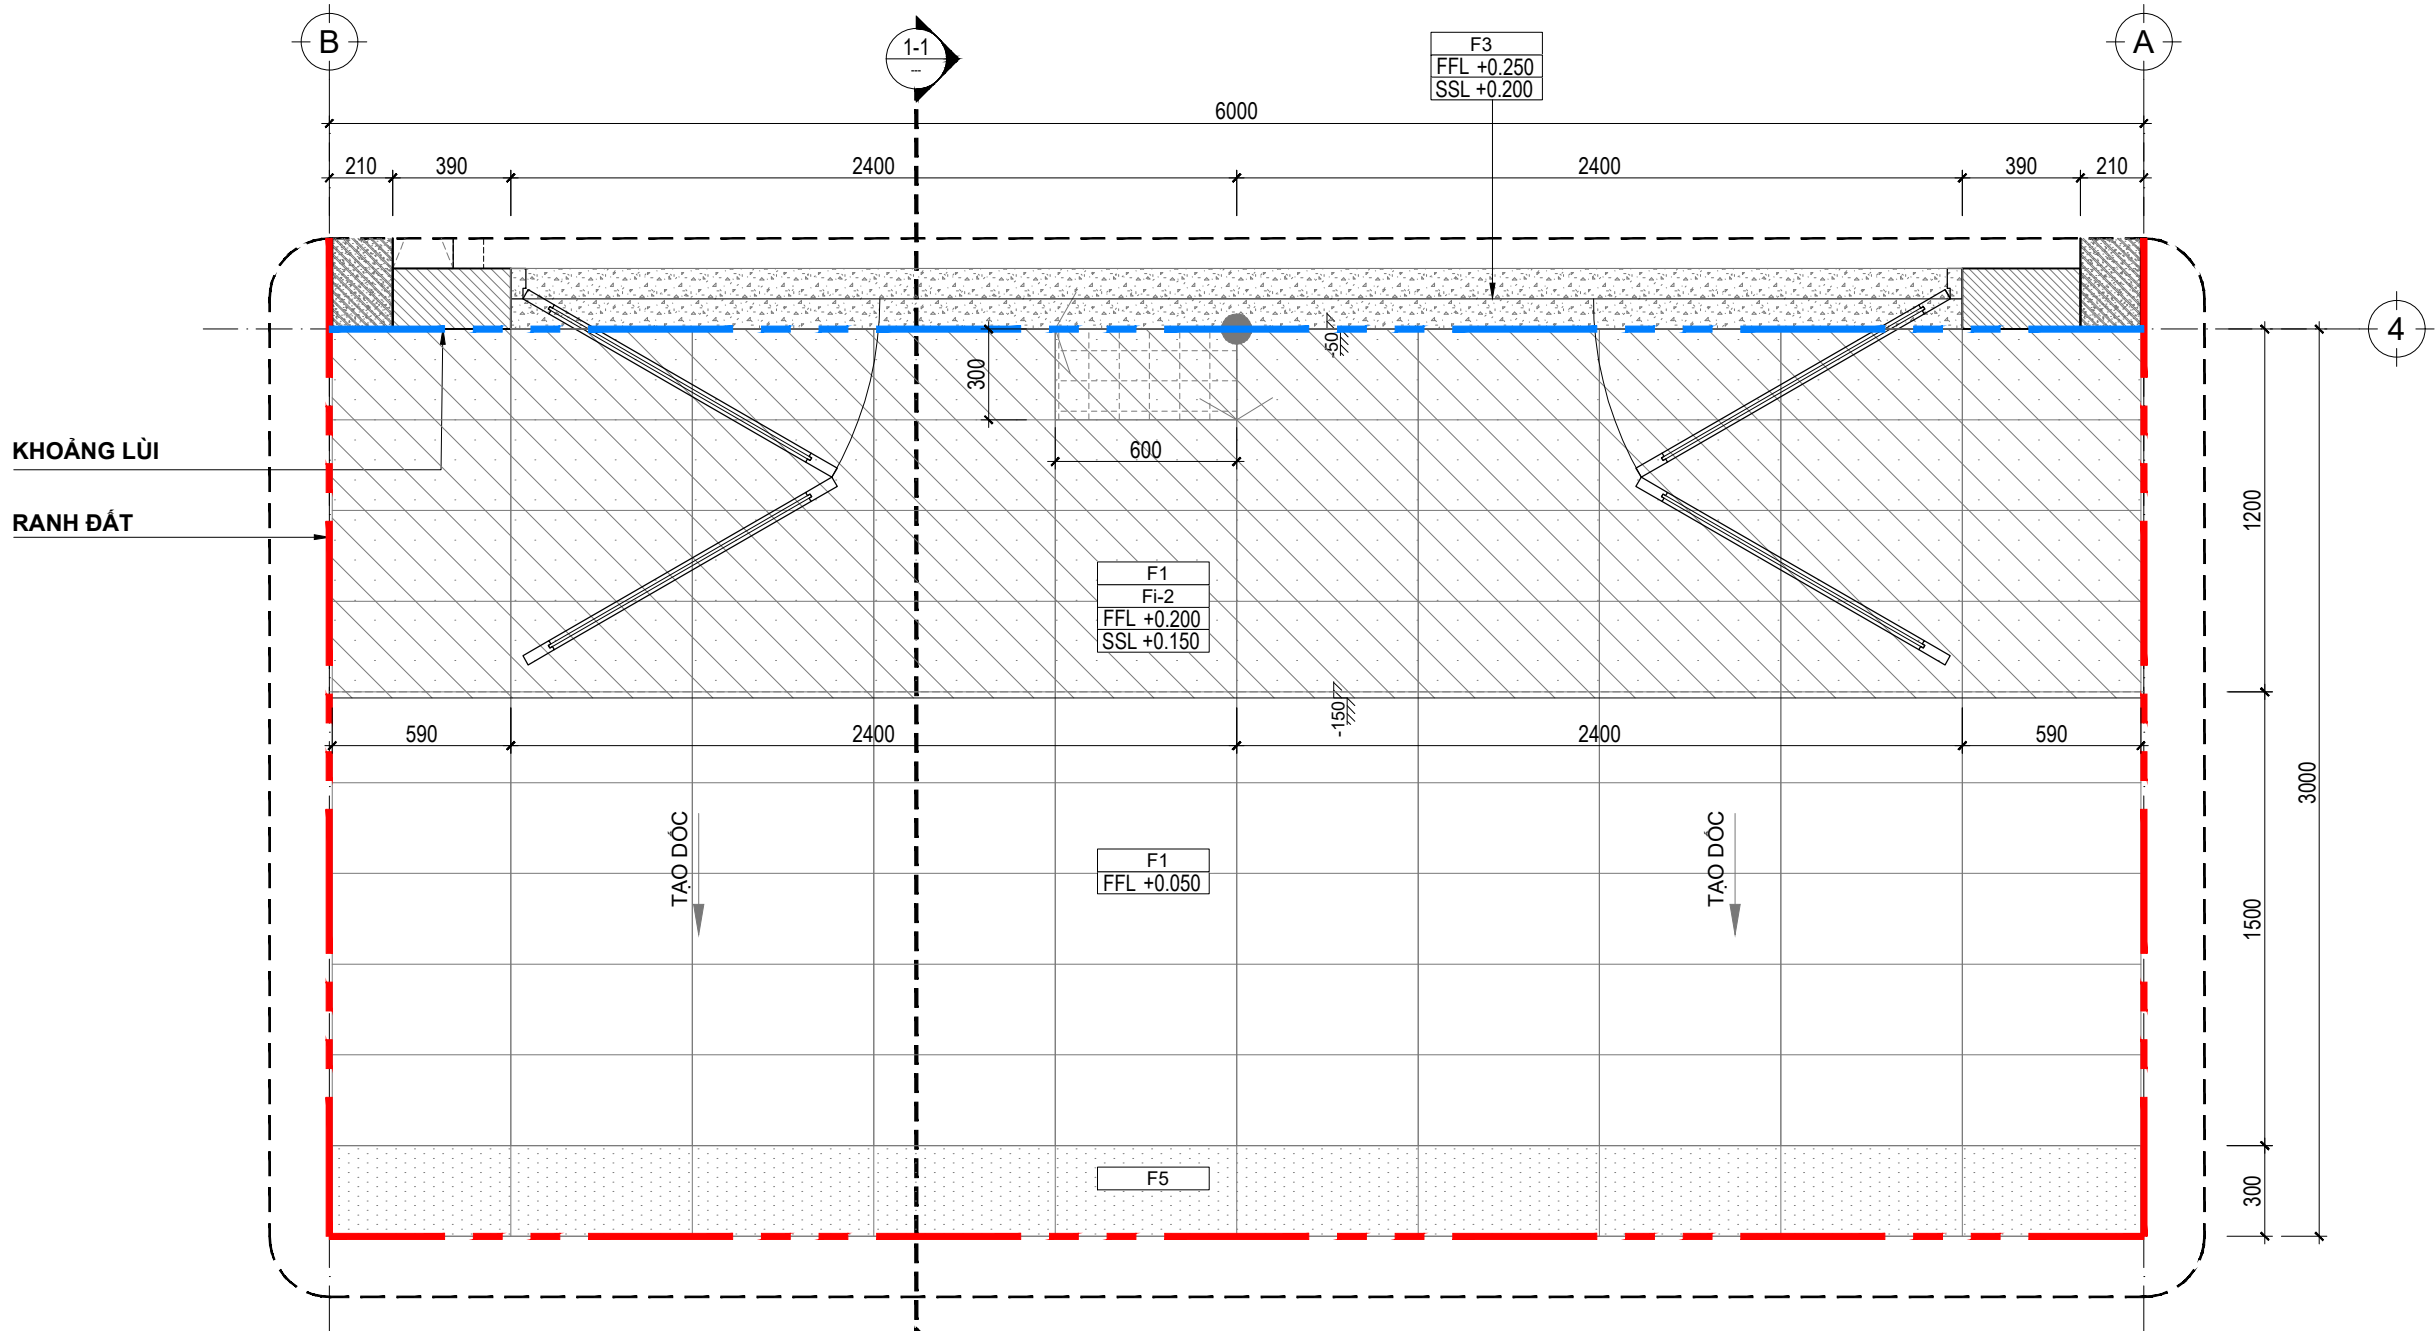


MẶT BẰNG SÂN TRƯỚC_TL:1/25

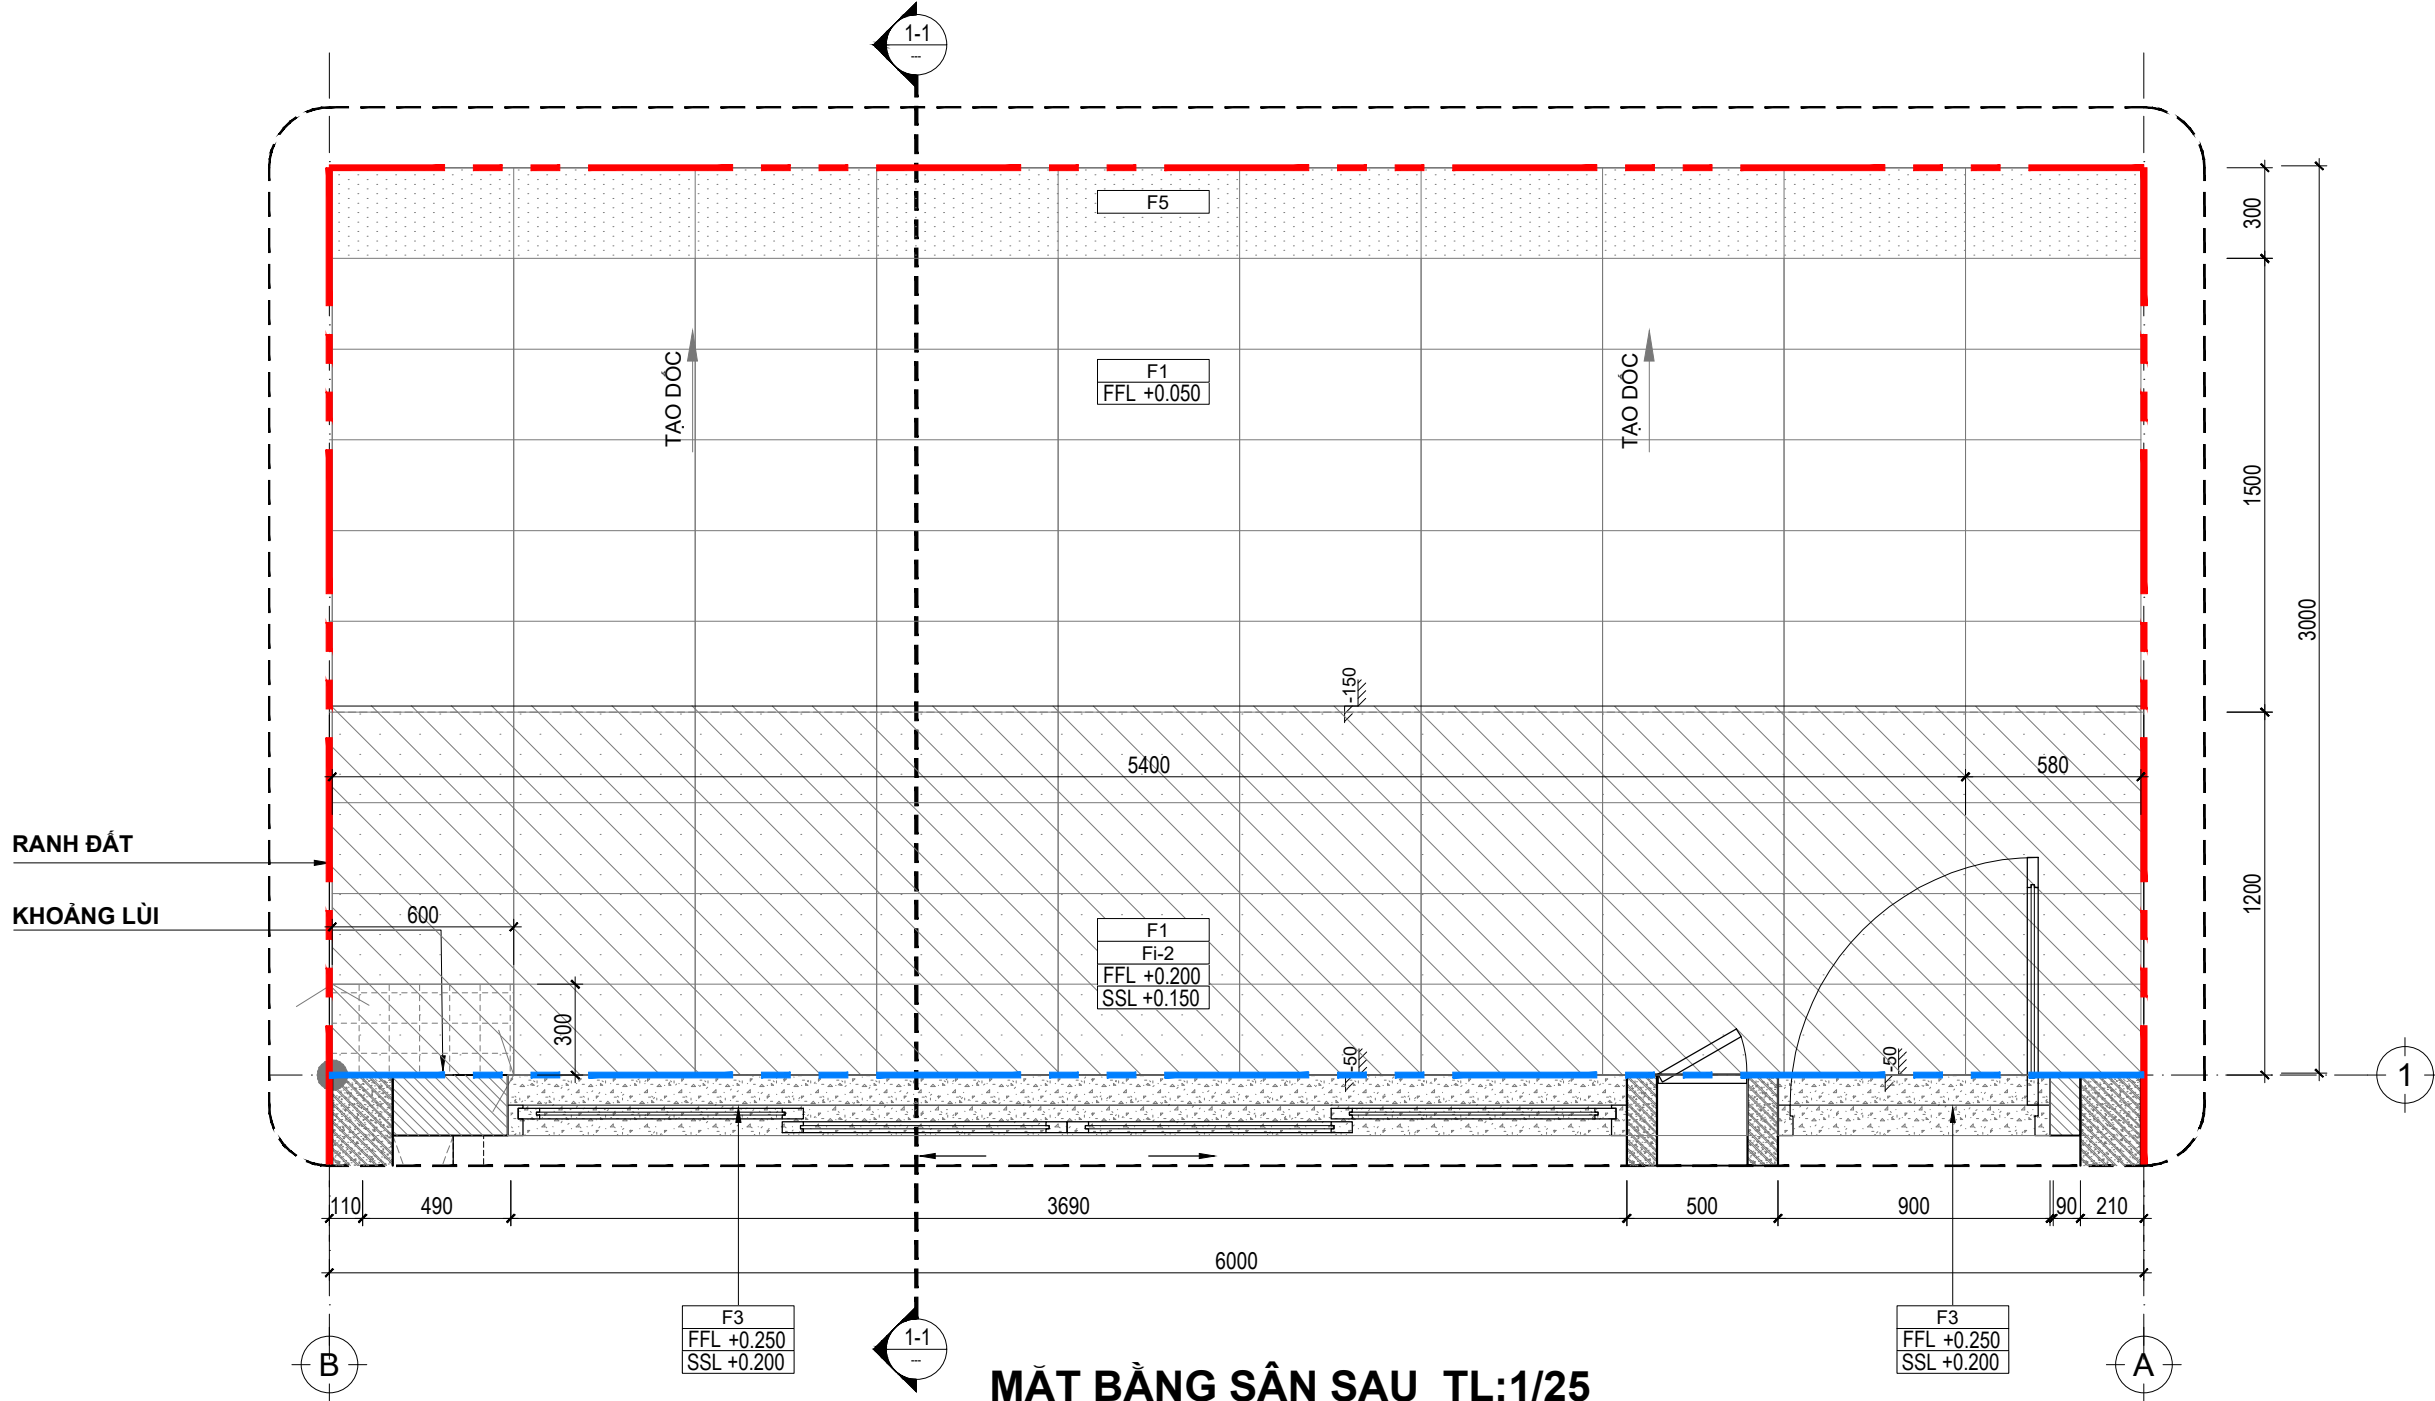

MẶT BẰNG SÂN SAU_TL:1/25

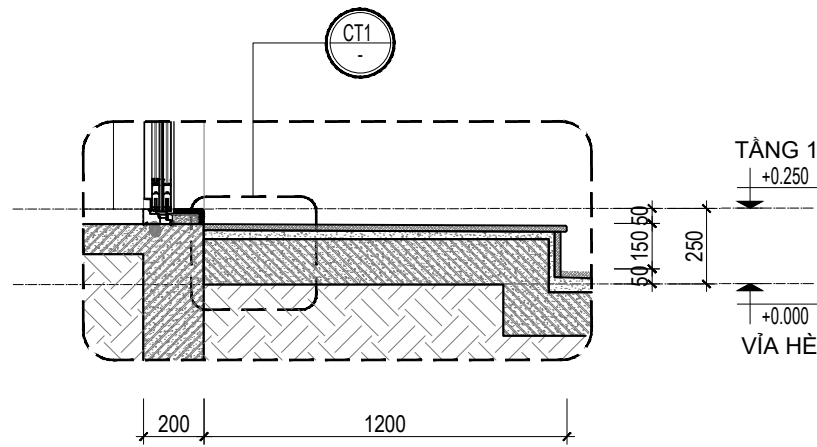


MẶT CẮT 1-1_TL:1/25

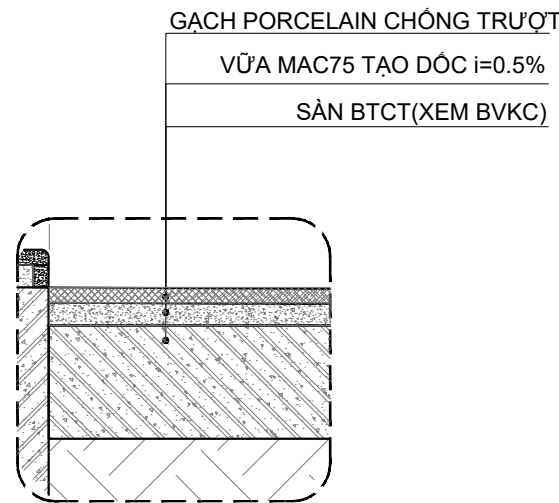


CHI TIẾT 1_TL:1/10

GHI CHÚ VẬT LIỆU SÀN NGOẠI THẤT		
TÊN	KÍ HIỆU	CHÚ THÍCH
F1		SÀN BÊ TÔNG CỐT THÉP THỎ
Fi-2		SÀN BÊ TÔNG CỐT THÉP, CHỐNG THÂM
F1		GẠCH PORCELAIN 300x600mm, CHỐNG TRƯỢT, NGOẠI THẤT
F2		ĐÁ ĐÀ GRANITE DÀY 20mm CHỐNG TRƯỢT 600x600mm
F3		ĐÁ ĐÀ GRANITE DÀY 20mm LÁT NGÁCH CỬA
F4		GẠCH ĐỒNG NHẤT CHỐNG TRƯỢT, MÀU SÁNG 300x300
F5		ĐÁ BAZAN 300x600


CHI TIẾT BAN CÔNG 01, 02

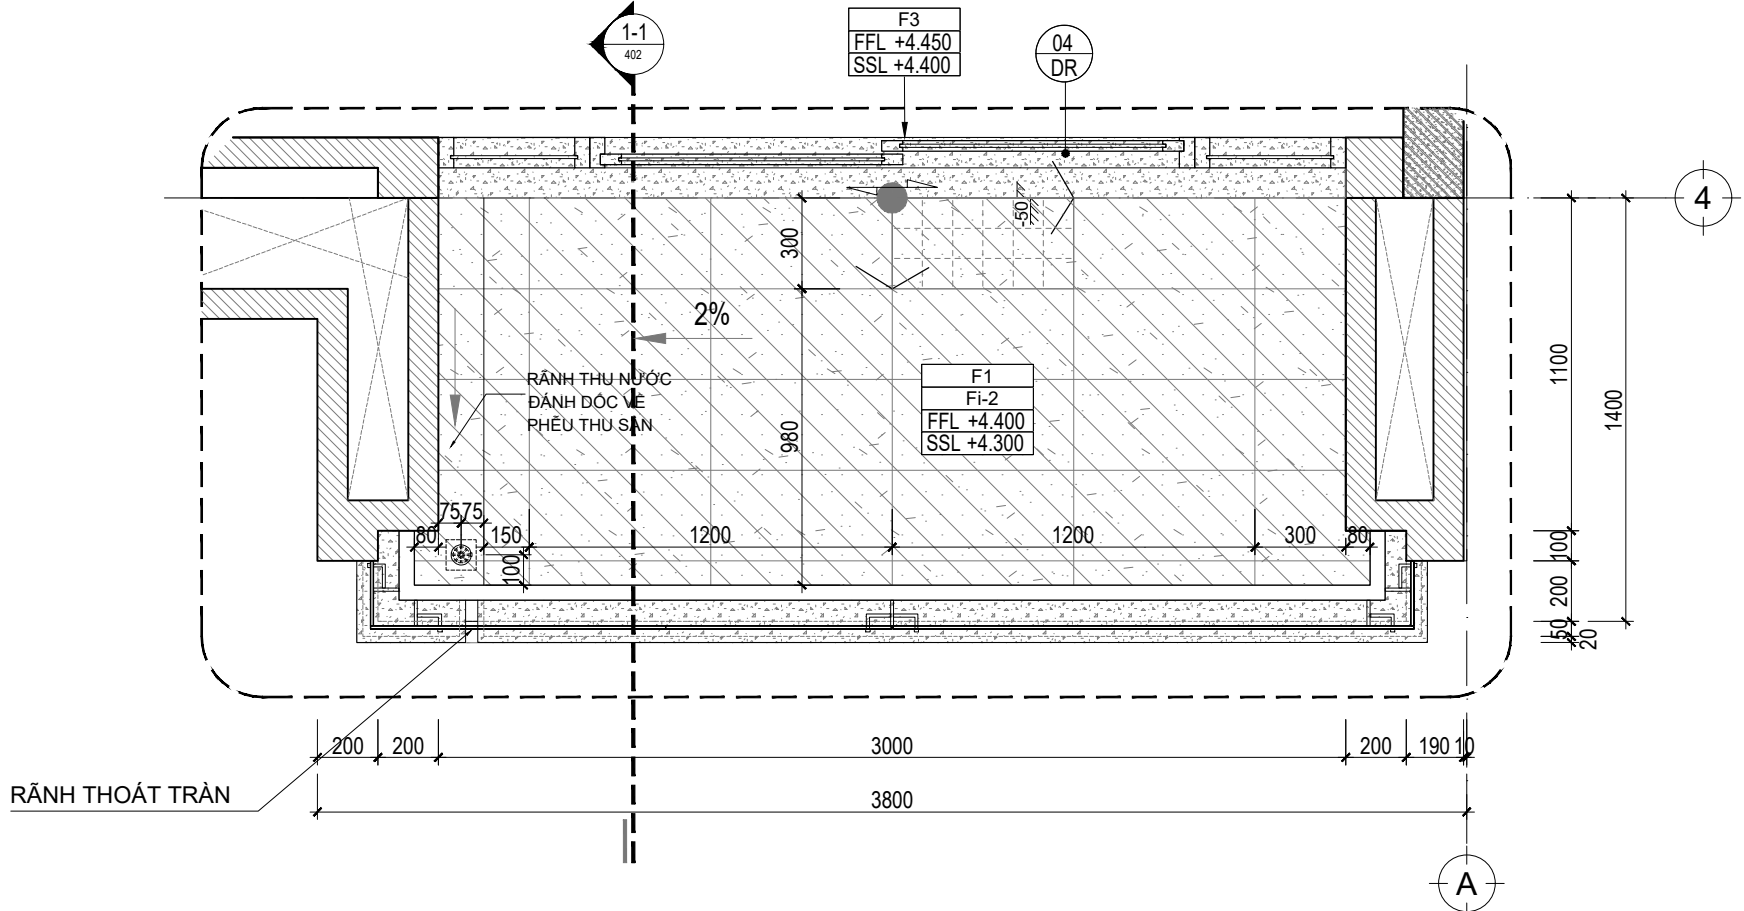


MẶT BẰNG BAN CÔNG TẦNG 2 ĐIỂN HÌNH_TL:1/25

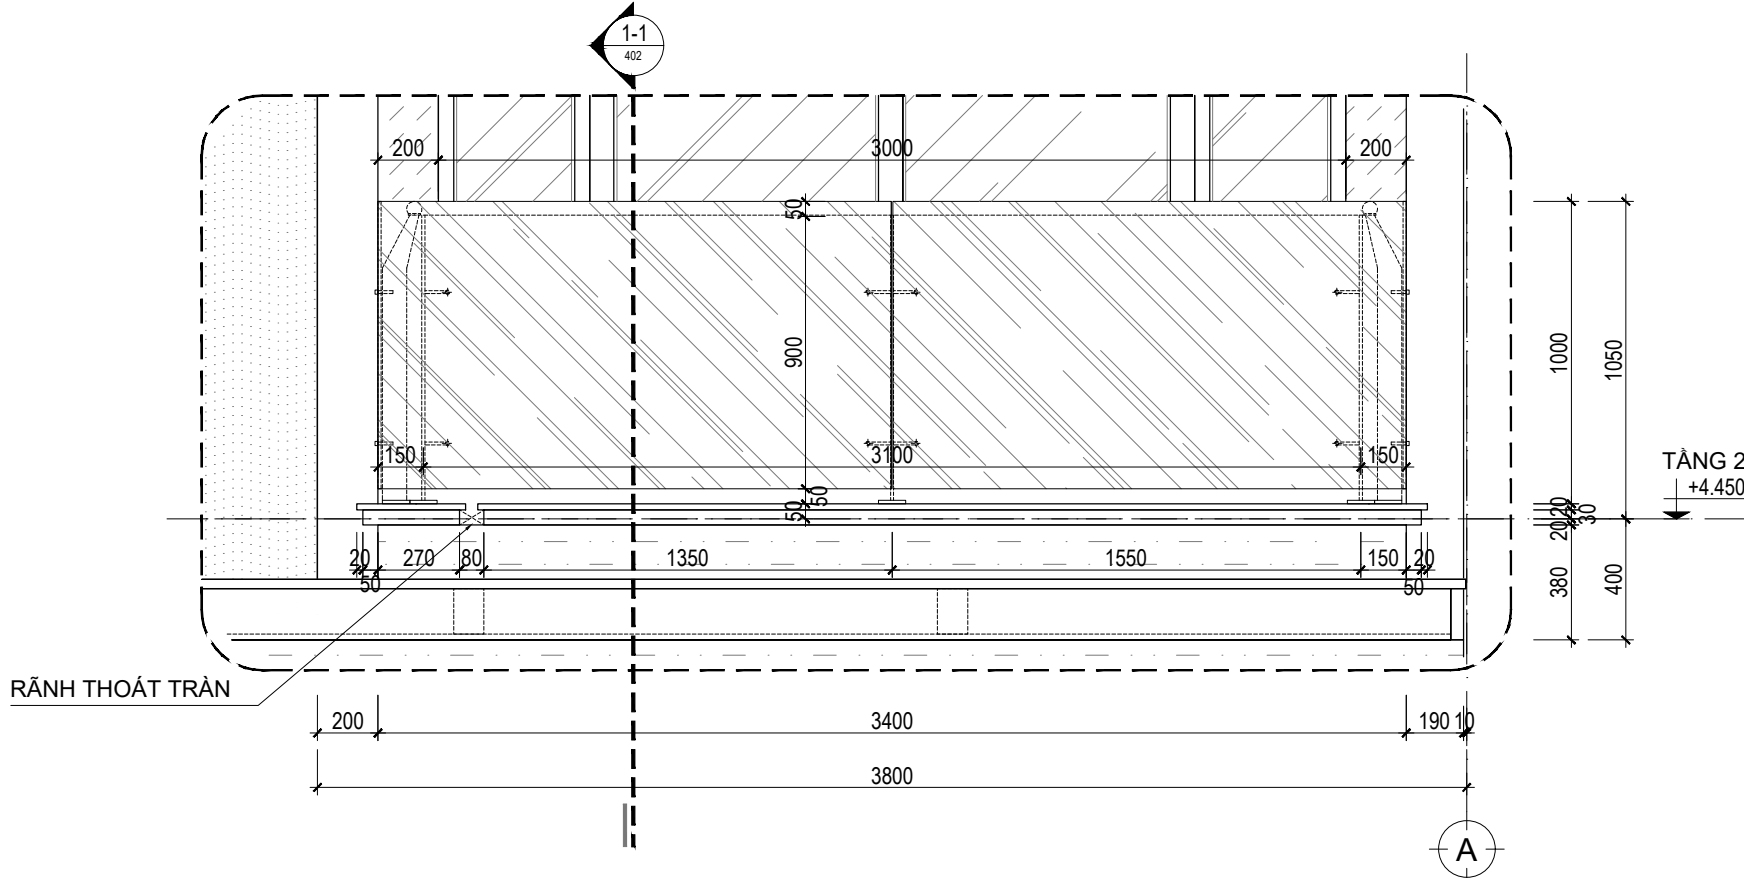


MẶT ĐỨNG BAN CÔNG TẦNG 2 ĐIỂN HÌNH_TL:1/25

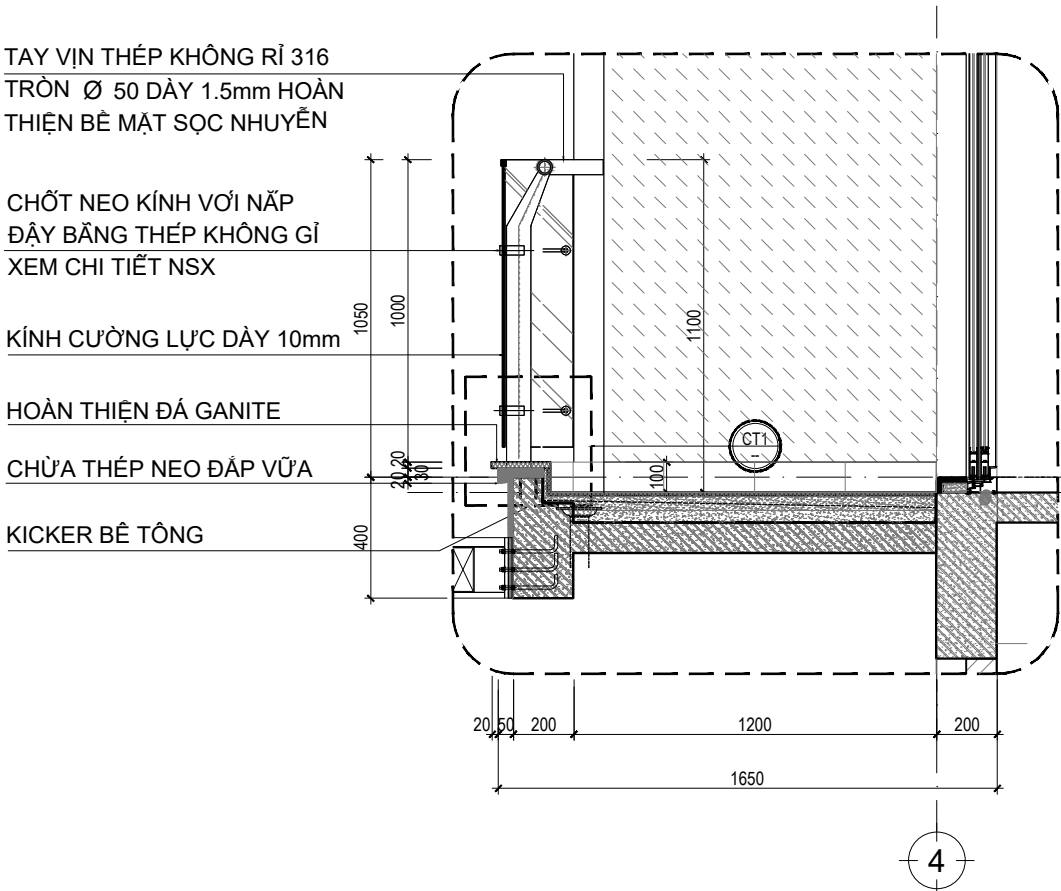


MC 1-1 BAN CÔNG TẦNG 2_TL:1/25

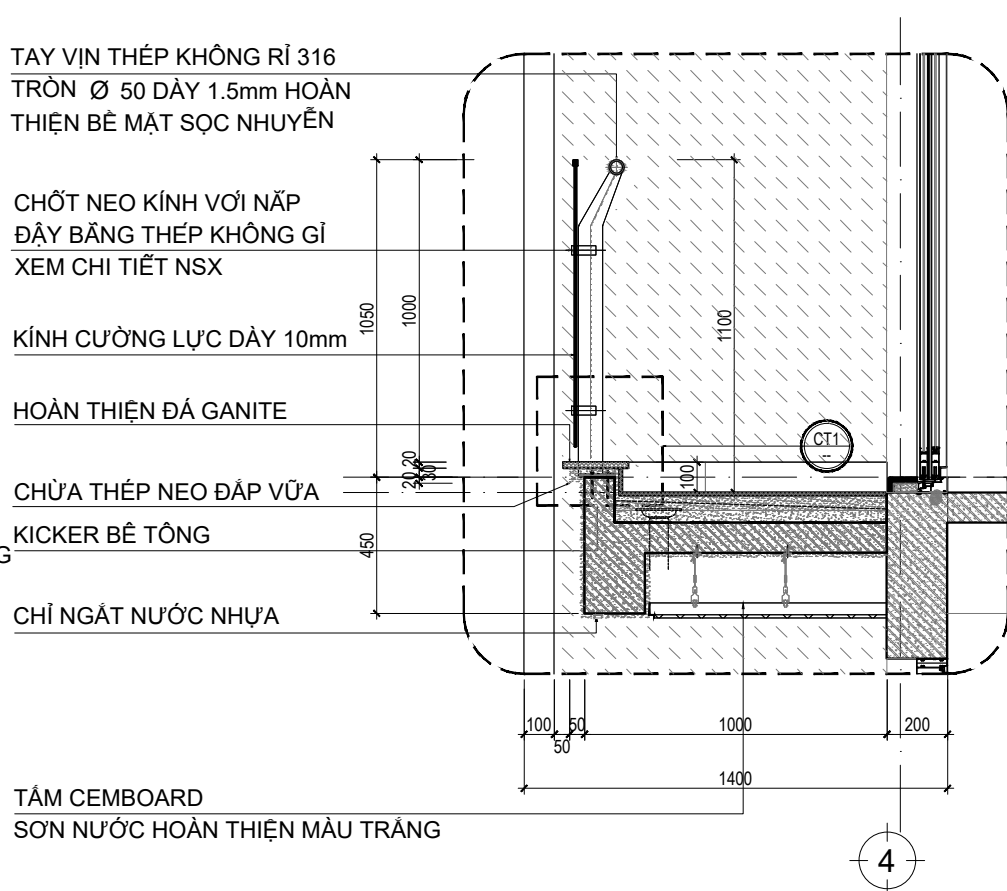

MC 2-2 BAN CÔNG TẦNG 3_TL:1/25

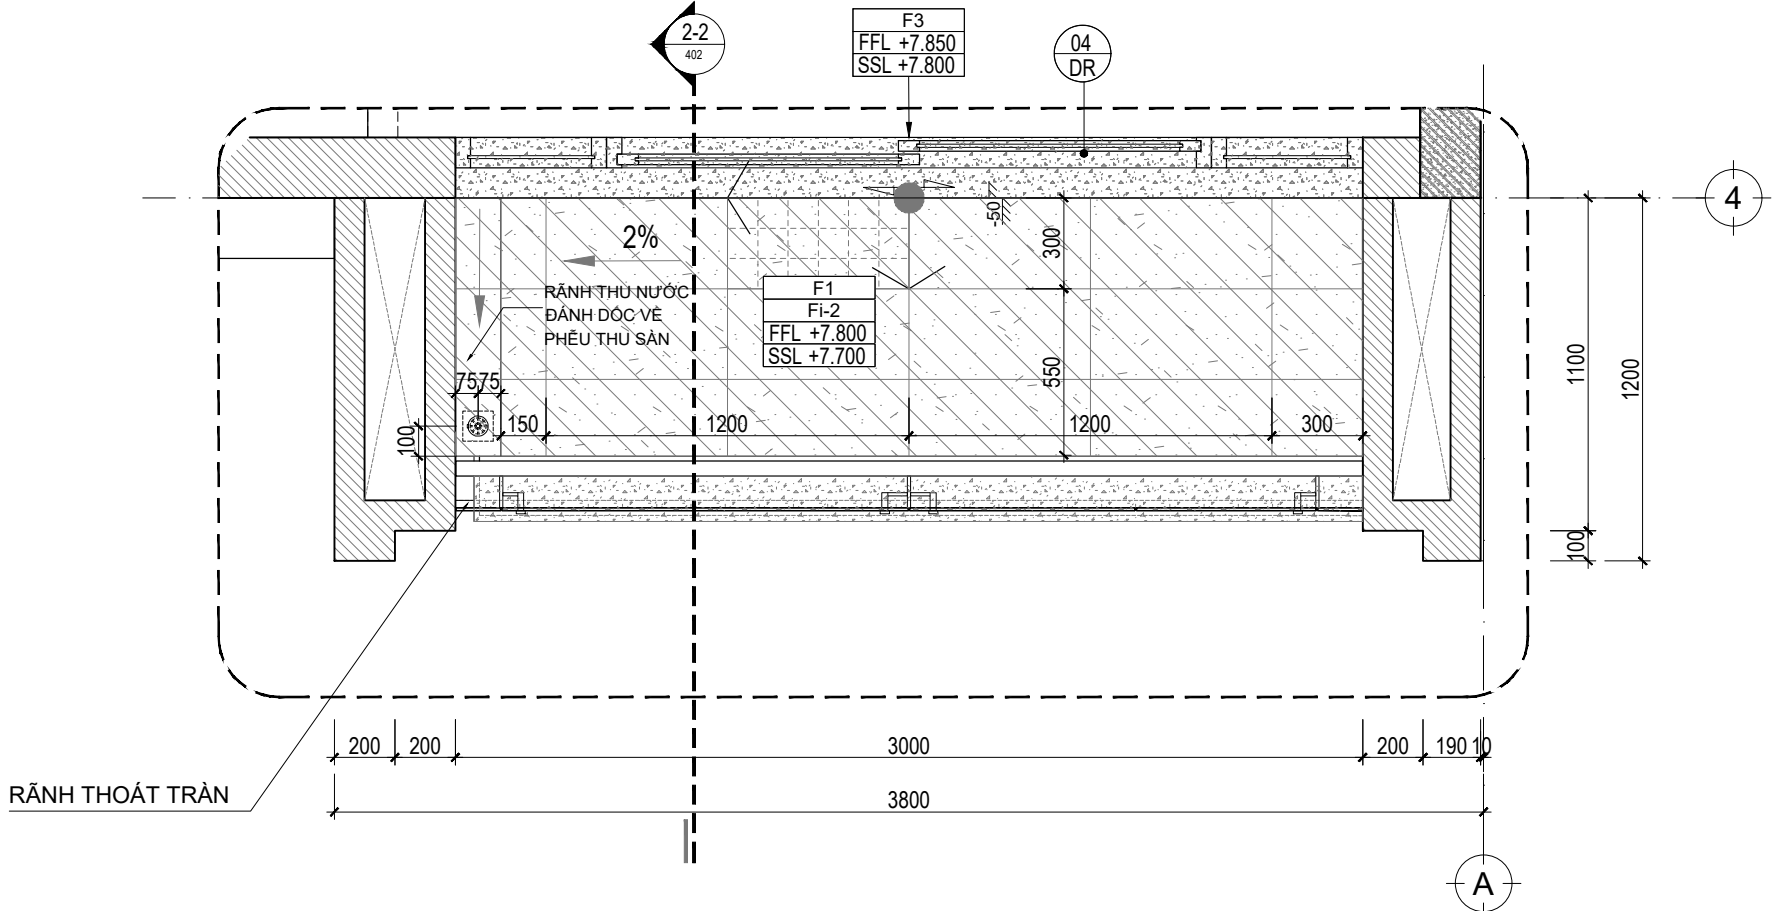


MẶT BẰNG BAN CÔNG TẦNG 3 ĐIỂN HÌNH_TL:1/25

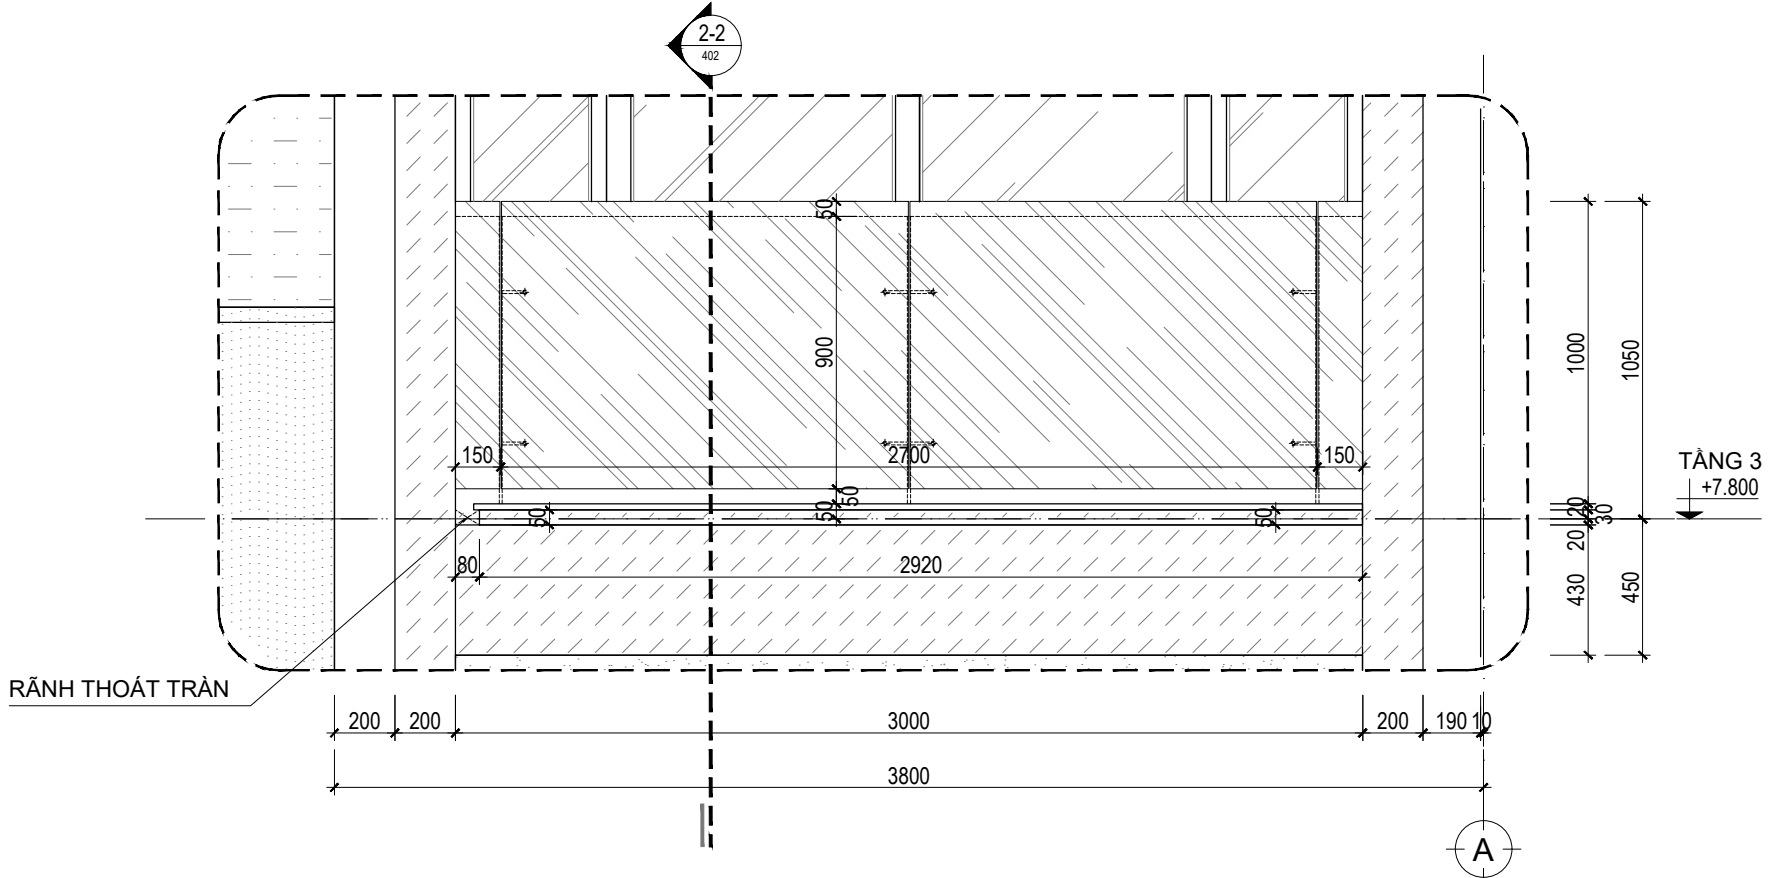

MẶT ĐỨNG BAN CÔNG TẦNG 3 ĐIỂN HÌNH_TL:1/25

THÔNG KÊ LAN CAN TẦNG 2

KÝ HIỆU	SL-01
KÍCH THƯỚC	(2x300+3400)x1000
SỐ LƯỢNG	02
VẬT LIỆU	THANH CHỐNG ĐỪNG INOX 316 DÂY 16mm - HOÀN THIỆN MỜ TAY Vịn INOX 316 TRÒN ø50 DÂY 1.5mm - HOÀN THIỆN MỜ KÍNH CƯỜNG LỰC DÂY 10MM HOẶC TƯƠNG ĐƯƠNG THEO NSX
VỊ TRÍ	TẦNG 2

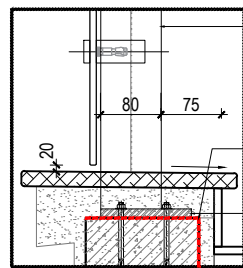


THANH CHỐNG ĐỪNG THÉP KHÔNG RỈ 80x10mm HOÀN THIỆN BỀ MẶT SỌC NHUYỄN

MÀNG CHỐNG THẤM XEM BÀN VẼ CẤU TẠO SÀN THÉP BÀN ẦM SÀN LIỀN KẾT VỚI DẦM BTCT BẰNG BU LÔNG NỖ

THÔNG KÊ LAN CAN TẦNG 3

KÝ HIỆU	SL-02
KÍCH THƯỚC	3000x1000
SỐ LƯỢNG	02
VẬT LIỆU	THANH CHỐNG ĐỪNG INOX 316 DÂY 16mm - HOÀN THIỆN MỜ TAY Vịn INOX 316 TRÒN ø50 DÂY 1.5mm - HOÀN THIỆN MỜ KÍNH CƯỜNG LỰC DÂY 10MM HOẶC TƯƠNG ĐƯƠNG THEO NSX
VỊ TRÍ	TẦNG 3

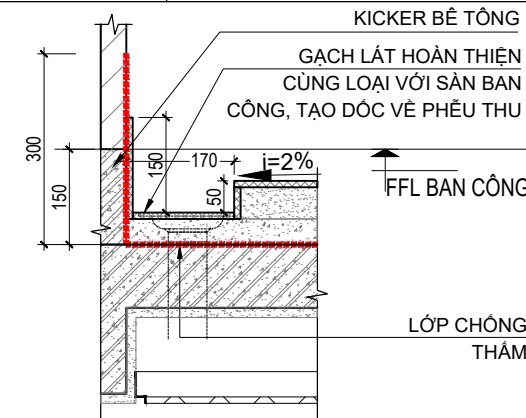


CHI TIẾT 1


GHI CHÚ: CAO ĐỘ ±0.00 TRONG BẢN VẼ TƯƠNG ỨNG CAO ĐỘ HỒN ĐẦU TẠI VĨA HÉ. CAO ĐỘ VĨA HÉ VUI LÒNG XEM CÁC BẢN VẼ "THIẾT KẾ HẠ TẦNG"

MC 3-3 - CT RĂNG THU NƯỚC


CHI TIẾT CẦU THANG

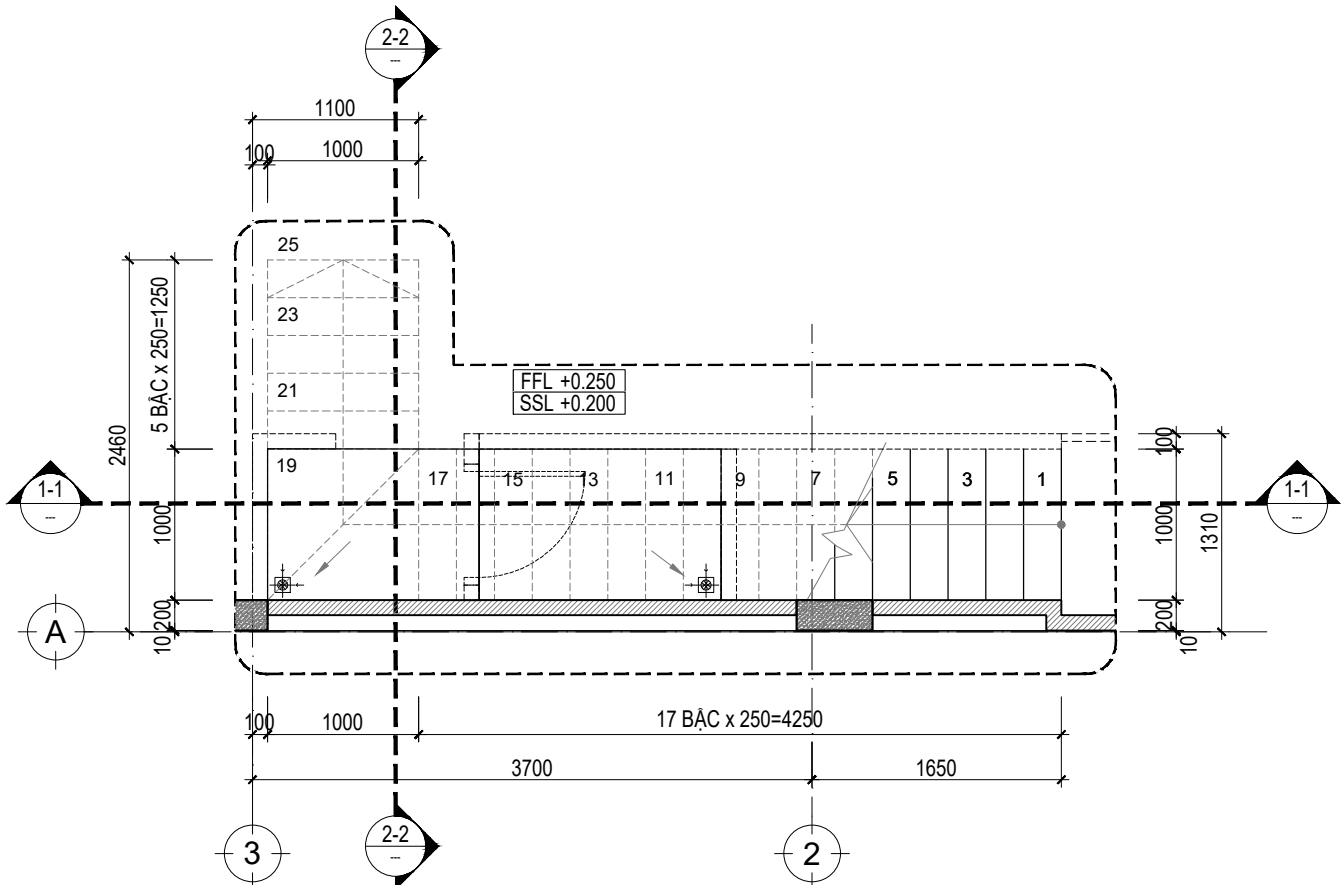


MẶT BẰNG THANG TẦNG 1_TL:1/50

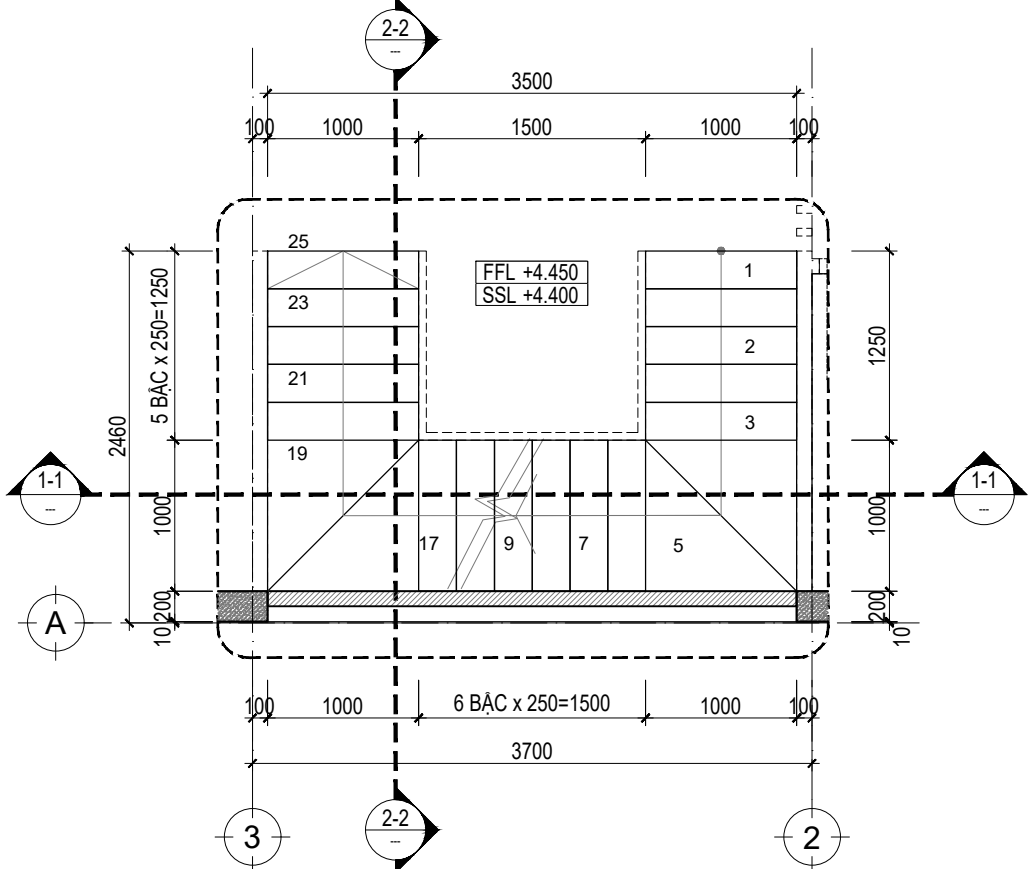


MẶT BẰNG THANG TẦNG 2_TL:1/50

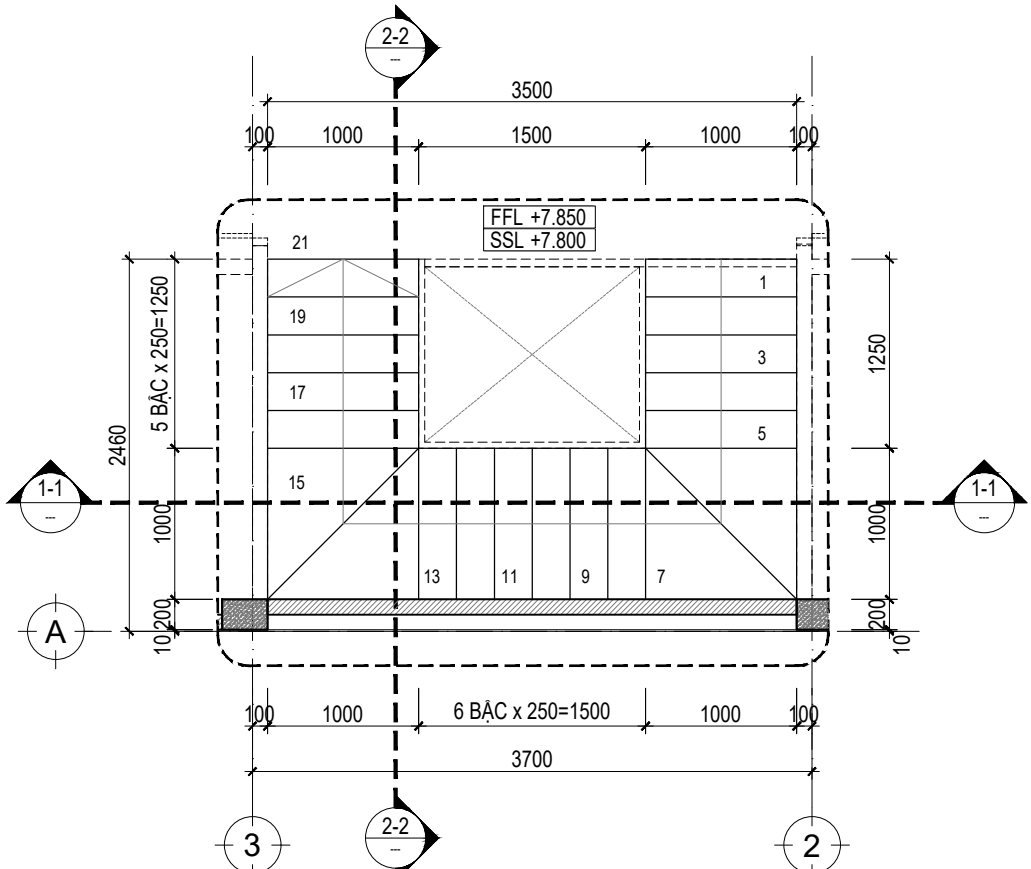


MẶT BẰNG THANG TẦNG 3_TL:1/50

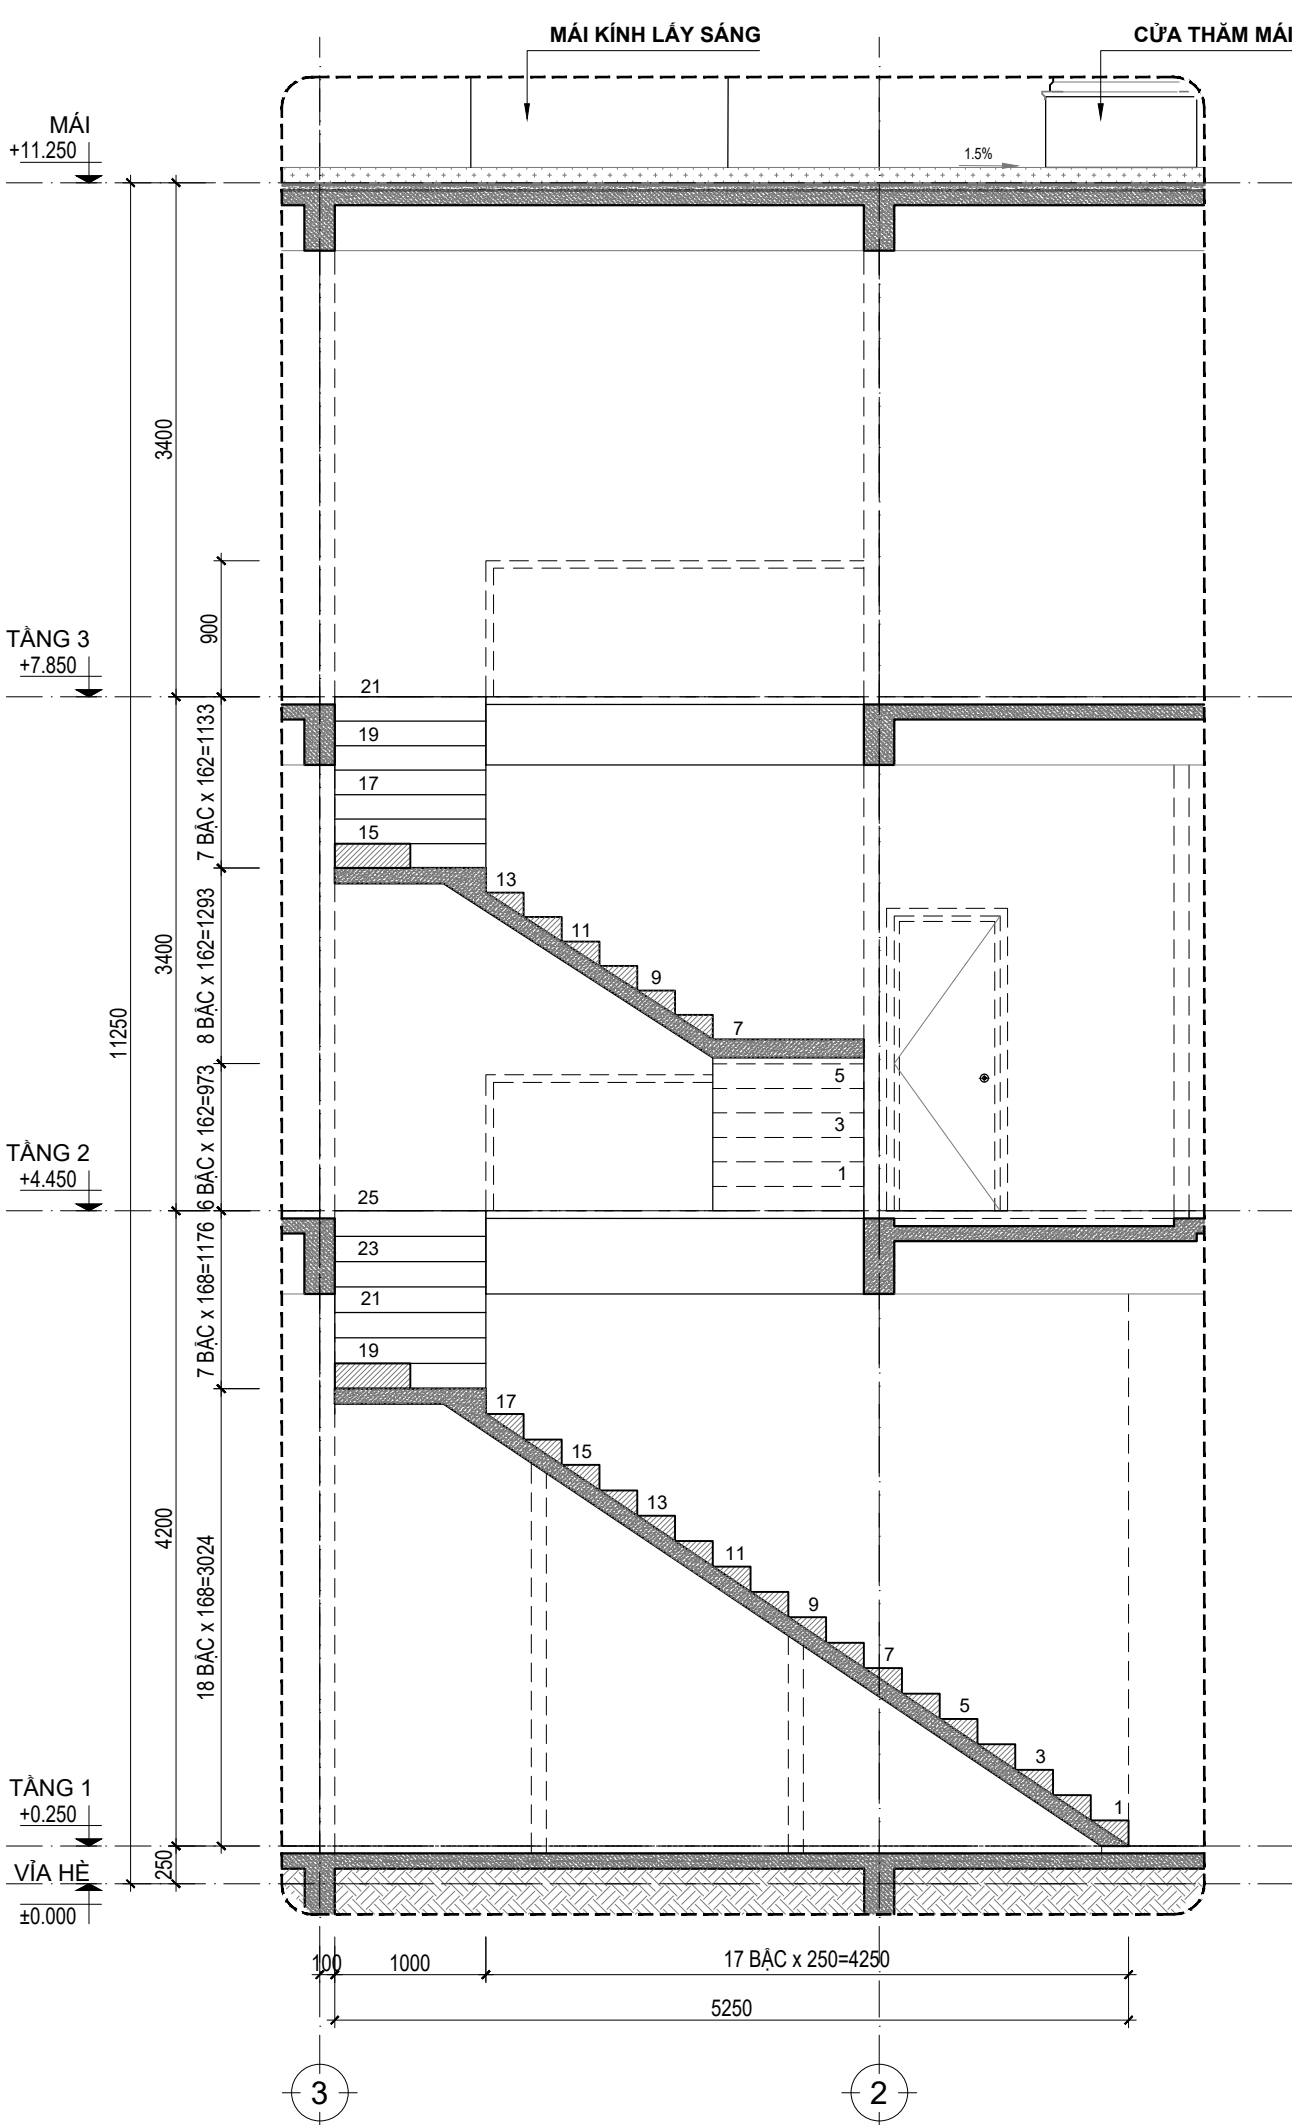

MẶT CẮT 1-1_TL:1/50

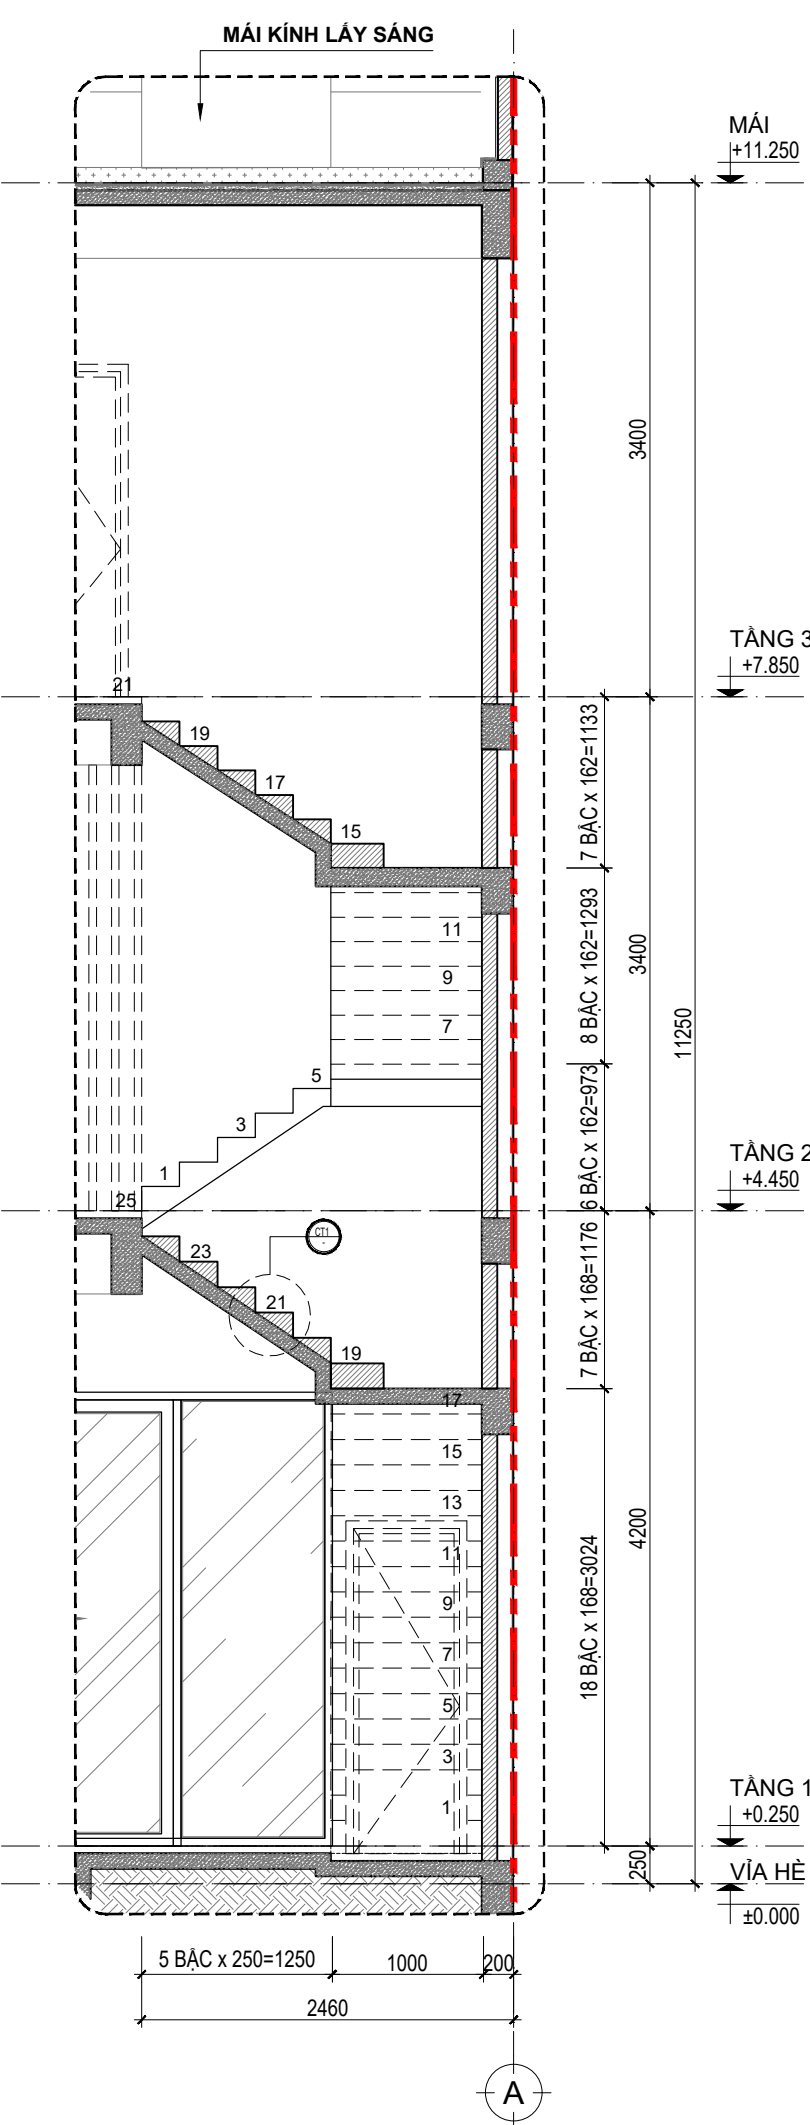


MẶT CẮT 2-2_TL:1/50

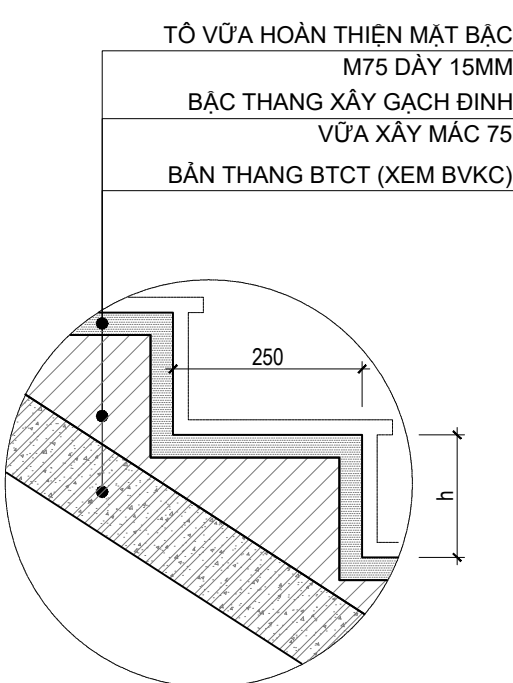


CHI TIẾT 1_TL:1/10

GHI CHÚ: CAO ĐỘ ±0.00 TRONG BẢN VẼ TƯƠNG ỨNG CAO ĐỘ HÒN DẦU TẠI VÍA HÈ. CAO ĐỘ VÍA HÈ VUI LÒNG XEM CÁC BẢN VẼ "THIẾT KẾ HẠ TẦNG"


CHI TIẾT MÁI ĐÓN

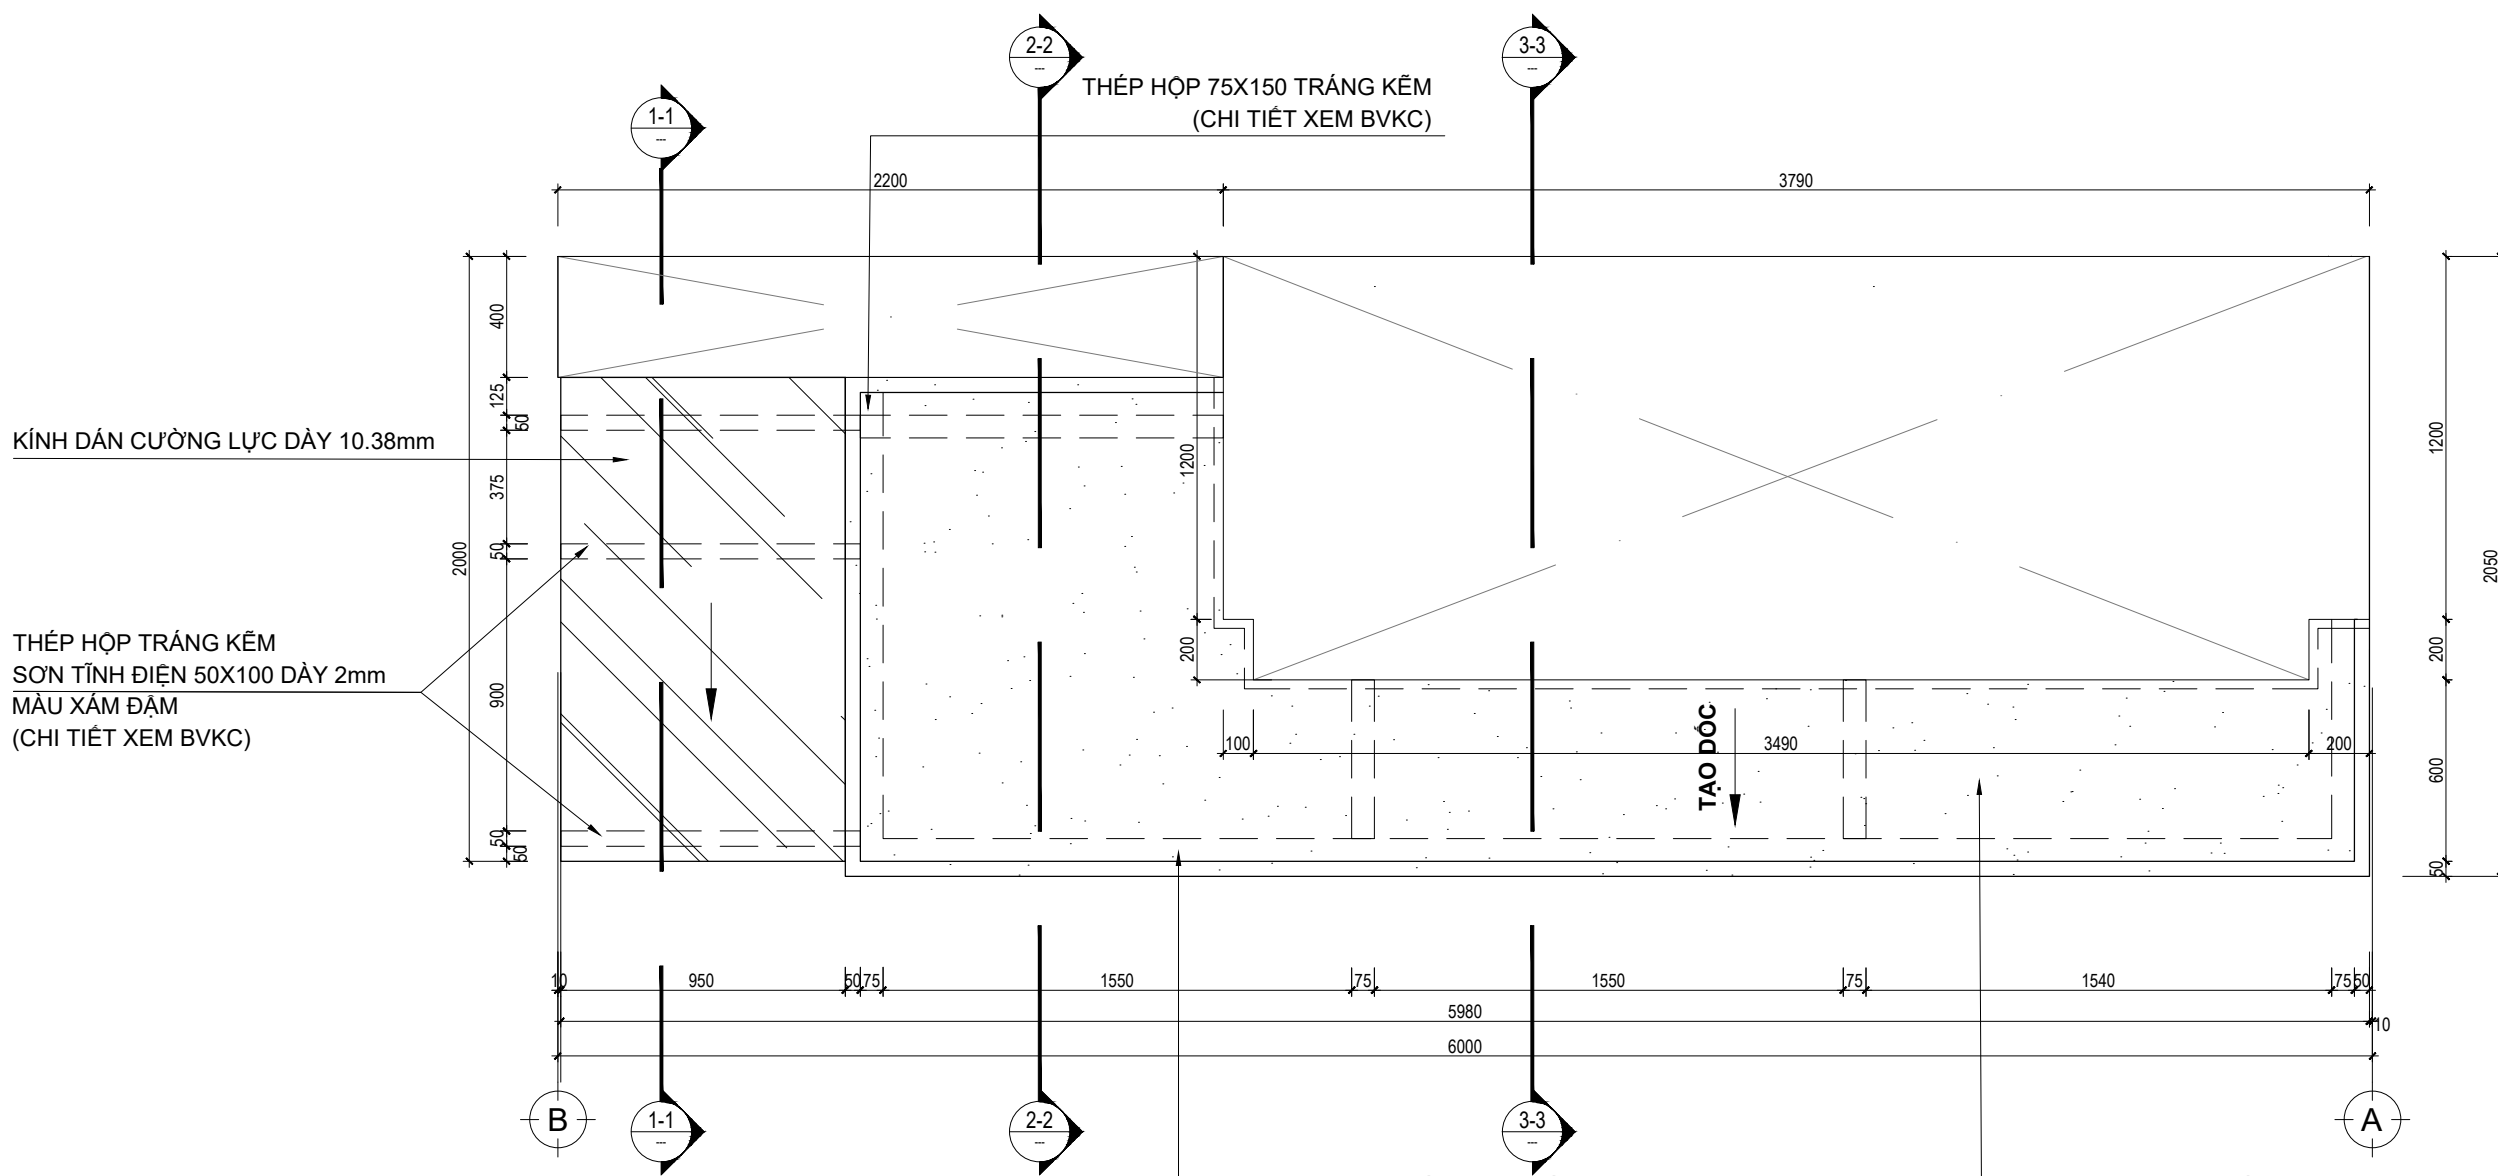





CHI TIẾT MẶT BẰNG MÁI ĐÓN TRỤC B-A_TL: 1/25

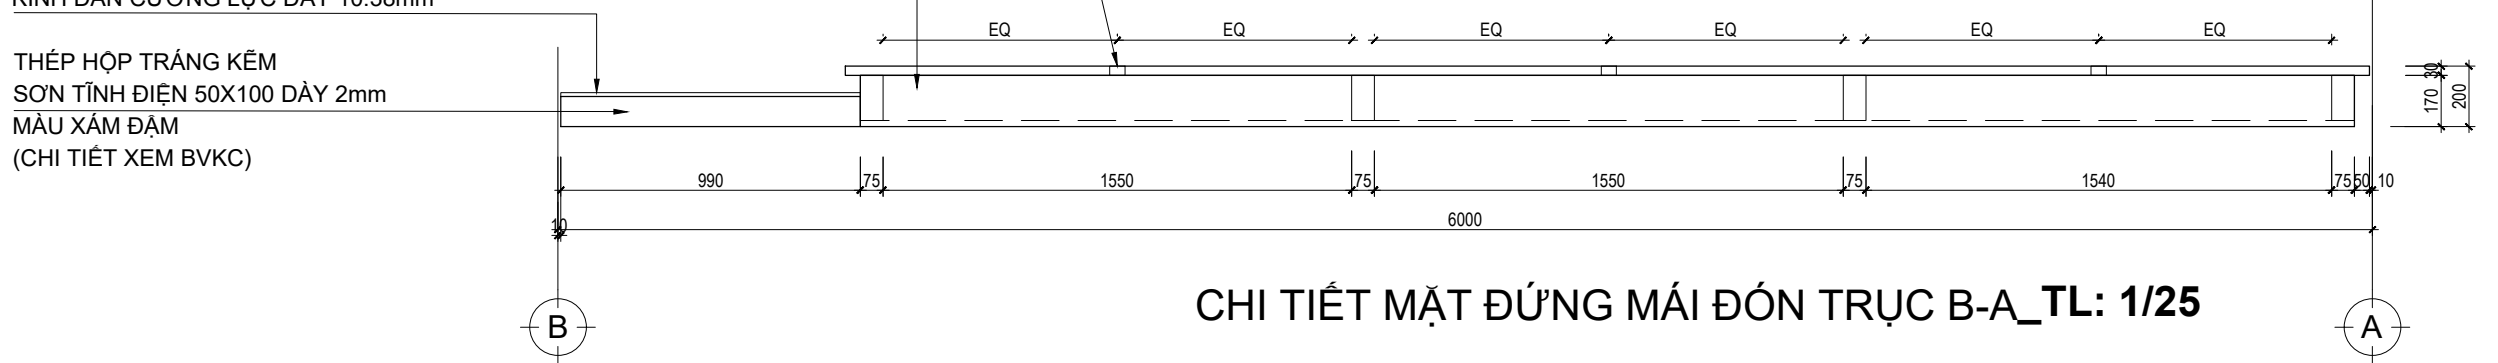

CHI TIẾT MẶT ĐỪNG MÁI ĐÓN TRỤC B-A_TL: 1/25

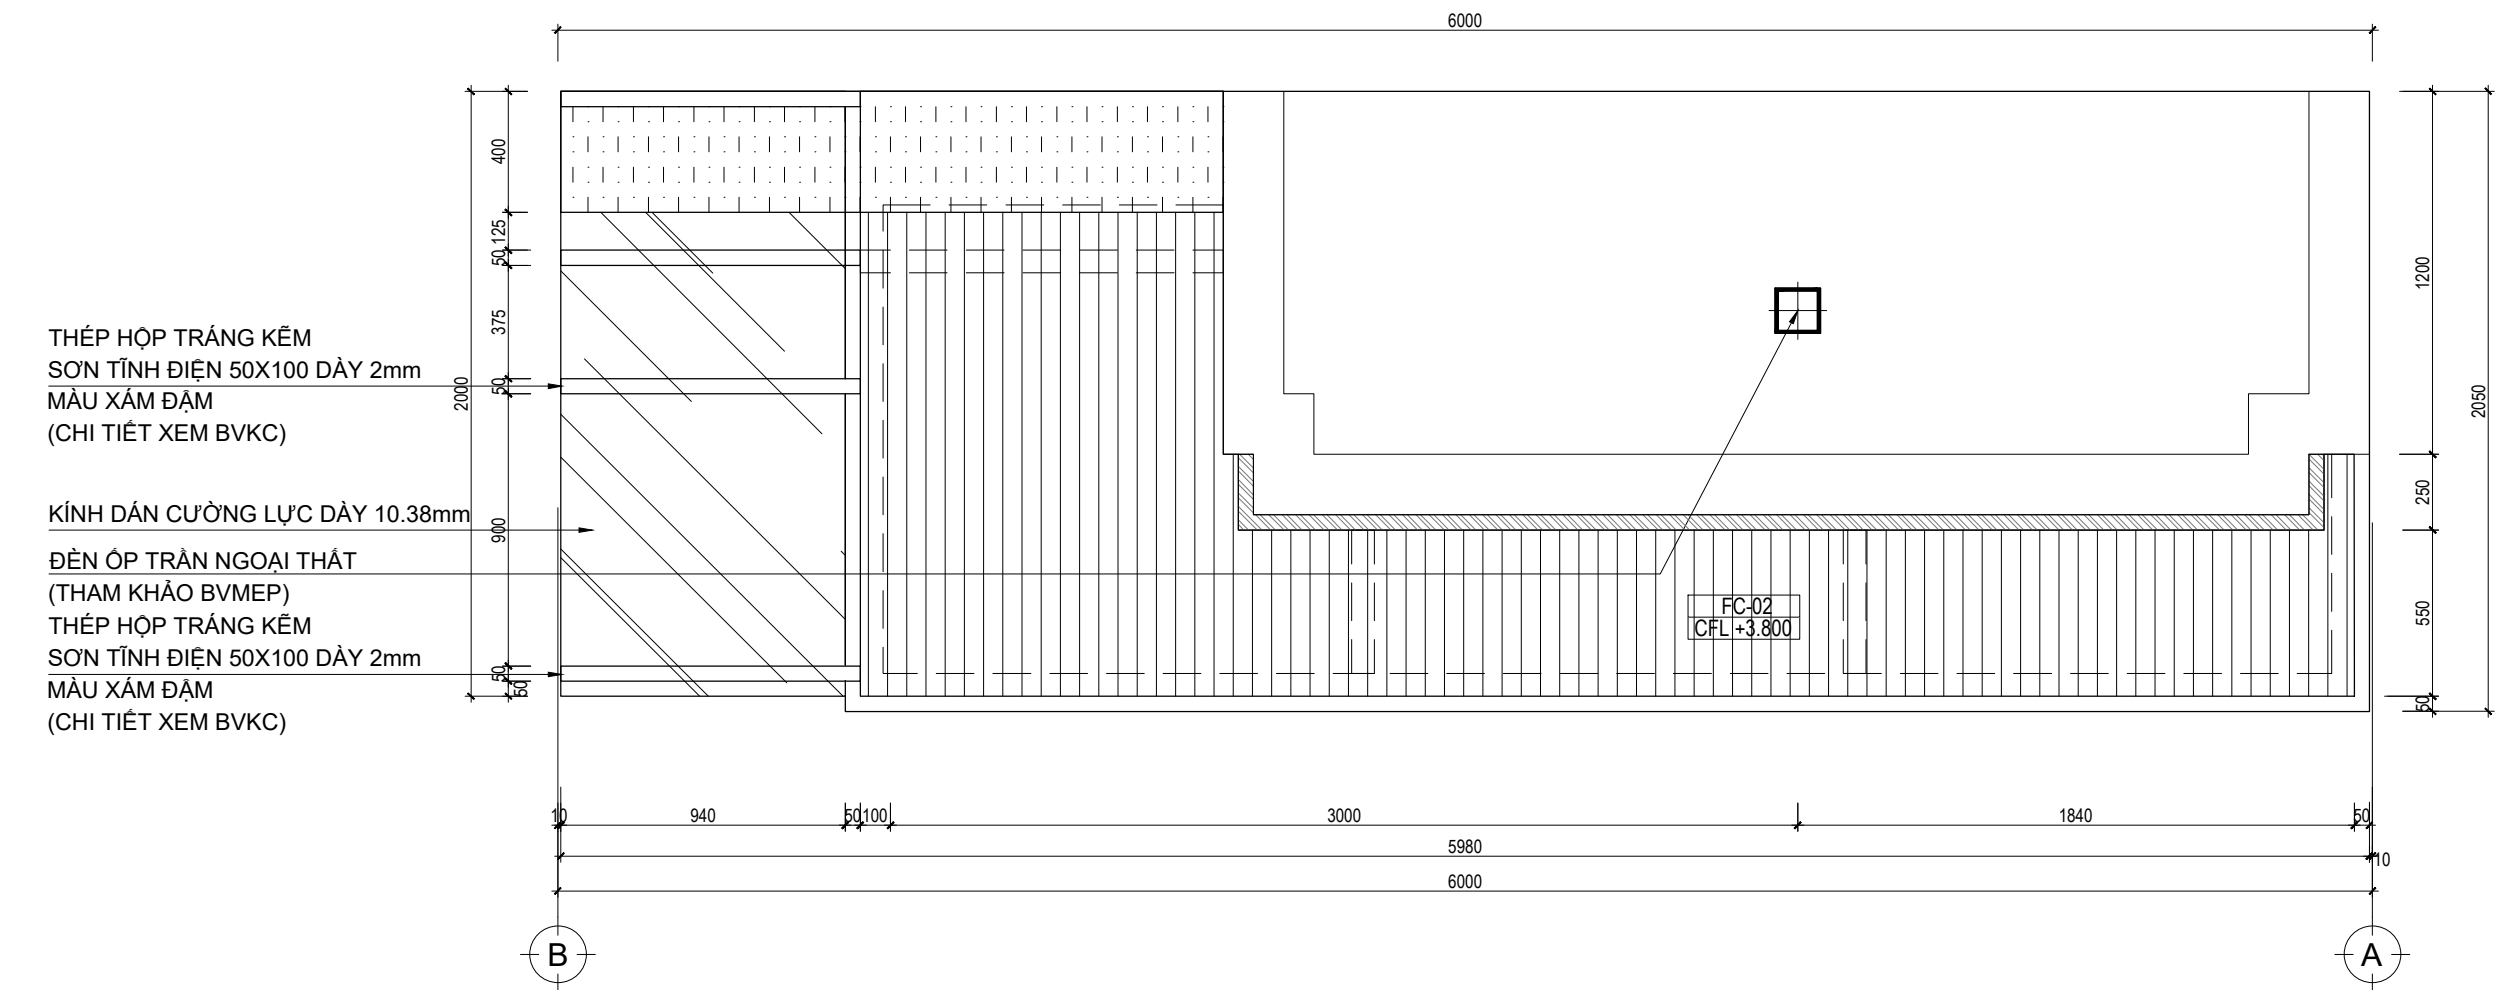


CHI TIẾT MẶT BẰNG TRẦN MÁI ĐÓN TRỤC B-A_TL: 1/25

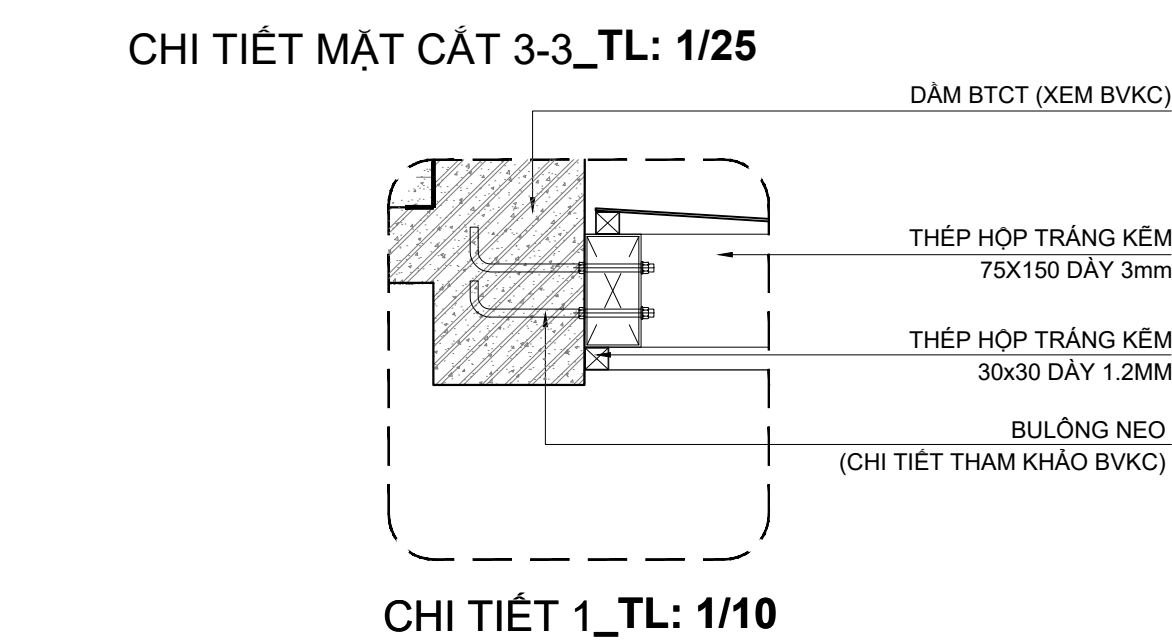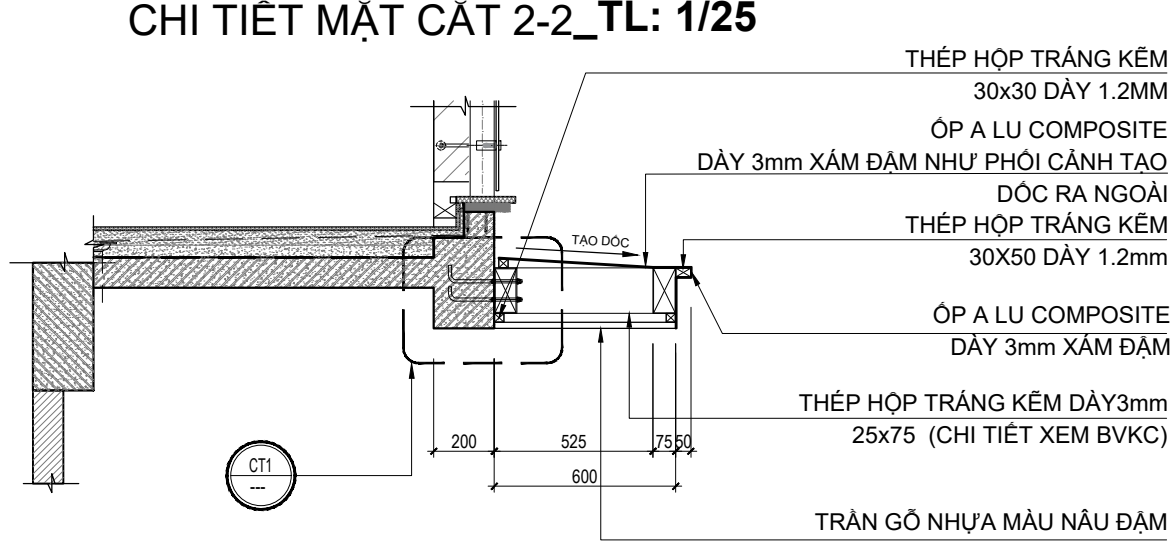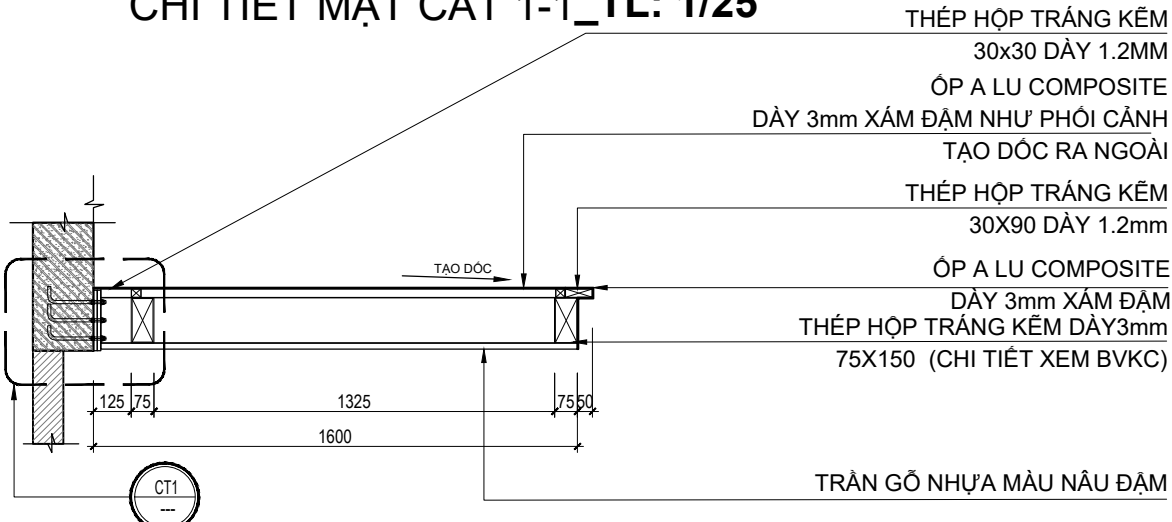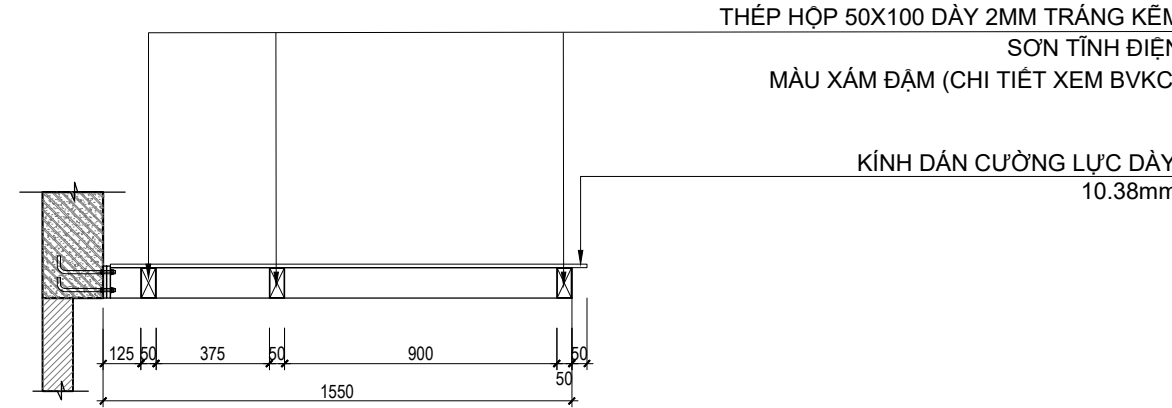

VẬT LIỆU HOÀN THIỆN TRẦN	
KÝ HIỆU	MÔ TẢ
FC-01	TRẦN CEMBOARD HOÀN THIỆN SƠN NƯỚC MÀU TRẮNG
FC-02	TRẦN GỖ NHỰA MÀU NÂU ĐÀM
FC-03	TRẦN ĐÉ THỎ

ĐÈN NGOẠI THẤT	
KÝ HIỆU	MÔ TẢ
ĐÈN ÁP TRẦN NGOẠI THẤT, 12W, ÁNH SÁNG 3700K	
ĐÈN GẮN TƯỜNG NGOẠI THẤT ÁNH SÁNG 3700K, CÔNG SUẤT 15W	
ĐÈN TRỤ CỐNG ÁNH SÁNG 3000K, CÔNG SUẤT 9W	


CHI TIẾT MÁI ĐÓN

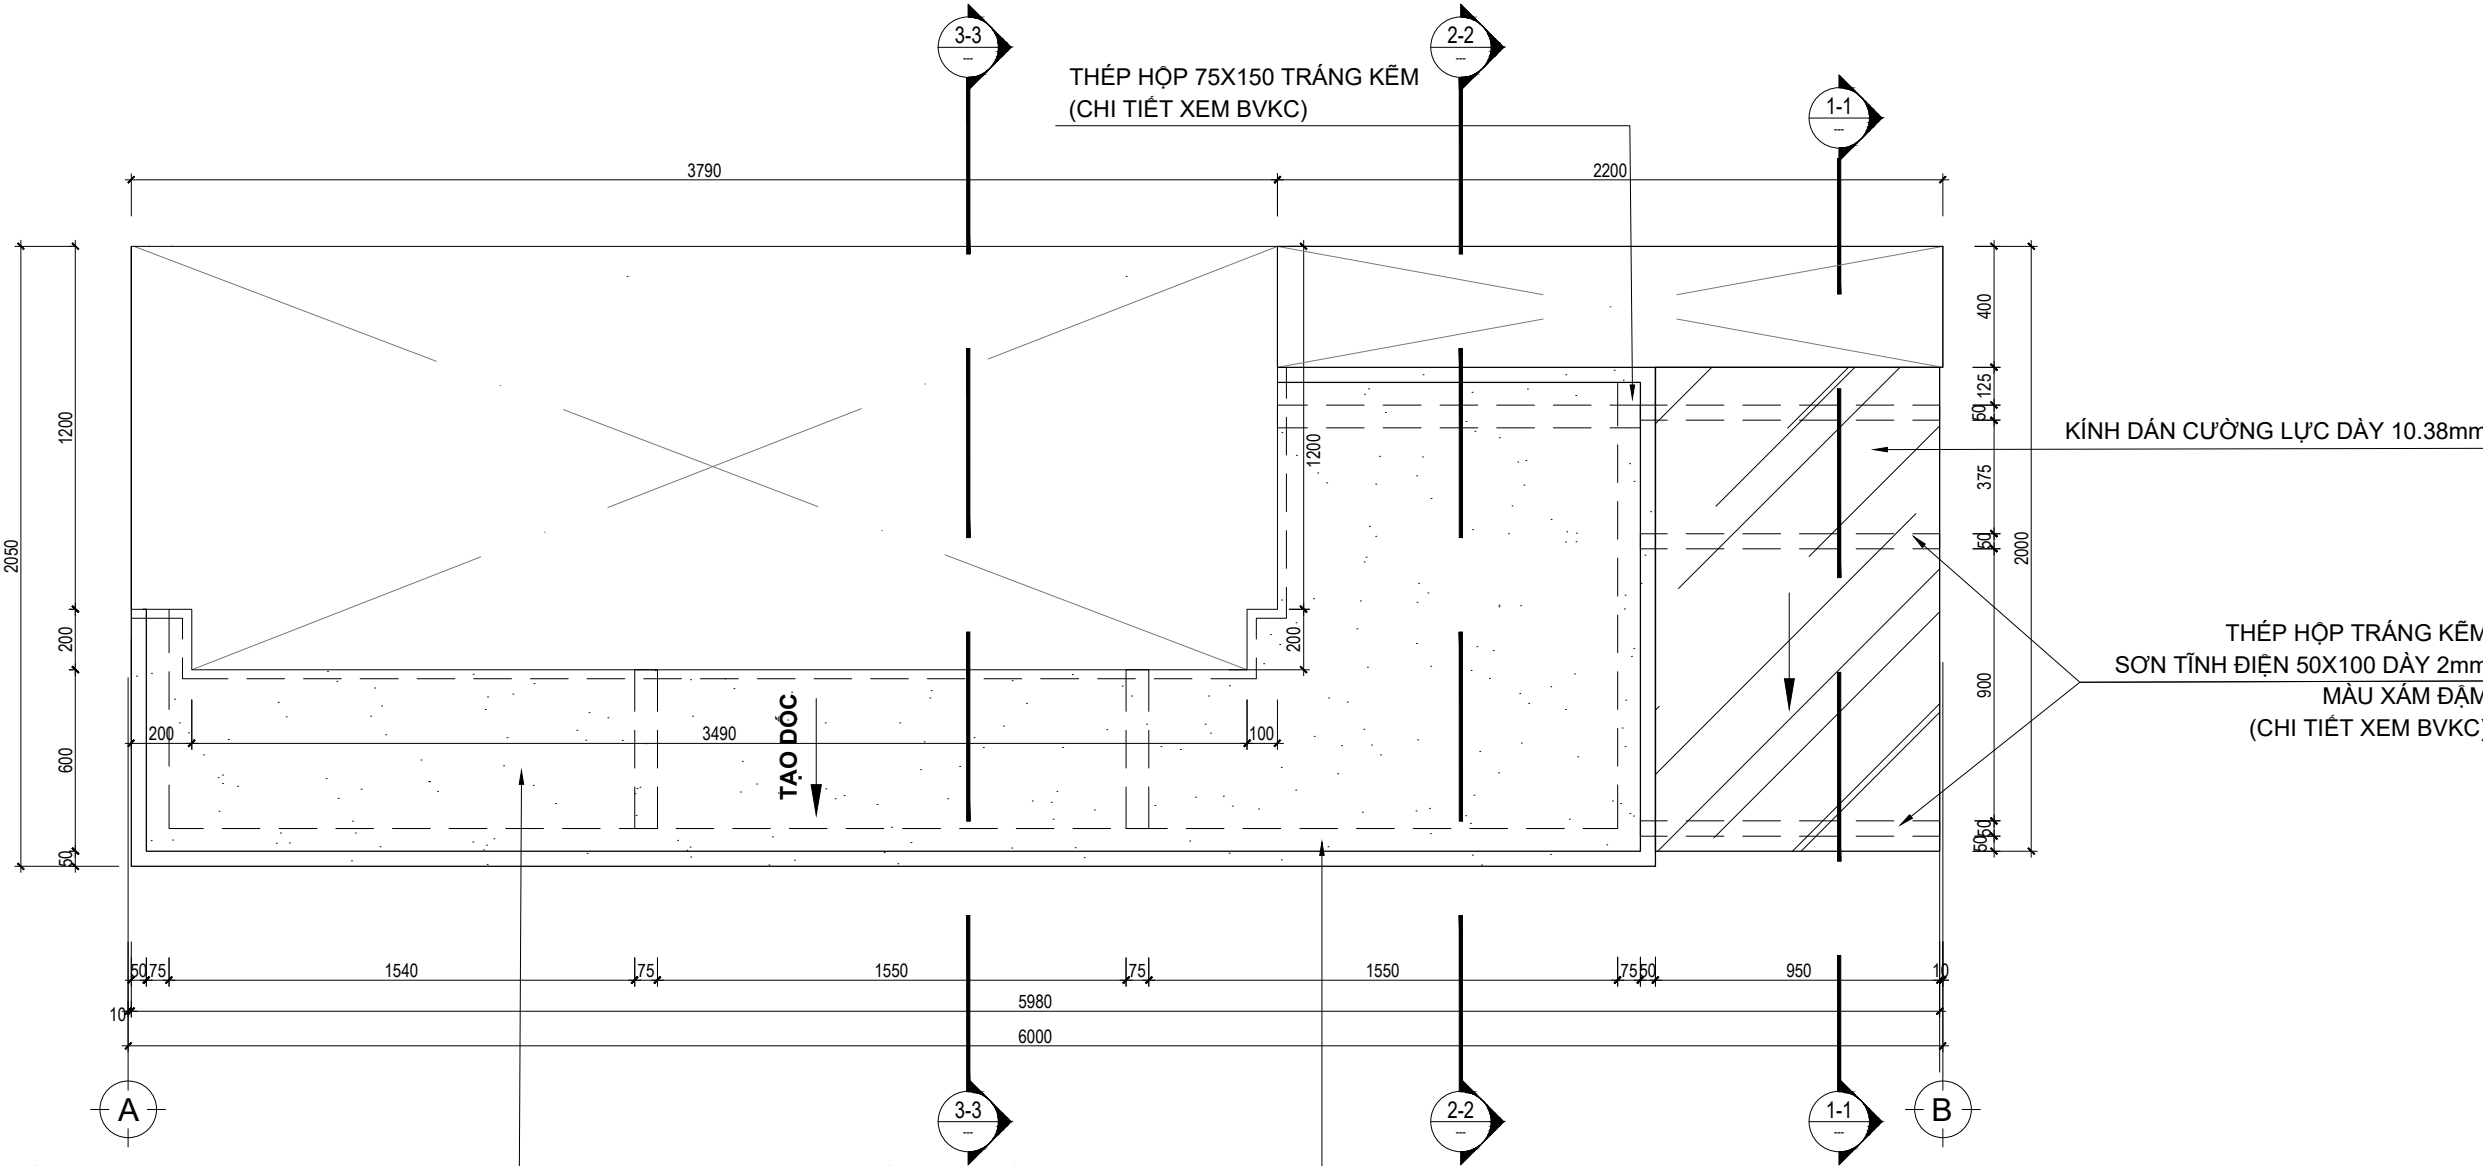

CHI TIẾT MẶT BẰNG MÁI ĐÓN TRỰC A-B_TL: 1/25


CHI TIẾT MẶT ĐỨNG MÁI ĐÓN TRỰC A-B_TL: 1/25

CHI TIẾT MẶT BẰNG TRẦN MÁI ĐÓN TRỰC A-B_TL: 1/25

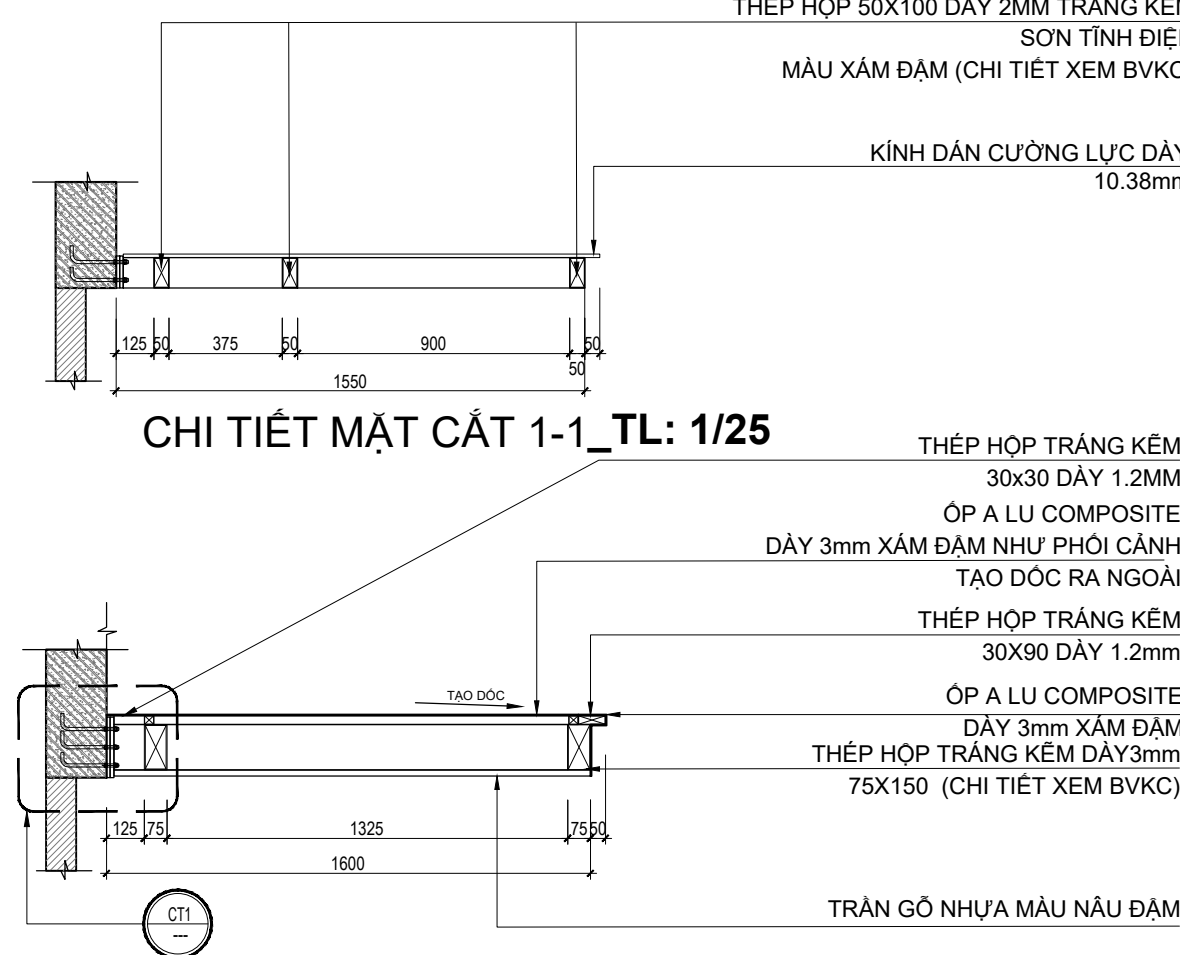

CHI TIẾT MẶT CẮT 2-2_TL: 1/25






CHI TIẾT MẶT CẮT 3-3_TL: 1/25

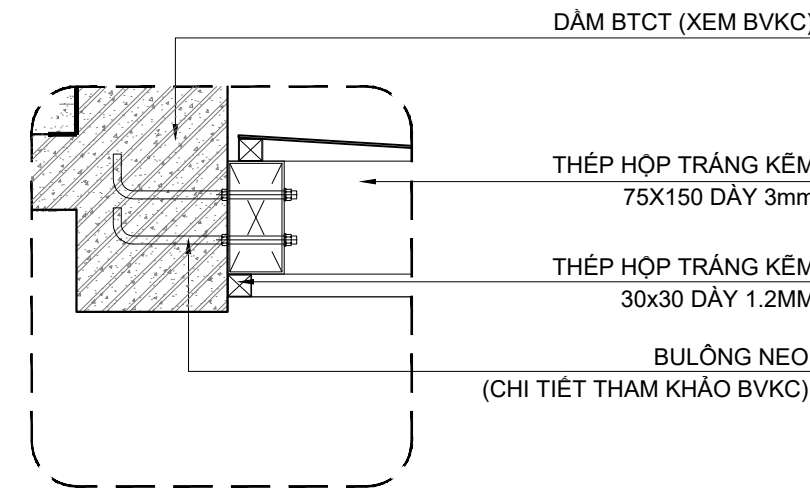


CHI TIẾT 1_TL: 1/10

VẬT LIỆU HOÀN THIỆN TRẦN		
KÝ HIỆU	MÔ TẢ	
FC-01	TRẦN CEMBOARD HOÀN THIỆN SON NƯỚC MÀU TRẮNG	
FC-02	TRẦN GỖ NHỰA MÀU NÂU ĐẬM	
FC-03	TRẦN ĐÉ THỎ	


ĐÈN NGOẠI THẤT	
KÝ HIỆU	MÔ TẢ
□	ĐÈN ÁP TRẦN NGOẠI THẤT, 12W, ÁNH SÁNG 3700K
○	ĐÈN GẮN TƯỜNG NGOẠI THẤT ÁNH SÁNG 3700K, CÔNG SUẤT 15W
⊙	ĐÈN TRỤ CÔNG ÁNH SÁNG 3000K, CÔNG SUẤT 9W

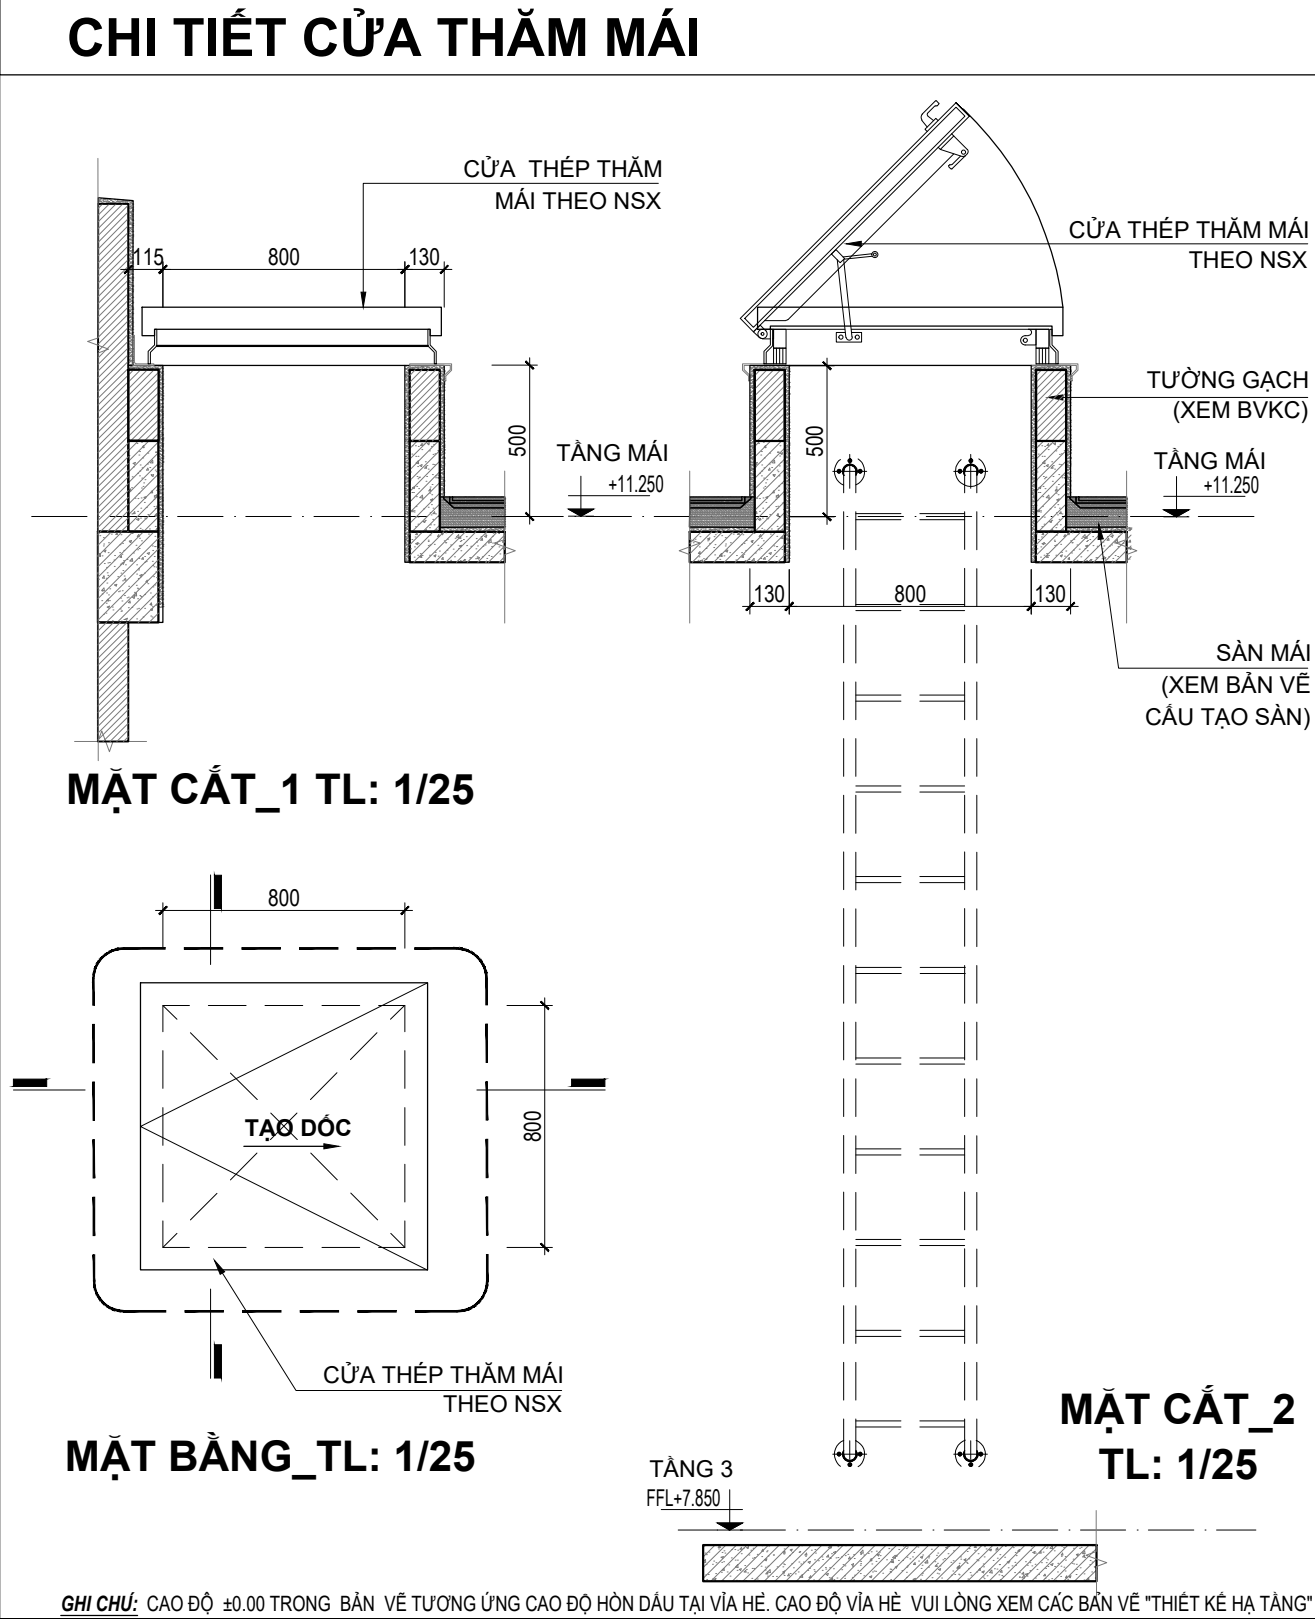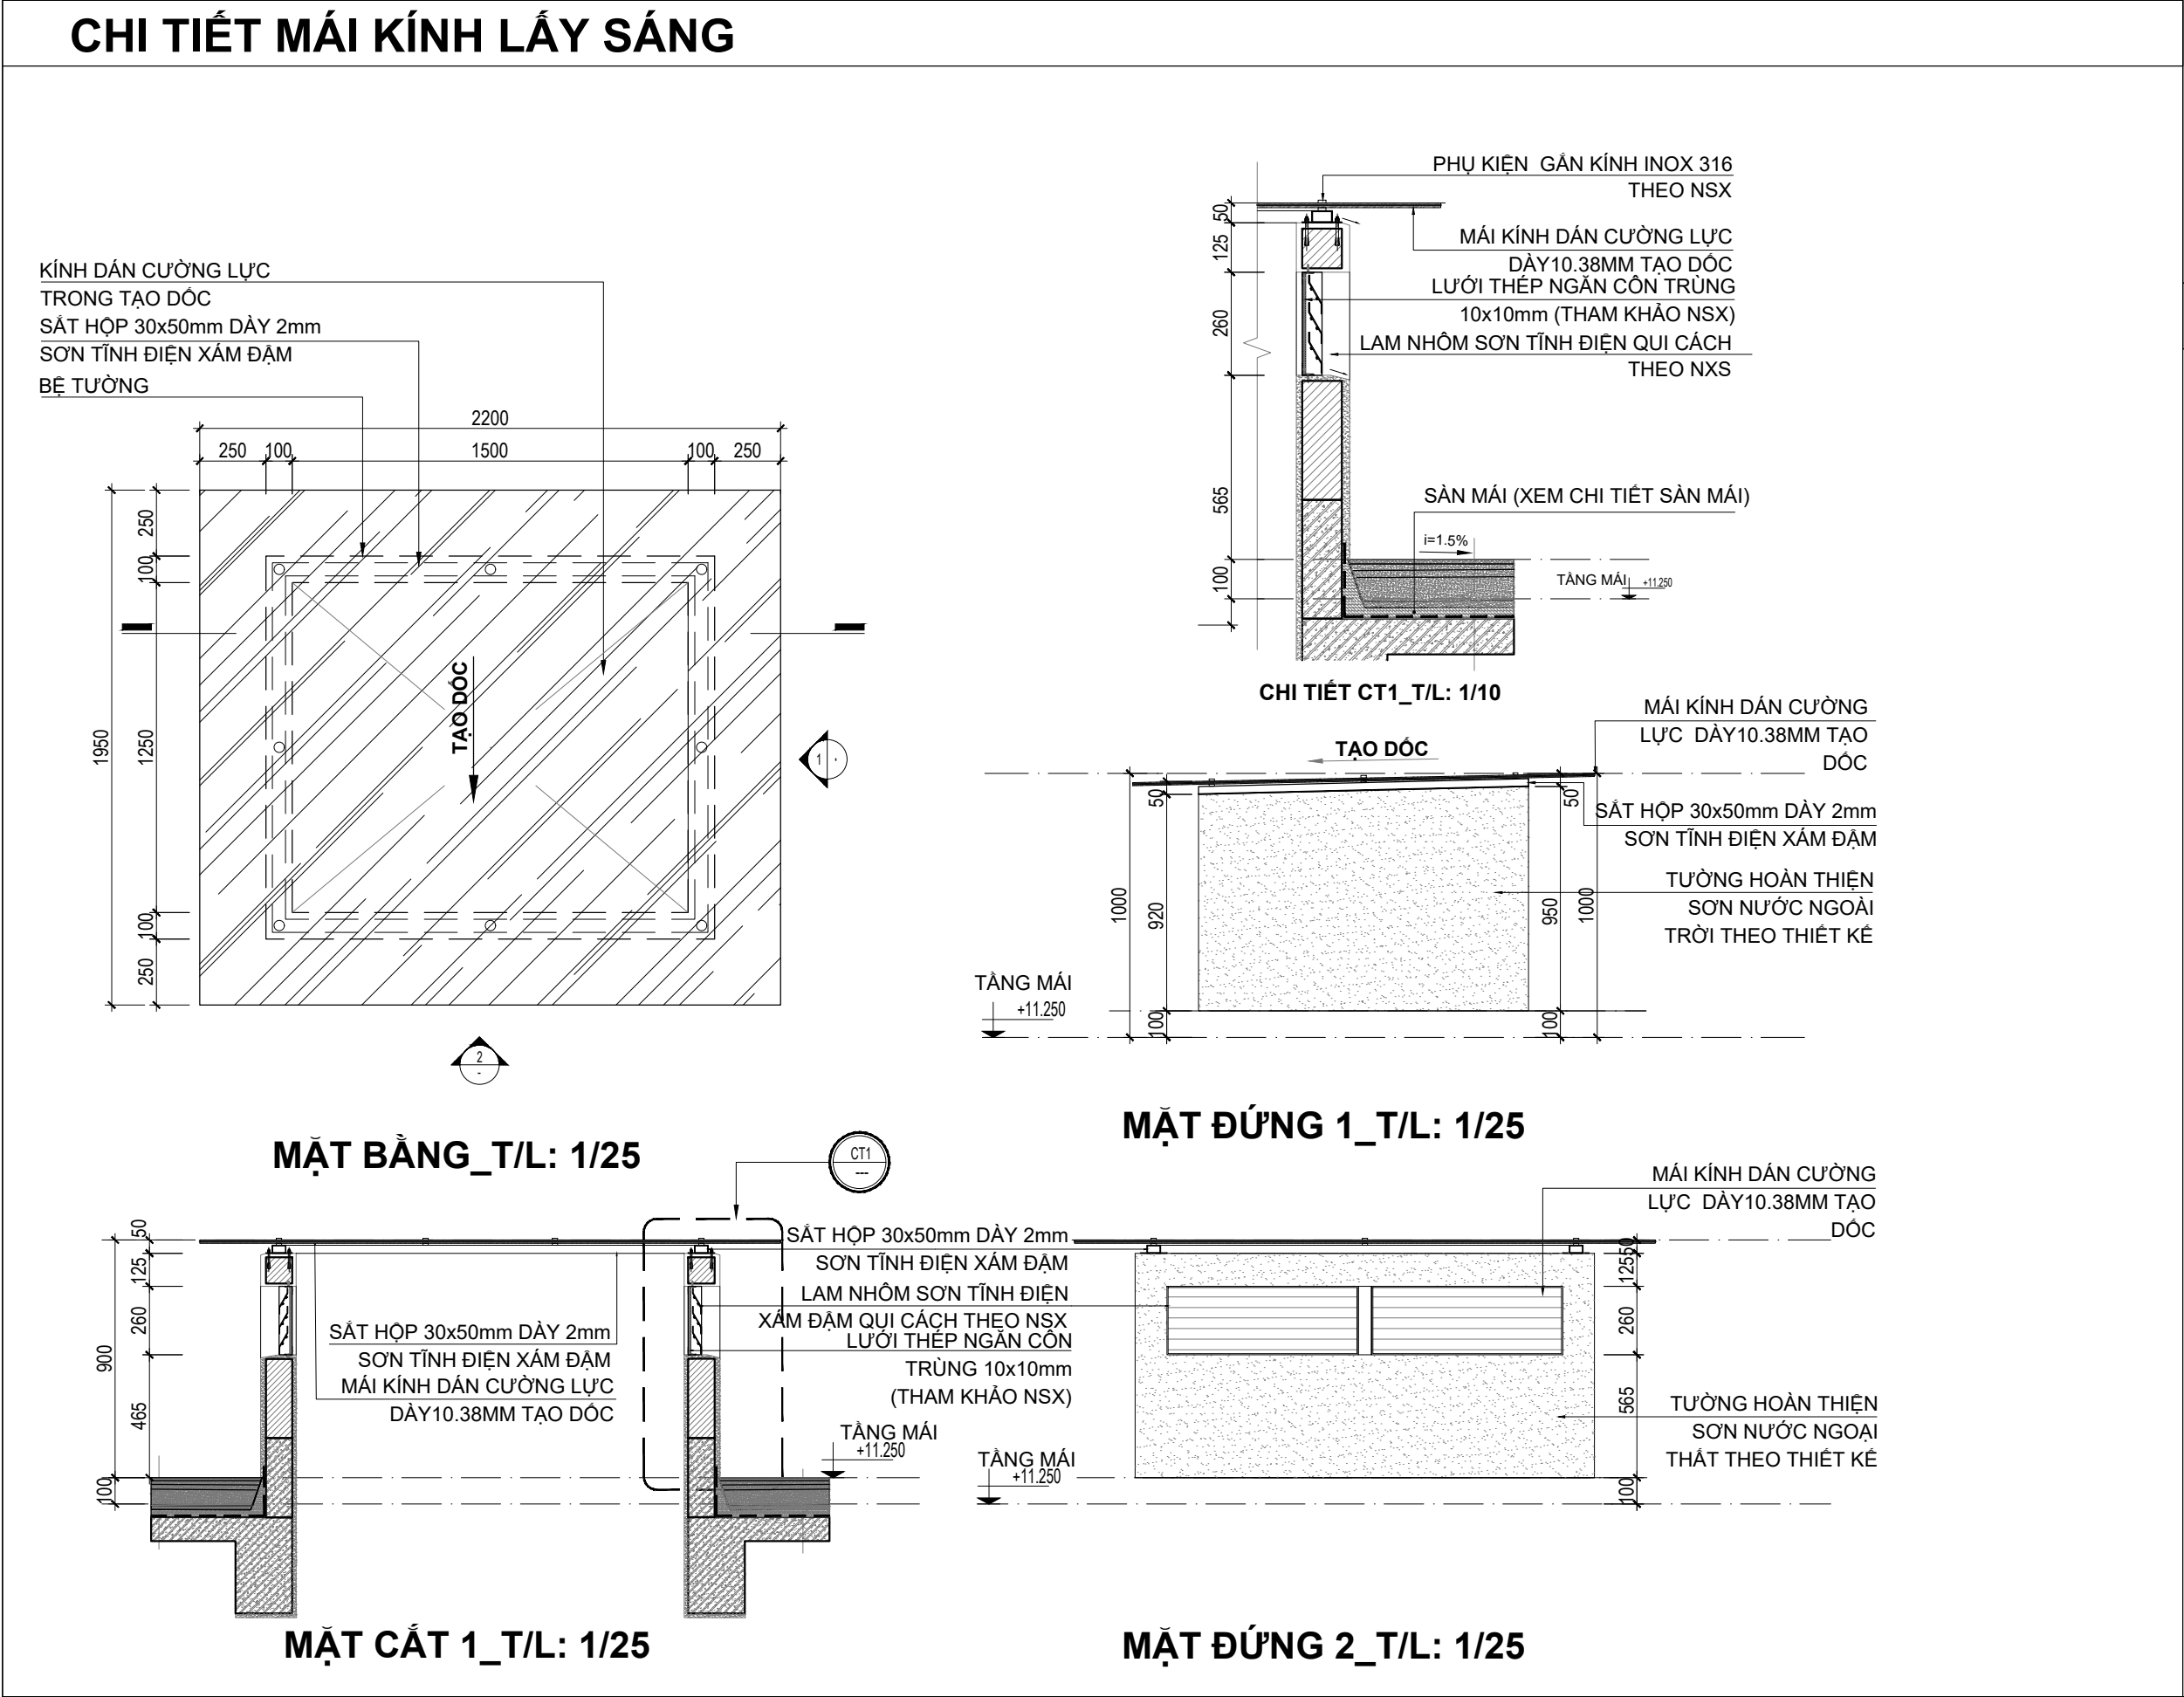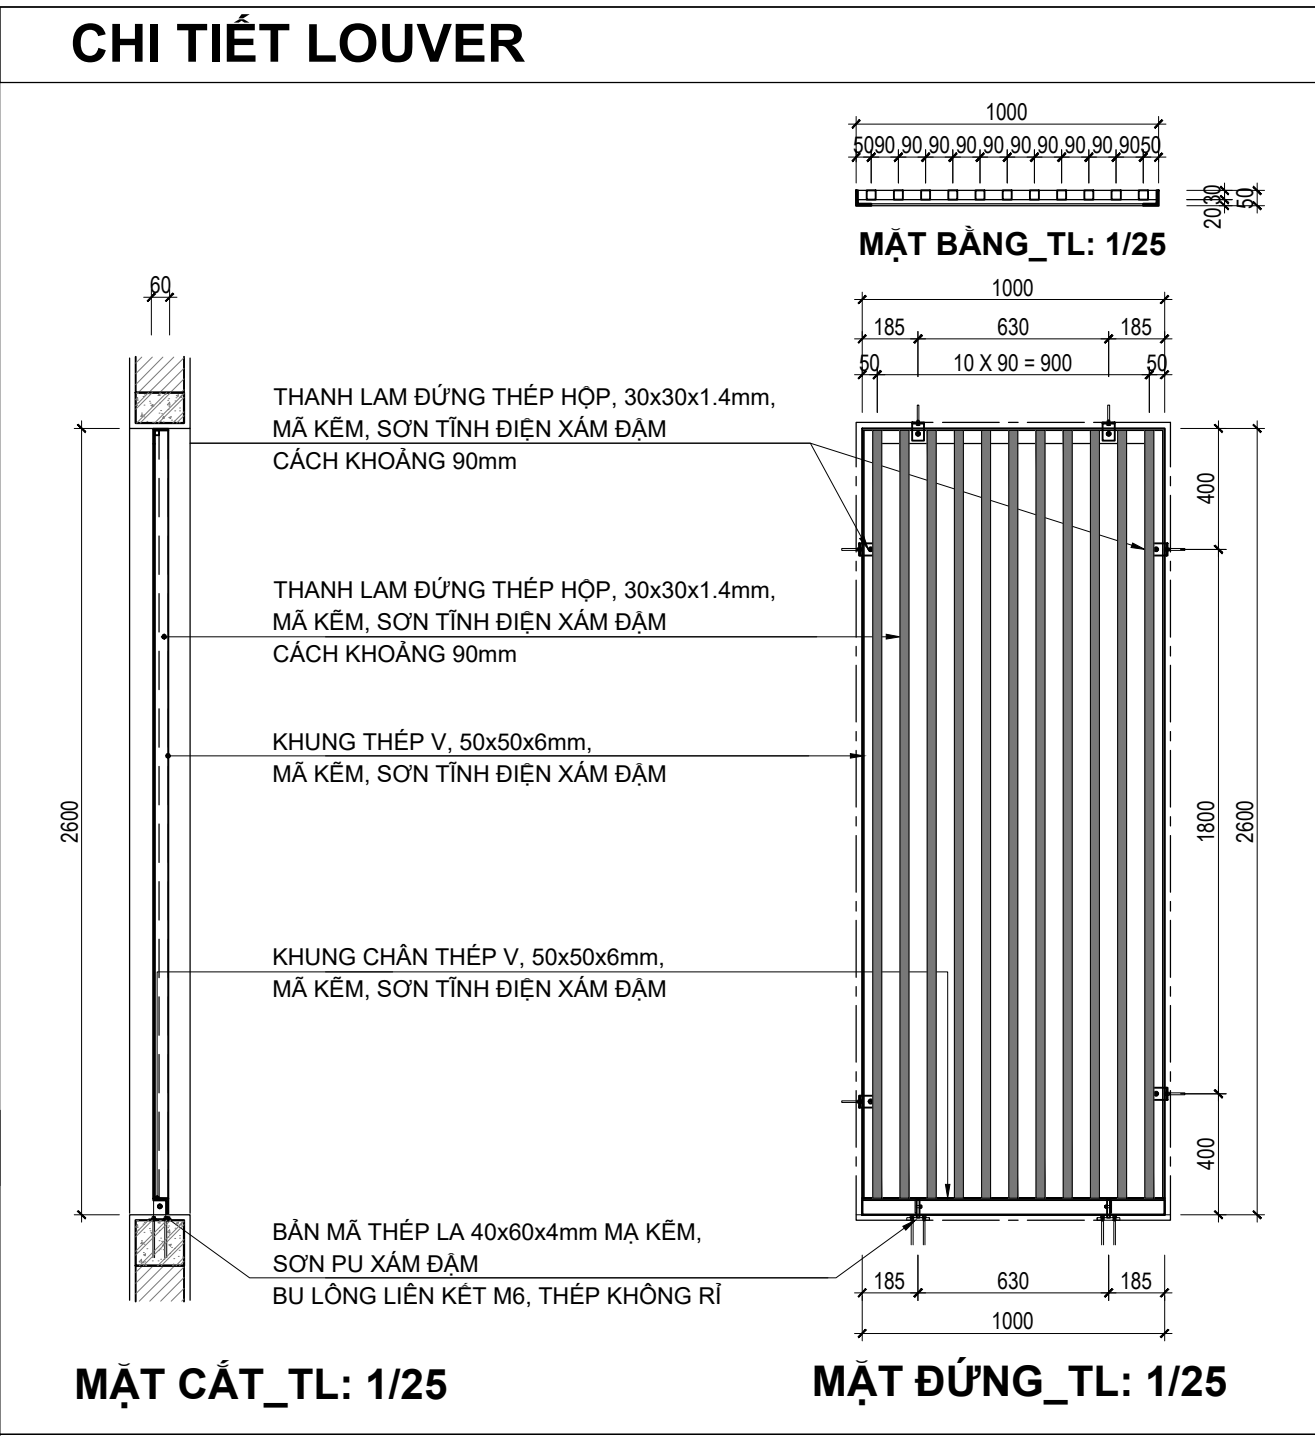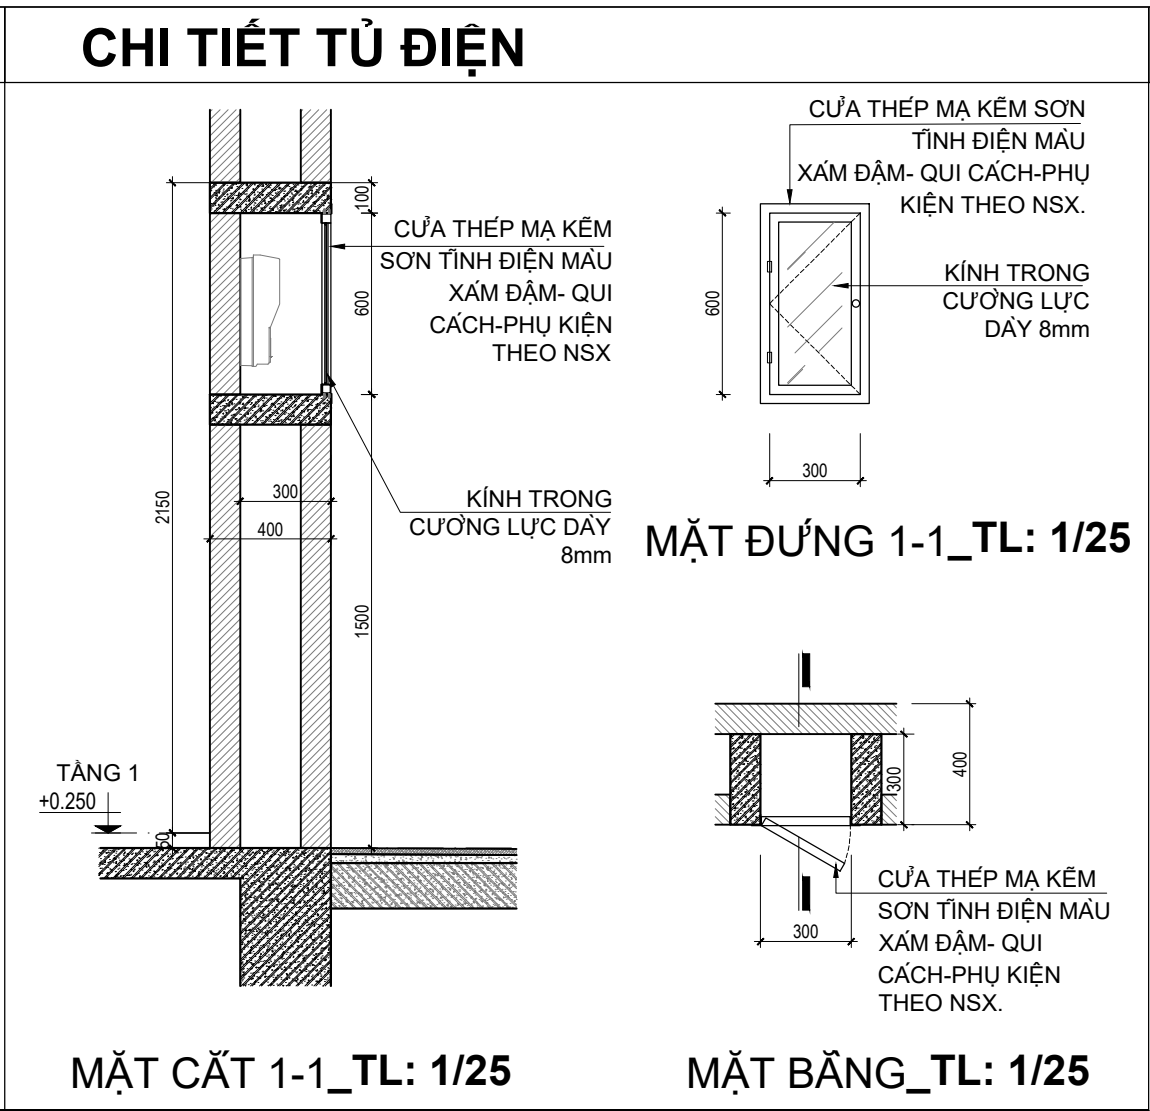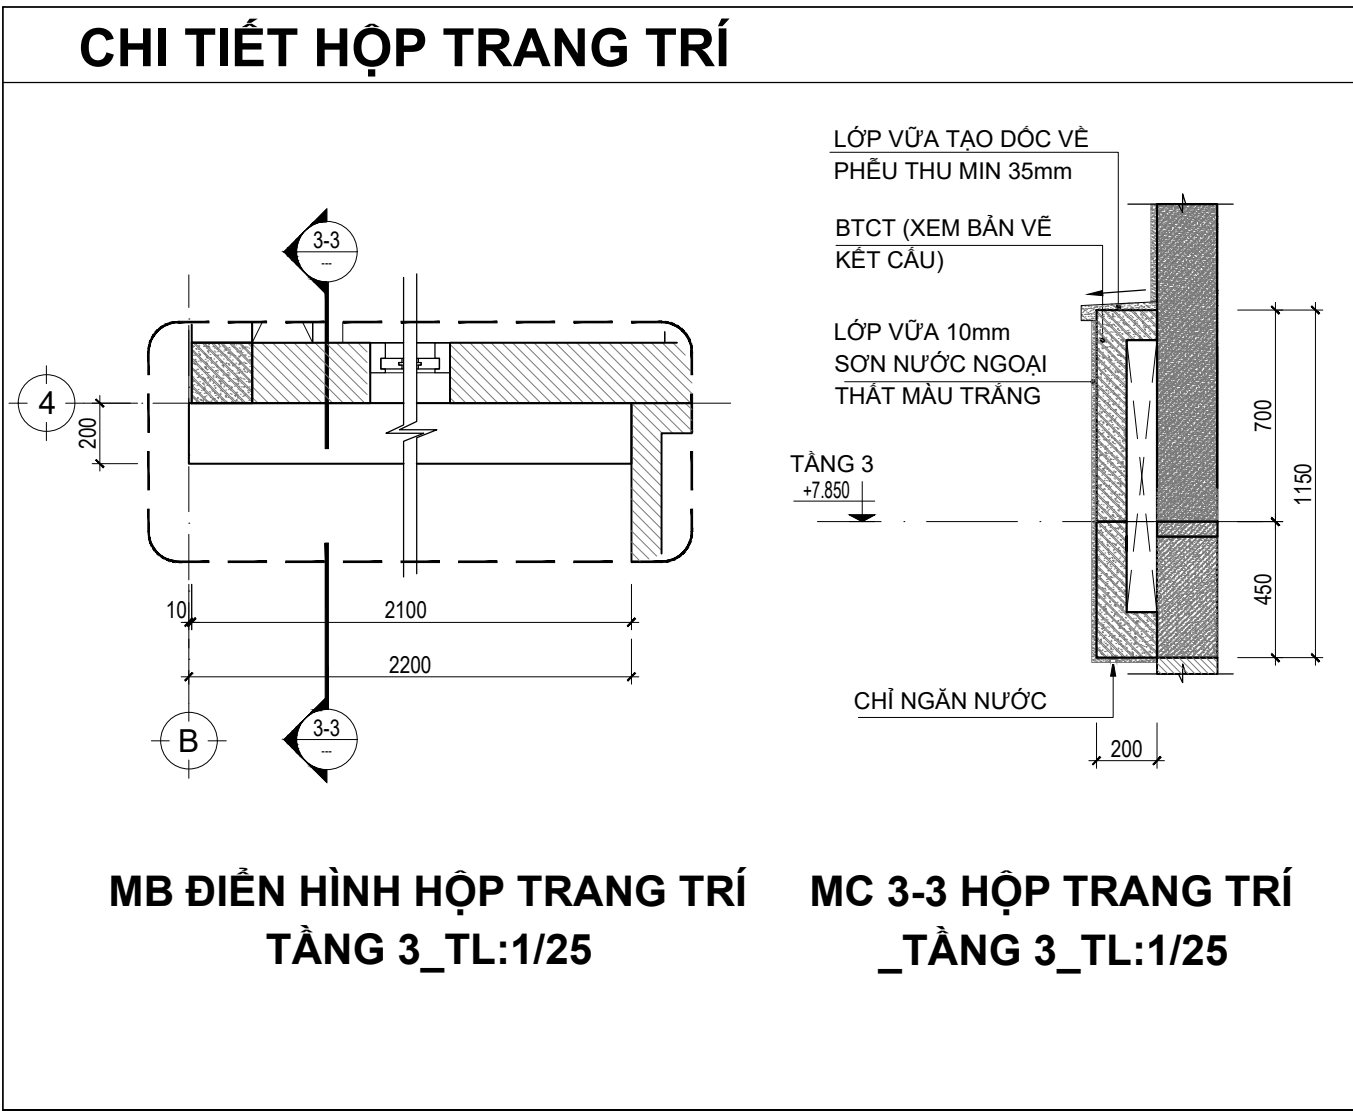


GHI CHÚ: CAO ĐỘ ±0.00 TRONG BẢN VẼ TƯƠNG ỨNG CAO ĐỘ HÒN DẦU TẠI VÍA HÉ. CAO ĐỘ VÍA HÉ VUI LÒNG XEM CÁC BẢN VẼ "THIẾT KẾ HẠ TẦNG"

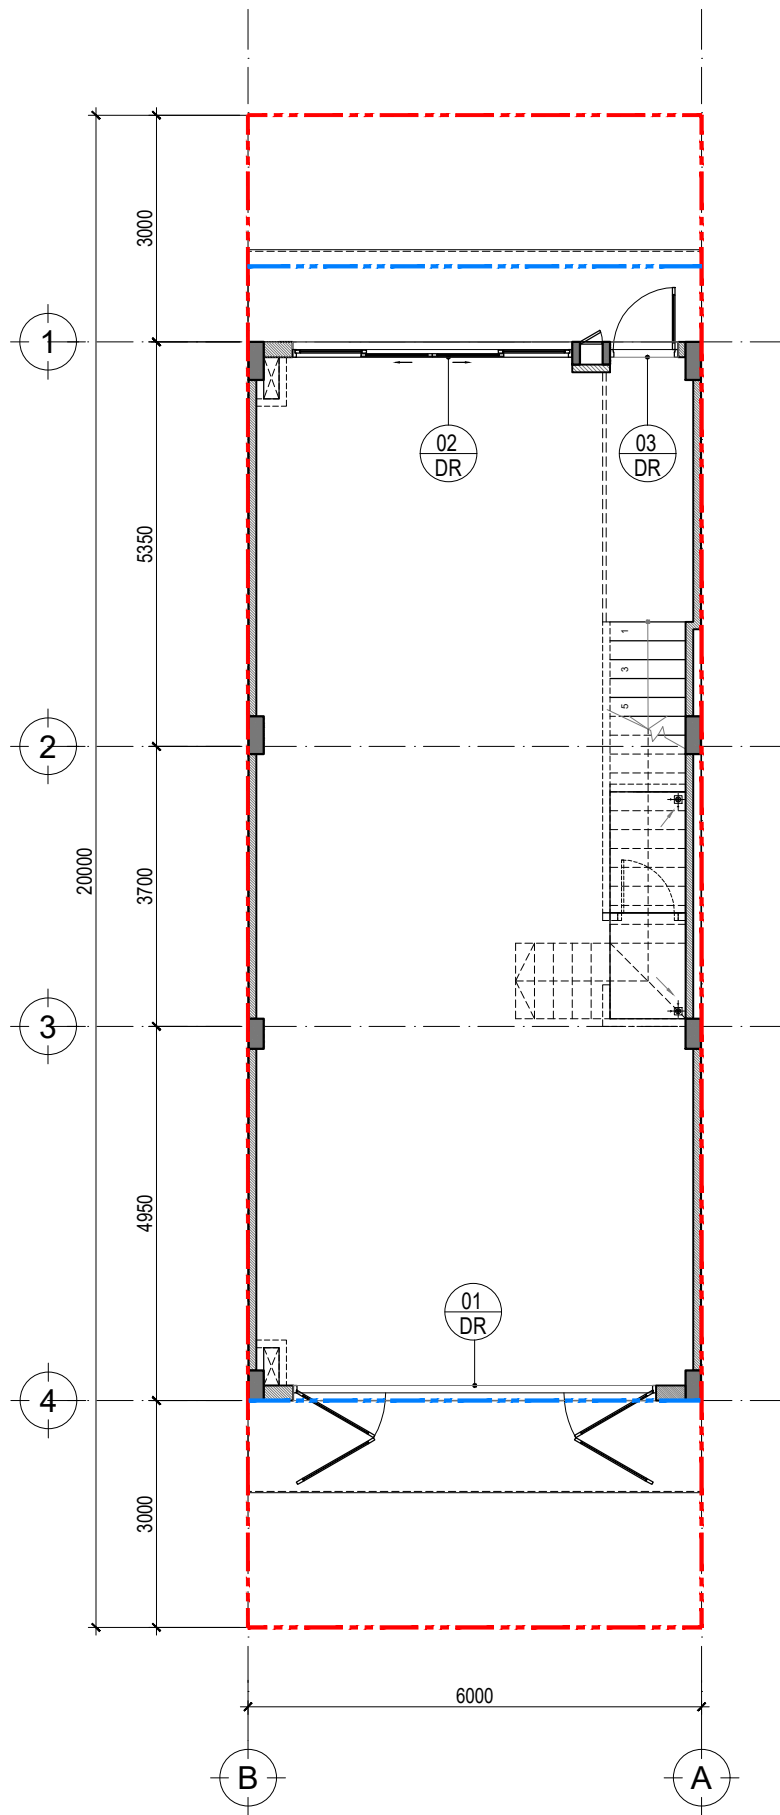
















MẶT BẰNG ĐỊNH VỊ CỬA ĐI, CỬA SỔ TẦNG 1
TL:1/100

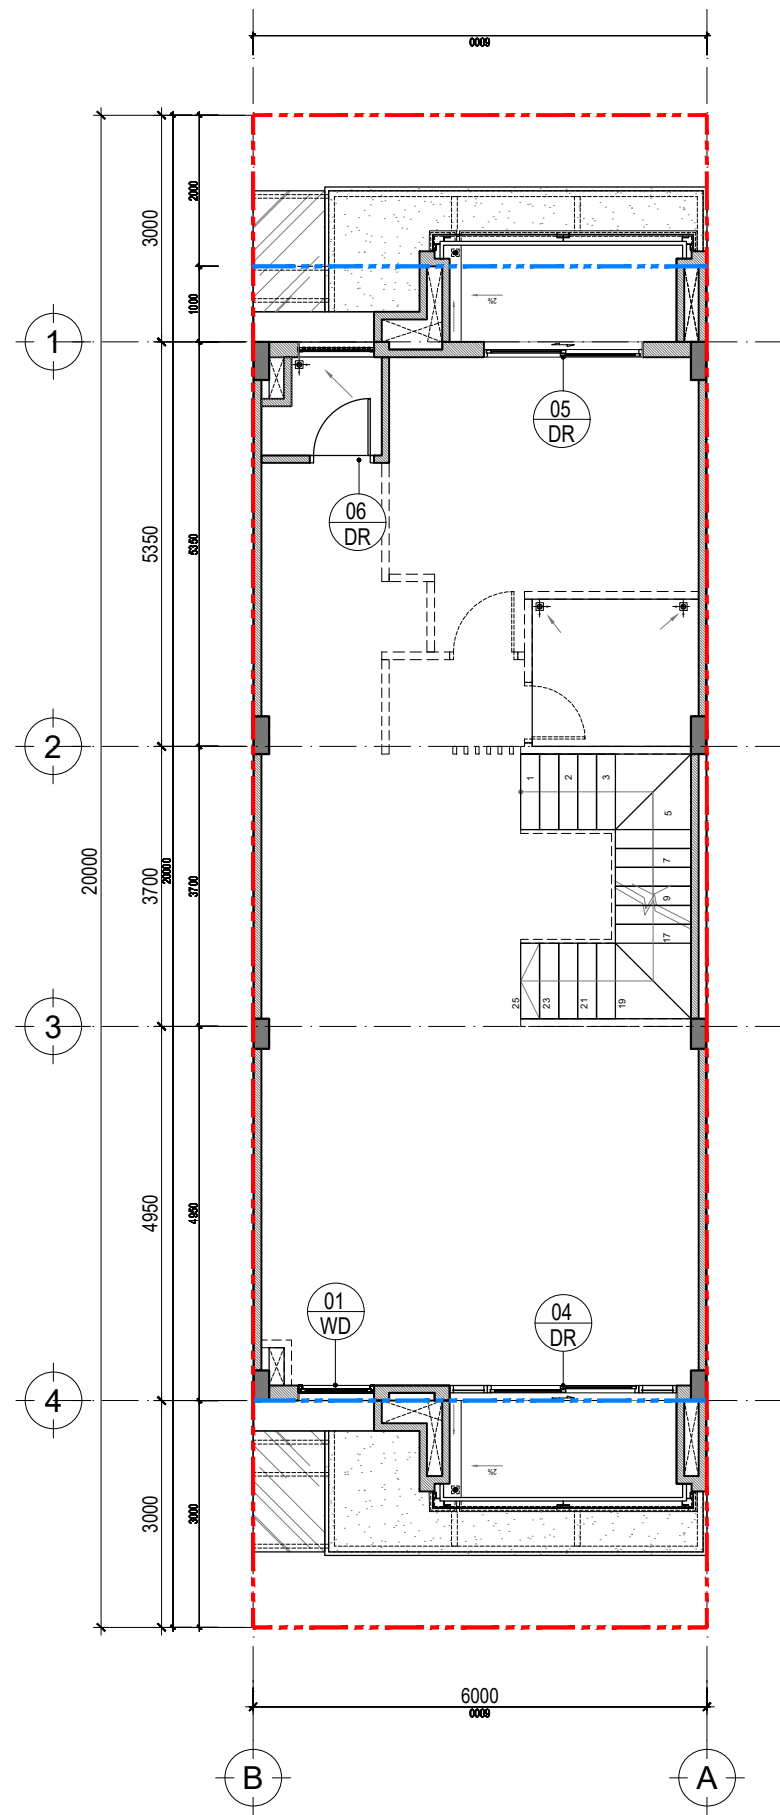









MẶT BẰNG ĐỊNH VỊ CỬA ĐI, CỬA SỔ TẦNG 2
TL:1/100

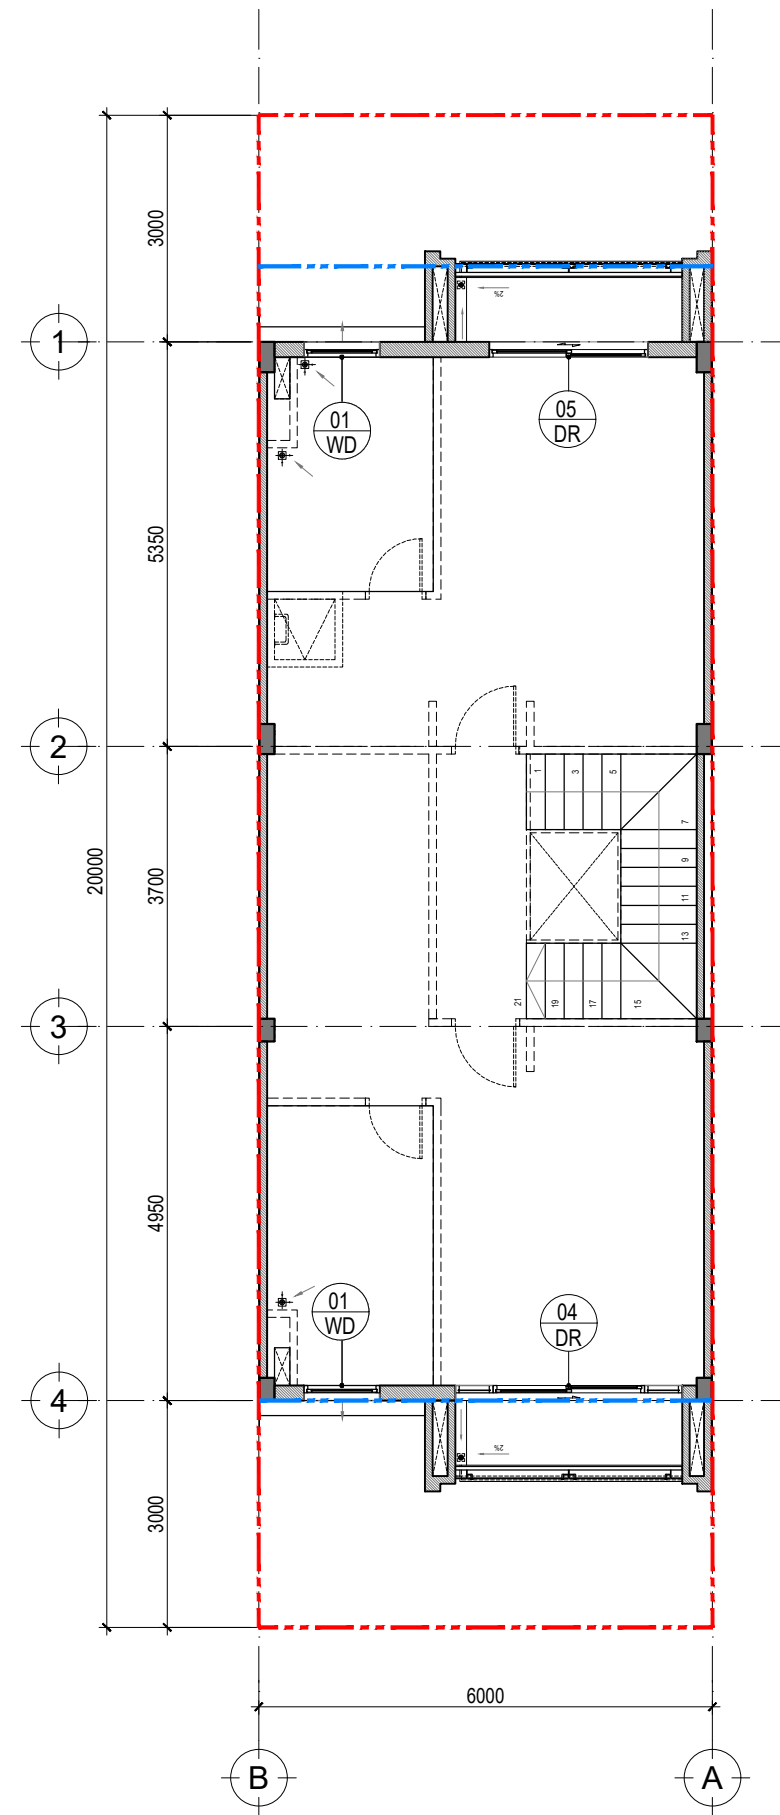

MẶT BẰNG ĐỊNH VỊ CỬA ĐI, CỬA SỔ TẦNG 3
TL:1/100

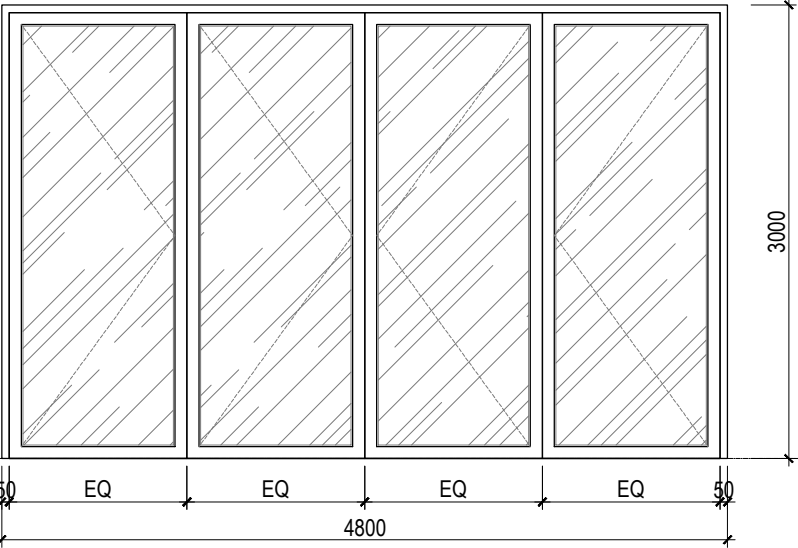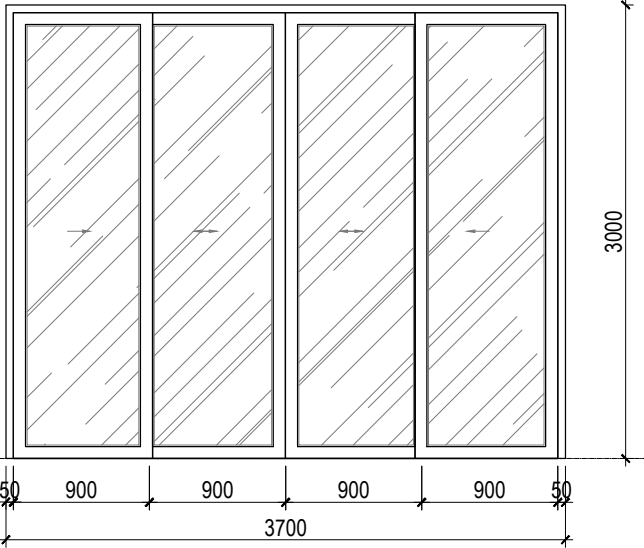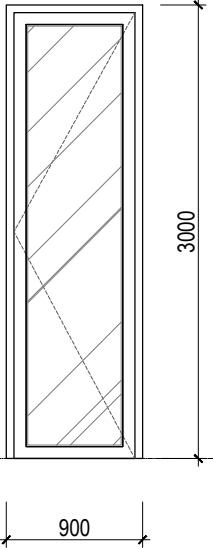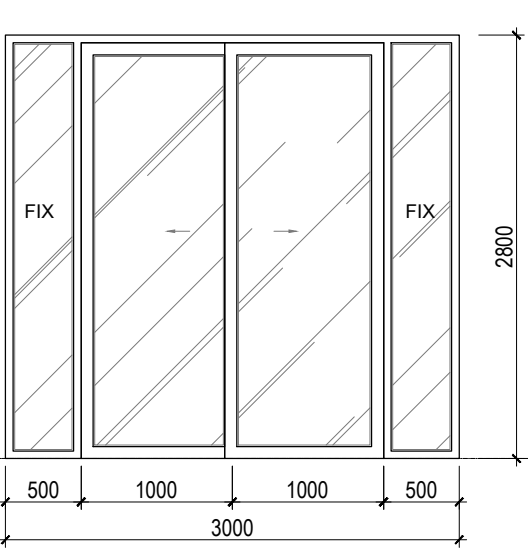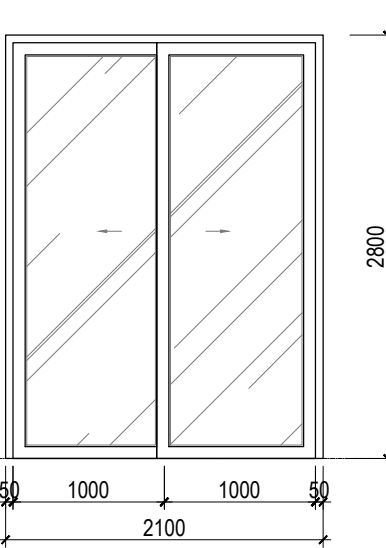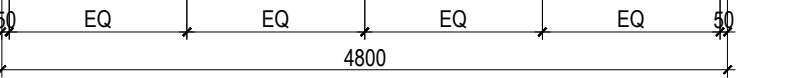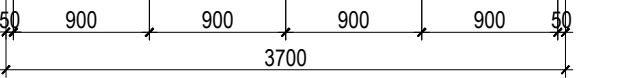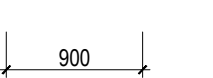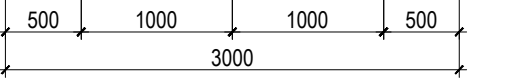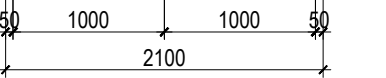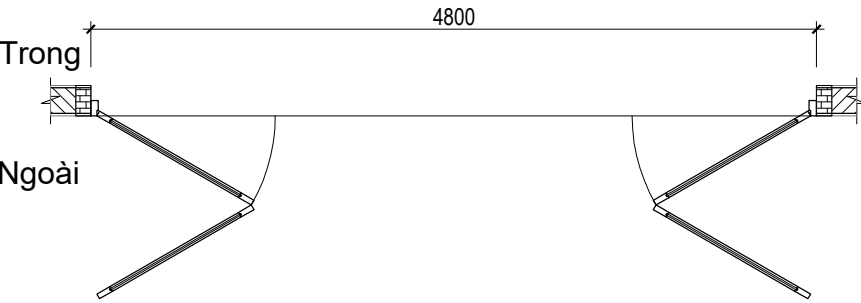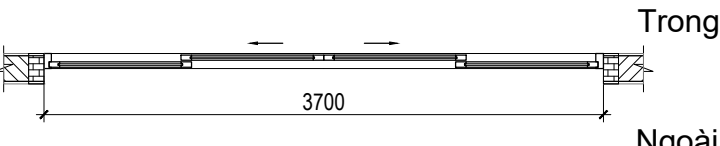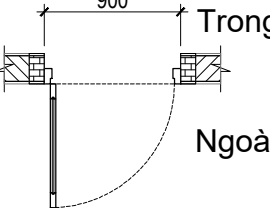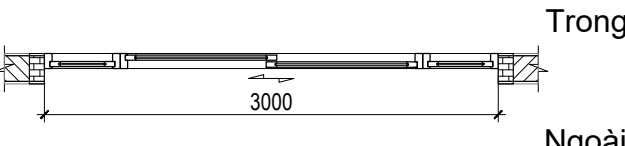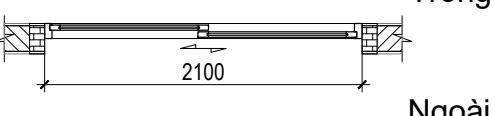KÝ HIỆU		DR-01	DR-02	DR-03	DR-04	DR-05
MẶT ĐÚNG						
Sàn hoàn thiện FFL						
MẶT BẰNG						
KÍCH THƯỚC (mm)		4800w x 3000h	3700w x 3000h	900w x 3000h	3000w x 2800h	2100w x 2800h
CÁNH CỬA	Loại	Cửa Khung nhôm trượt, 2 cánh cố định Kính trong cường lực dày 8mm, mài cạnh	Cửa Khung nhôm 2 cánh trượt, 2 cánh cố định Kính trong cường lực dày 8mm, mài cạnh	Cửa Khung nhôm mở Kính trong cường lực dày 8mm, mài cạnh	Cửa Khung nhôm 2 cánh trượt, 2 cánh cố định Kính trong cường lực dày 8mm, mài cạnh	Cửa Khung nhôm 2 cánh trượt, Kính trong cường lực dày 8mm, mài cạnh
	Hoàn thiện	Sơn tĩnh điện màu xám đậm	Sơn tĩnh điện màu xám đậm	Sơn tĩnh điện màu xám đậm	Sơn tĩnh điện màu xám đậm	Sơn tĩnh điện màu xám đậm
KHUNG NGOÀI	Loại	Khung nhôm Theo nhà cung cấp	Khung nhôm Theo nhà cung cấp	Khung nhôm Theo nhà cung cấp	Khung nhôm Theo nhà cung cấp	Khung nhôm Theo nhà cung cấp
	Hoàn thiện	Sơn tĩnh điện màu xám đậm	Sơn tĩnh điện màu xám đậm	Sơn tĩnh điện màu xám đậm	Sơn tĩnh điện màu xám đậm	Sơn tĩnh điện màu xám đậm
PHỤ KIỆN	Bản Lề	Theo nhà cung cấp	Theo nhà cung cấp	Theo nhà cung cấp	Theo nhà cung cấp	Theo nhà cung cấp
	Tay nắm	Theo nhà cung cấp	Theo nhà cung cấp	Theo nhà cung cấp	Theo nhà cung cấp	Theo nhà cung cấp
VỊ TRÍ		Cửa đi sảnh chính	Cửa đi sau nhà	Cửa đi sau nhà	Cửa đi ban công	Cửa đi ban công
TẦNG		Tầng 1	Tầng 1	Tầng 1	Tầng 2,3	Tầng 2,3
SỐ LƯỢNG (Bộ/ set)		01	01	01	02	02
GHI CHÚ		1/ TẤT CẢ HƯỚNG MỞ CỬA CẦN PHẢI XEM BẢN VẼ MẶT BẰNG KÍ HIỆU CỬA TRƯỚC KHI ĐẶT HÀNG 2/ NHÀ CUNG CẤP CẦN CÂN CỨ VÀO TẢI TRONG GIÓ QUY ĐỊNH ĐỂ XÁC ĐỊNH KÍCH THƯỚC VÀ KHUNG NHÔM VÀ KÍNH PHÙ HỢP 3/ TẤT CẢ CÁC HẠNG MỤC CỬA NHÔM KÍNH ĐỀU ĐƯỢC CUNG CẤP ĐẦY ĐỦ VÀ KHÔNG GIỚI HẠN PHỤ KIỆN BAO GỒM TRỌN BỘ PHỤ KIỆN TAY NẮM, PHỤ KIỆN CHỐNG BỤI VÀ Ổ KHOÁ ẨM ĐỐI VỚI CỬA ĐI				

GHI CHÚ: CAO ĐỘ ±0.00 TRONG BẢN VẼ TƯƠNG ỨNG CAO ĐỘ HÒN DẦU TẠI VÍA HÉ. CAO ĐỘ VÍA HÉ VUI LÒNG XEM CÁC BẢN VẼ "THIẾT KẾ HẠ TẦNG"

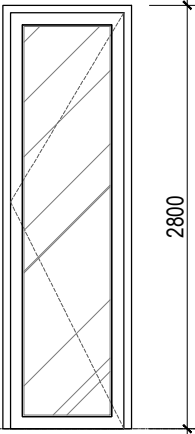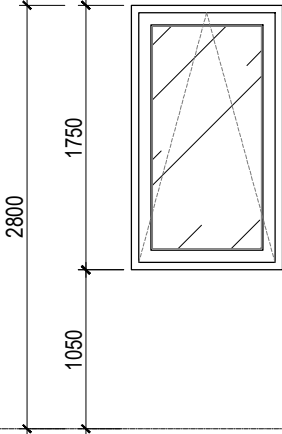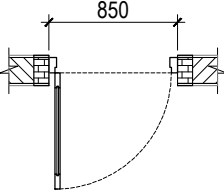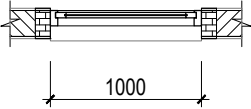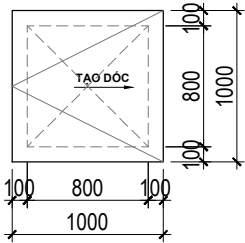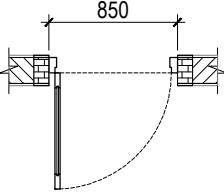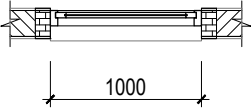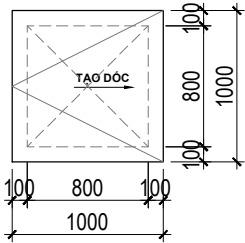KÝ HIỆU		DR-06	WD-01		
MẶT ĐÚNG					
					
SÀN HOÀN THIỆN FFL					
MẶT BẰNG					
KÍCH THƯỚC (mm)		850w x 2800h	1000w x 1750h	1000w x 1000h	
CÁNH CỬA	Loại	Cửa Khung nhôm mở Kính trong cường lực dày 8mm, mài cạnh	Cửa sổ Khung nhôm bật Kính trong cường lực dày 6mm, mài cạnh	Kích thước lỗ mở sàn 800x800 Kích thước cửa theo qui cách nhà cung cấp	
	Hoàn thiện	Sơn tĩnh điện màu xám đậm	Sơn tĩnh điện màu xám đậm	Sơn tĩnh điện màu trắng	
KHUNG NGOÀI	Loại	Khung nhôm Theo nhà cung cấp	Khung nhôm Theo nhà cung cấp		
	Hoàn thiện	Sơn tĩnh điện màu xám đậm	Sơn tĩnh điện màu xám đậm		
PHỤ KIỆN	Bản Lề	Theo nhà cung cấp	Theo nhà cung cấp	Theo nhà cung cấp	
	Tay nắm	Theo nhà cung cấp	Theo nhà cung cấp	Theo nhà cung cấp	
VỊ TRÍ		Cửa đi phòng giặt		Cửa thăm mái	
TẦNG		Tầng 2	Tầng 2,3	Tầng mái	
SỐ LƯỢNG (Bộ/ set)		01	03	01	
GHI CHÚ		1/ TẤT CẢ HƯỚNG MỞ CỬA CẦN PHẢI XEM BẢN VẼ MẶT BẰNG KÍ HIỆU CỬA TRƯỚC KHI ĐẶT HÀNG 2/ NHÀ CUNG CẤP CẦN CÂN CỨ VÀO TẢI TRONG GIÓ QUY ĐỊNH ĐỂ XÁC ĐỊNH KÍCH THƯỚC VÀ KHUNG NHÔM VÀ KÍNH PHÙ HỢP 3/ TẤT CẢ CÁC HẠNG MỤC CỬA NHÔM KÍNH ĐỀU ĐƯỢC CUNG CẤP ĐẦY ĐỦ VÀ KHÔNG GIỚI HẠN PHỤ KIỆN BAO GỒM TRỌN BỘ PHỤ KIỆN TAY NẮM, PHỤ KIỆN CHỐNG BỤI VÀ Ổ KHOÁ ẨM ĐỐI VỚI CỬA ĐI			